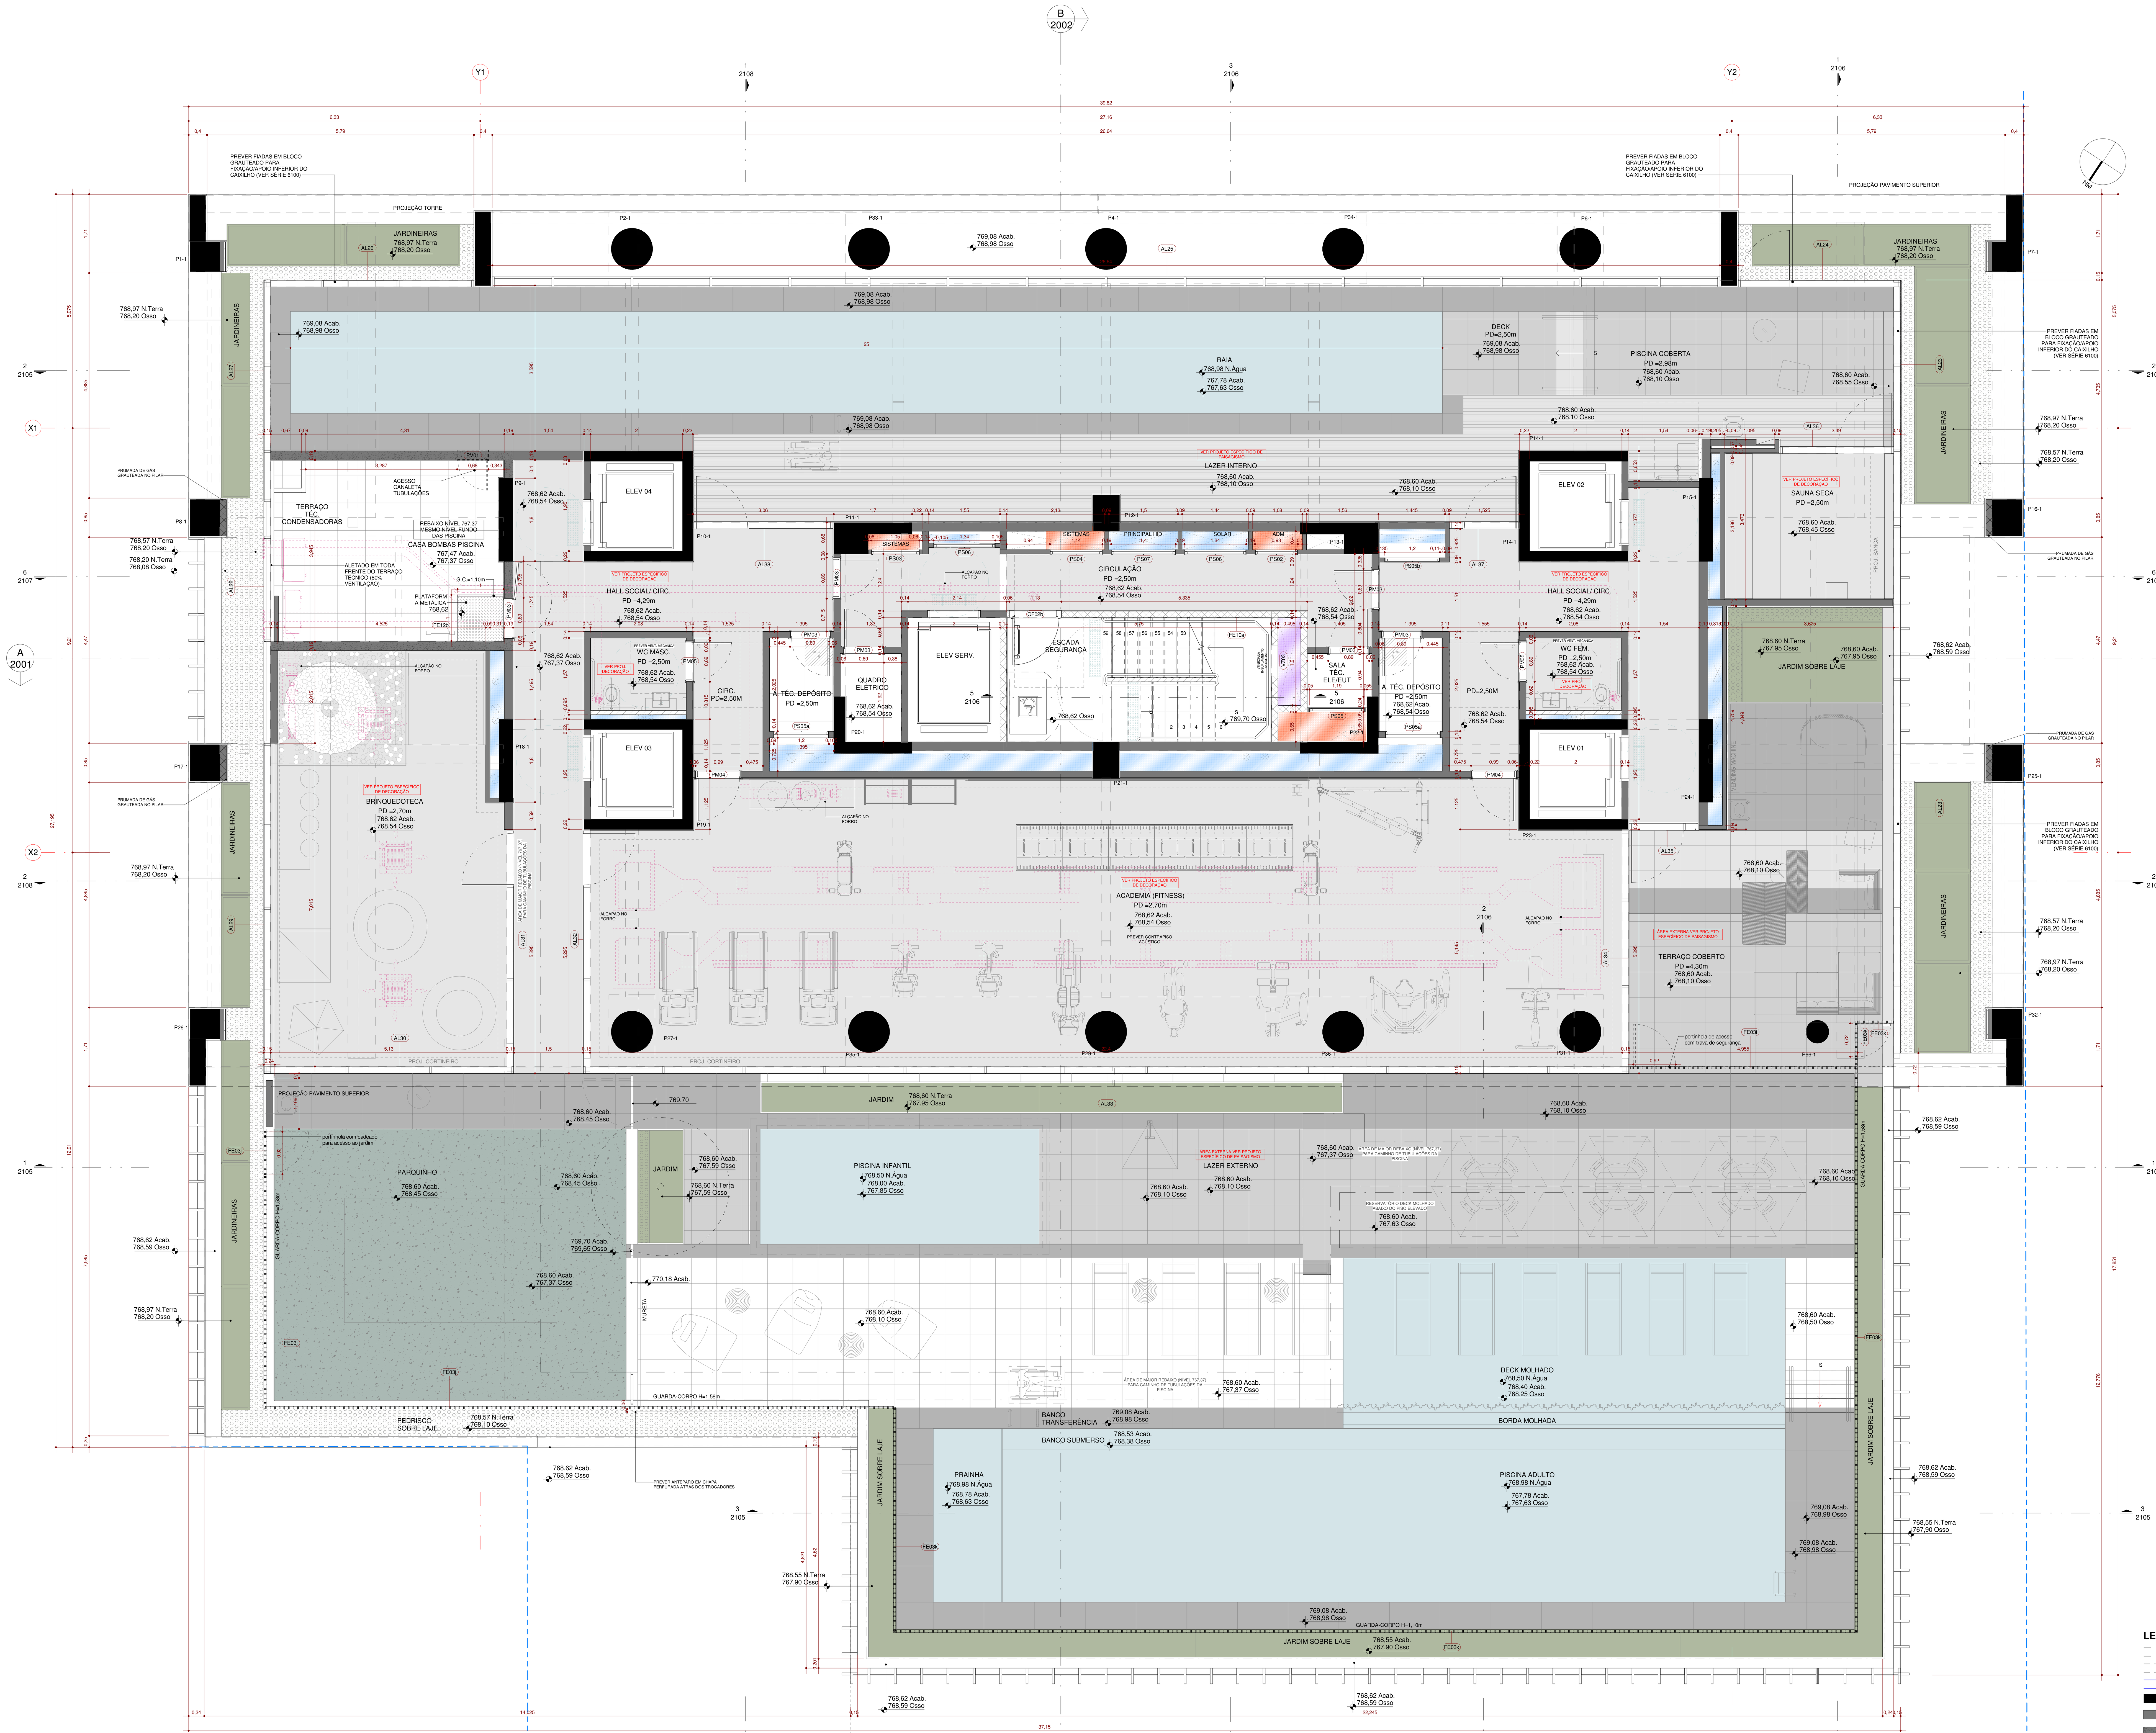

PLANTA DO 3º PAVIMENTO
1106 1:50

TABELA DE ACABAMENTOS - LAZER (ART-LC-EP-0003-ACA-R01)

DOCUMENTO DESENVOLVIDO PELA INCORPORADORA E DEVE ATENDER A NORMA ABNT NBR 15.575

Item	Ambientes	Piso	Parede	Forro	Louças e Cubas	Metais	Bancadas	Complementos
1	Halls Sociais (01 e 02)	Granito Branco Siena, acabamento escovado 120x120cm. Rodapé idem piso, h= 50cm com perfil metálico embutido (na parte superior), na cor grafite.	Pintura latex cor self color, conforme projeto de decoração.	Forro de Gesso com pintura cor self color	____	____	____	Aduelas e soleiras dos elevadores em Granito Branco Siena, acabamento escovado. Soleiras das portas externas, adotar idem ao piso externo - ver paisagismo. Soleiras de portas internas em Granito Branco Siena acabamento escovado. Não considerar soleira para portas internas entre ambientes com mesmo piso.
2	Brinquedoteca	Piso Vinílico Forbo, Allura, Linha Stone, cor Iced Stream ref S63774, 75x50cm.Rodapé invertido com perfil metálico em aluminio, na cor cinza RAL 7043.	Pintura latex cor self color, conforme projeto de decoração.	Forro de Gesso com pintura cor self color	____	____	____	Soleiras de portas internas em Granito Branco Siena, acabamento escovado. Soleiras das portas externas, adotar idem ao piso externo - ver paisagismo.
3	Academia	Piso emborrachado Impact Soft Peso Livre, Colors Blend cor Cinza e para tepete funcional piso emborrachado Impact Soft Peso Livre, Linha Gráficos cor Terracota e cor Coral, 1x1m (15mm), Aubicon.Rodapé invertido com perfil metálico em aluminio, na cor cinza RAL 7043.	Pintura latex cor self color, conforme projeto de decoração.Para pilares redondos adotar acabamento em concreto aparente.	Forro de Gesso com pintura cor self color	____	____	____	Soleiras de portas internas em Granito Branco Siena, acabamento escovado. Soleiras das portas externas, adotar idem ao piso externo - ver paisagismo.
4	WCs PNE	Granito Branco Siena, acabamento escovado 120x120cm. Rodapé idem piso, h= 50cm com perfil metálico embutido (na parte superior), na cor grafite.	Pintura acrílica cor self color conforme projeto de decoração.Trechos em Pastilha Cerâmica Hexagonal Timor, cor Verde, ref M6435, 5x5cm Atlas.	Forro de Gesso com pintura cor self color	Bacia convencional Deca, cor branca, Vogue Plus, linha Conforto, sem abertura, ref. P.510.17.Lavatório semi-encaixe com mesa Deca Monte Carlo, cor branca, ref. L82.17.	Caixa embutida Montana.Torneira de mesa Deca, linha Link Conforto, ref. 1196.C.LNK.Barras de apoio Deca, Conforto, com acabamento cromado.Acabamento de registro Deca, linha Link, ref. 4900.C.PQ.LKN	Bancada em Granito Branco Siena, considerar frontão e saia, conforme projeto civil de decoração.	Não considerar soleira para portas internas entre ambientes com mesmo piso.
5	Sauna Seca	Granito Branco Siena, acabamento escovado 120x120cm.	Considerar padrão diferenciado do fornecedor - ripas de 2cm - madeira Tauari (Fornecedor TecnoSaunas).	Conforme projeto específico do fornecedor -idem revestimento de parede.	____	____	____	Não considerar soleira para portas internas entre ambientes com mesmo piso.

TABELA DE ACABAMENTOS - ÁREAS OPERACIONAIS 3º PAV. (ART-LC-EP-0013-ACA-R03)

DOCUMENTO DESENVOLVIDO PELA INCORPORADORA E DEVE ATENDER A NORMA ABNT NBR 15.575

Item	Ambientes	Piso	Parede	Forro	Louças e Cubas	Metais	Bancadas	Complementos
14	Casa de Bombas dos reservatórios (2º e 1º subsolos e Ático) /Casa de Bombas da piscina (3º Pav.)	Porcelanato Portobello, Cetim Bianco Bold, (60x60)cm.	Azulejo Portobello, Idea Bianco Bold, (30x60)cm.	____	____	____	____	Granito Branco Itaunas com acabamento satinado.

NOTAS GERAIS:

PARA CONSULTA DO PROJETO DE ARQUITETURA, VER SÉRIES ABAIXO:
- 0000 PARA ÍNDICES, LEGENDAS E TABELAS GERAIS.
- 1000 PARA PLANTAS DE LOCAÇÃO E IMPLANTAÇÃO.
- 1100 PARA PLANTAS GERAIS.
- 1150 PARA PLANTAS AMPLIADAS.
- 2000 PARA CORTES
- 3000 PARA ELEVAÇÕES.
- 4000 PARA DETALHAMENTO DE ESCADAS.
- 4100 PARA AMPLIAÇÃO DE SANITÁRIOS E ÁREAS MOLHADAS.
- 4200 PARA AMPLIAÇÃO DE ÁREAS COMUNS.
- 4300 PARA DETALHAMENTO DE MARQUISES.
- 5000 PARA DETALHAMENTO DE FORROS.
- 6100 PARA DETALHAMENTO DE ESQUADRIAS DE ALUMÍNIO.
- 6200 PARA DETALHAMENTO DE ESQUADRIAS DE ALUMÍNIO VENEZIANA.
- 6300 PARA DETALHAMENTO DE ESQUADRIAS DE FERRO.
- 6400 PARA DETALHAMENTO DE ESQUADRIAS DE MADEIRA.
- 6500 PARA DETALHAMENTO DE PORTAS CORTA-FOGO.
- 6600 PARA DETALHAMENTO DE GRELHAS E ESCADAS MARINHEIRO.
- 7000 PARA DETALHES CONSTRUTIVOS, PRÉ-MOLDADOS E COBERTURAS.
- 8000 PARA DETALHES DE BANCADAS E SOLEIRAS.

1) MEDIDAS EM METROS.
2) DIMENSÕES DOS PILARES EM CENTÍMETROS.
3) TODAS AS COTAS INTERNAS ESTÃO MEDIDAS NO OSSO E TODAS AS COTAS EXTERNAS ESTÃO MEDIDAS NO ACABADO.
4) TODAS AS MEDIDAS DEVEM SER VERIFICADAS EM OBRA.
5) PARA ESPECIFICAÇÃO DE ACABAMENTOS, VER CADERNO DE ESPECIFICAÇÕES DE ACABAMENTOS DA ARQUITETURA OU DA INCORPORAÇÃO.
6) AS ESPESSURAS DOS REVESTIMENTOS PARA PROJETO FORAM DEFINIDAS COM O CLIENTE E/OU CONSTRUTORA E/OU PROJETISTA ESPECÍFICO E DEVERÃO SER CONFERIDAS NA OBRA.
7) PARA A FORMA DE FIXAÇÃO, NECESSIDADE DE ESTRUTURAS AUXILIARES E OUTRAS INFORMAÇÕES DOS REVESTIMENTOS EM PEDRA, VER PROJETO DE ROCHAS ORNAMENTAIS OU CONSULTAR FORNECEDOR.
8) A CHECAGEM DAS FURAÇÕES NAS FORMAS DE ESTRUTURA É DE RESPONSABILIDADE DO RESPECTIVO PROJETISTA COMPLEMENTAR.
9) PARA AS VEDAÇÕES E RESPECTIVAS FURAÇÕES, VER PROJETO ESPECÍFICO DE VEDAÇÕES.
10) OS VÃOS DE ALVENARIAS PARA INSTALAÇÃO DAS ESQUADRIAS DEVERÃO SER REVISTOS PELA CONSTRUTORA EM FUNÇÃO DO SEU SISTEMA CONSTRUTIVO E DOS RESPECTIVOS FORNECEDORES.
11) PARA CINTAS DE AMARRAÇÃO E VERGAS QUE SE FAÇAM NECESSÁRIAS NAS ALVENARIAS, VER PROJETO DE VEDAÇÕES.
12) DEVERÃO SER PREVISTAS CANTONEIRAS "INVISÍVEIS" NOS CANTOS VIVOS DAS ALVENARIAS REVESTIDAS EM ARGAMASSA.
13) A CONSTRUTORA DEVERÁ PLANEJAR COM AS INSTALADORAS E/OU PROJETISTAS COMPLEMENTARES TODAS AS VEDAÇÕES QUE NECESSITEM SER EXECUTADAS APÓS A ENTRADA DOS EQUIPAMENTOS NAS RESPECTIVAS ÁREAS TÉCNICAS.
14) AS CARACTERÍSTICAS E DIMENSIONAMENTO DAS PORTAS DE ÁREAS TÉCNICAS, BEM COMO CIRCULAÇÕES DE ACESSO A EQUIPAMENTOS, DEVEM SER FORNECIDOS PELOS RESPECTIVOS PROJETISTAS COMPLEMENTARES.
15) PARA DETALHES INTERNOS DAS CASAS DE MÁQUINAS, VER PROJETO ESPECÍFICO E/OU CONSULTAR INSTALADORA.
16) PARA ESPECIFICAÇÃO E DIMENSIONAMENTO DAS GRELHAS DE PRESSURIZAÇÃO, VENTILAÇÃO E EXAUSTÃO, VER PROJETO DE AR CONDICIONADO.
17) PARA EXECUÇÃO DAS CANALETAS DE AP DAS DIAFRAGMAS, VER PROJETO ESPECÍFICO DE IMPERMEABILIZAÇÃO.
18) PARA ELEMENTOS DE FACHADA, VER PROJETOS DE CAIXILHARIA, REVESTIMENTOS EM ROCHAS ORNAMENTAIS E ESTRUTURA METÁLICA.
19) VERIFICAR OS PROJETOS COMPLEMENTARES E SEUS RELATÓRIOS, ASSIM COMO OS RELATÓRIOS DAS CONSULTORIAS DE INCÊNDIO, CAIXILHARIA, SUSTENTABILIDADE E OUTRAS ENVOLVIDAS NO PROJETO.
20) AS ALVENARIAS E VEDAÇÕES CORTA-FOGO, VALIDADAS PELA CONSULTORIA OU PROJETO DE COMABTE À INCÊNDIO, SERÃO RESISTENTES A, NO MÍNIMO, 2 (DUAS) HORAS DE FOGO OU CONFORME TRRF ESPECÍFICO DO PROJETO OU EXIGÊNCIA DO CORPO DE BOMBEIROS LOCAL; VER PROJETO ESPECÍFICO DE VEDAÇÕES.
21) AS INSTALAÇÕES ELÉTRICAS E DUTOS QUE EVENTUALMENTE PASSEM POR DENTRO DAS CASAS DE MÁQUINAS DE PRESSURIZAÇÃO, EXTRAÇÃO DE FUMAÇA E OUTRAS DESTINADAS À PREVENÇÃO E COMBATE À INCÊNDIO DEVERÃO SER ENCAPADAS COM ELEMENTOS CORTA-FOGO.
22) VERIFICAR POSIÇÃO E DETALHES DOS ELEMENTOS CORTA-FOGO DOS CAIXILHOS ("FIRE STOP" OU OUTROS NECESSÁRIOS) NO PROJETO DE CAIXILHARIA.
23) TODOS OS PROJETISTAS DEVEM ANALISAR, COMENTAR E APROVAR OS PROJETOS DOS ELEVADORES PREVENDO OS ITENS CABÍVEIS EM SEUS PROJETOS.
24) VER SISTEMA DE DRENAGEM, CAIMENTOS DE PISO E GRELHAS DE CAPTAÇÃO NOS PROJETOS ESPECÍFICOS DE HIDRÁULICA, IMPERMEABILIZAÇÃO E CLIMATIZAÇÃO.
25) AS VAGAS DO PROJETO DE ARQUITETURA REFEREM-SE AO PROJETO LEGAL.
26) PARA OS DETALHES E LOCAÇÕES REFERENTES ÀS ÁREAS DE ESTACIONAMENTO, COMO PINTURAS DE SINALIZAÇÃO, CALÇADAS, LOCAÇÃO DE CANCELAS E EQUIPAMENTOS, ETC., VER PROJETO ESPECÍFICO DE GARAGENS.
27) PARA ESPECIFICAÇÃO E LOCAÇÃO DE PISOS TÁTEIS, VER PROJETO DE ACESSIBILIDADE.
28) PARA EQUIPAMENTOS DE ACESSIBILIDADE NAS GARAGENS, VER PROJETO DE ACESSIBILIDADE E DE GARAGENS.
29) PARA PONTOS DE ILUMINAÇÃO FORA DOS FORROS, NÃO COTADOS NO PROJETO DE ARQUITETURA, VERIFICAR A LOCAÇÃO NOS PROJETOS DE LUMINOTÉCNICA, PAISAGISMO E DECORAÇÃO.

PLANTA DE SITUAÇÃO

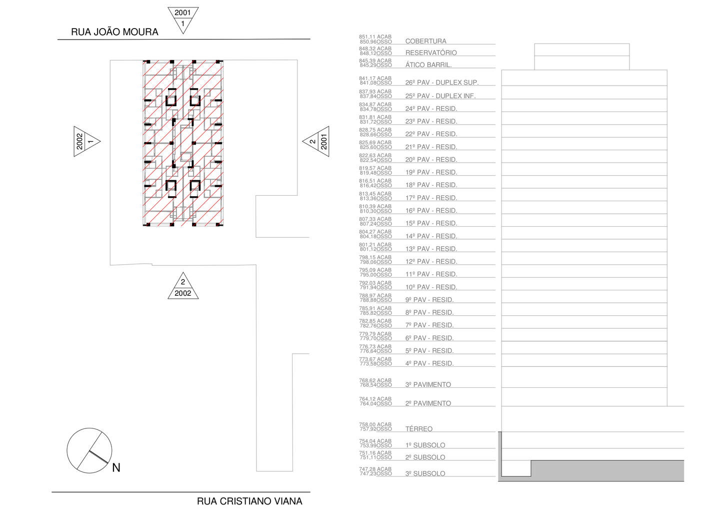

TORRE 01 - TABELA COMPARATIVO ELEVADORES

Itens	Atlas	Thyssen	Otis
Elevadores Sociais			
Modelo	Linha Schindler 3600	_	GEN2 Confort Estética Ambiance Advanced
Casa de Máquinas (sim/não)	sim	não	não
Capacidade	9 pessoas	8 pessoas	8 pessoas
Número de Paradas	26 paradas	26 paradas	26 paradas
Percurso Total	86,76m	86,76m	86,76m
Caixas de Instalação (mínima)	1950x1850mm	1900x1900mm	1960x1750mm
Profundidade do Poço	1900mm	1600mm	1400mm
Última Parada	4700mm	4600mm	4200mm
Pé-Direito Casa de Máquinas	2500mm	sem casa de máquinas	sem casa de máquinas
Dimesão da Cabine	1200x1400mm	1100x1400mm	1100x1400mm
Pé-Direito da Cabine	2500mm	2600mm	2500mm
Abertura das Portas	lateral	lateral direito	central
Dimensão das Portas (LxA)	900x2100mm	900x2100mm	800x2100mm
Altura entre piso acabado e viga da porta	A + 140mm	A + 350mm	A + 215mm
Ventilação	10% casa de máquinas	500x800mm(A/L)	
Elevadores Serviço			
Modelo	Linha Schindler 5500	_	GEN2 Confort Estética Ambiance Advanced
Casa de Máquinas (sim/não)	sim	não	não
Capacidade	18 pessoas	12 pessoas	12 pessoas
Número de Paradas	26 paradas	26 paradas	26 paradas
Percurso Total	86,76m	86,76m	86,76m
Caixas de Instalação (mínima)	2000x2700mm	2100x1900mm	1960x1750mm
Profundidade do Poço	1900mm	1600mm	1400mm
Última Parada	4700mm	4600mm	4200mm
Pé-Direito Casa de Máquinas	2500mm	sem casa de máquinas	sem casa de máquinas
Dimesão da Cabine	1250x2300mm	1400x1400mm	1100x1400mm
Pé-Direito da Cabine	2600mm	2600mm	2500mm
Abertura das Portas	central	lateral direito	central
Dimensão das Portas (LxA)	800x2100mm	1000x2100mm	800x2100mm
Altura entre piso acabado e viga da porta	A + 140mm	A + 350mm	A + 215mm
Elevador Fachada Ativa 01 (Loja 01)			
Modelo	Linha Schindler 3300	V300	_
Casa de Máquinas (sim/não)	não	não	não
Capacidade	8 passageiros	3 passageiros (exlusivo PNE)	_
Número de Paradas	2 paradas	2 paradas	2 paradas
Percurso Total	6,12m	6,12m	6,12m
Caixas de Instalação (mínima)	1600x1800	1500X16500mm	1810x1750mm
Profundidade do Poço	1250mm	250mm	1100mm
Última Parada	4000mm	3000mm	3900 a 4200mm
Abertura das Portas	lateral	lateral	central
Dimensão das Portas (LxA)	800x2100mm	800x2000mm	800x2100mm
Altura entre piso acabado e viga da porta	A + 140mm	A + 110mm	A + 215mm

1. Verificar a gola lateral disponível em projeto
3. Caso seja contratado Otis, teremos que prever vigas ou laje intermediária com menos de 4,70m para a ultima altura.
4. Ventilação da casa de máquinas de 10% da área da mesma. Sem casa de máquina conforme projeto específico.
5. Projeto atende situação mais restritiva (elevadores com casa de máquinas). Para opção de elevadores sem casa de máquinas deverá ser prevista ventilação dutada até venezianas no pav. do reservatório/cs. Máquinas
6. Atendimento à NM313/2007 (elevadores)

LEGENDA DE VEDAÇÕES

- PROJEÇÃO VIGAS ACIMA
- PROJEÇÃO VIGAS ABAIXO
- PROJEÇÃO FUNDAÇÃO
- ESTRUTURA DE CONCRETO
- ALVENARIA
- ALVENARIA PREENCHIDA / BLOCO ACÚSTICO
- ALVENARIA GRAUTEADA
- ALVENARIA CORTA-FOGO
- DRYWALL

NOTA: PARA ESPECIFICAÇÃO DAS VEDAÇÕES E NECESSIDADE DE TRATAMENTO ACÚSTICO, VERIFICAR PROJETOS ESPECÍFICOS.

LEGENDA DE SHAFTS

- CLI - Ar Condicionado
- CLI - Pressurização
- HID - Hidráulica/ Incêndio
- ELE - Elétrica
- EUT - Automação/ Telecom
- EXT - Exaustão Churrasqueiras

LEGENDA DE FORRO E PISO

- AMBIENTE COM FORRO (VER ACAB. PROJ. ESPECÍFICOS INT/PSG)
- PROJEÇÃO CAMINHOS INSTALAÇÕES
- PARTIDA PAGINAÇÃO (PARA REVESTIMENTOS DE PAREDE SEGUIR PAGINAÇÃO DO PISO)

NÚMERO	DATA	MODIFICAÇÃO	NOME
R04	18/11/22	SOLICITAÇÃO EVEN AJUSTE CAIXILHOS E GRADIS PARA ACESSO AOS JARDINS	EQ
R03	19/01/22	INDICAÇÃO DE PREVISÃO DE CONTRAPISO ACÚSTICO NA ACADEMIA	EQ
R02	03/09/21	TROCADORES DE CALOR ELIMINADOS E INIDCAÇÃO DE NOTA BLOCOS GRAUTEADOS PARA APOIO AL23/AL24/AL26	EQ
R01	02/07/21	INCLUSÃO AL35	EQ
R00	14/06/21	EMISSÃO INICIAL	EQ

EMPREENDIMENTO
CLĀRI

CLIENTE
even

NOME/ ENDEREÇO EMPREENDIMENTO
ARTUR DE AZEVEDO
RUA JOÃO MOURA, 502, 512 e 518
RUA ARTUR DE AZEVEDO, 527
RUA CRISTIANO VIANA, 295

No PROJETO: 19640
ÁREA TÉCNICA: ARQUITETURA

TÍTULO DO DESENHO
TORRE 01 - PLANTA DO 3º PAVIMENTO

DATA INICIAL FASE: 31/08/2021
FASE DO PROJETO: LO

PROJETISTA
aflalo gasperini / arquitetos

No FOLHA: AQ 1106 R04
ARQUIVO: ART-AQ-LO -1106 -1LZ -R04

RESPONSÁVEL: LUIZ FELIPE AFLALO HERMAN
COORDENADOR: FABIANO SINIBALDI
DESENHO: EQUIPE
ESCALA: INDICADA

RUA HELENA,235 2° ANDAR VILA OLÍMPIA 04552-050 SAO PAULO SP TEL +55 11 3040 7200 FAX +55 11 3040 7213 ag@aflaloegasperini.com.br