



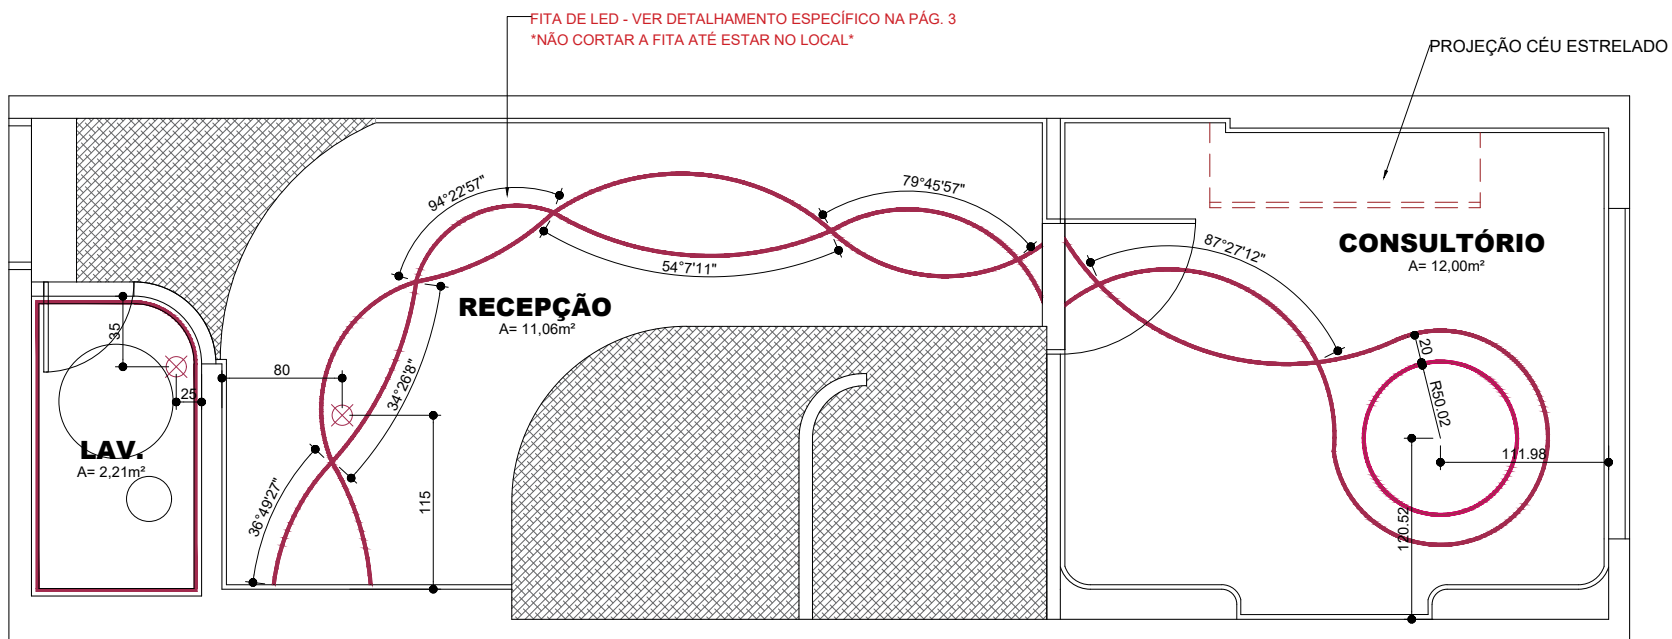

PLANTA BAIXA - LUMINOTÉCNICO
ESCALA 1:100

LEGENDA						
Símb.	Descrição	Tipo	Acabam.	Lampada	Fluxo Lumin.	Temp. Cor
	PERFIL PARA FITA DE LED	EMBURIR	BRANCO	FITA DE LED	1000lm/m	4000K
	ESPERA PARA PENDENTE	ESPERA	-	-	-	4000K

*Conferir medidas no local.

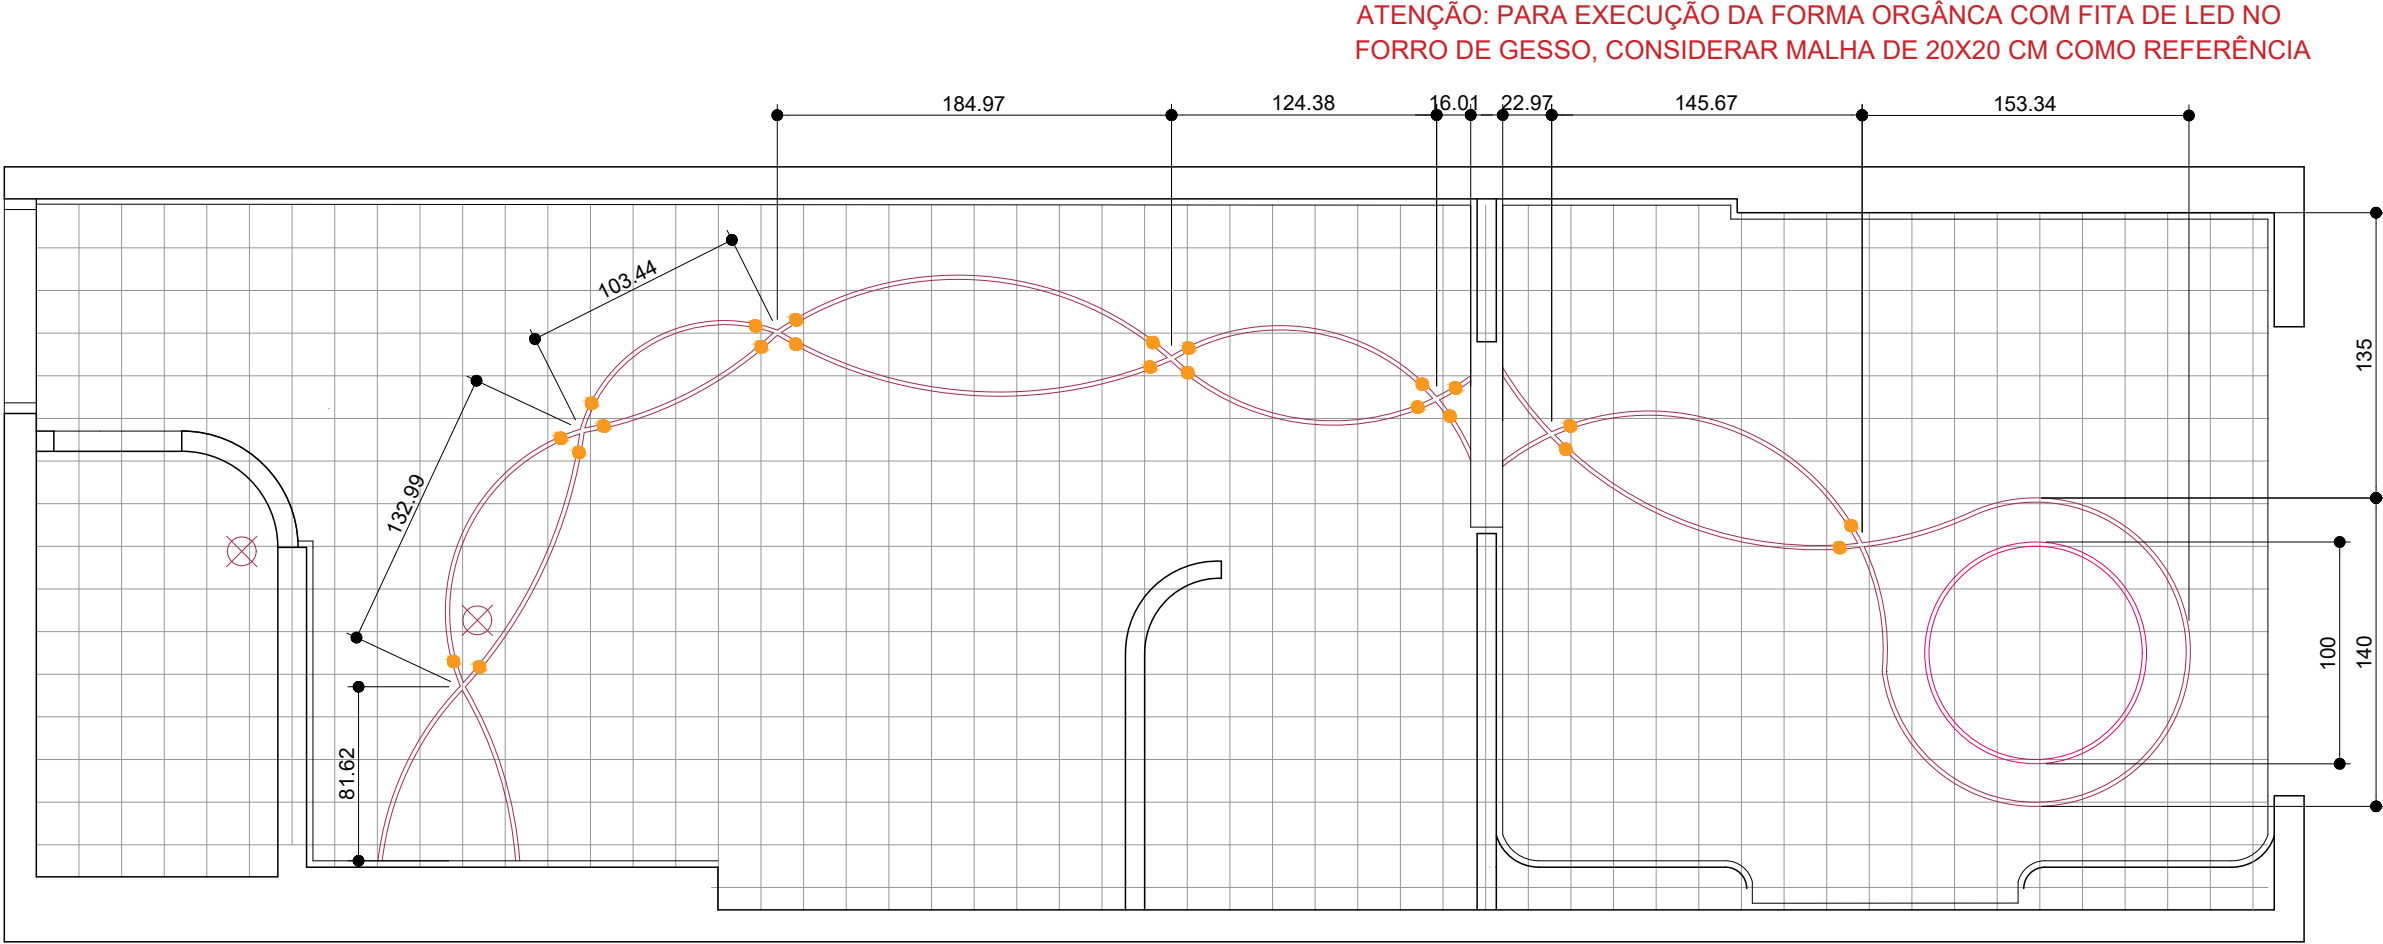

DETALHAMENTO - ILUMINAÇÃO COM FORMA ORGÂNICA
ESCALA 1:100

● PONTO ONDE SE INICIA OU TERMINA UM ARCO