



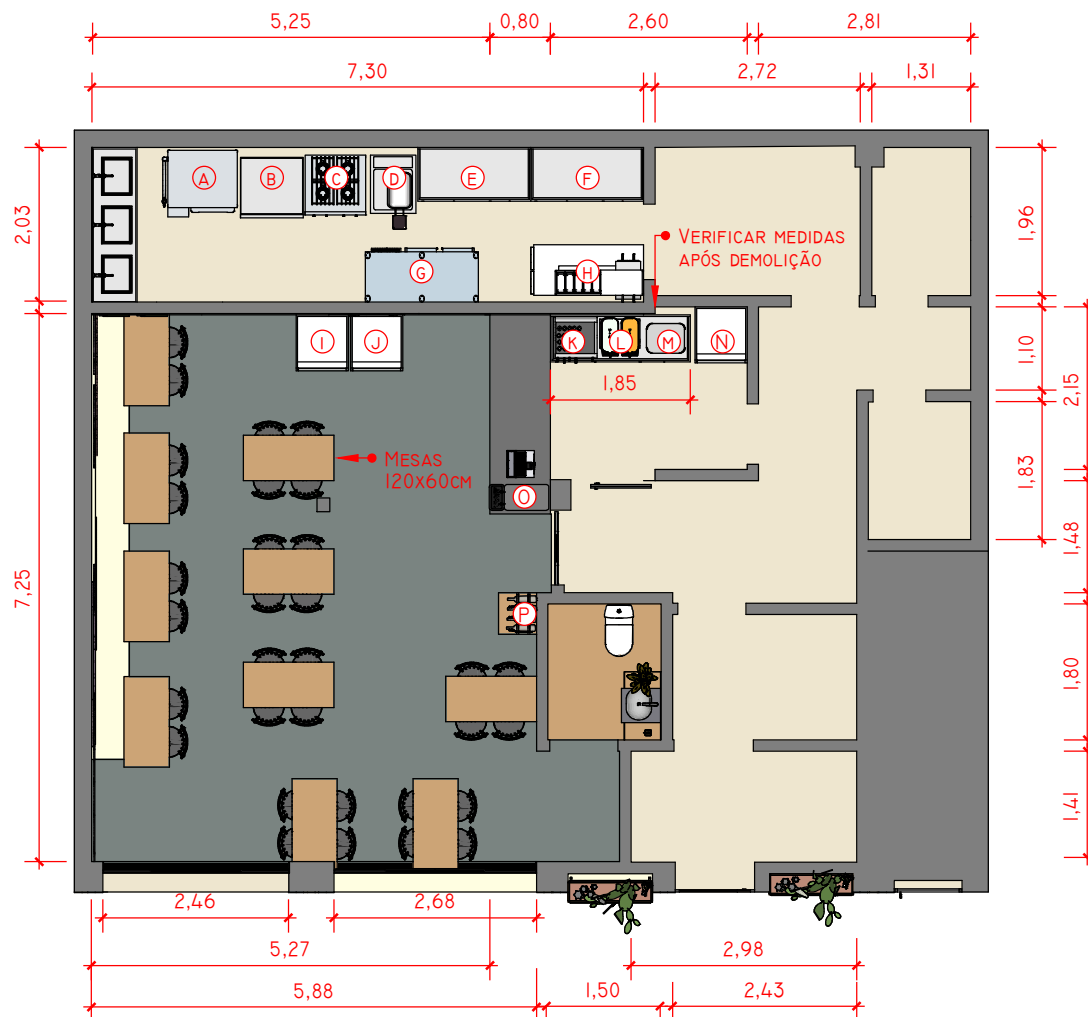

EQUIPAMENTO	DESCRIÇÃO
A	FORNO COMBINADO
B	CHAPA À GÁS
C	FOGÃO 4 BOCAS
D	FRITADEIRA
E	REFRIGERADOR HORIZONTAL
F	REFRIGERADOR HORIZONTAL
G	REFRIGERADOR VERTICAL
H	MESA INOX
I	GELADEIRA VERTICAL EXPOSITORA
J	GELADEIRA VERTICAL EXPOSITORA
K	CAFETEIRA
L	REFRESQUEIRA
M	BALCÃO REFRIGERADO COM CUBA
N	FREEZER VERTICAL
O	CHOPPEIRA
P	ADEGA REFRIGERADA




TÍTULO:	PLANTA DE LAYOUT HUMANIZADO - MEDIDAS	ENDEREÇO:	RUA MINISTRO FERREIRA ALVES, 438
PROPRIETÁRIO:	LA CHOLITA	ESCALA:	1:75
RESPONSÁVEL TÉCNICO:	JULIANA PADILLA	FOLHA:	1
		DESENHISTA:	JULIANA PADILLA
		DATA:	26.03.2025

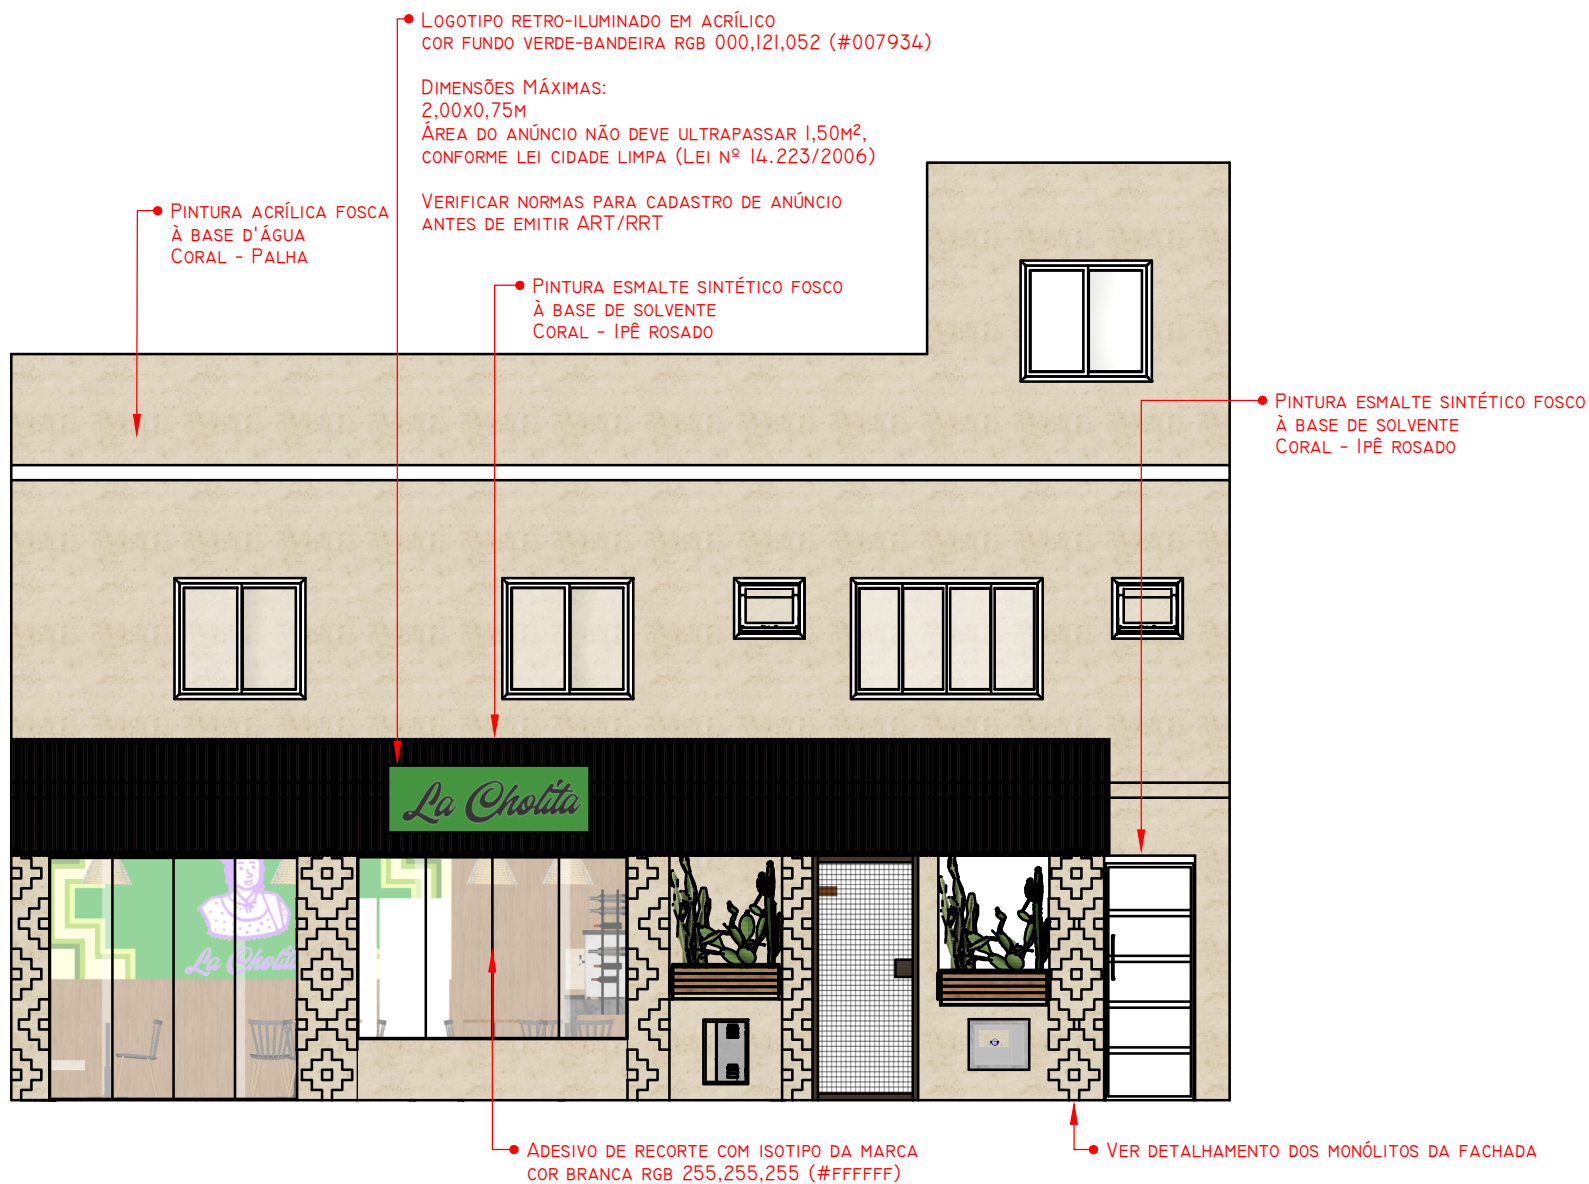


TÍTULO:	FACHADA - COMUNICAÇÃO VISUAL	ENDEREÇO:	RUA MINISTRO FERREIRA ALVES, 438
PROPRIETÁRIO:	LA CHOLITA	ESCALA:	1:75
RESPONSÁVEL TÉCNICO:	JULIANA PADILLA	FOLHA:	2
		DESENHISTA:	JULIANA PADILLA
		DATA:	26.03.2025



VISTA DA FACHADA
ESC: 1:50

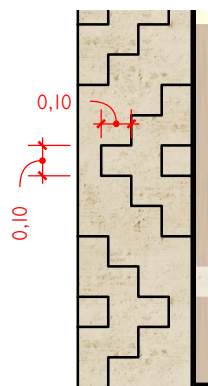

DETALHE MONOLITOS CHAKANA
ESC: 1:25

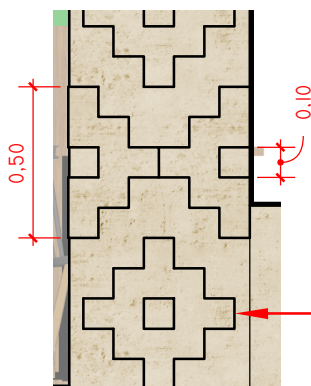

DETALHE MONOLITOS CHAKANA
ESC: 1:25

- JARDINEIRA COM ESPÉCIES DE BAIXA MANUTENÇÃO
- ESPÉCIES SUGERIDAS:
 - CACTO-MONSTRO-PERUANO: *CEREUS PERUVIANUS MONSTRUOSUS*
 - CACTO-DO-PERU: *CEREUS REPANDUS*
 - CACTO-DE-SÃO-PEDRO: *ECHINOPSIS PERUVIANA*
 - CACTO-PALMA: *OPUNTIA FÍCUS INDICA*
 - CACTO -DE-SANTA-RITA: *OPUNTIA VIOLÁCEA*
 - PITAYA-TIÚ: *SELENICEREUS SETACEUS*

- PREVER RETRO-ILUMINAÇÃO, BALIZADORES OU ARANDELAS

- EXECUTAR MONOLITOS COM RECORTES DE CHAPA DE DRYWALL RU (RESISTENTE A UMIDADE)
APLICAR PARA ACABAMENTO MASSA ACRÍLICA



TÍTULO:

FACHADA - DETALHAMENTOS

PROPRIETÁRIO:

LA CHOLITA

RESPONSÁVEL TÉCNICO:

JULIANA PADILLA

ENDEREÇO:

RUA MINISTRO FERREIRA ALVES, 438

ESCALA:

INDICADA

FOLHA:

3

DESENHISTA:

JULIANA PADILLA

DATA:

26.03.2025