


01 - CONFERIR MEDIDAS NO LOCAL ANTES DA EXECUÇÃO. 02 - CONFIRMAR ESPECIFICAÇÕES E DIMENSÕES CORRETAS E DIMENSÕES EXECUTIVAS. 03 - CONFIRMAR ESPECIFICAÇÕES E DIMENSÕES CORRETAS E DIMENSÕES EXECUTIVAS. 04 - QUALQUER INCOMPATIBILIDADE EXECUTIVA, A ARQUITETA DEVERÁ SER CONTATADA ANTES DA EXECUÇÃO.

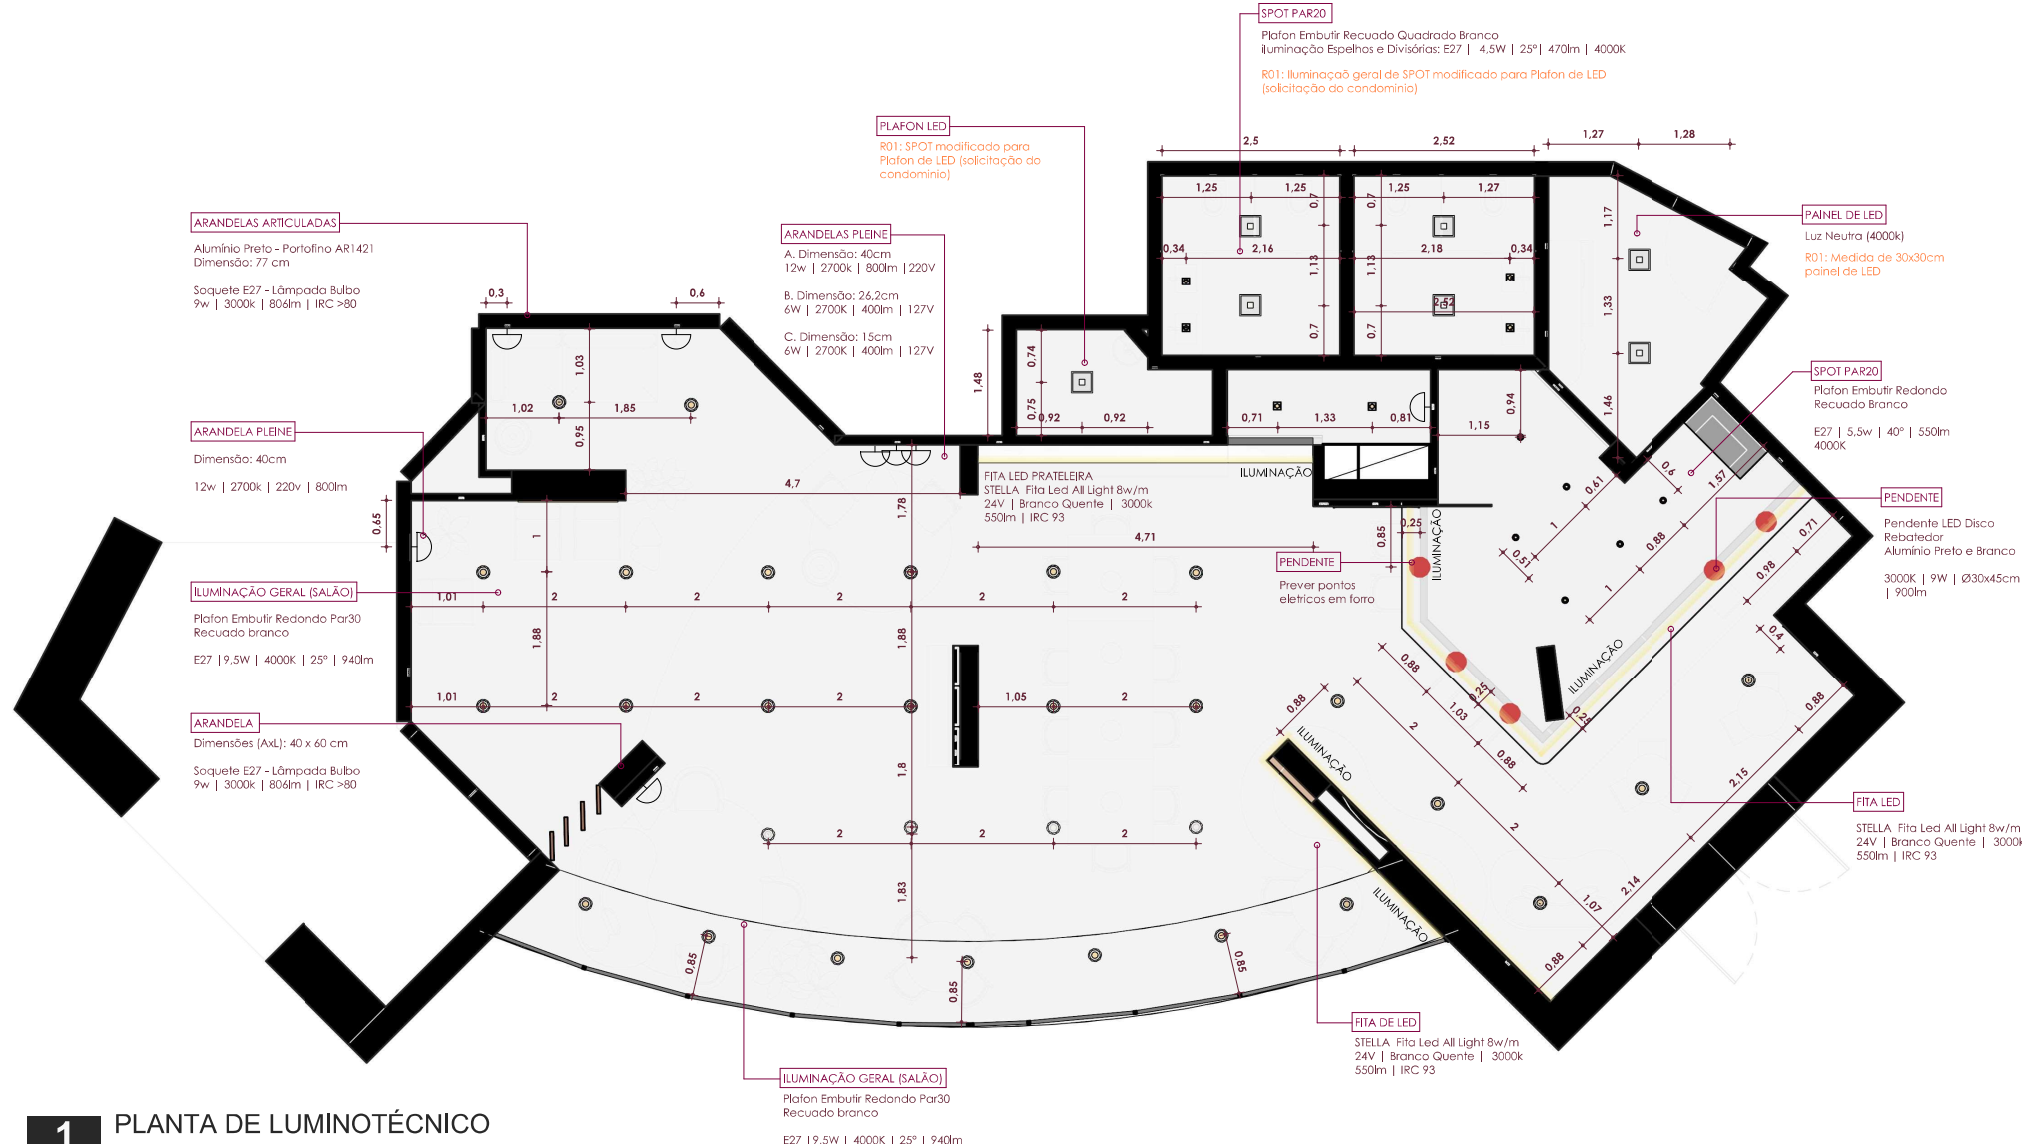

1 PLANTA DE LUMINOTÉCNICO
Escala: 1 : 75

SALÃO DE FESTAS CCI		STATUS: EXECUTIVO CONTEÚDO: PLANTA LUMINOTÉCNICO	DATA: 13/01/2025 ESCALA: 1 : 75	02C1 MALVAARQUITETURA-ADM@GMAIL.COM <u>@MALVA_ARQUITETURA</u>		MALVA arquitetura					
ENDEREÇO: Alameda dos Jurupis, 900 - Moema											
CCI							MALVA ARQUITETURA				