





PLANTA DE ARQUITETURA

RESIDENCIAL RESERVA CIDADE MAIA
TORRE ATLÂNTICA OPÇÃO 5 - FINAIS 1 E 3

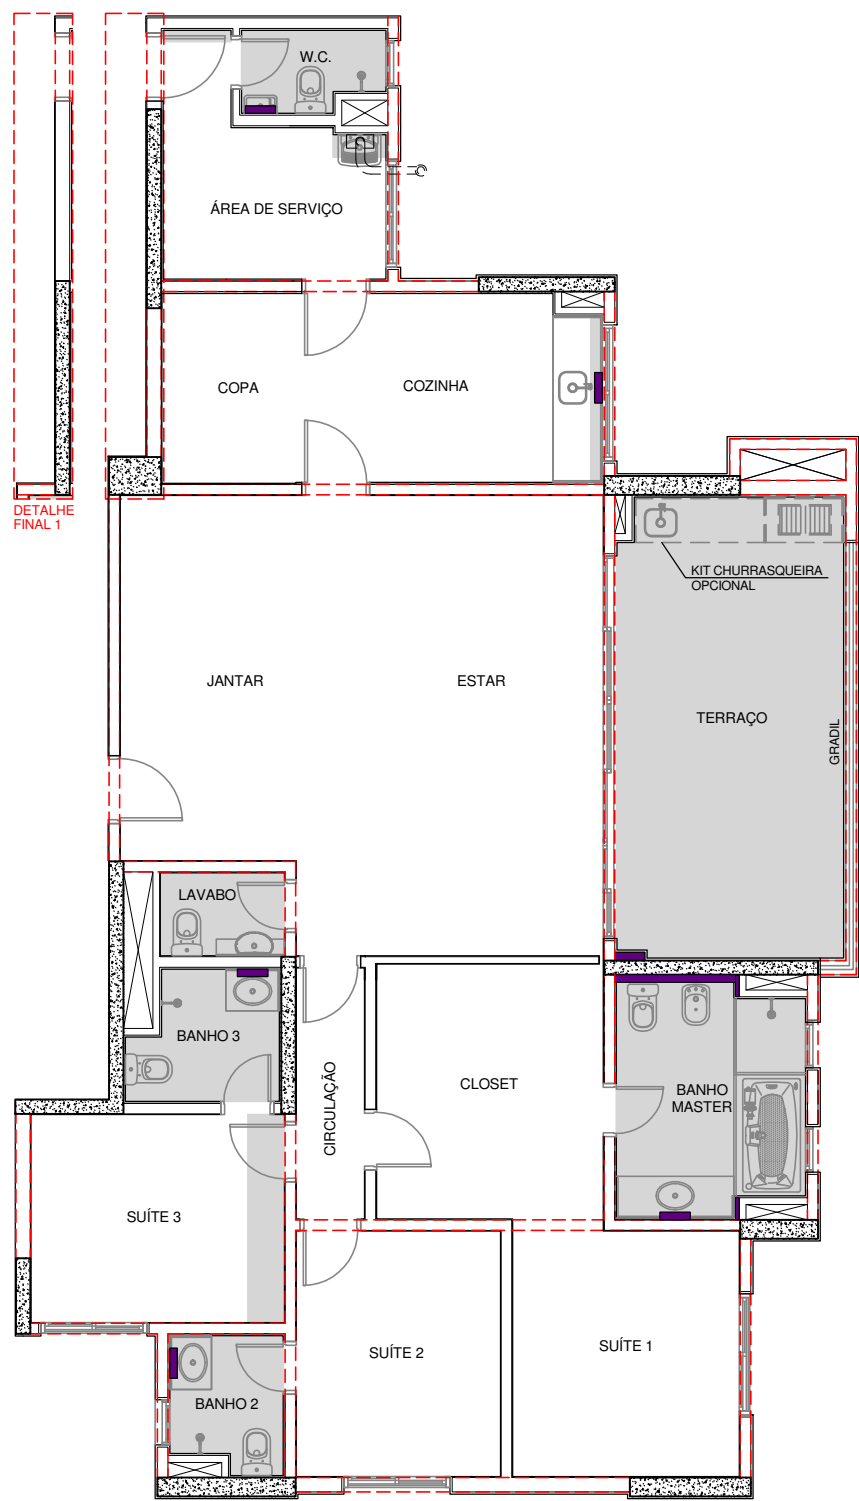


LEGENDA

ESCALA: 1 : 100

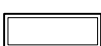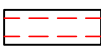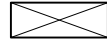	ÁREAS COM FORRO / SANCA DE GESSO		ALVENARIA
	PILAR DE CONCRETO		PROJEÇÃO DE VIGA
	CARENAGEM		PROJEÇÃO
	VAZIO / SHAFT		

PLANTA DE ELÉTRICA

RESIDENCIAL RESERVA CIDADE MAIA
TORRE ATLÂNTICA OPÇÃO 5 - FINAIS 1 E 3

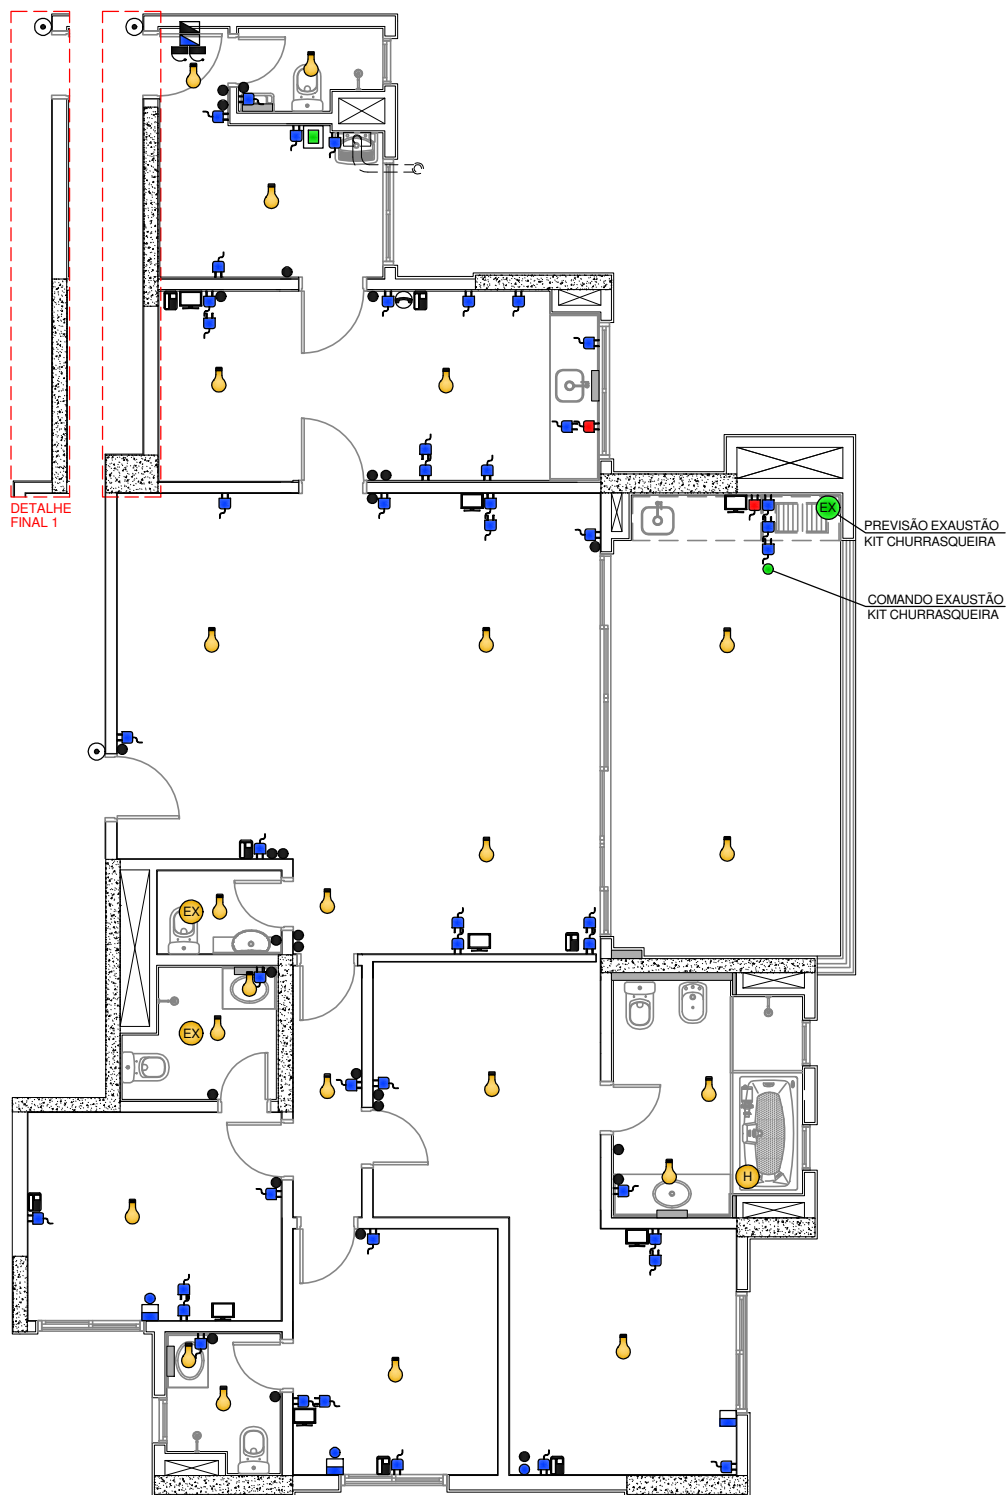

LEGENDA

OBS: NÃO SE DEVE EXECUTAR FUIROS NA REGIÃO DO QUADRO DE LUZ E FORÇA

	PONTO PARA ILUMINAÇÃO DE TETO		PONTO PARA TELEFONE		BOTÃO DA CAMPAINHA
	INTERRUPTOR DE LUZ		PONTO PARA INTERFONE		CAMPAINHA DE PAREDE
	QUADRO DE LUZ E FORÇA		PONTO PARA MEDIÇÃO DE GÁS		TOMADA 127V
	QUADRO DE SISTEMAS		PREVISÃO EXAUSTÃO KIT CHURRASQUEIRA		TOMADA 220V
	PONTO PARA TV		COMANDO EXAUSTÃO KIT CHURRASQUEIRA		PONTO DE FORÇA PARA PERSIANA
	COMANDO DA PERSIANA		PONTO PARA HIDROMASSAGEM		


QUADRO DE LUZ E FORÇA

RESIDENCIAL RESERVA CIDADE MAIA
TORRE ATLÂNTICA OPÇÃO 5

CIRCUITO	DESCRIÇÃO	CORRENTE (A)	POTÊNCIA (KVA)	TENSÃO (V)
1	SUÍTES 1, 2 E 3 / BANHOS 1, 2 E 3	16	1,18	127
2	JANTAR/ESTAR/TERRAÇO/LAVABO/CIRC./CAMPAINHA	16	1,18	127
3	COZINHA/A.SERVIÇO/W.C./HALL/CAMPAINHA	16	0,61	127
4	SUÍTE 1/BANHO 1/CLOSET/CIRCULAÇÃO/PREV.PERSIANA	16	1,20	127
5	SUÍTE 2/BANHO 2/PREV.PERSIANA	16	1,00	127
6	SUÍTE 3/BANHO 3/PREV.PERSIANA	16	1,00	127
7	ESTAR	16	1,00	127
8	CIRCULAÇÃO / ESTAR / JANTAR	16	1,00	127
9	TERRAÇO/PREV.EXAUTÃO	20	1,40	127
10	COZINHA/FILTRO	20	1,50	127
11	COZINHA	20	1,40	127
12	ÁREA DE SERVIÇO / W.C.	20	1,30	127
13	MICROONDAS	20	1,20	127
14	MÁQUINA DE LAVAR LOUÇA	20	2,00	220
15	MÁQUINA LAVA-SECA	20	2,50	127
16	PREVISÃO AR CONDICIONADO	20	1,50	220
17	COOKTOP	20	3,00	220
18	HIDROMASSAGEM	20	0,60	220
R	RESERVA	-	-	-
R	RESERVA	-	-	-
R	RESERVA	-	-	-
R	RESERVA	-	-	-
R	RESERVA	-	-	-



PLANTA DE AR CONDICIONADO E EXAUSTÃO

RESIDENCIAL RESERVA CIDADE MAIA
TORRE ATLÂNTICA OPÇÃO 5 - FINAIS 1 E 3

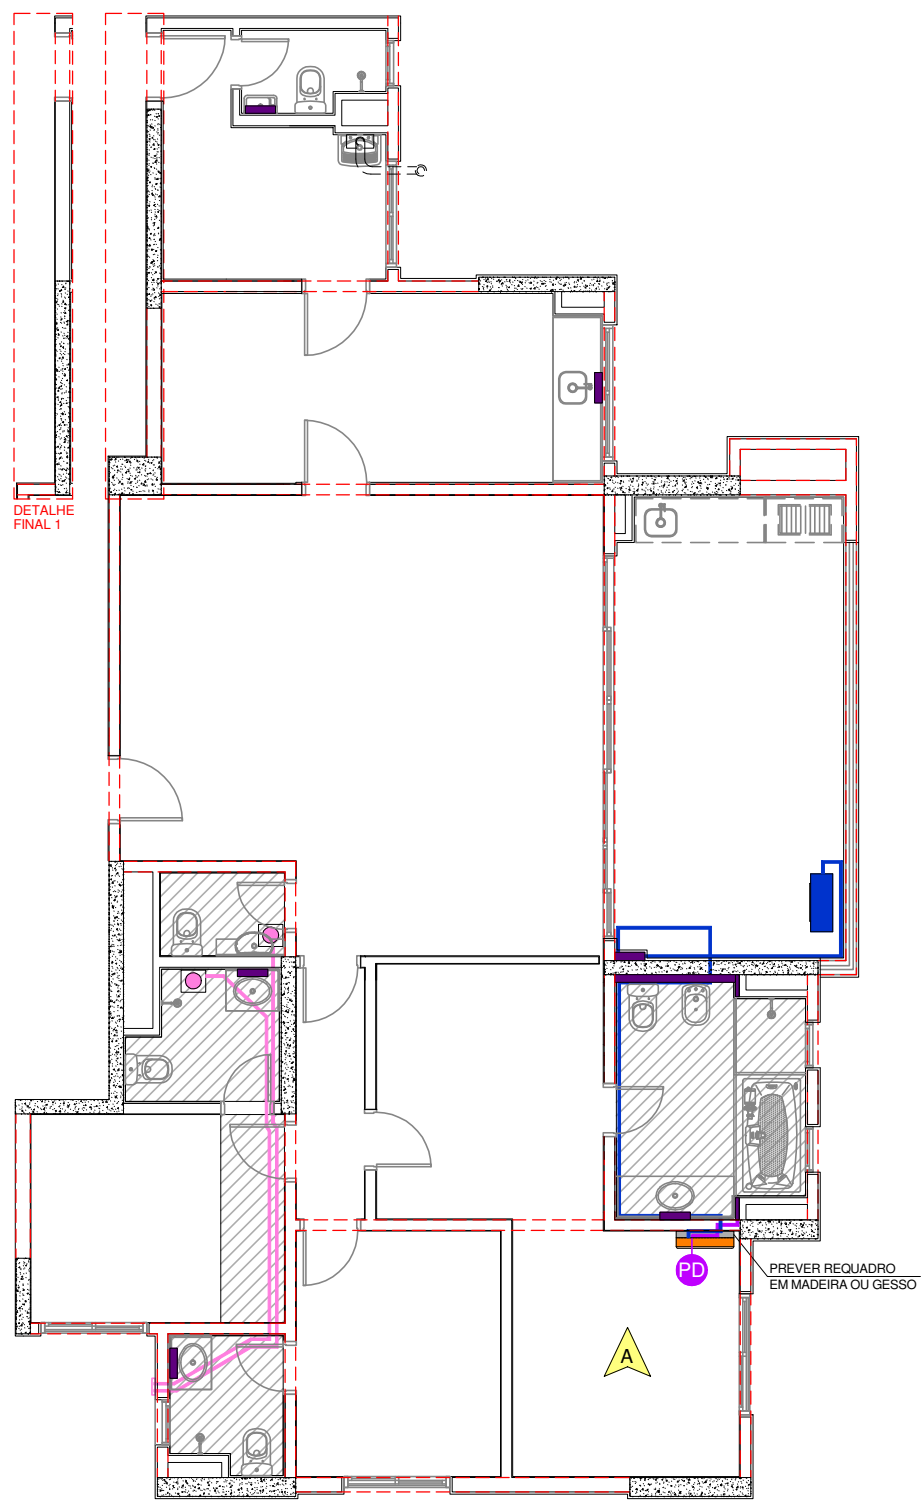

LEGENDA

PONTOS

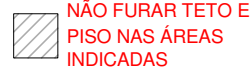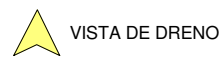

PREVISÃO PARA TUBULAÇÃO FRIGORÍGENA

LOCAL PREVISTO P/ INSTALAÇÃO DA CONDENSADORA DE AR CONDICIONADO

LOCAL PREVISTO P/ INSTALAÇÃO DA EVAPORADORA DE AR CONDICIONADO DE PAREDE

TUBULAÇÃO DE DRENO

TUBULAÇÃO DO EXAUSTOR NO TETO

PONTO DO EXAUSTOR

OBS: REDE FRIGORÍGENA INSTALADA SOMENTE PARA OS PROPRIETÁRIOS QUE ADQUIRIRAM O KIT!


OBS.: NÃO EXECUTAR FUROS NA REGIÃO DAS PRUMADAS!

LEMBRE-SE DE QUE OS ENCANAMENTOS QUE PASSAM POR UMA PAREDE HIDRÁULICA, MOSTRADA NOS BANHOS, COZINHA ETC., TAMBÉM ESTÃO PASSANDO POR ESTA MESMA PAREDE NA ÁREA SECA VIZINHA. NAS COLOCAÇÕES DOS ARMÁRIOS, TOMAR TODOS OS CUIDADOS POSSÍVEIS.

ATENÇÃO: USAR LIMITADOR DE BROCA E NÃO ULTRAPASSAR 2 CM DE PROFUNDIDADE!

PLANTA DE PRUMADAS E GÁS

RESIDENCIAL RESERVA CIDADE MAIA
TORRE ATLÂNTICA OPÇÃO 5 - FINAIS 1 E 3

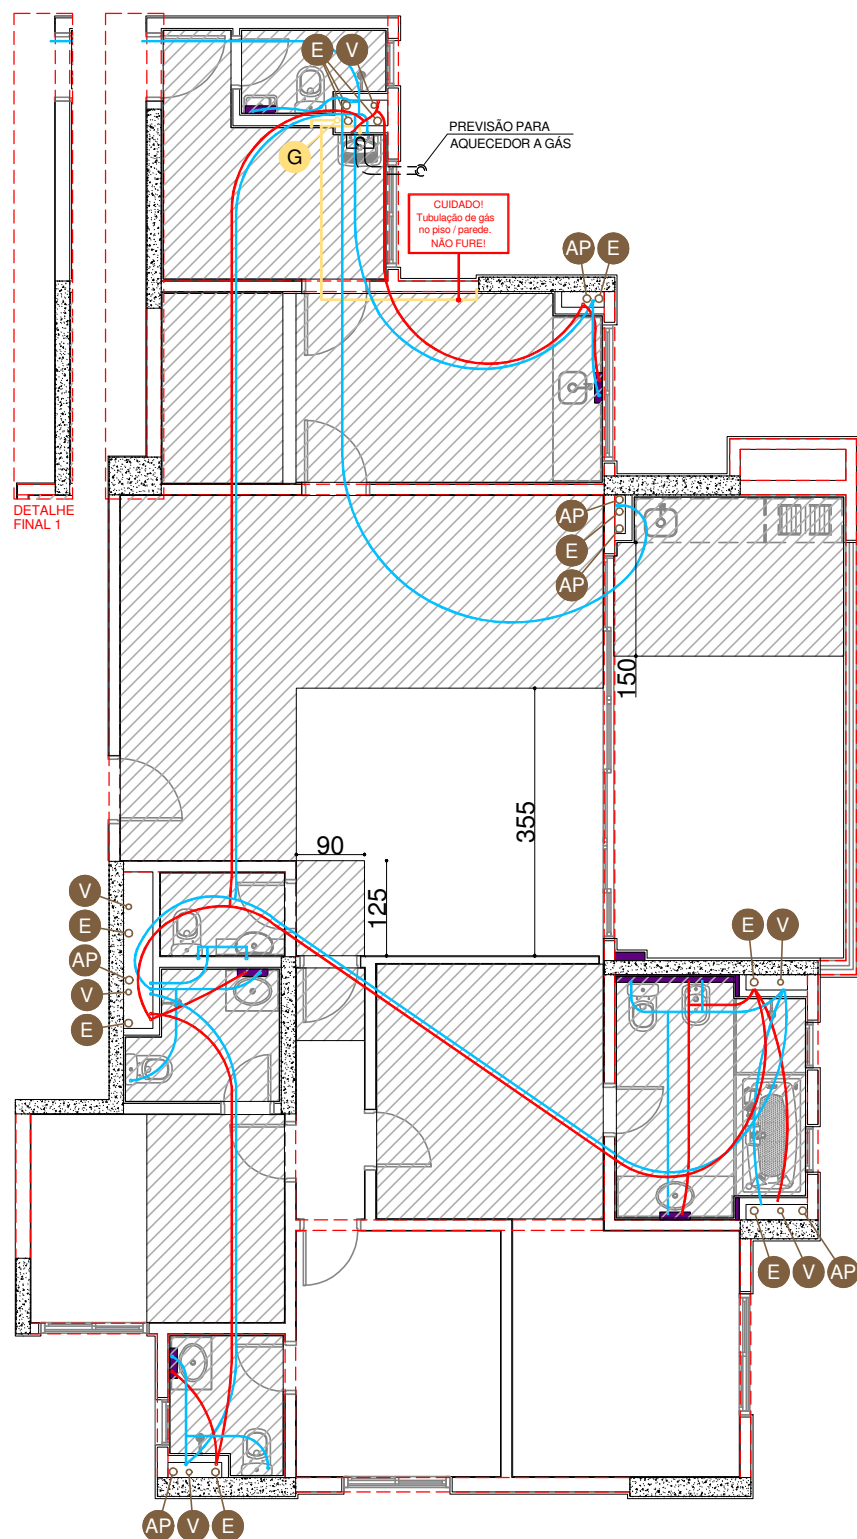

LEGENDA

PRUMADAS

V	VENTILAÇÃO
E	ESGOTO
AP	ÁGUA PLUVIAL
G	GÁS

NÃO FURAR TETO E PISO
NAS ÁREAS INDICADAS

—	TUBULAÇÃO DE GÁS NO PISO/PAREDE
—	TUBULAÇÃO DE ÁGUA FRIA
—	TUBULAÇÃO DE ÁGUA QUENTE


OBS.: NÃO EXECUTAR FUROS NA REGIÃO DAS PRUMADAS!

LEMBRE-SE DE QUE OS ENCANAMENTOS QUE PASSAM POR UMA PAREDE HIDRÁULICA, MOSTRADA NOS BANHOS, COZINHA ETC., TAMBÉM ESTÃO PASSANDO POR ESTA MESMA PAREDE NA ÁREA SECA VIZINHA. NAS COLOCAÇÕES DOS ARMÁRIOS, TOMAR TODOS OS CUIDADOS POSSÍVEIS.


ATENÇÃO: USAR LIMITADOR DE BROCA E NÃO ULTRAPASSAR 2 CM DE PROFUNDIDADE!

ESQUEMA DO DRENO

RESIDENCIAL RESERVA CIDADE MAIA
TORRE ATLÂNTICA OPÇÃO 5 - FINAIS 1 E 3
SUÍTE 1

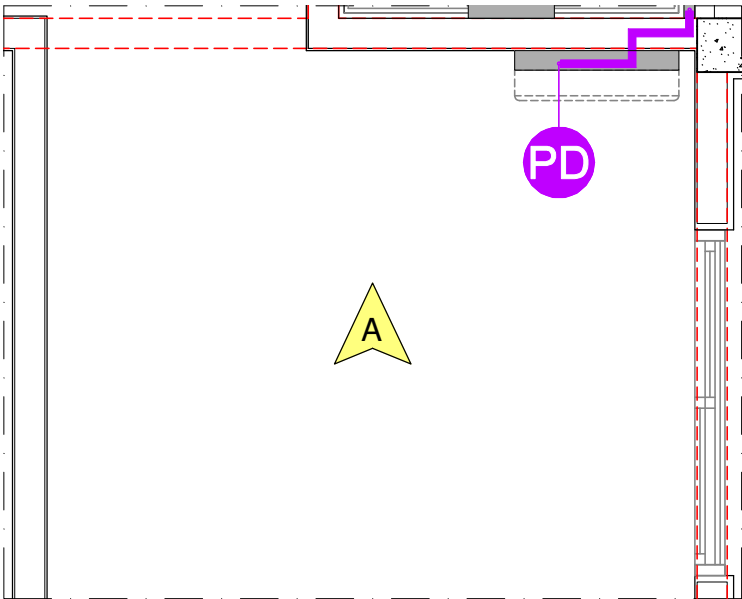

PLANTA

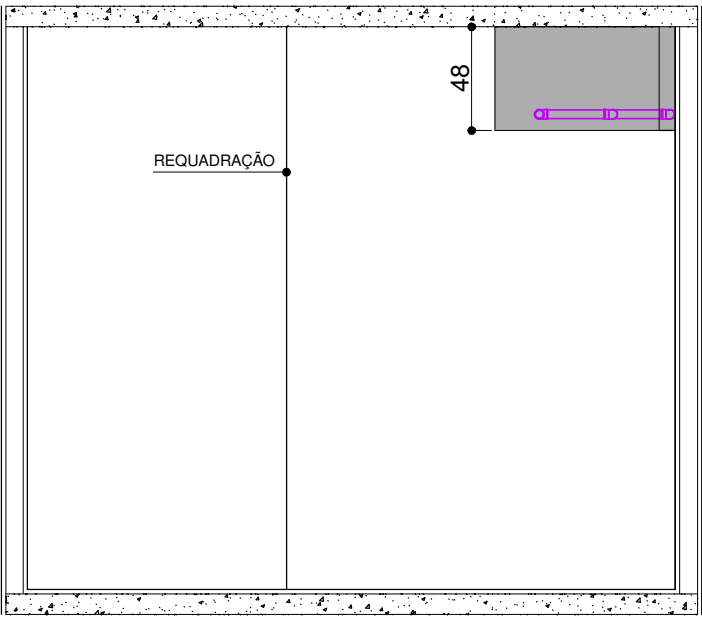


VISTA A

LEGENDA

PRUMADAS



TUBULAÇÕES

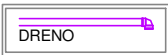

OBSERVAÇÕES:

AS MEDIDAS INDICADAS NAS VISTAS ESTÃO EM CENTÍMETROS.

ANTES DE FURAR:

USAR LIMITADOR DE BROCA E NÃO ULTRAPASSAR 2 CM DE PROFUNDIDADE.
LEMBRE-SE QUE OS ENCANAMENTOS QUE PASSAM NA PAREDE ACIMA
TAMBÉM ESTÃO PASSANDO POR ESTA MESMA PAREDE NO LADO OPOSTO.
CONSULTE A PLANTA DE PRUMADAS.

NÃO FURAR NAS ÁREAS
INDICADAS NA COR CINZA






CONCRETO



VISTA

ESQUEMA HIDRÁULICO

RESIDENCIAL RESERVA CIDADE MAIA
TORRE ATLÂNTICA OPÇÃO 5 - FINAIS 1 E 3
BANHO MÁSTER

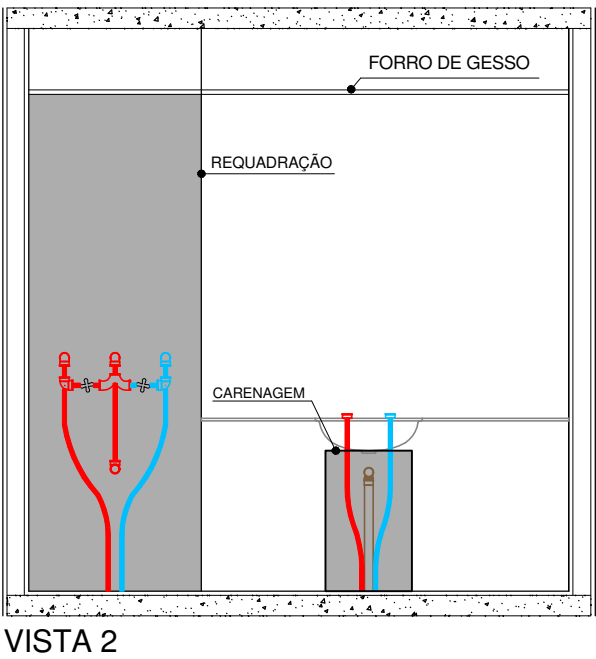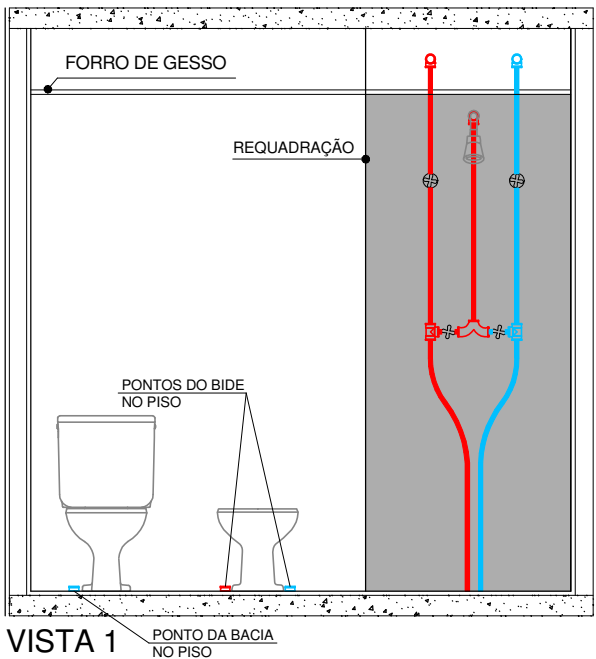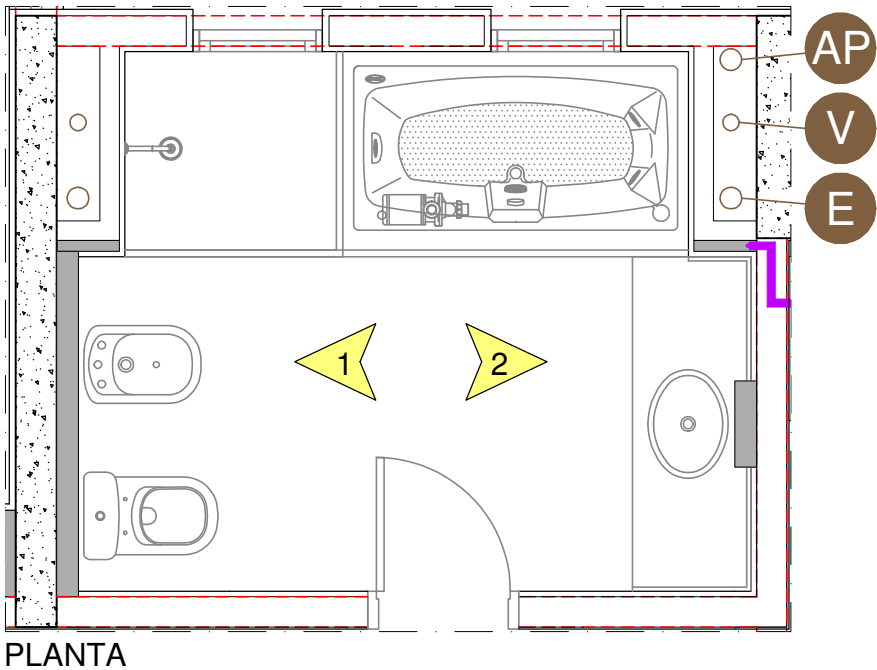

LEGENDA

PRUMADAS

V	VENTILAÇÃO
E	ESGOTO
AP	ÁGUA PLUVIAL
G	GÁS

TUBULAÇÕES

ÁGUA FRIA - PEX
ÁGUA QUENTE - PEX
ÁGUA FRIA
ESGOTO
GÁS
DRENO

OBSERVAÇÕES:

NAS MEDIDAS ACIMA, USE COMO REFERÊNCIA OS PONTOS APARENTES DE ÁGUA, GÁS, ESGOTO E REGISTROS.
AS MEDIDAS INDICADAS NAS VISTAS ESTÃO EM CENTÍMETROS.




ANTES DE FURAR:

USAR LIMITADOR DE BROCA E NÃO ULTRAPASSAR 2 CM DE PROFUNDIDADE.
LEMBRE-SE QUE OS ENCANAMENTOS QUE PASSAM NA PAREDE ACIMA
TAMBÉM ESTÃO PASSANDO POR ESTA MESMA PAREDE NO LADO OPOSTO.
CONSULTE A PLANTA DE PRUMADAS.
NÃO FURE AS SANCAS E FORROS DE GESSO POIS ELES TAMBÉM ABRIGAM
TUBULAÇÕES HIDRÁULICAS.

■	NÃO FURAR NAS ÁREAS INDICADAS NA COR CINZA
■	CONCRETO
▲	VISTA

ESQUEMA HIDRÁULICO

RESIDENCIAL RESERVA CIDADE MAIA
TORRE ATLÂNTICA OPÇÃO 5 - FINAIS 1 E 3
BANHO 2

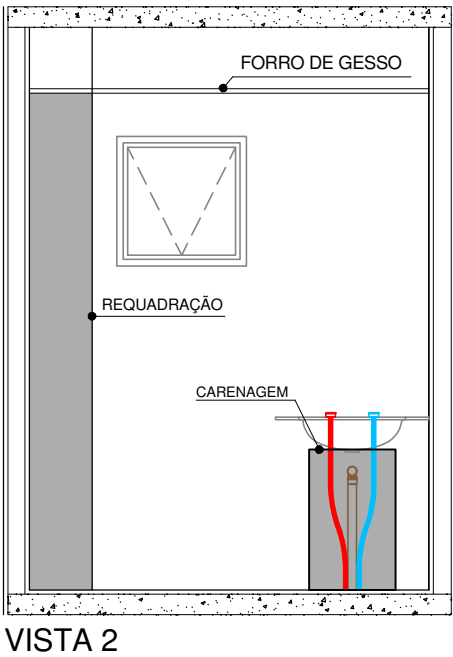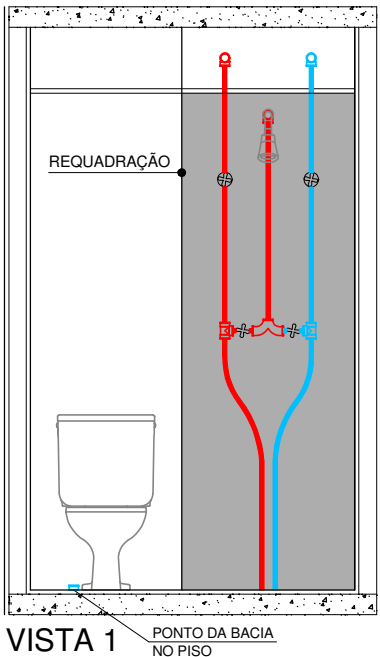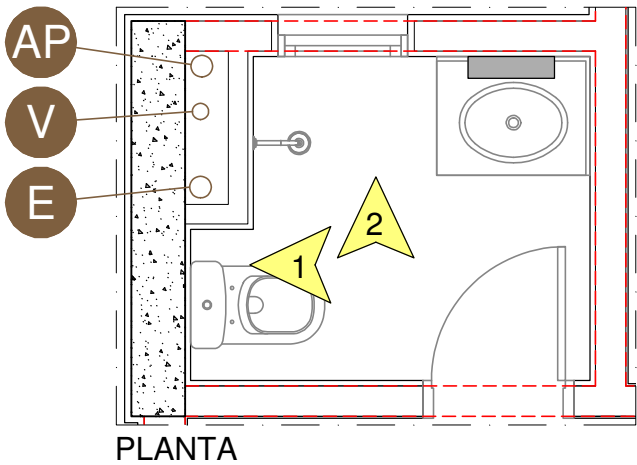

LEGENDA

PRUMADAS

V	VENTILAÇÃO
E	ESGOTO
AP	ÁGUA PLUVIAL
G	GÁS

TUBULAÇÕES

ÁGUA FRIA - PEX
ÁGUA QUENTE - PEX
ÁGUA FRIA
ESGOTO
GÁS
DRENO

OBSERVAÇÕES:

NAS MEDIDAS ACIMA, USE COMO REFERÊNCIA OS PONTOS APARENTES DE ÁGUA, GÁS, ESGOTO E REGISTROS.
AS MEDIDAS INDICADAS NAS VISTAS ESTÃO EM CENTÍMETROS.


ANTES DE FURAR:

USAR LIMITADOR DE BROCA E NÃO ULTRAPASSAR 2 CM DE PROFUNDIDADE.
LEMBRE-SE QUE OS ENCANAMENTOS QUE PASSAM NA PAREDE ACIMA
TAMBÉM ESTÃO PASSANDO POR ESTA MESMA PAREDE NO LADO OPOSTO.
CONSULTE A PLANTA DE PRUMADAS.
NÃO FURE AS SANCAS E FORROS DE GESSO POIS ELES TAMBÉM ABRIGAM
TUBULAÇÕES HIDRÁULICAS.


■	NÃO FURAR NAS ÁREAS INDICADAS NA COR CINZA
■	CONCRETO
▲	VISTA

ESQUEMA HIDRÁULICO


RESIDENCIAL RESERVA CIDADE MAIA
TORRE ATLÂNTICA OPÇÃO 5 - FINAIS 1 E 3
BANHO 3

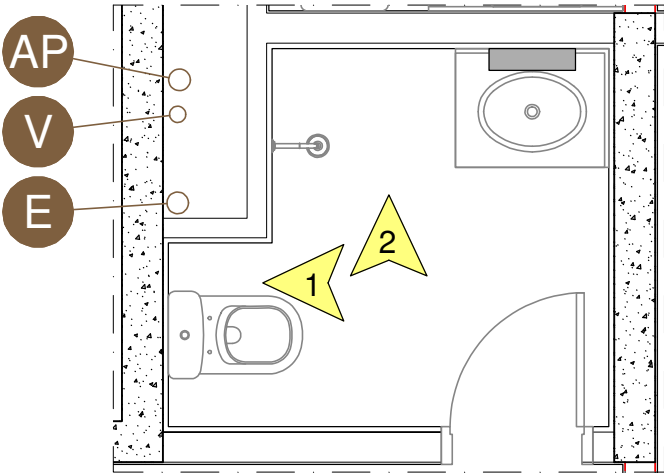

PLANTA

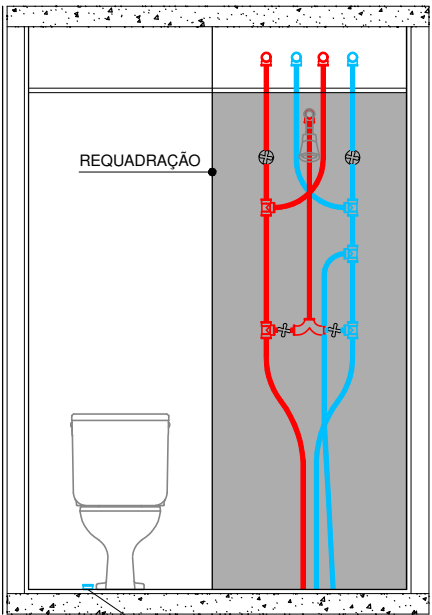

VISTA 1

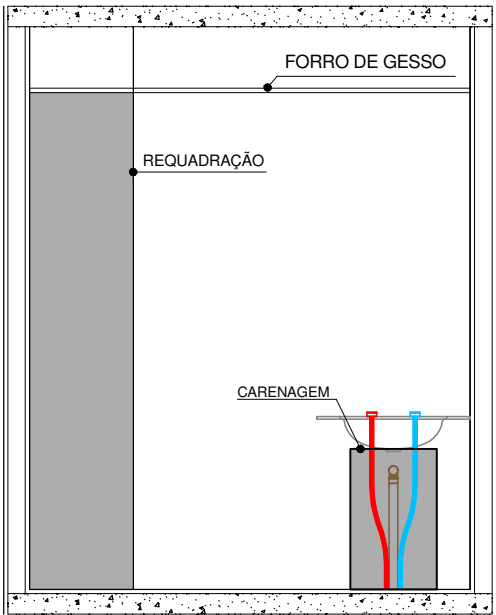

VISTA 2

LEGENDA

PRUMADAS

V	VENTILAÇÃO
E	ESGOTO
AP	ÁGUA PLUVIAL
G	GÁS

TUBULAÇÕES

ÁGUA FRIA - PEX
ÁGUA QUENTE - PEX
ÁGUA FRIA
ESGOTO
GÁS
DRENO

OBSERVAÇÕES:

NAS MEDIDAS ACIMA, USE COMO REFERÊNCIA OS PONTOS APARENTES DE ÁGUA, GÁS, ESGOTO E REGISTROS.
AS MEDIDAS INDICADAS NAS VISTAS ESTÃO EM CENTÍMETROS.

ANTES DE FURAR:

USAR LIMITADOR DE BROCA E NÃO ULTRAPASSAR 2 CM DE PROFUNDIDADE.
LEMBRE-SE QUE OS ENCANAMENTOS QUE PASSAM NA PAREDE ACIMA
TAMBÉM ESTÃO PASSANDO POR ESTA MESMA PAREDE NO LADO OPOSTO.
CONSULTE A PLANTA DE PRUMADAS.
NÃO FURE AS SANCAS E FORROS DE GESSO POIS ELES TAMBÉM ABRIGAM
TUBULAÇÕES HIDRÁULICAS.


NÃO FURAR NAS ÁREAS
INDICADAS NA COR CINZA

CONCRETO


VISTA

ESQUEMA HIDRÁULICO

RESIDENCIAL RESERVA CIDADE MAIA
TORRE ATLÂNTICA OPÇÃO 5 - FINAIS 1 E 3
LAVABO

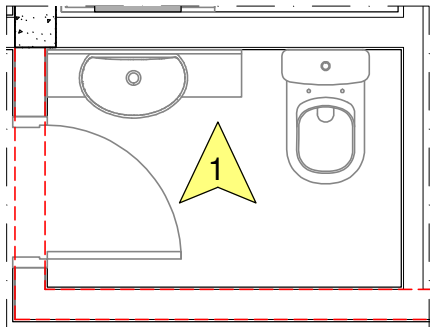

PLANTA

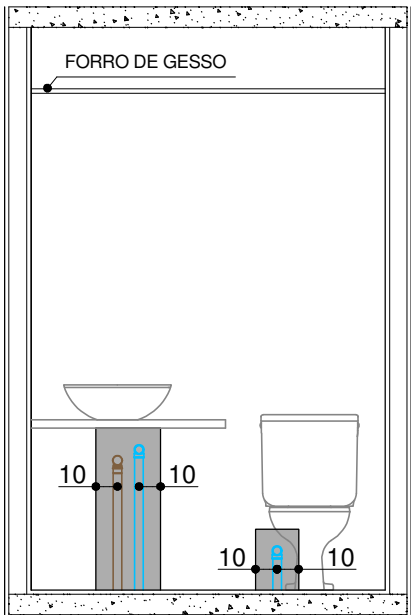

VISTA 1

LEGENDA

PRUMADAS

V	VENTILAÇÃO
E	ESGOTO
AP	ÁGUA PLUVIAL
G	GÁS

TUBULAÇÕES

ÁGUA FRIA - PEX
ÁGUA QUENTE - PEX
ÁGUA FRIA
ESGOTO
GÁS
DRENO

OBSERVAÇÕES:

NAS MEDIDAS ACIMA, USE COMO REFERÊNCIA OS PONTOS APARENTES DE ÁGUA, GÁS, ESGOTO E REGISTROS.
AS MEDIDAS INDICADAS NAS VISTAS ESTÃO EM CENTÍMETROS.

ANTES DE FURAR:

USAR LIMITADOR DE BROCA E NÃO ULTRAPASSAR 2 CM DE PROFUNDIDADE.
LEMBRE-SE QUE OS ENCANAMENTOS QUE PASSAM NA PAREDE ACIMA
TAMBÉM ESTÃO PASSANDO POR ESTA MESMA PAREDE NO LADO OPOSTO.
CONSULTE A PLANTA DE PRUMADAS.
NÃO FURE AS SANCAS E FORROS DE GESSO POIS ELES TAMBÉM ABRIGAM
TUBULAÇÕES HIDRÁULICAS.


NÃO FURAR NAS ÁREAS
INDICADAS NA COR CINZA

CONCRETO


VISTA

ESQUEMA HIDRÁULICO

RESIDENCIAL RESERVA CIDADE MAIA
TORRE ATLÂNTICA OPÇÃO 5 - FINAIS 1 E 3
W.C.

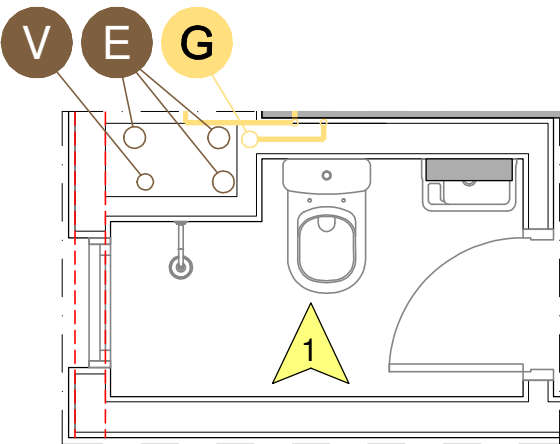

PLANTA

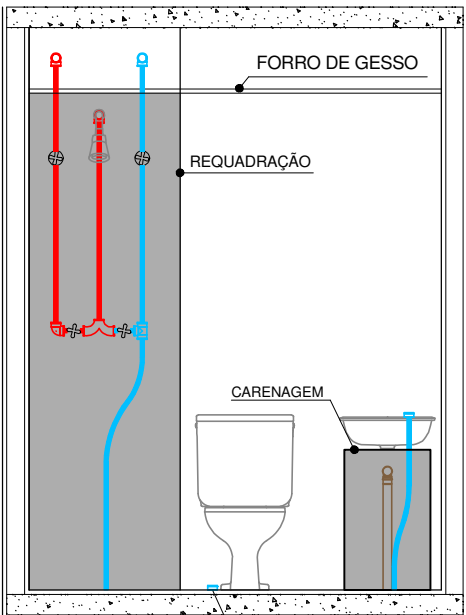

VISTA 1

LEGENDA

PRUMADAS

V	VENTILAÇÃO
E	ESGOTO
AP	ÁGUA PLUVIAL
G	GÁS

TUBULAÇÕES

ÁGUA FRIA - PEX
ÁGUA QUENTE - PEX
ÁGUA FRIA
ESGOTO
GÁS
DRENO

OBSERVAÇÕES:

NAS MEDIDAS ACIMA, USE COMO REFERÊNCIA OS PONTOS APARENTES DE ÁGUA, GÁS, ESGOTO E REGISTROS.
AS MEDIDAS INDICADAS NAS VISTAS ESTÃO EM CENTÍMETROS.

ANTES DE FURAR:

USAR LIMITADOR DE BROCA E NÃO ULTRAPASSAR 2 CM DE PROFUNDIDADE.
LEMBRE-SE QUE OS ENCANAMENTOS QUE PASSAM NA PAREDE ACIMA
TAMBÉM ESTÃO PASSANDO POR ESTA MESMA PAREDE NO LADO OPOSTO.
CONSULTE A PLANTA DE PRUMADAS.
NÃO FURE AS SANCAS E FORROS DE GESSO POIS ELES TAMBÉM ABRIGAM
TUBULAÇÕES HIDRÁULICAS.




NÃO FURAR NAS ÁREAS
INDICADAS NA COR CINZA

CONCRETO

VISTA

ESQUEMA HIDRÁULICO

RESIDENCIAL RESERVA CIDADE MAIA
TORRE ATLÂNTICA OPÇÃO 5 - FINAIS 1 E 3
COZINHA

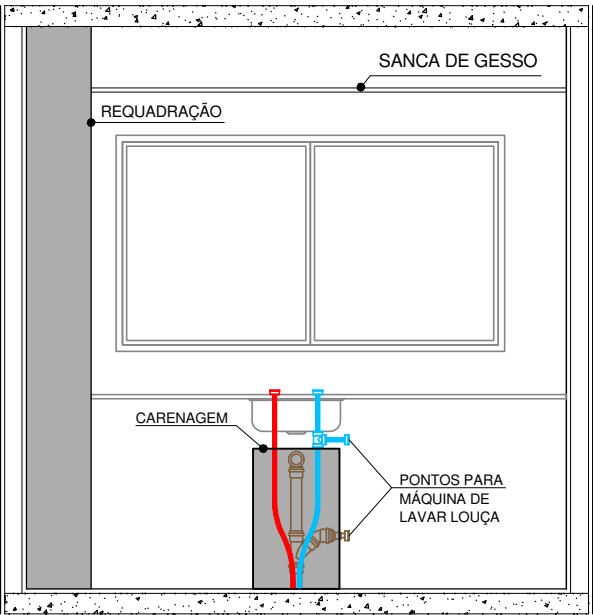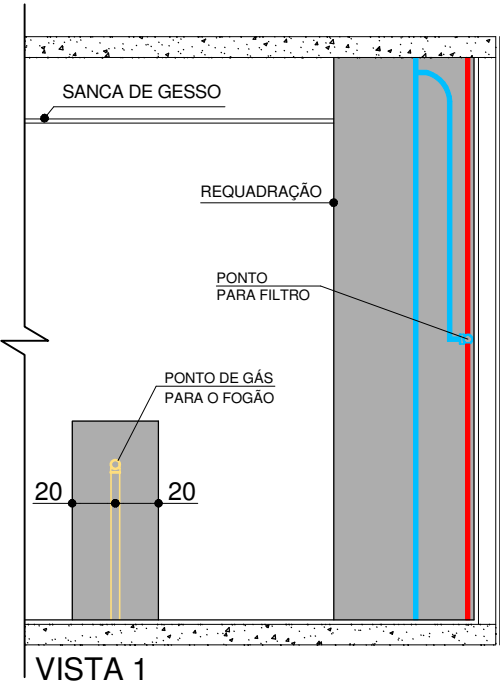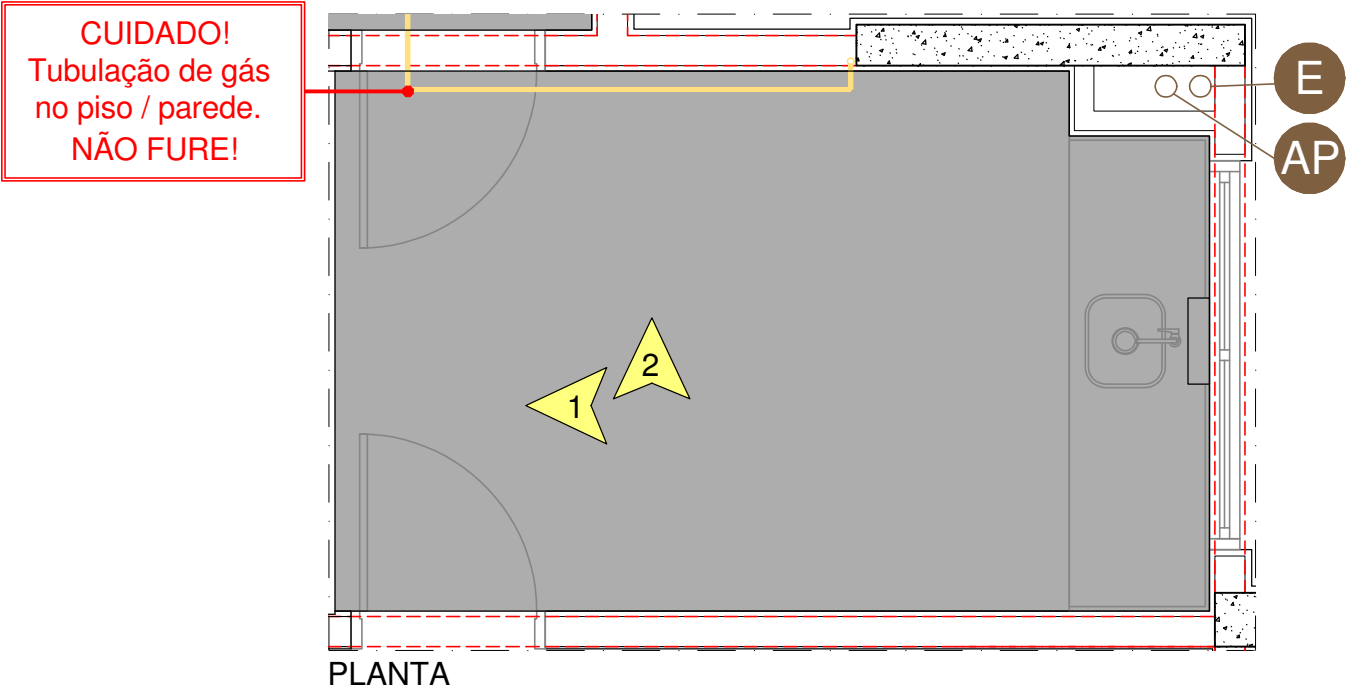

LEGENDA

PRUMADAS

V	VENTILAÇÃO
E	ESGOTO
AP	ÁGUA PLUVIAL
G	GÁS

TUBULAÇÕES

ÁGUA FRIA - PEX
ÁGUA QUENTE - PEX
ÁGUA FRIA
ESGOTO
GÁS
DRENO

OBSERVAÇÕES:

NAS MEDIDAS ACIMA, USE COMO REFERÊNCIA OS PONTOS APARENTES DE ÁGUA, GÁS, ESGOTO E REGISTROS.
AS MEDIDAS INDICADAS NAS VISTAS ESTÃO EM CENTÍMETROS.



ANTES DE FURAR:

USAR LIMITADOR DE BROCA E NÃO ULTRAPASSAR 2 CM DE PROFUNDIDADE.
LEMBRE-SE QUE OS ENCANAMENTOS QUE PASSAM NA PAREDE ACIMA
TAMBÉM ESTÃO PASSANDO POR ESTA MESMA PAREDE NO LADO OPOSTO.
CONSULTE A PLANTA DE PRUMADAS.
NÃO FURE AS SANCAS E FORROS DE GESSO POIS ELES TAMBÉM ABRIGAM
TUBULAÇÕES HIDRÁULICAS.

■	NÃO FURAR NAS ÁREAS INDICADAS NA COR CINZA
■	CONCRETO
▲	VISTA

ESQUEMA HIDRÁULICO

RESIDENCIAL RESERVA CIDADE MAIA
TORRE ATLÂNTICA OPÇÃO 5 - FINAIS 1 E 3
ÁREA DE SERVIÇO

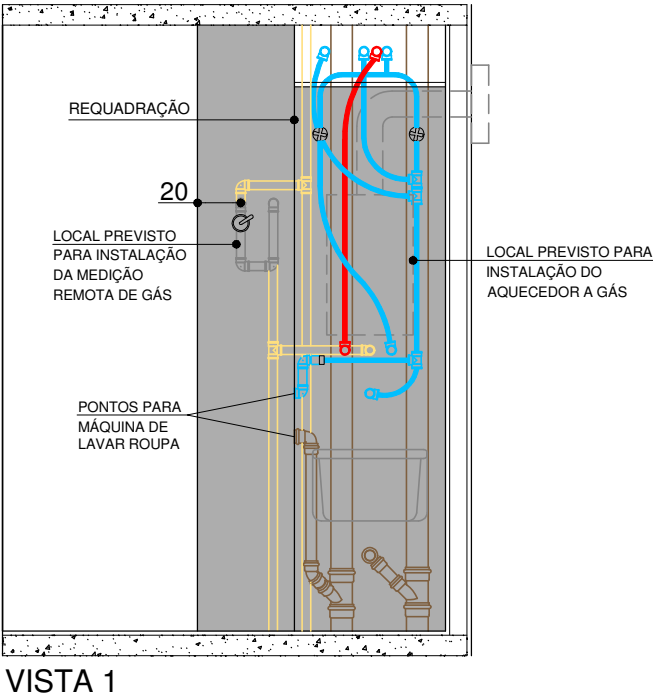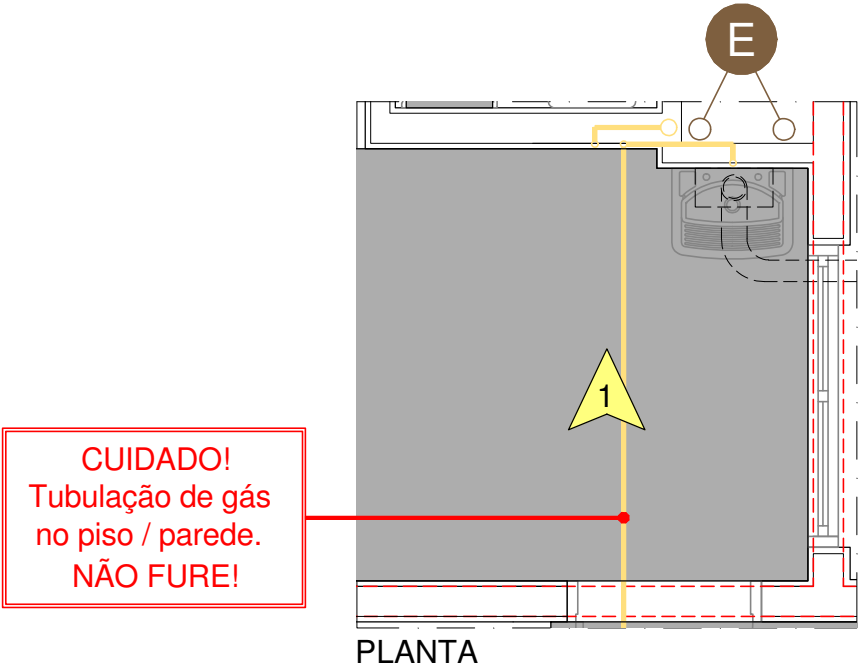

LEGENDA

PRUMADAS

V	VENTILAÇÃO
E	ESGOTO
AP	ÁGUA PLUVIAL
G	GÁS

TUBULAÇÕES

ÁGUA FRIA - PEX
ÁGUA QUENTE - PEX
ÁGUA FRIA
ESGOTO
GÁS
DRENO

OBSERVAÇÕES:

NAS MEDIDAS ACIMA, USE COMO REFERÊNCIA OS PONTOS APARENTES DE ÁGUA, GÁS, ESGOTO E REGISTROS.
AS MEDIDAS INDICADAS NAS VISTAS ESTÃO EM CENTÍMETROS.



ANTES DE FURAR:

USAR LIMITADOR DE BROCA E NÃO ULTRAPASSAR 2 CM DE PROFUNDIDADE.
LEMBRE-SE QUE OS ENCANAMENTOS QUE PASSAM NA PAREDE ACIMA
TAMBÉM ESTÃO PASSANDO POR ESTA MESMA PAREDE NO LADO OPOSTO.
CONSULTE A PLANTA DE PRUMADAS.
NÃO FURE AS SANCAS E FORROS DE GESSO POIS ELES TAMBÉM ABRIGAM
TUBULAÇÕES HIDRÁULICAS.

NÃO FURAR NAS ÁREAS INDICADAS NA COR CINZA
CONCRETO
VISTA

ESQUEMA HIDRÁULICO

RESIDENCIAL RESERVA CIDADE MAIA
TORRE ATLÂNTICA OPÇÃO 5 - FINAIS 1 E 3
TERRAÇO

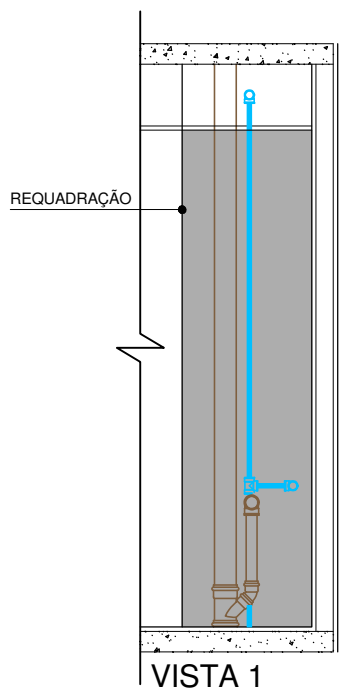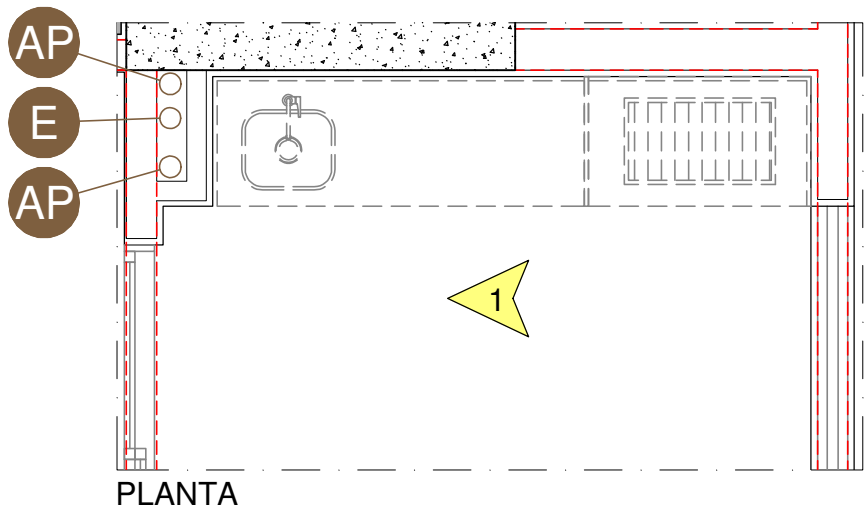

LEGENDA

PRUMADAS

V	VENTILAÇÃO
E	ESGOTO
AP	ÁGUA PLUVIAL
G	GÁS

TUBULAÇÕES

ÁGUA FRIA - PEX
ÁGUA QUENTE - PEX
ÁGUA FRIA
ESGOTO
GÁS
DRENO

OBSERVAÇÕES:

NAS MEDIDAS ACIMA, USE COMO REFERÊNCIA OS PONTOS APARENTES DE ÁGUA, GÁS, ESGOTO E REGISTROS.
AS MEDIDAS INDICADAS NAS VISTAS ESTÃO EM CENTÍMETROS.

ANTES DE FURAR:

USAR LIMITADOR DE BROCA E NÃO ULTRAPASSAR 2 CM DE PROFUNDIDADE.
LEMBRE-SE QUE OS ENCANAMENTOS QUE PASSAM NA PAREDE ACIMA
TAMBÉM ESTÃO PASSANDO POR ESTA MESMA PAREDE NO LADO OPOSTO.
CONSULTE A PLANTA DE PRUMADAS.
NÃO FURE AS SANCAS E FORROS DE GESSO POIS ELES TAMBÉM ABRIGAM
TUBULAÇÕES HIDRÁULICAS.

NÃO FURAR NAS ÁREAS INDICADAS NA COR CINZA
CONCRETO
VISTA