



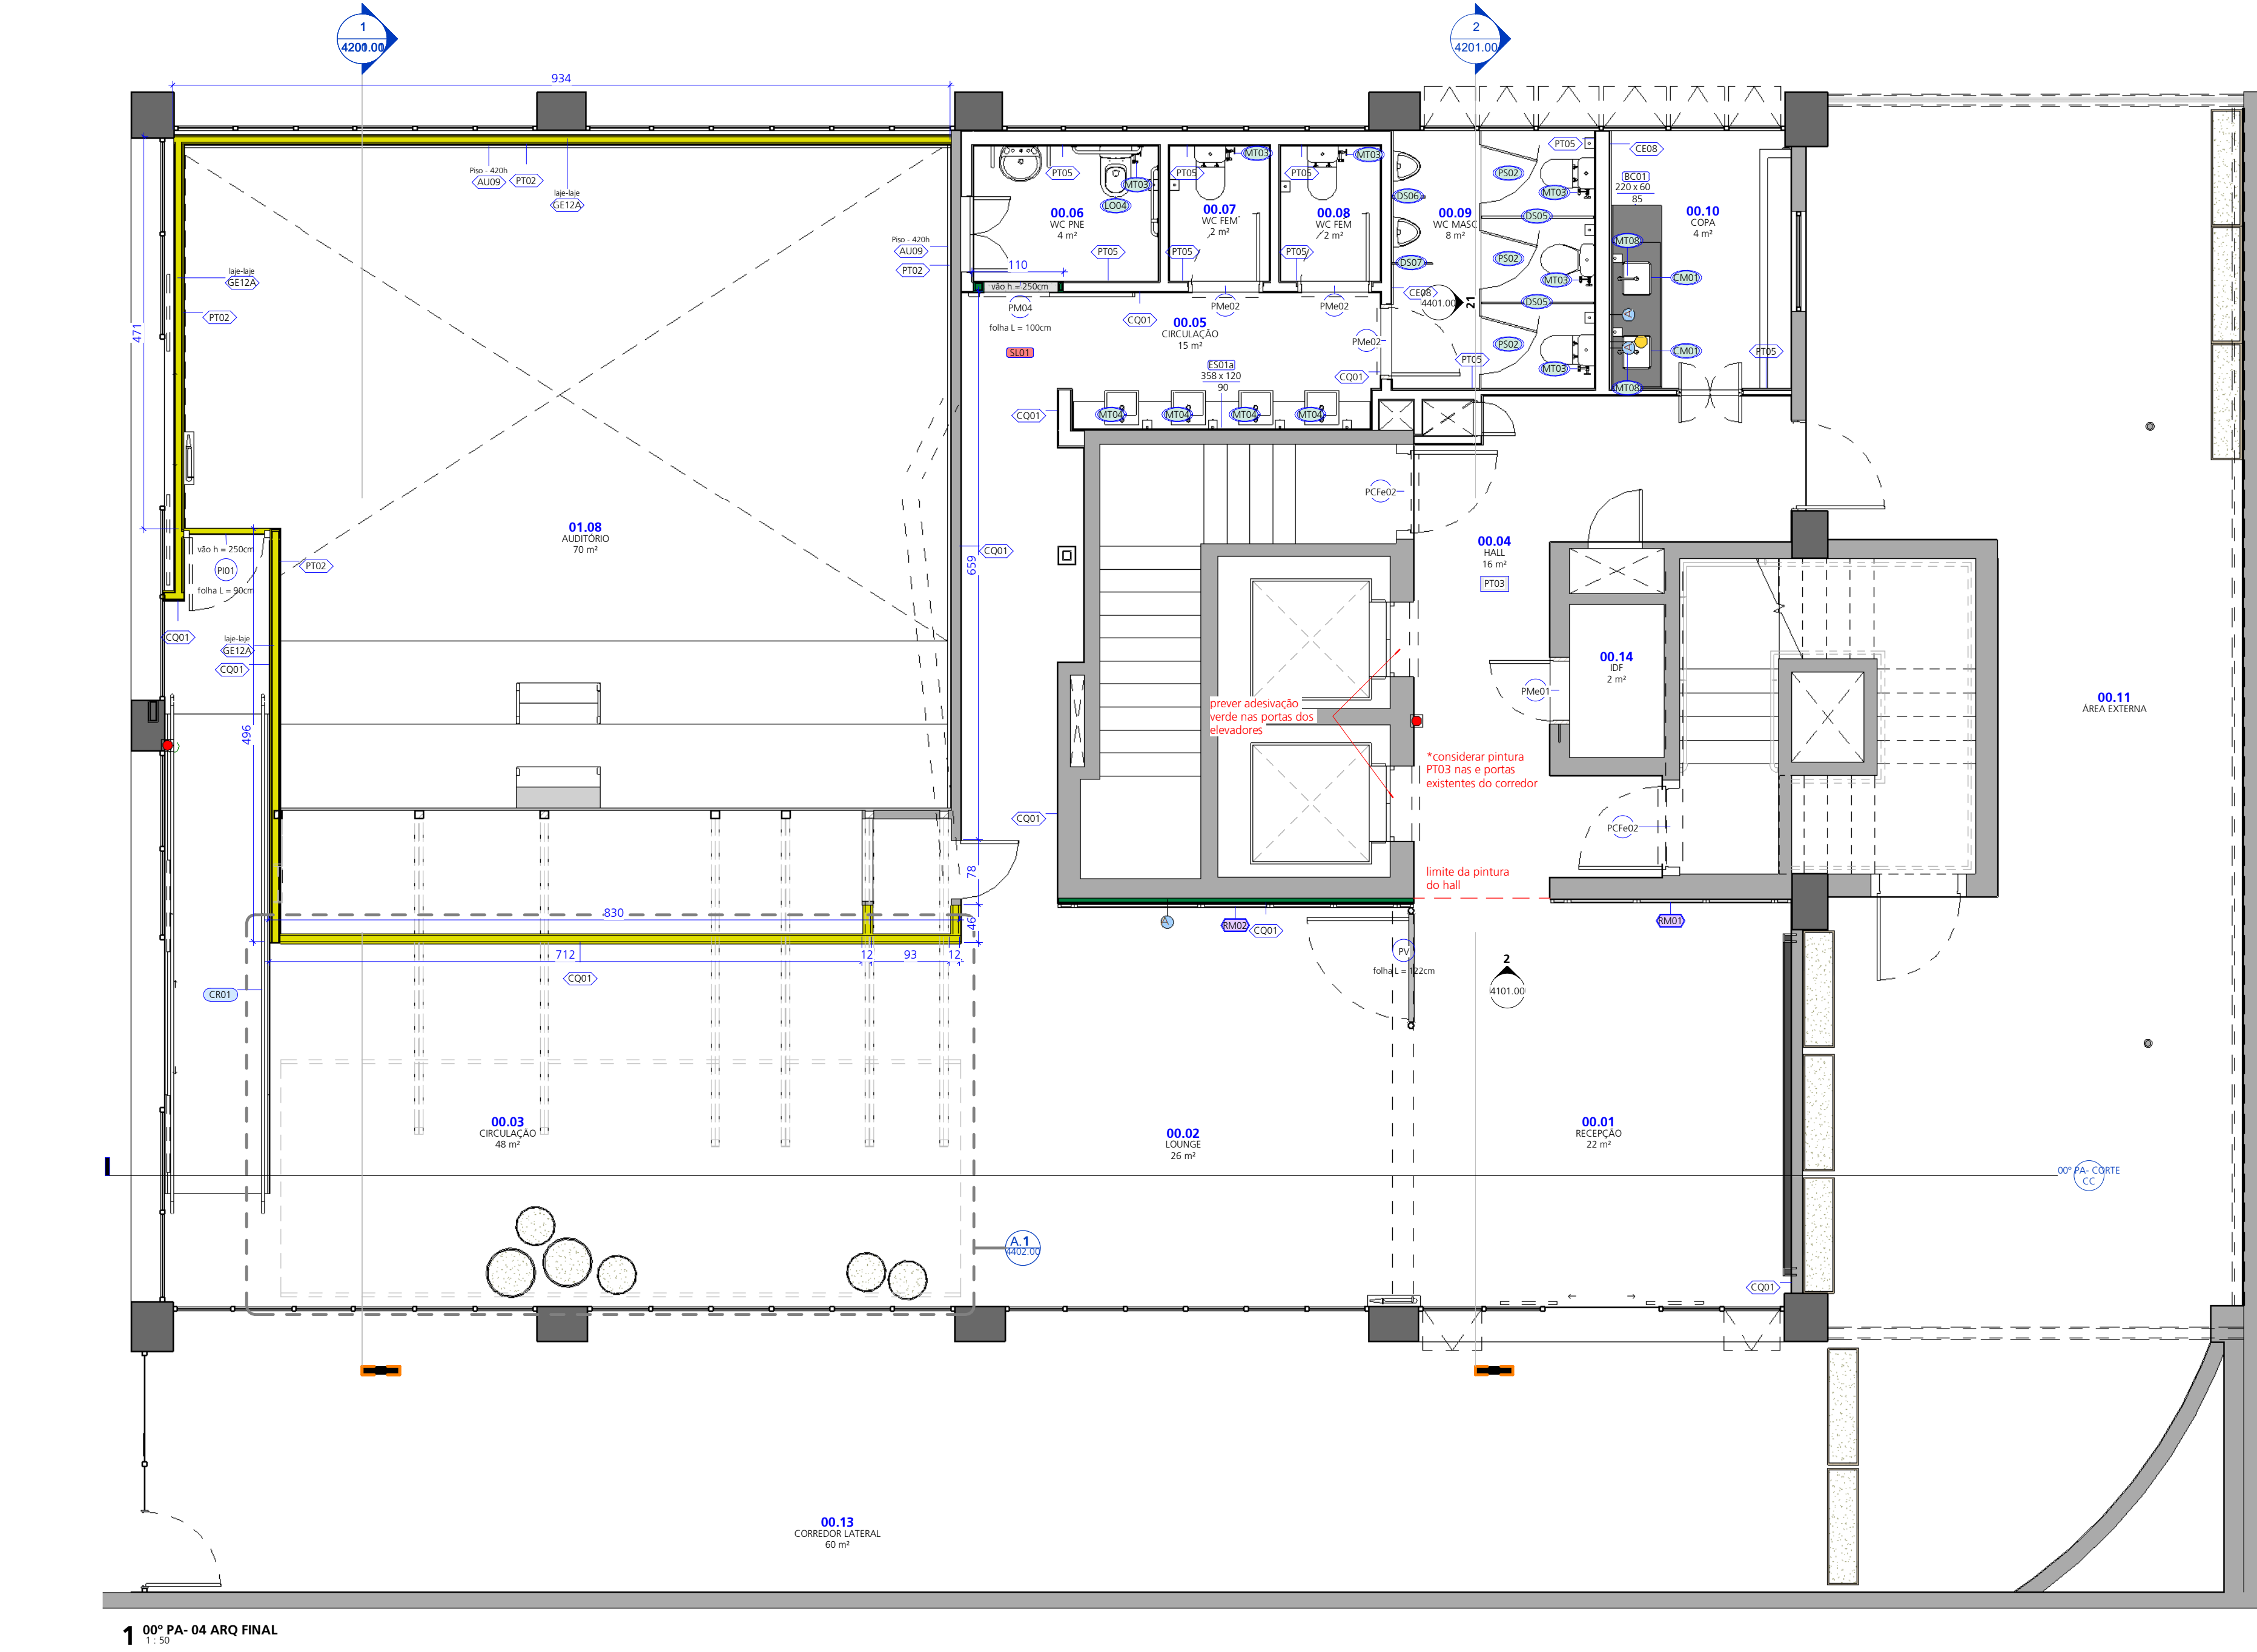


04 VEDAÇÕES	
NOTA PARA ALVENARIA: Todas as paredes de alvenaria executadas receberam acabamento com chapisco, emboco e reboco desempenado...	
NOTA PARA DRYWALL: As paredes em sistema drywall deverão ser executadas conforme as boas práticas de montagem e recomendações do...	
COD	DESCRIÇÃO
ALV2	Alvenaria de vedação interna executada em blocos de concreto de vedação, com espessura nominal de 10cm
DRYWALL	Aplicação de chapa de gesso acartonado 12.5mm, colada diretamente sobre superfície adequada, para regularização e acabamento interno
GE02A	Parede drywall 120/70400/2412.5 + 2412.5 com 18 128 kg/m³ - parede de gesso acartonado em chapa dupla com estrutura metálica composta por dois perfis de 70mm, espaçados a 120mm entre si. Revestimento em duas chapas de 12.5mm em cada face, com preenchimento interno em lâ mineral de densidade 128 kg/m³ para isolamento acústico
GE04A	Parede drywall 120/70400/2412.5 + 2412.5 com 18 128 kg/m³ - parede de gesso acartonado em chapa simples de 70mm, empacamento total de 120mm, com revestimento híbrido: chapa ru (resistente à unidade) + st (standard) em uma face e st + ru na outra. Com preenchimento interno em lâ mineral de densidade 128 kg/m³ para isolamento acústico
GE06B	Parede drywall 61/48/400/112.5 - parede de gesso acartonado em chapa simples, com estrutura de 48mm e uma chapa st de 12.5mm em cada face, sem isolamento
GE07B	Parede drywall 61/48/400/112.5 - parede de gesso acartonado em chapa simples, parede com estrutura de 48mm e chapas ru de 12.5mm, indicadas para áreas úmidas (banheiros, cozinhas, etc.), sem isolamento
GE12A	Parede drywall 120/70400/2412.5 + 2412.5 com 18 128 kg/m³ - parede de gesso acartonado em chapa dupla com estrutura metálica composta por dois perfis de 70mm, espaçados a 120mm entre si. Revestimento em duas chapas st de 12.5mm em cada face, com preenchimento interno em lâ mineral de densidade 128 kg/m³ para isolamento acústico - PARA PAREDES ACIMA DE 4M DE ALTURA
04 GUARDA CORPO E CORRIMÃO	
COD	DESCRIÇÃO
CORRIMÃO	Corrimão para rampa em tubo de aço inox, duplo, instalado em ambos os lados, com diâmetro de 38mm, acabamento anodizado natural cromado. Instalação conforme NBR9050, com altura de 90cm do piso, prolongamento de 30cm nas extremidades, distância mínima de 4cm da parede, superfície contínua e livre de arestas cortantes, garantindo empunhação segura e confortável. Fixado no piso
CR02	Corrimão para escada de auditorio, em tubo de aço inox, duplo, acabamento em pintura eletrolítica preta fosca, instalado em ambos os lados, com diâmetro de 38mm, com pintura em esmalte sintético na cor cinza ral 9007, com fundo zarcão. Instalação conforme NBR9050, com altura de 92cm do piso. Fixado no piso

04 ACABAMENTOS	
COD	DESCRIÇÃO
PTV01A	Pintura de parede na cor preta, acabamento fosco, coral. Indicado no mínimo 03 de mãos
PTV03	Pintura de parede na cor verde sintético, acabamento fosco, coral. Indicado no mínimo 03 de mãos
PTV05	Pintura de parede na cor cinza escura gelada, acabamento fosco, coral. Indicado no mínimo 03 de mãos
PTV07	Repintura do muro no pavimento térreo, seguir cor e acabamento conforme existente in loco
PTV01A ESPECIAL	
CO01	Pintura de parede em cimento queimado na cor cinza tubarão branco, acabamento fosco, coral. Indicado no mínimo 02 de mãos
REVESTIMENTO ACÚSTICO	
AU09	Revestimento de parede acústico, linha inovavall creative, cor cinza escuro cod.: 1019, lady. Nic. 0.70 a 0.85
REVESTIMENTO CERÂMICO	
CE08	Revestimento de parede prima de vidro, monocolor, interno, na cor branco brilhante, borda arredondada, 7x25cm, eliane. Prever rejunte na cor branca. Para os banheiros do P Pav prever pignação vertical alinhada. Para as áreas de copa, prever pignação horizontal em transpassé

04 DIVISÓRIAS SANITÁRIAS	
COD	DESCRIÇÃO
DIVISÓRIA SANITÁRIA	
D505	Divisória sanitária com porta integrada, composta por painéis em laminado melamínico, com estrutura e ferragens em aço inox, linha inox, acabamento na cor vibrant green, métrica. Afastado 15cm do piso, com altura final de 195cm, largura e profundidade conforme projeto de arquitetura, e=18mm
D506	Divisória sanitária para micrônio, composta por painel em laminado melamínico, com estrutura e ferragens em aço inox, linha inox, acabamento na cor vibrant green, métrica. H=120, p=40, e=18mm. Indico paralela
D507	Divisória sanitária cego, composta por painéis em laminado melamínico, com estrutura e ferragens em aço inox, linha inox, acabamento na cor vibrant green, métrica. Afastado 15cm do piso, com altura final de 195cm, p=50cm, e=18mm. Indico paralela
PORTA DIVISÓRIA SANITÁRIA	
PS02	Porta sanitária, em laminado melamínico, com estrutura e ferragens em aço inox, linha inox, acabamento na cor vibrant green, métrica. Afastado 15cm do piso, com altura final de 195cm, l=100cm, e=19mm. Prever fechadura na cor prata


04 REVESTIMENTO METÁLICO			
CÓD	DESCRIÇÃO		
RM01	Panel metálico pintado, cor branco Aspen, COD: SM 2030 RAL 7047, SuMetals. Fixado na parede, pignação conforme projeto		
RM02	Panel metálico pintado, cor branco Aspen, COD: SM 2030 RAL 7047, SuMetals. Fixado na parede, pignação conforme projeto		
04 LOUÇAS E METAIS			
PARA BACIAS EXISTENTES: as que não sofrerão intervenção, prever a troca do assento sanitário existente por assento em plástico			
PARA REGISTROS: Acabamento para registro de gaveta, cromado, aspen, cod.: 4900.c35.pq, deca			
PARA REGISTROS DO 6º PAVIMENTO: Acabamento para registro de gaveta, cromado, polo, cod.: 4900.c33.pq, deca			
Type Comments	CÓD	DESCRIÇÃO	Level
ACESSÓRIOS			
ACESSÓRIOS	AE01	Dispenser para papel higiênico	
ACESSÓRIOS	AE01	Dispenser para papel higiênico	00º PA
ACESSÓRIOS	AE03	Dispenser de sabonete líquido	00º PA
CUBA METÁLICA			
CUBA METÁLICA	CM01	Cuba de embutir retangular, em aço inox, polida, com válvula, 40x34cm, p=17cm, lamina, cod.: 406i, tranmontina	00º PA
LOUÇAS			
LOUÇAS	LO04	Bacia para caixa acoplada, na cor branca, vogue plus confort, cod.: p 515 17, deca + 4 assento em plástico (com microban para bacia vogue plus na cor branca, cod.: ap 50 17, deca + 4 caixa acoplada com acionamento duplo para bacia vogue plus confort, na cor branca, cerâmica, cod.: cdc 011 17, deca	00º PA
LOUÇAS	LO06	Troca do assento sanitário existente por assento em plástico com microban para bacias vogue plus na cor branca, cod.: ap 50 17, deca	
METAIS			
METAIS	MT03	Ducha higiênica universal despressurizada, cromada, de parede, cod.: 1948.c.act.cr, deca	00º PA
METAIS	MT04	Torneira de mesa com fechamento automático para lavatório, cromada, decamatic aço, cod.: 1173.c	00º PA
METAIS	MT08	Torneira de mesa de 90º com bica móvel para cozinha, cromada, link, cod.: 1166.c.link, deca	
METAIS	MT08	Torneira de mesa de 90º com bica móvel para cozinha, cromada, link, cod.: 1166.c.link, deca	00º PA
SIFÃO			
SIFÃO	SF01	Sifão articulado para lavatório, cromado, cod.: 1682.c.100.112, deca	
SIFÃO	SF01	Sifão articulado para lavatório, cromado, cod.: 1682.c.100.112, deca	00º PA

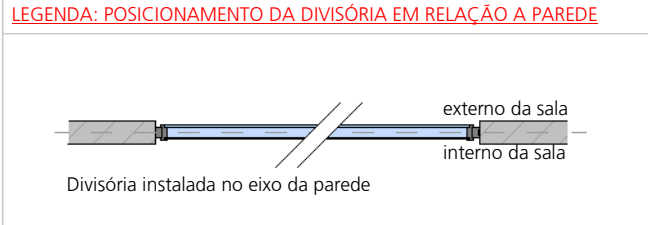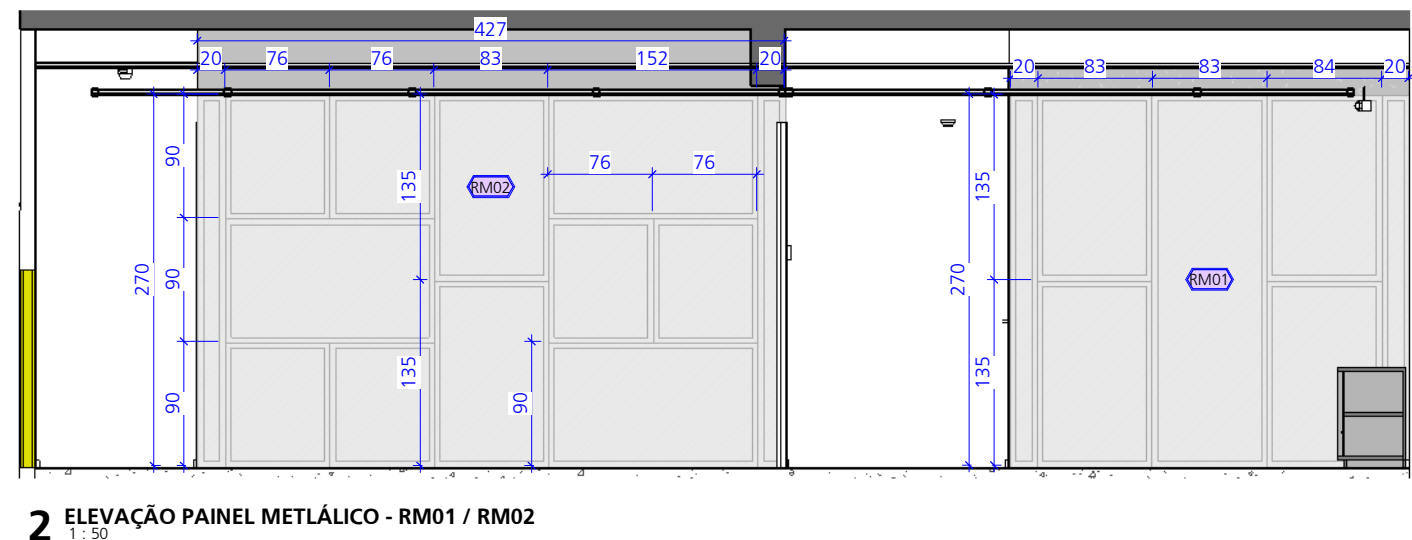

HIDRAULICA	
COD	DESCRIÇÃO
TO1	TOILET
TO2	TUBO DO PONTO DE LAVAGEM
TO3	TUBO DO PONTO DE ÁGUA FRIA
TO4	TUBO DO PONTO DE ESGOTO
TO5	VALVULA DE REGISTO
TO6	TUBO DO PONTO DE GÁS
TO7	DUCHA HIGIÊNICA


LEGENDA - VEDAÇÕES	
REPRESENTAÇÃO	TIPO DE VEDAÇÕES (VER DESCRITIVO) NAS TABELAS DE VEDAÇÕES)
FECHAMENTOS EXISTENTES	
ALVENARIAS	

LEGENDA - TIPO CHAPA DRYWALL	
REPRESENTAÇÃO	CHAPAS DOS DRYWALLS
DRYWALL CHAPA STANDARD	
DRYWALL CHAPA RU (RESISTENTE A UMIDADE)	
DRYWALL CHAPA MISTA (ST/RU)	
DRYWALL CHAPA RF (RESISTENTE A FOGO)	
DRYWALL CHAPA PERFORMA (ACÚSTICA)	

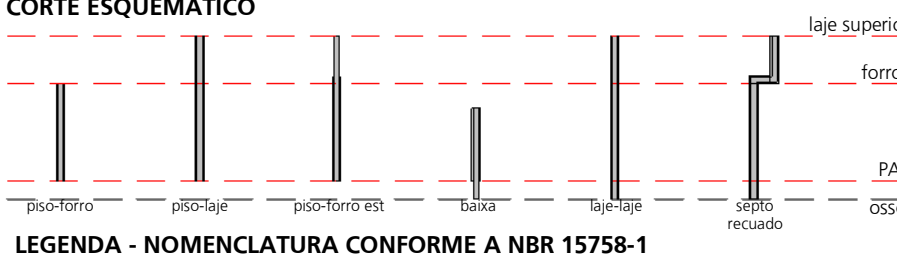

LEGENDA - NOMENCLATURA CONFORME A NBR 15758-1	
REPRESENTAÇÃO	TIPO DE VEDAÇÕES (VER DESCRITIVO) NAS TABELAS DE VEDAÇÕES)
FECHAMENTOS EXISTENTES	
ALVENARIAS	

0.0 NOTAS DE ORÇAMENTO PARA BID	
Para fins de orçamento, prever os itens abaixo do Auditório do pavimento térreo, como opcionais:	
1. Retirada de guarda-corpo existente, bem como execução de fechamento lateral da arquibancada em drywall, piso-teto, visando o fechamento completo do ambiente. Bem como, execução de fechamento do forro acima da rampa em gesso liso;	
2. Prever a instalação de porta industrial no acesso ao auditório;	
3. Prever o remanejamento de rede de hidrantes junto ao acesso do auditório, haja vista a necessidade de instalação da porta bem como, a exigência da NBR9050 para criação de um vão livre mínimo de 120cm, na passagem da rampa;	
4. Instalação de revestimento acústico lacy na parede do fundo da arquibancada, no primeiro pavimento. Prever como obrigatório apenas nas duas paredes, sendo esta terceira como opcional;	
5. Prever a instalação de placas acústicas sonex nas cubetas da laje;	

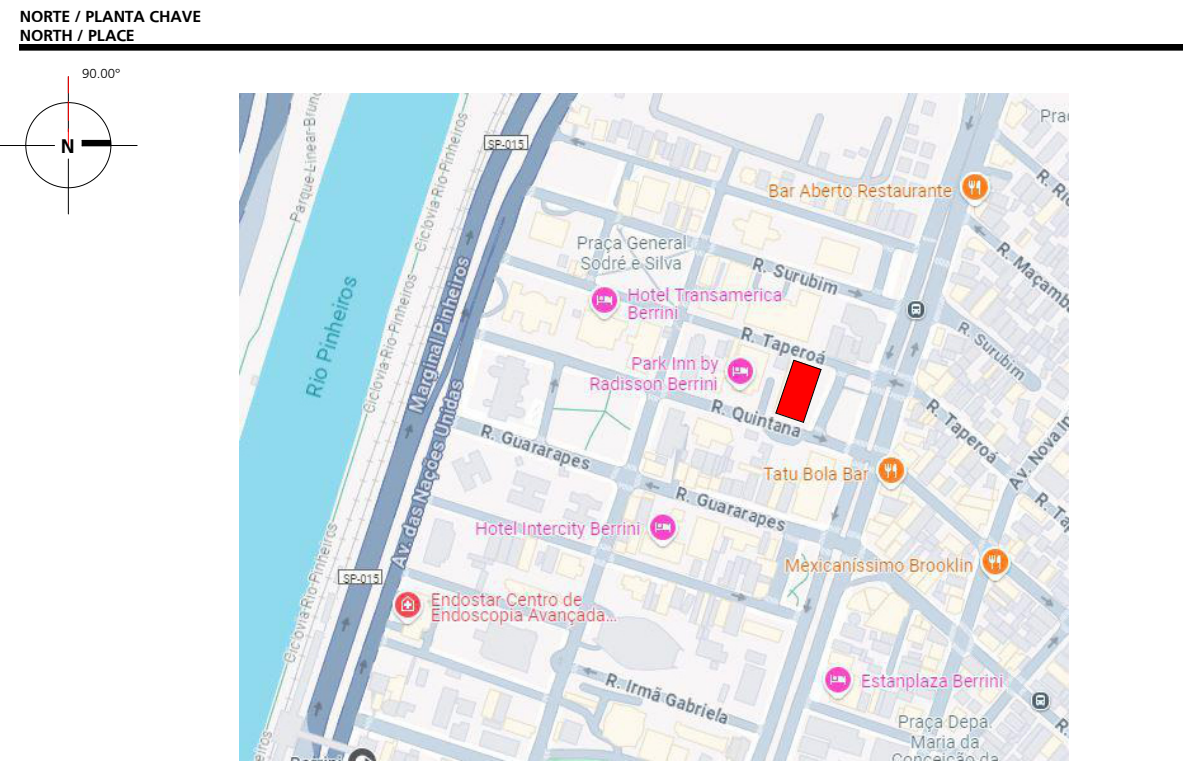

NOTAS GERAIS	
NOTAS	
- MEDIDAS EM CENTÍMETROS	
- EM FASE DE LUTADAO, AS MEDIDAS EXTRAIADAS PELO SOFTWARE SÃO MERAMENTE ORIENTATIVAS, CABENDO AO FORNECEDOR CONFERIR E ESTABELECER SEU CRITÉRIO DE PESSOAS	
- EM FASE DE EXECUÇÃO, CONFERIR TODAS AS MEDIDAS NO LOCAL	
- DOCUMENTO IMPRESSO APENAS PARA CONSULTA. VERIFIQUE SEMPRE A ÚLTIMA VERSÃO ELETRÔNICA.	
ESTE PROJETO CONSTA COM PROJETOS TÉCNICOS ESPECÍFICOS DAS SEGUINTES DISCIPLINAS:	
- AR C ONDICIONAD	
- BOMBEIROS	
- CABEAMENTO	
- DETECÇÃO E ALARME	
- ELETÉRICA	
- HIGIENIZANTARIO	
- LUMINOTÉCNICO	
- MULTIMÍDIA	
VERIFICAR DETALHES E ESPECIFICAÇÕES TÉCNICAS NOS PROJETOS DAS DISCIPLINAS ESPECÍFICAS.	
PORTAS E DIVISÓRIAS	
1. TODAS AS LINHAS DE DIVISÓRIAS, TANTO REMANEJAMENTOS COMO NOVAS, DEVEM CONTER BANDA ACÚSTICA NOS ENCONTROS DE PAREDES, PISO E FORRO (PAINÉIS E BATENTES);	
2. TODAS AS PORTAS DE BANHEIROS COLETIVOS E DMS DEVEM TER MOLAS COM BRAÇO DE PARADA	
3. TODAS AS PORTAS DE SALAS COM DIVISÓRIA DE VIDRO DUPLA DEVE TER VEDA PORTA TIPO GUILHOTINA	
4. PORTAS COM PUXADOR NÃO DEVEM TER TRINCO ROLETE E DEVEM OBRIGATORIAMENTE TER MOLAS COM BRAÇO DE PARADA	
5. NÃO INSTALAR DIVISÓRIA JUNTA SECA EM ÁREAS COM VÃO DE RE-DIREITO DUPLA - NECESSIDADE DE ENCAIXILHAR PELO RISCO A SEGURANÇA. SEGUIR ESPECIFICAÇÃO DO PROJETO	
9.0 ACÚSTICA	
1. UTILIZAR BANDEIA ACÚSTICA 3mm (TIPO JUNEAU) NOS PERÍMETROS DAS DIVISÓRIAS INDUSTRIAIS, PRINCIPALMENTE NOS ENCONTROS COM PLASES, ALVENARIAS E FACHONÇAS ACÍDUOS;	
2. QUANDO HOUVER SALAS CONSTRUÍDAS LINTO AO CORE (ENCONTRO DE DRYWALL COM PAREDE CORE DO EDIFÍCIO), EXECUTAR CONTRAPAREDE COM LÂ DE VIDRO OU ROCHA (DENSIDADE = 32kg/m³) PARA EVITAR QUE O SOM TRANSPASSE DE UM LADO PARA O OUTRO;	

0	Emissão Projeto Executivo	16/07/2025	Debora C.
Nº	REVISÃO	DATA	DESENHADO POR
REVISION	REVISION	DATE	DRAWING BY

PROJETA TÉCNICO		STATUS	
TECHNICAL CONSULTANT		STATUS	
896.25		em desenvolvimento	

PROJ. Nº		STATUS	
DRAWING Nº		STATUS	
896.25		em desenvolvimento	

LOCALIDADE		ANDAR	
BUILDING		FLOOR	
LVM		1	
LVM0000 - RUA DR. CARDOZO DE MELO, 1168			

ARQUIVO		896.25-AIT-EX-LVMD-4101.00-PJT-R0	
FILE		DRAWING Nº	
SUBJECT		4101.00	
ESCALA		DISCIPLINA	
SCALE		AIT	
As indicated		REVISÃO	
ETAPA		REVISION	
PHASE		DATE	
Projeto Executivo		16/07/2025	
ARB. CONC. DESIGN ARCH.		REBECA TRINDADE	
GERENTE		ADRIANA DALMASO	
APPROVAL BY AN APPROVAL		APPROVAL BY CLIENT	
		DATE	
		DEBORA CASULLO	

ARQUITETURA FECHAMENTOS E ACABAMENTOS		4101.00	
SUBJECT		DRAWING Nº	
		4101.00	
ESCALA		DISCIPLINA	
SCALE		AIT	
As indicated		REVISÃO	
ETAPA		REVISION	
PHASE		DATE	
Projeto Executivo		16/07/2025	
ARB. CONC. DESIGN ARCH.		REBECA TRINDADE	
GERENTE		ADRIANA DALMASO	
APPROVAL BY AN APPROVAL		APPROVAL BY CLIENT	
		DATE	
		DEBORA CASULLO	

PROJETO DE ARQUITETURA		896.25-AIT-EX-LVMD-4101.00-PJT-R0	
ARCHITECTURAL SUBJECT		DRAWING Nº	
		4101.00	
OS DESENHOS E MATERIAIS QUE CONSTAM DESTA PLANTA CONSTITUEM TRABALHOS ORIGINAIS DO ARQUITETO		16/07/2025	
ESTES TRABALHOS SÃO PROPRIEDADE DO ARQUITETO E SÃO O RESULTADO DE SEU TRABALHO E NÃO SÃO PARA SEREM REPRODUZIDOS SEM O CONSENTIMENTO DO ARQUITETO		16/07/2025	
ALL DRAWING AND WRITTEN MATERIAL APPEARING HEREIN CONSTITUTE ORIGINAL AND UNPUBLISHED WORK OF THE ARCHITECT		16/07/2025	
WORKS MAY NOT BE REPRODUCED, COPIED OR OTHERWISE USED OR EXPOSED WITHOUT WRITTEN PERMISSION OF THE ARCHITECT		16/07/2025	
Este projeto foi gerado a partir do software Autodesk Revit Architecture e utilizado templates Revit RMT			