



1 PLANTA BAIXA DE LAYOUT

SALÃO DE FESTAS CCI

ENDEREÇO:
Alameda dos Jurupis, 900 - Moema

CCI

MALVA ARQUITETURA

STATUS:
EXECUTIVO
CONTEÚDO:
PLANTA BAIXA - LAYOUT


DATA:
13/01/2025
ESCALA:
1 : 75

01C1

MALVAARQUITETURA@GMAIL.COM
@MALVA_ARQUITETURA



MALVA
arquitetura

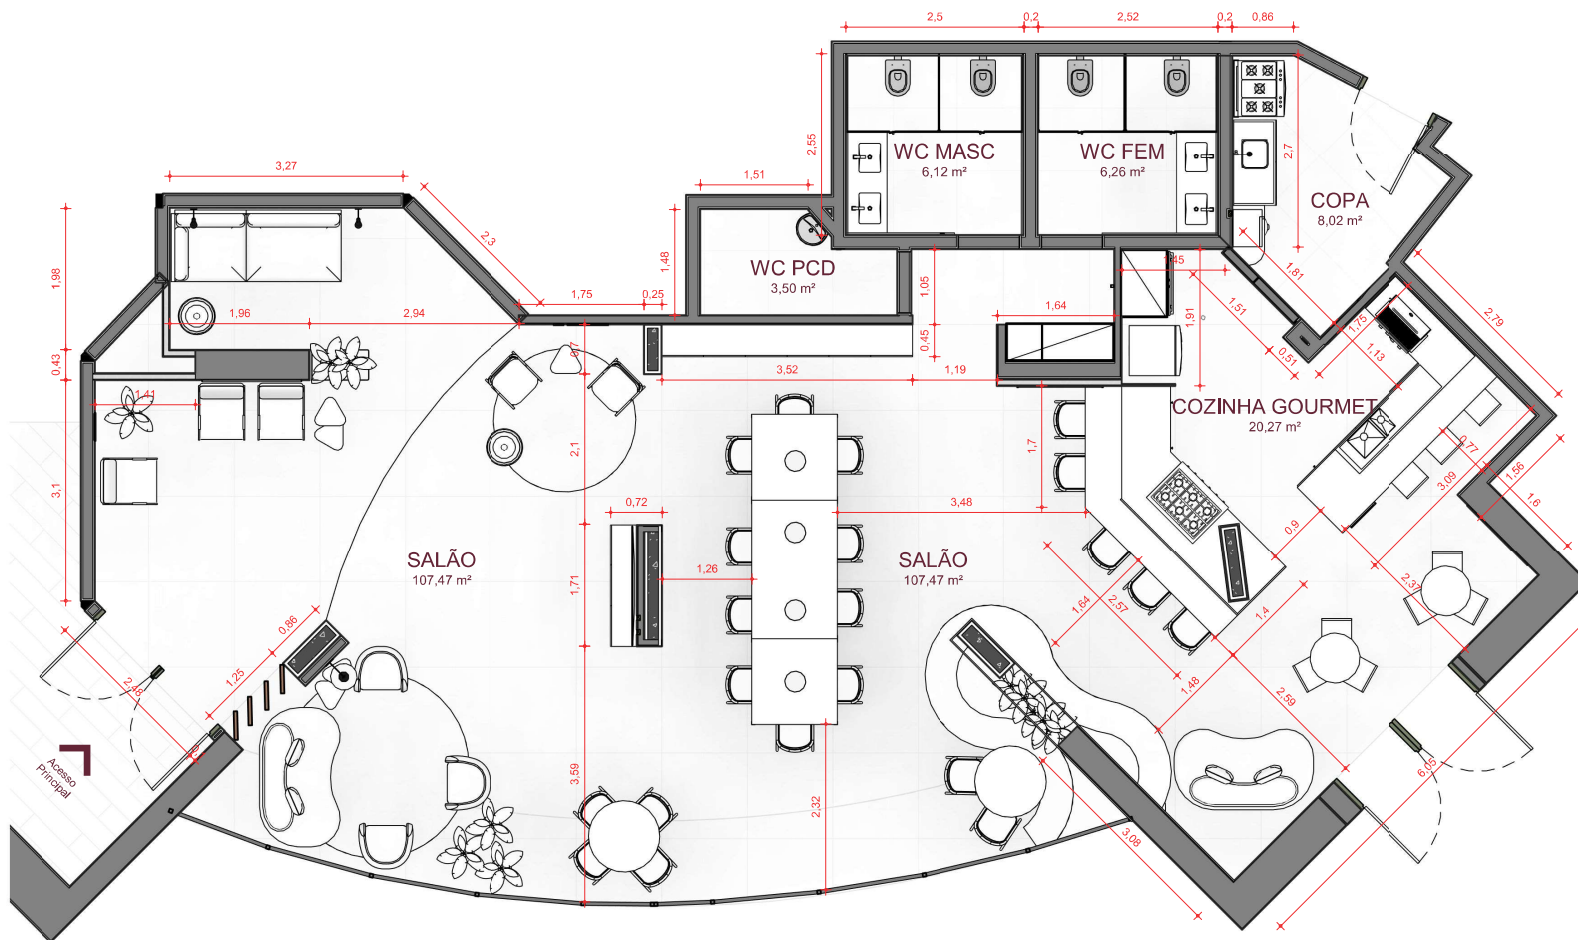

1

PLANTA BAIXA DE LAYOUT TÉCNICO

Escala: 1 : 75

SALÃO DE FESTAS CCI

ENDEREÇO:
Alameda dos Jurupis, 900 - Moema

CCI

MALVA ARQUITETURA

STATUS:
EXECUTIVO
CONTEÚDO:
PLANTA BAIXA DE LAYOUT TÉCNICA

DATA:
13/01/2025
ESCALA:
1 : 75

01C2

MALVA ARQUITETURA
@MALVA_ARQUITETURA



MALVA
arquitetura