


PODE OCORRER VARIAÇÃO DE 2W A 5W EM SUAS POTÊNCIAS DE ACORDO COM FABRICANTE DA LUMINÁRIA.
TABELA APENAS PARA 20W
OS PERFILES DE 20W SÃO COMPOSTOS POR DUAS FITAS DE LED CADA (EXCETO PERFIL SLIM). AS FITAS QUE SÃO UTILIZADAS NESSES PERFILES NÃO DEVEM SER CONSIDERADAS AO CÁLCULO DA POTÊNCIA DE FITA DE LED DA MARCENARIA A MARCENARIA DEVERÃO SER DEIXADOS NO FORRO PARA PUXAR NO MOMENTO DA INSTALAÇÃO DOS MÓVEIS OU COM ALTURA INDICADA.

SÍMBOLO	LUMINÁRIA	LÂMPADA	WATT	QNTD.
	PERFIL SLIM COM FITA DE LED COB TEMPERATURA DE COR 4000K – EMBUTIR	LED	20W	7,89m
	PERFIL SLIM COM FITA DE LED COB TEMPERATURA DE COR 3000K – EMBUTIR	LED	20W	4,82m
	PERFIL SLIM COM FITA DE LED COB TEMPERATURA DE COR 3000K – EMBUTIR	LED	20W	17,86m
	PLAFON DE LED INTEGRADO TEMPERATURA DE COR 3000K – EMBUTIR 40x40cm	LED	32W	04
	PLAFON DE LED INTEGRADO TEMPERATURA DE COR 3000K – EMBUTIR 26x26cm	LED	20W	09
	SPOT DE LED DIRECIONÁVEL – EMBUTIR (ÂNGULO 60°) 3000K Lâmpada dicrótica	LED	07W	32
	SPOT DE LED DIRECIONÁVEL – EMBUTIR (ÂNGULO 36°) 3000K Lâmpada AR-70	LED	07W	03
	PENDENTE LÂMPADA DE LED 3000K	LED	25W	02
	ARANDELA COM LÂMPADA DE LED COR 3000K	LED	10W	
	PONTO DE ESPERA NA PAREDE PARA LED EM ESPELHO COR 3000K	LED	07W	01
	FITA DE LED COB PARA FIXAR EM MARCENARIA 3000K	LED	12W	34,87m
	FITA DE LED COB PARA NICHOS (BANHEIRO) TEMPERATURA DE COR 3000K	LED	12W	
	FITA DE LED COB PARA SANCA INVERTIDA/ CORTINEIRO TEMPERATURA DE COR 3000K	LED	12W	5,76m
	CAIXAS DE SOM AMBIENTE			

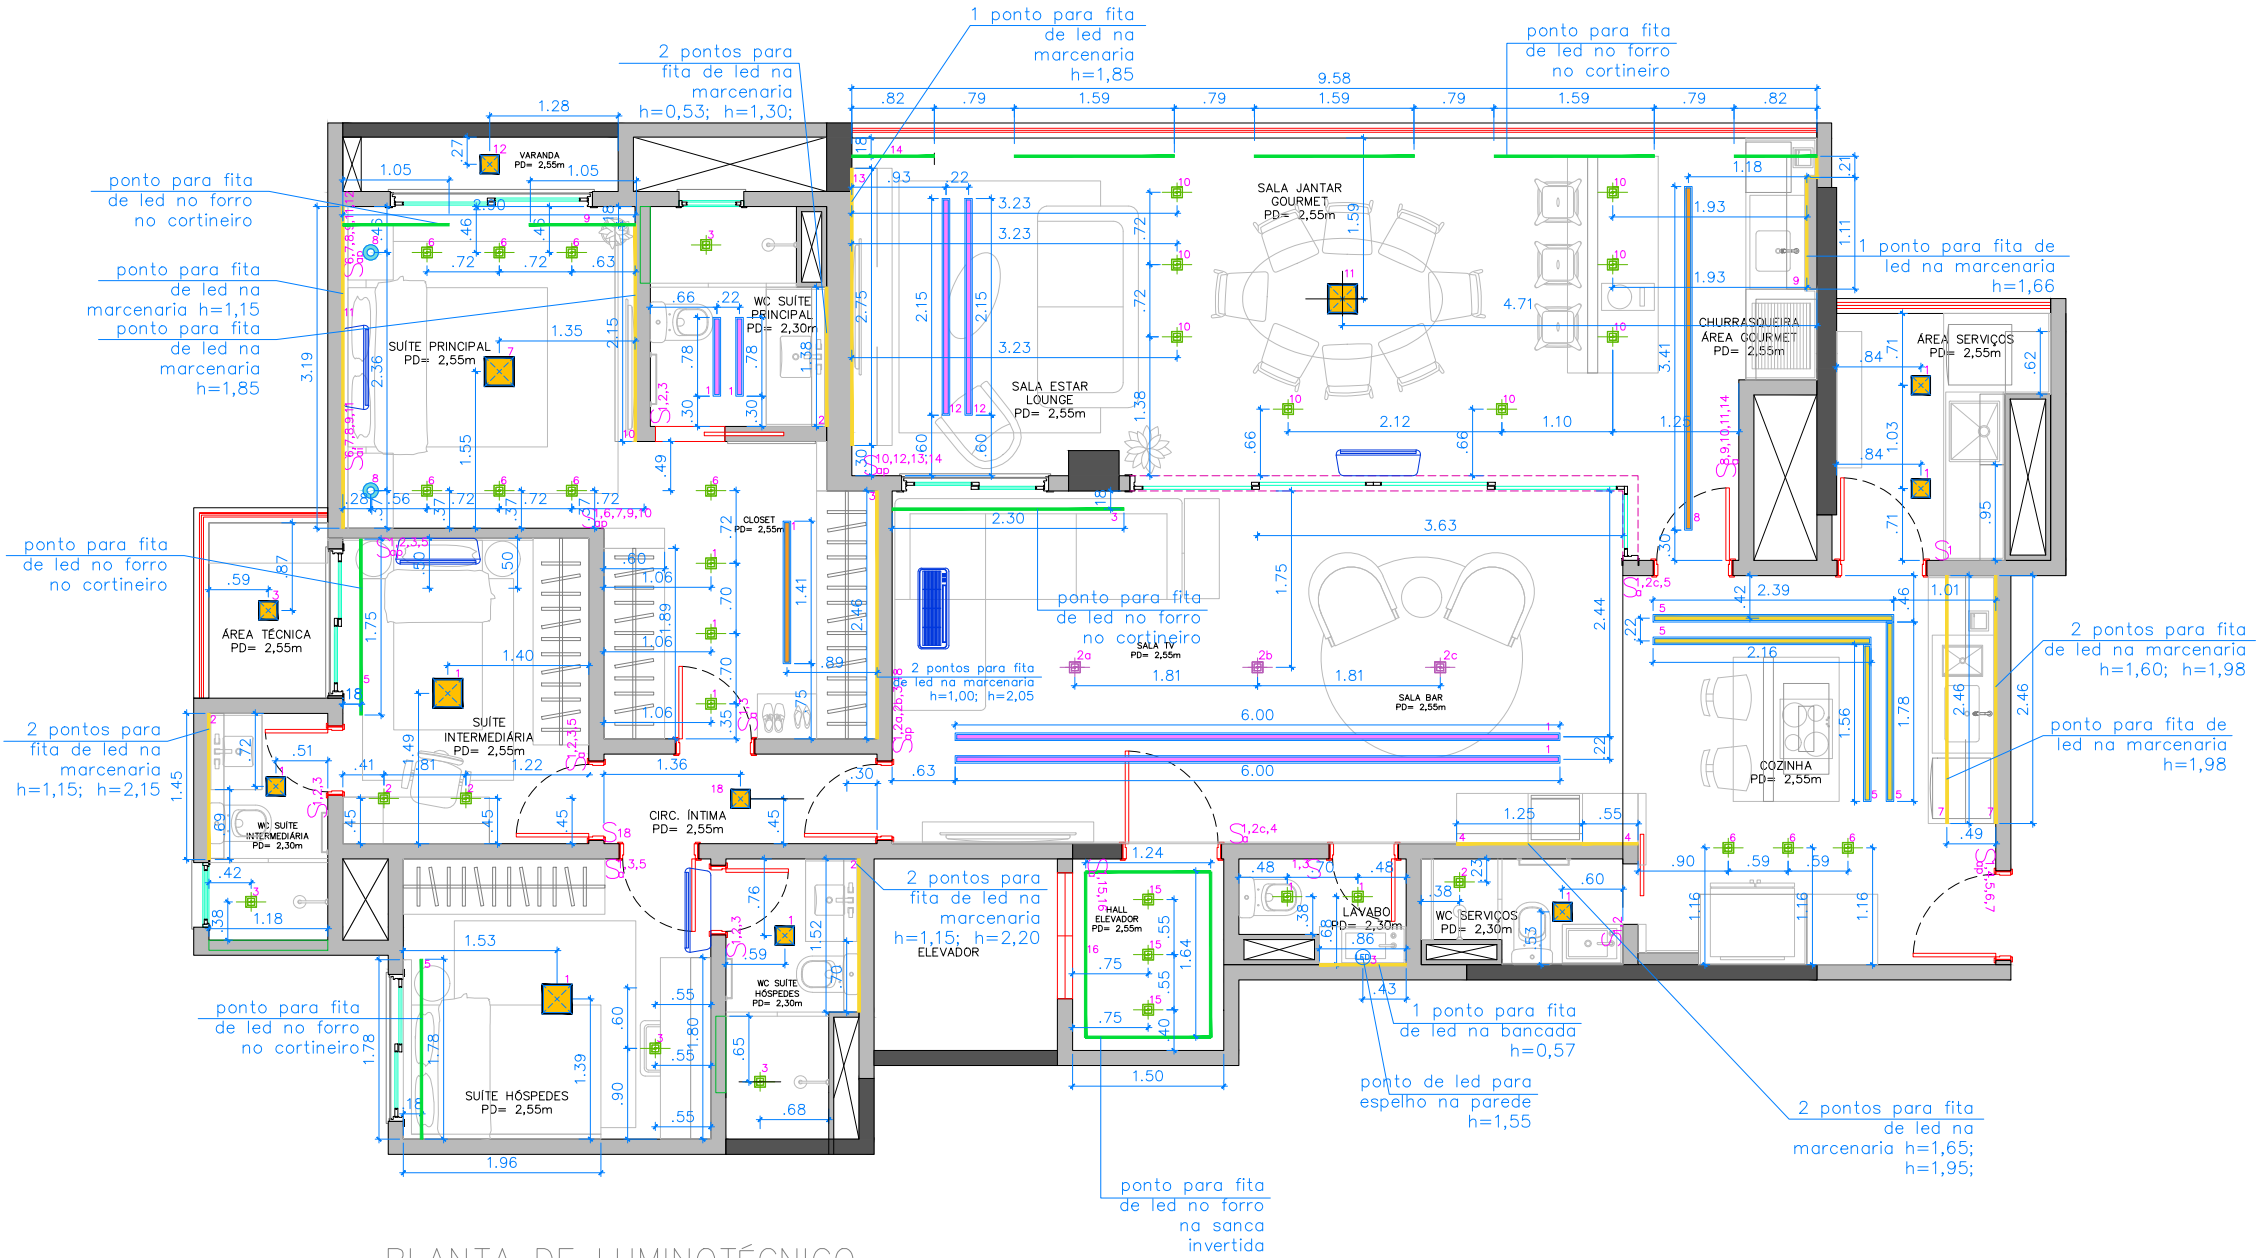

PLANTA DE LUMINOTÉCNICO

* CONFERIR MEDIDAS NA OBRA

PROJETO ARQUITETURA DE INTERIORES: REFORMA INTERIORES		PROPRIETÁRIOS: PEDRO DESENZI		PE	PÁG.
ENDEREÇO: RUA BARTIRA, 856 – APTO 184 – TORRE ÚNICA – PERDIZES/SP		PRANCHA: PLANTA DE LUMINOTÉCNICO		R01	
EMIÇÃO INICIAL:	ESCALA:	DESENHISTA:	DATA:		
14/10/2024	1: 75		19/09/2025		