



CADERNO DE PLANTAS GERAIS PROJETO ALEX E KARINE

CADERNO DE PLANTAS GERAIS

FOLHA 1 - PLANTA DE LAYOUT
FOLHA 2 - PLANTA DE LAYOUT COM COTAS
FOLHA 3 - PLANTA DE DEMOLIR
FOLHA 4 - PLANTA DE CONSTRUIR
FOLHA 5 - PLANTA DE PONTOS HIDRÁULICOS
FOLHA 6 - PLANTA DE PONTOS ELÉTRICOS
FOLHA 7 A 18 - VISTAS DE PONTOS ELÉTRICOS
FOLHA 19 - PLANTA DE REVESTIMENTOS
FOLHA 20 - VISTAS DE REVESTIMENTOS
FOLHA 21 - PLANTA DE FORRO
FOLHA 22 - PLANTA DE FORRO COM ILUMINAÇÃO
FOLHA 23 - PLANTA DE ILUMINAÇÃO
FOLHA 24 - PLANTA DE CIRCUITOS
FOLHA 25 - AR CONDICIONADO




PLANTA DE LAYOUT
ESCALA 1:75

LEGENDA LAYOUT SOCIAL

SÍMBOLO	DESCRIÇÃO
1	ARMÁRIO EM MARCENARIA COM PORTAS DE VIDRO
2	ESTANTE EM MARCENARIA COM PAINEL E PORTA MIMETIZADA
3	BANCO EM MARCENARIA
4	ARANDELA
5	SOFÁ EM L COM CHAISE COM TECIDO CINZA2,60X2,70M
6	RACK EM MARCENARIA COM PAINEL PARA TV
7	MESA DE CENTRO EM ACRÍLICO OU VIDRO
8	TAPETE 2.80X3.30M
9	ARANDELA
10	CRISTALEIRA EM MARCENARIA COM PORTAS DE VIDRO
11	APARADOR + SERRALHERIA PARA GARRAFAS DE VINHOS
12	MESA DE JANTAR DE MADEIRA COM APLICAÇÃO DE RESINA - EXISTENTE
13	JOGO DE 6 CADEIRAS COM TECIDO CINZA
14	LUMINÁRIA PENDENTE
15	ARMÁRIO EM MARCENARIA
16	BANCADA DE PEDRA
17	TORNEIRA DE BANCADA + CUBA
18	BANCADA EM PEDRA
19	LUMINÁRIA PENDENTE
20	PRATELEIRA SUSPensa COM METALON
21	BANQUETA COM TECIDO CINZA
22	CUBA RETANGULAR
23	TORNEIRA DE BANCADA
24	DOSADOR DE DETERGENTE
25	LAVA LOUÇAS DE EMBUTIR
26	BANCADA DE PEDRA
27	FORNO ELÉTRICO
28	COOKTOP A GÁS
29	COIFA DE PAREDE
30	GELADEIRA
31	ARMÁRIO ALTO EM MARCENARIA
32	BANCADA DE PEDRA COM CUBA ESCULPIDA + TORNEIRA
33	LUMINÁRIA PENDENTE
34	BACIA SANITÁRIA
35	ARMÁRIO EM MARCENARIA
36	ARMÁRIO EM MARCENARIA
37	ARMÁRIO ALTO EM MARCENARIA
38	TORRE DE LAVA E SECA
39	BANCADA DE PEDRA + TANQUE ESCULPIDO E TORNEIRA
40	ARMÁRIO EM MARCENARIA

LEGENDA LAYOUT INTIMO

SÍMBOLO	DESCRIÇÃO
41	ARANDELA
42	ARMÁRIO SAPATEIRA EM MARCENARIA
43	GUARDA ROUPA EM MARCENARIA
44	GUARDA ROUPA EM MARCENARIA
45	GUARDA ROUPA EM MARCENARIA
46	PENTEADEIRA EM MARCENARIA + ESPELHO FRONTAL COM LED + PUFF
47	CAMA BOX KING
48	CABECEIRA ESTOFADA
49	MESA DE CABECEIRA
50	CUBA OVAL BRANCA
51	ESPELHEIRA EM MARCENARIA
52	BANCADA EM PEDRA
53	TORNEIRA DE BANCADA
54	TORNEIRA DE BANCADA
55	ESPELHEIRA EM MARCENARIA
56	DUCHA HIGIÊNICA
57	CHUVEIRO
58	ACABAMENTO DE REGISTRO
59	RACK + PRATELEIRA EM MARCENARIA
60	CAMA "VIÚVA" EM MARCENARIA
61	MESA LATERAL
62	GUARDA ROUPA EM MARCENARIA
63	CAMA CASAL EM MARCENARIA
64	GUARDA ROUPA EM MARCENARIA
65	MESA DE CABECEIRA
66	ARANDELA
67	TORNEIRA DE BANCADA
68	ESPELHEIRA
69	DUCHA HIGIÊNICA
70	CHUVEIRO
71	ACABAMENTO DE REGISTRO

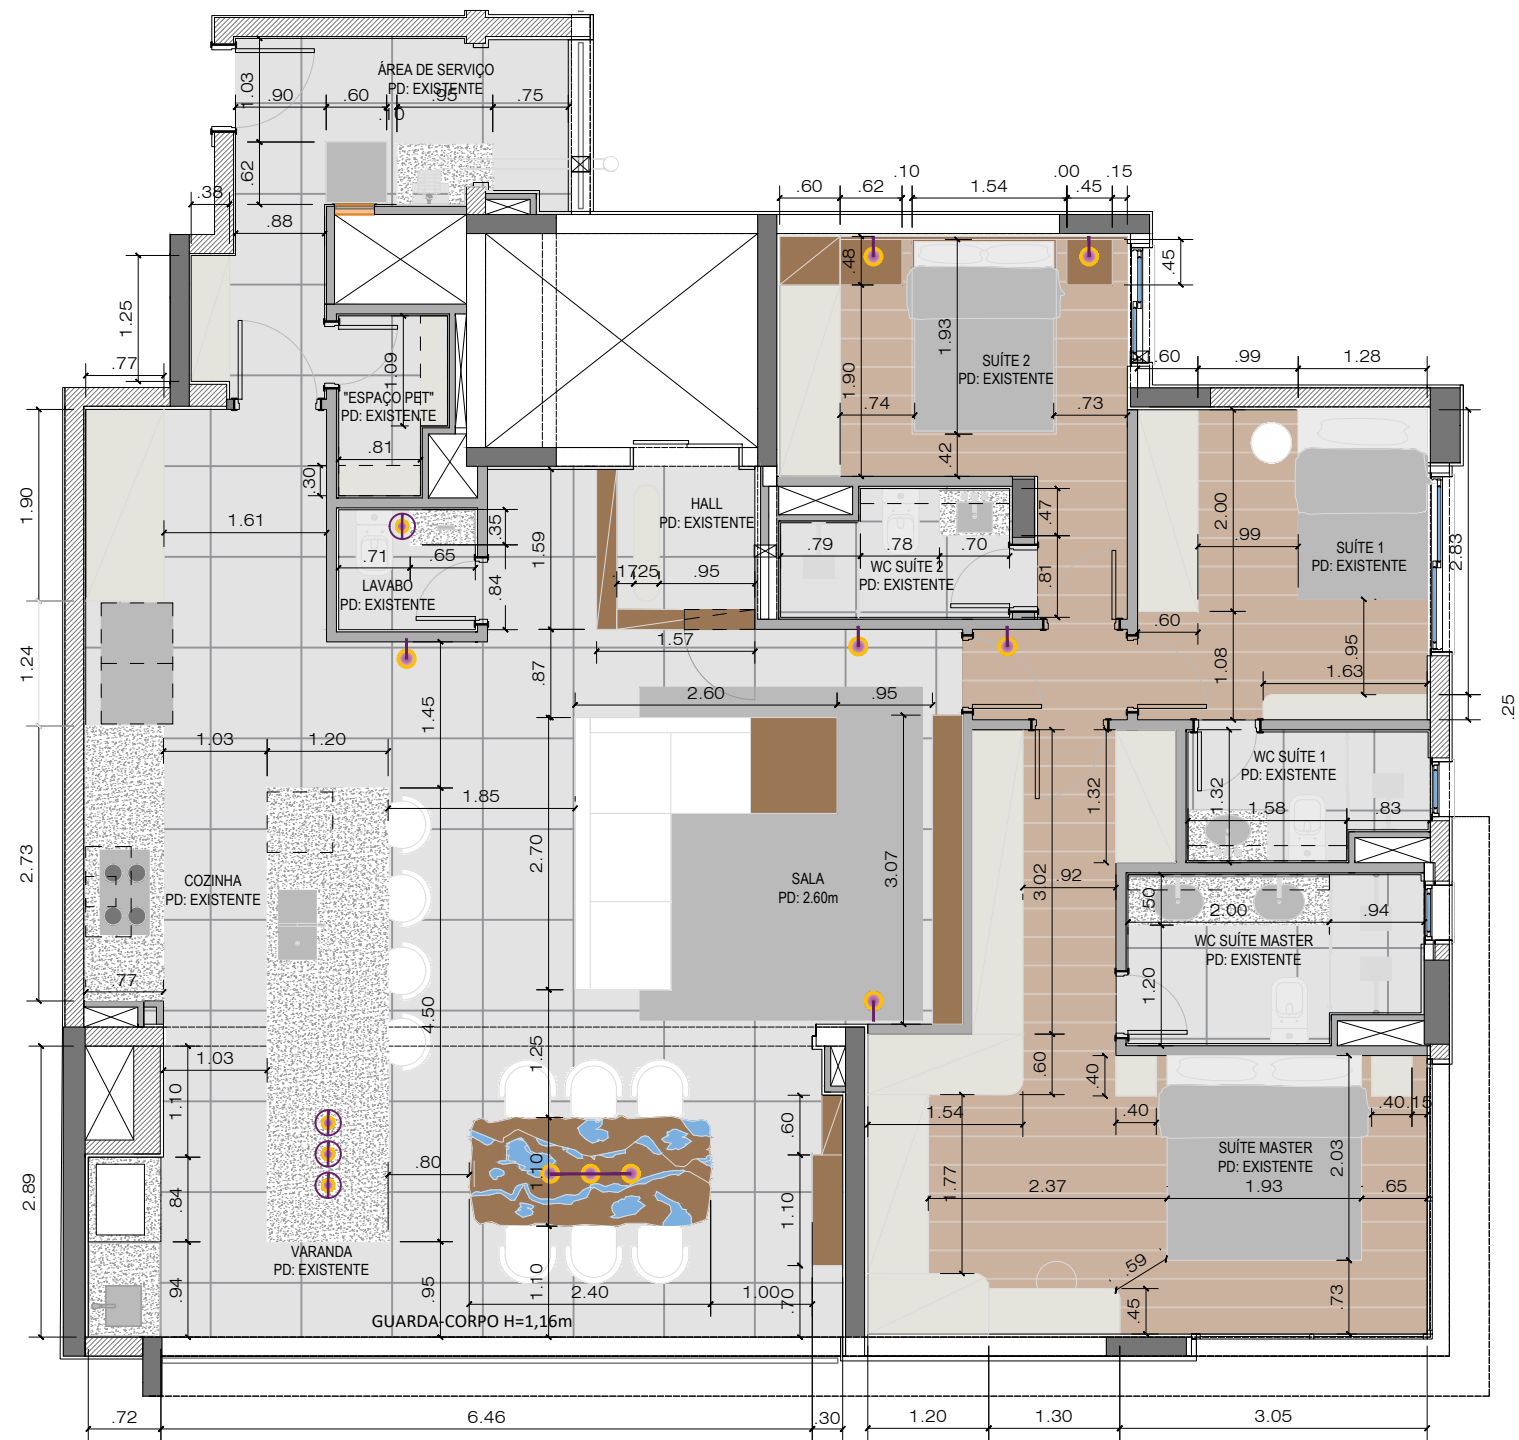

Remover porta balcão e demolir toda a parede para integração da área de serviço com a área técnica

Demolir parede do shaft e fazer fechamento alinhado a parede do lavabo. Ver planta de construir.

Fazer remoção da bacia sanitária, lavatório, box e chuveiro existente

Fazer remoção de bancada e bacia sanitária existente

Demolir paredes e porta para integração do hall de entrada

Fazer remoção de bancada existente


Demolir mureta existente

Fazer remoção de bancada existente

Demolir "dente" e deixar alinhado com o shaft

Fazer a remoção da porta existente. O piso já está nivelado, não havendo necessidade de intervenção.


Fazer remoção de bancada existente

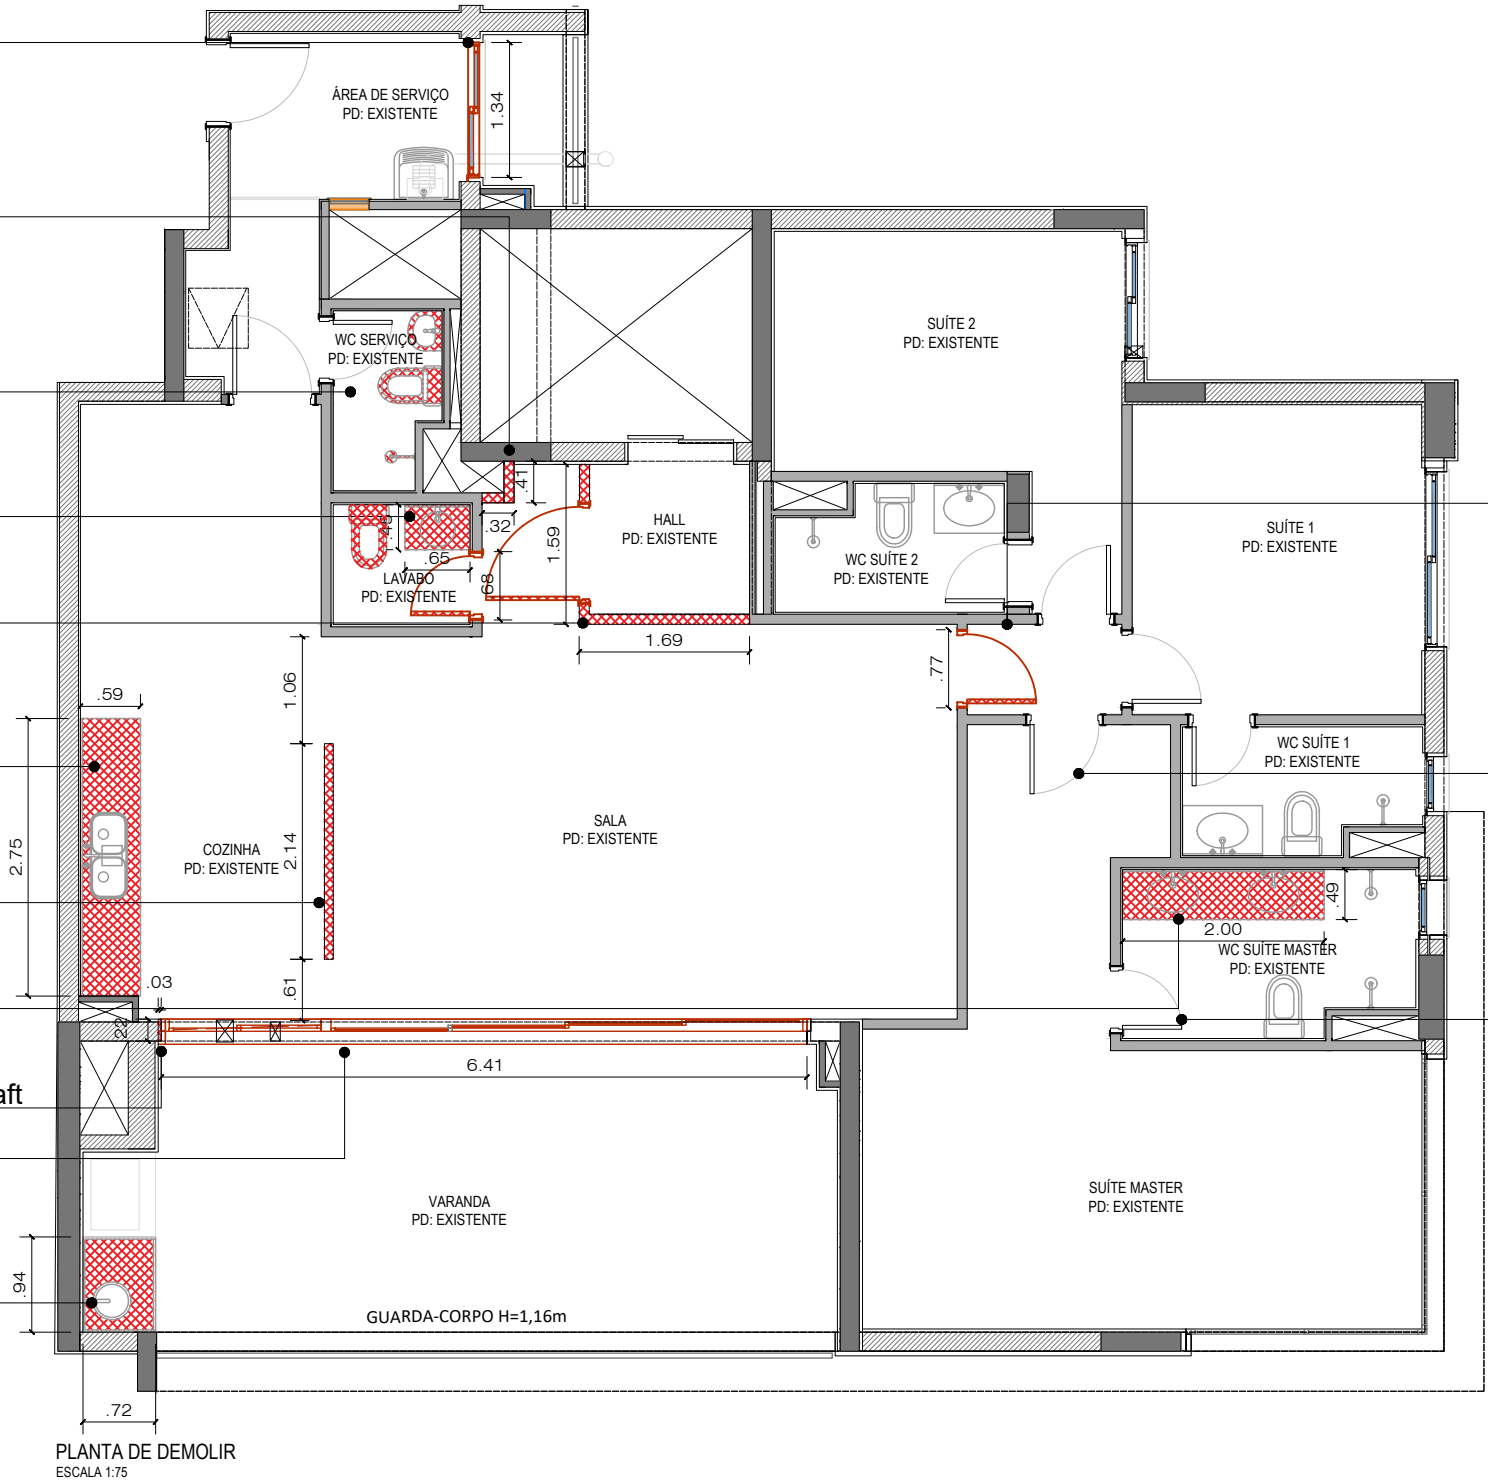

Corredor, lavabo e hall: remover portas, batentes e guarnições e requadrar o vão para receber porta em marcenaria

Suíte master: remover a guarnição interna da porta para que seja possível instalação de chapa de mdf sobre a porta para criar o efeito de porta mimetizada.

Banheiro master: remover a guarnição externa da porta para que seja possível instalação de chapa de mdf sobre a porta para criar o efeito de porta mimetizada.

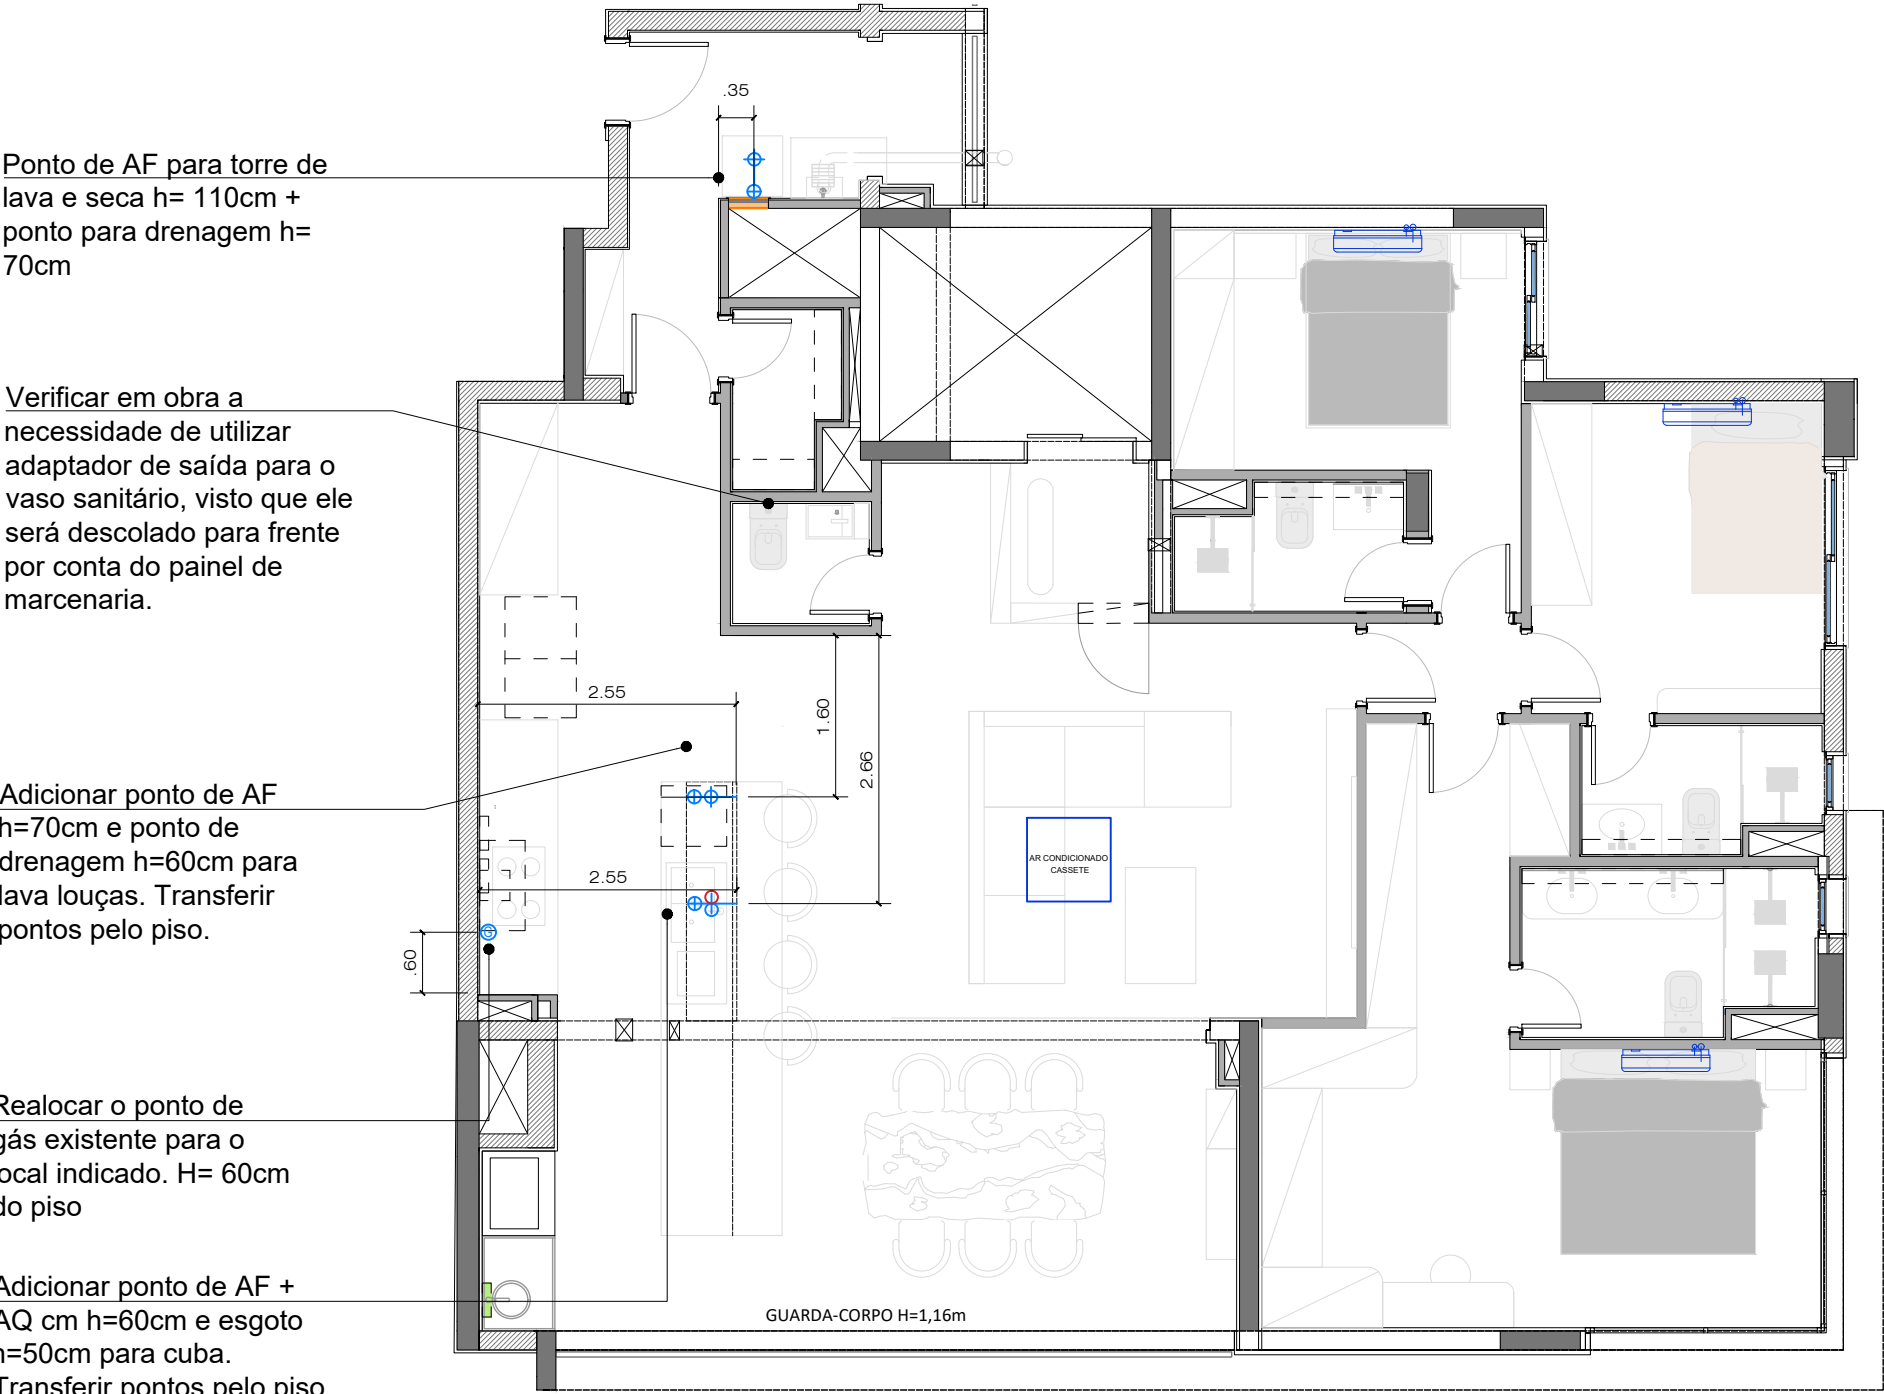

Ponto de AF para torre de lava e seca h= 110cm + ponto para drenagem h= 70cm

Verificar em obra a necessidade de utilizar adaptador de saída para o vaso sanitário, visto que ele será descolado para frente por conta do painel de marcenaria.

Adicionar ponto de AF h=70cm e ponto de drenagem h=60cm para lava louças. Transferir pontos pelo piso.


Realocar o ponto de gás existente para o local indicado. H= 60cm do piso

Adicionar ponto de AF + AQ cm h=60cm e esgoto h=50cm para cuba. Transferir pontos pelo piso.

PLANTA DE HIDRÁULICA E GÁS
ESCALA 1:75

SIMBOLOS	DESCRIÇÃO
	PONTO DE AF H= 60CM
	PONTO DE MONOCOMANDO H= 60CM
	PONTO DE ESGOTO H= 50CM
	PONTO DE GÁS H= 60CM

Prever dreno para ar condicionado. Conferir posicionamentos das máquinas.

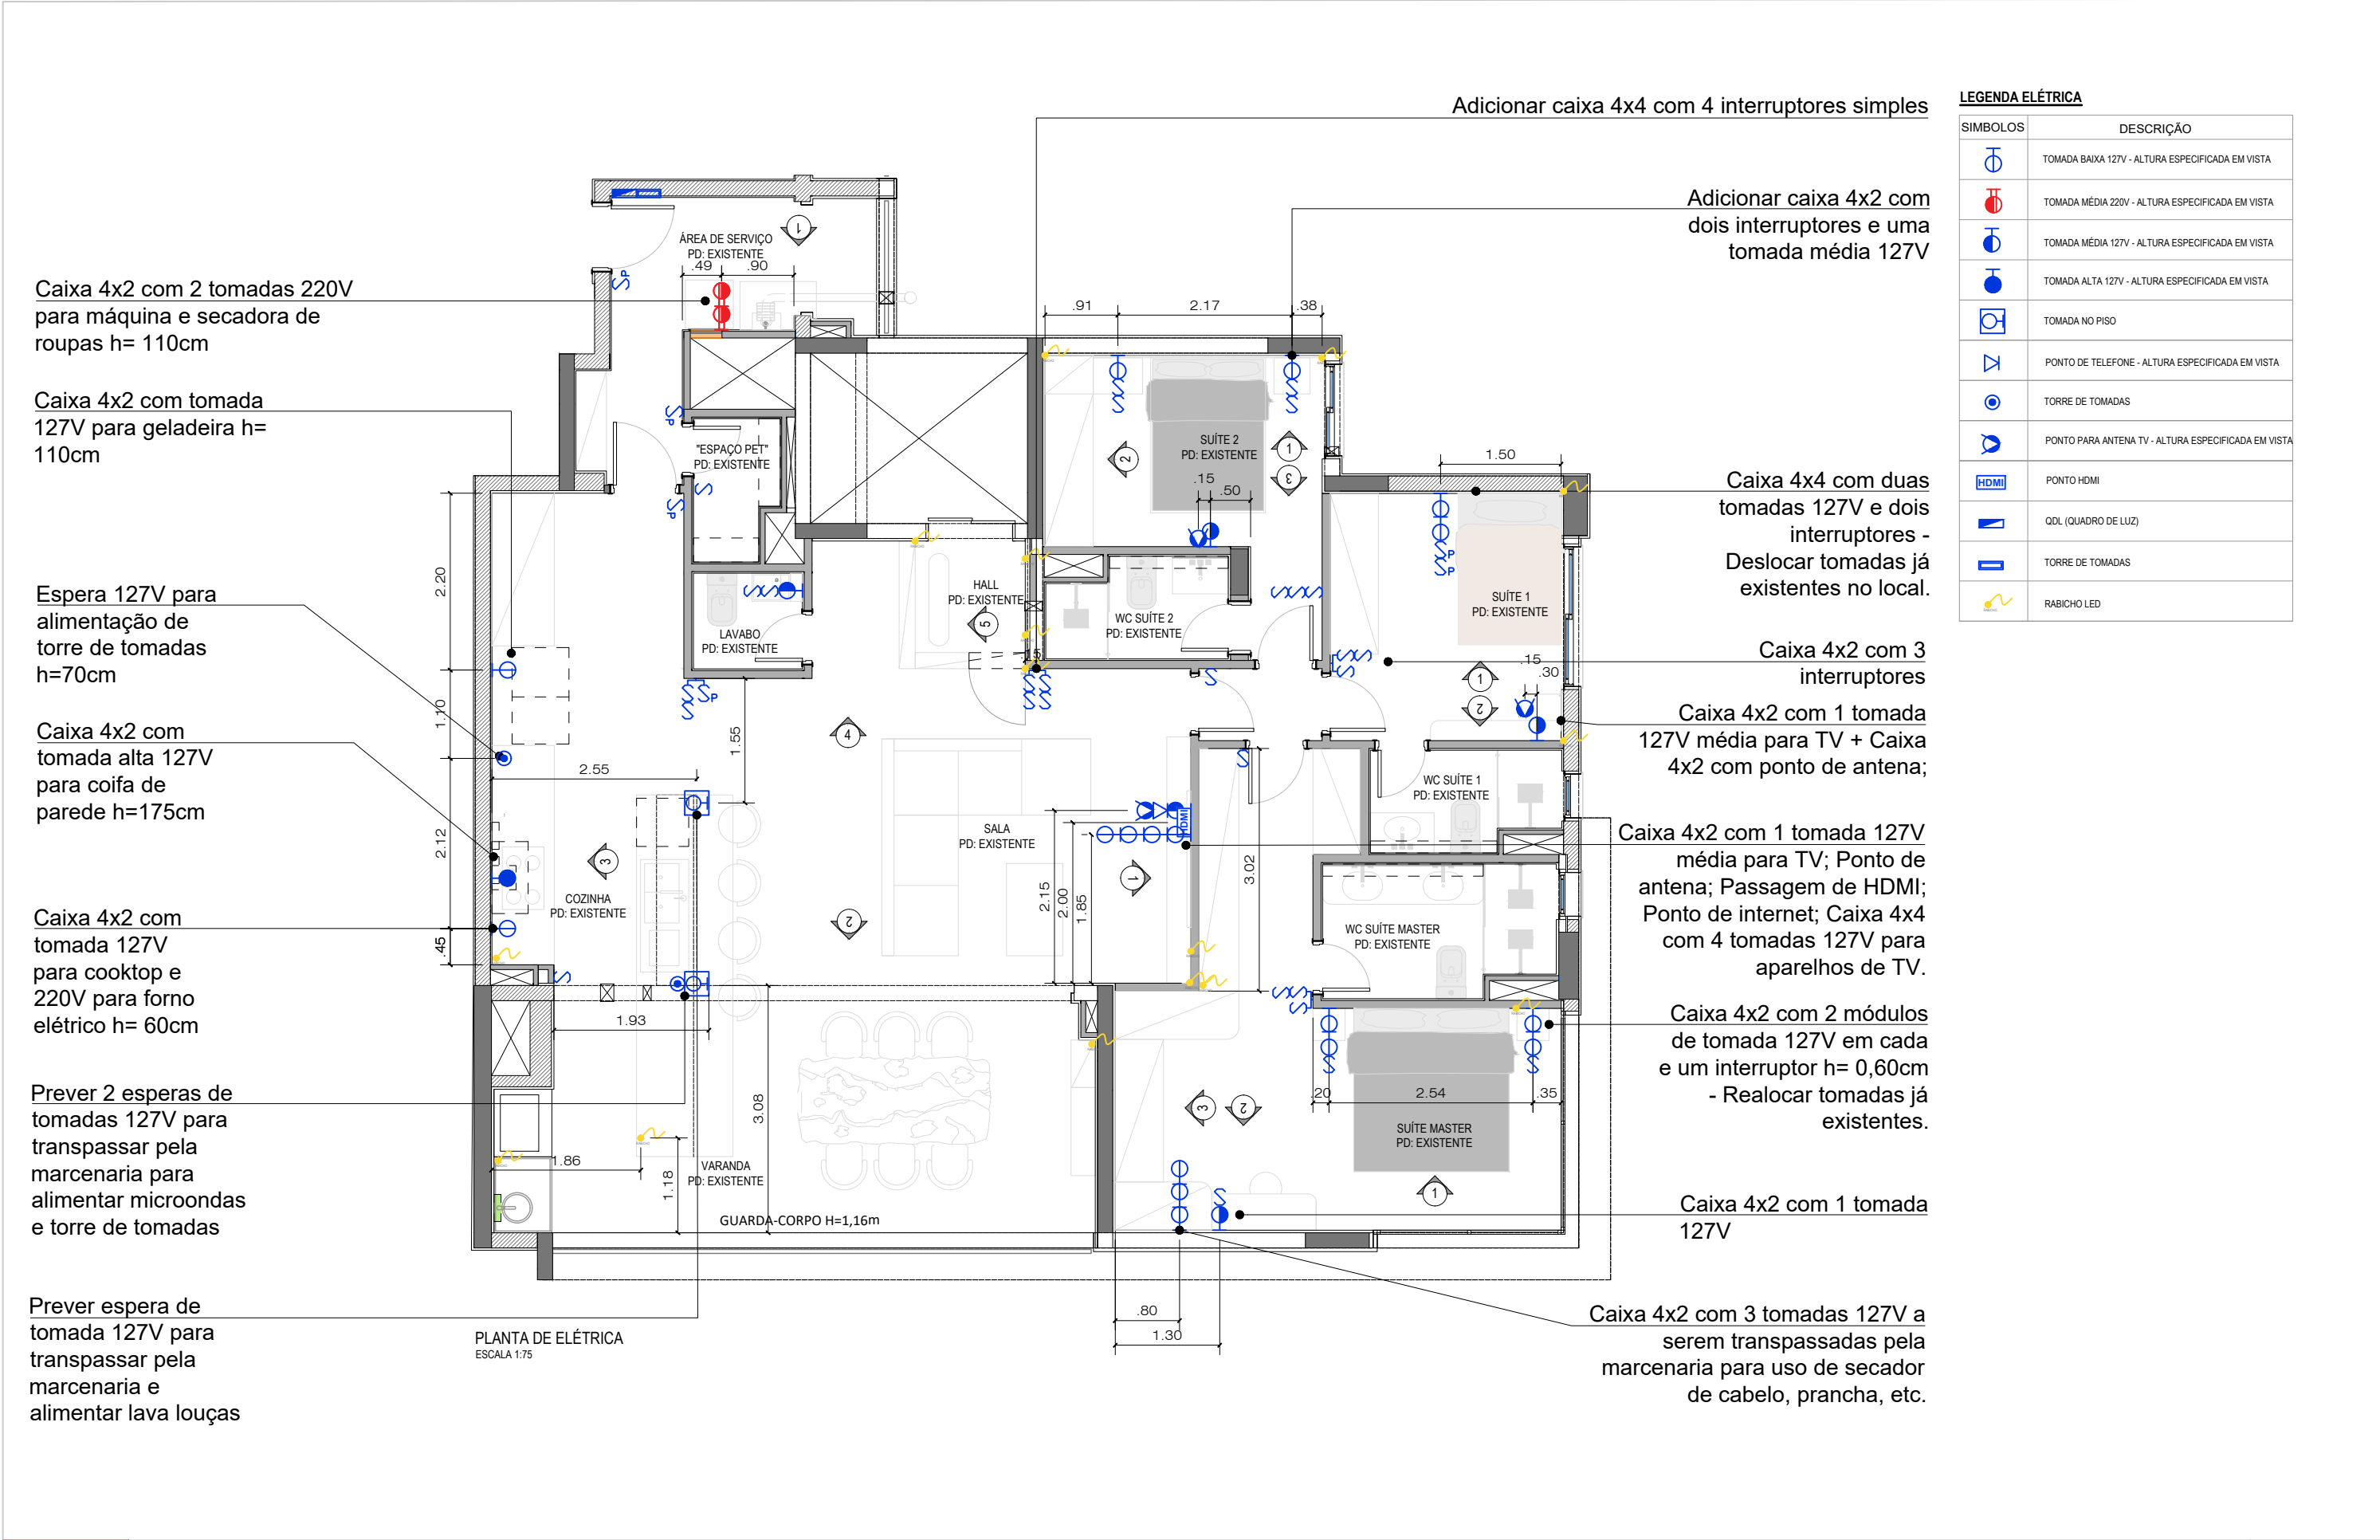

Caixa 4x2 com 2 tomadas 220V para máquina e secadora de roupas h= 110cm

Caixa 4x2 com tomada 127V para geladeira h= 110cm

Espera 127V para alimentação de torre de tomadas h=70cm

Caixa 4x2 com tomada alta 127V para coifa de parede h=175cm

Caixa 4x2 com tomada 127V para cooktop e 220V para forno elétrico h= 60cm

Prever 2 esperas de tomadas 127V para transpassar pela marcenaria para alimentar microondas e torre de tomadas

Prever espera de tomada 127V para transpassar pela marcenaria e alimentar lava louças

Adicionar caixa 4x4 com 4 interruptores simples

Adicionar caixa 4x2 com dois interruptores e uma tomada média 127V

Caixa 4x4 com duas tomadas 127V e dois interruptores - Deslocar tomadas já existentes no local.

Caixa 4x2 com 3 interruptores

Caixa 4x2 com 1 tomada 127V média para TV + Caixa 4x2 com ponto de antena;


Caixa 4x2 com 1 tomada 127V média para TV; Ponto de antena; Passagem de HDMI; Ponto de internet; Caixa 4x4 com 4 tomadas 127V para aparelhos de TV.

Caixa 4x2 com 2 módulos de tomada 127V em cada e um interruptor h= 0,60cm - Realocar tomadas já existentes.


Caixa 4x2 com 1 tomada 127V

Caixa 4x2 com 3 tomadas 127V a serem transpassadas pela marcenaria para uso de secador de cabelo, prancha, etc.

SIMBOLOS	DESCRIÇÃO
	TOMADA BAIXA 127V - ALTURA ESPECIFICADA EM VISTA
	TOMADA MÉDIA 220V - ALTURA ESPECIFICADA EM VISTA
	TOMADA MÉDIA 127V - ALTURA ESPECIFICADA EM VISTA
	TOMADA ALTA 127V - ALTURA ESPECIFICADA EM VISTA
	TOMADA NO PISO
	PONTO DE TELEFONE - ALTURA ESPECIFICADA EM VISTA
	TORRE DE TOMADAS
	PONTO PARA ANTENA TV - ALTURA ESPECIFICADA EM VISTA
	PONTO HDMI
	QDL (QUADRO DE LUZ)
	TORRE DE TOMADAS
	RABICHO LED

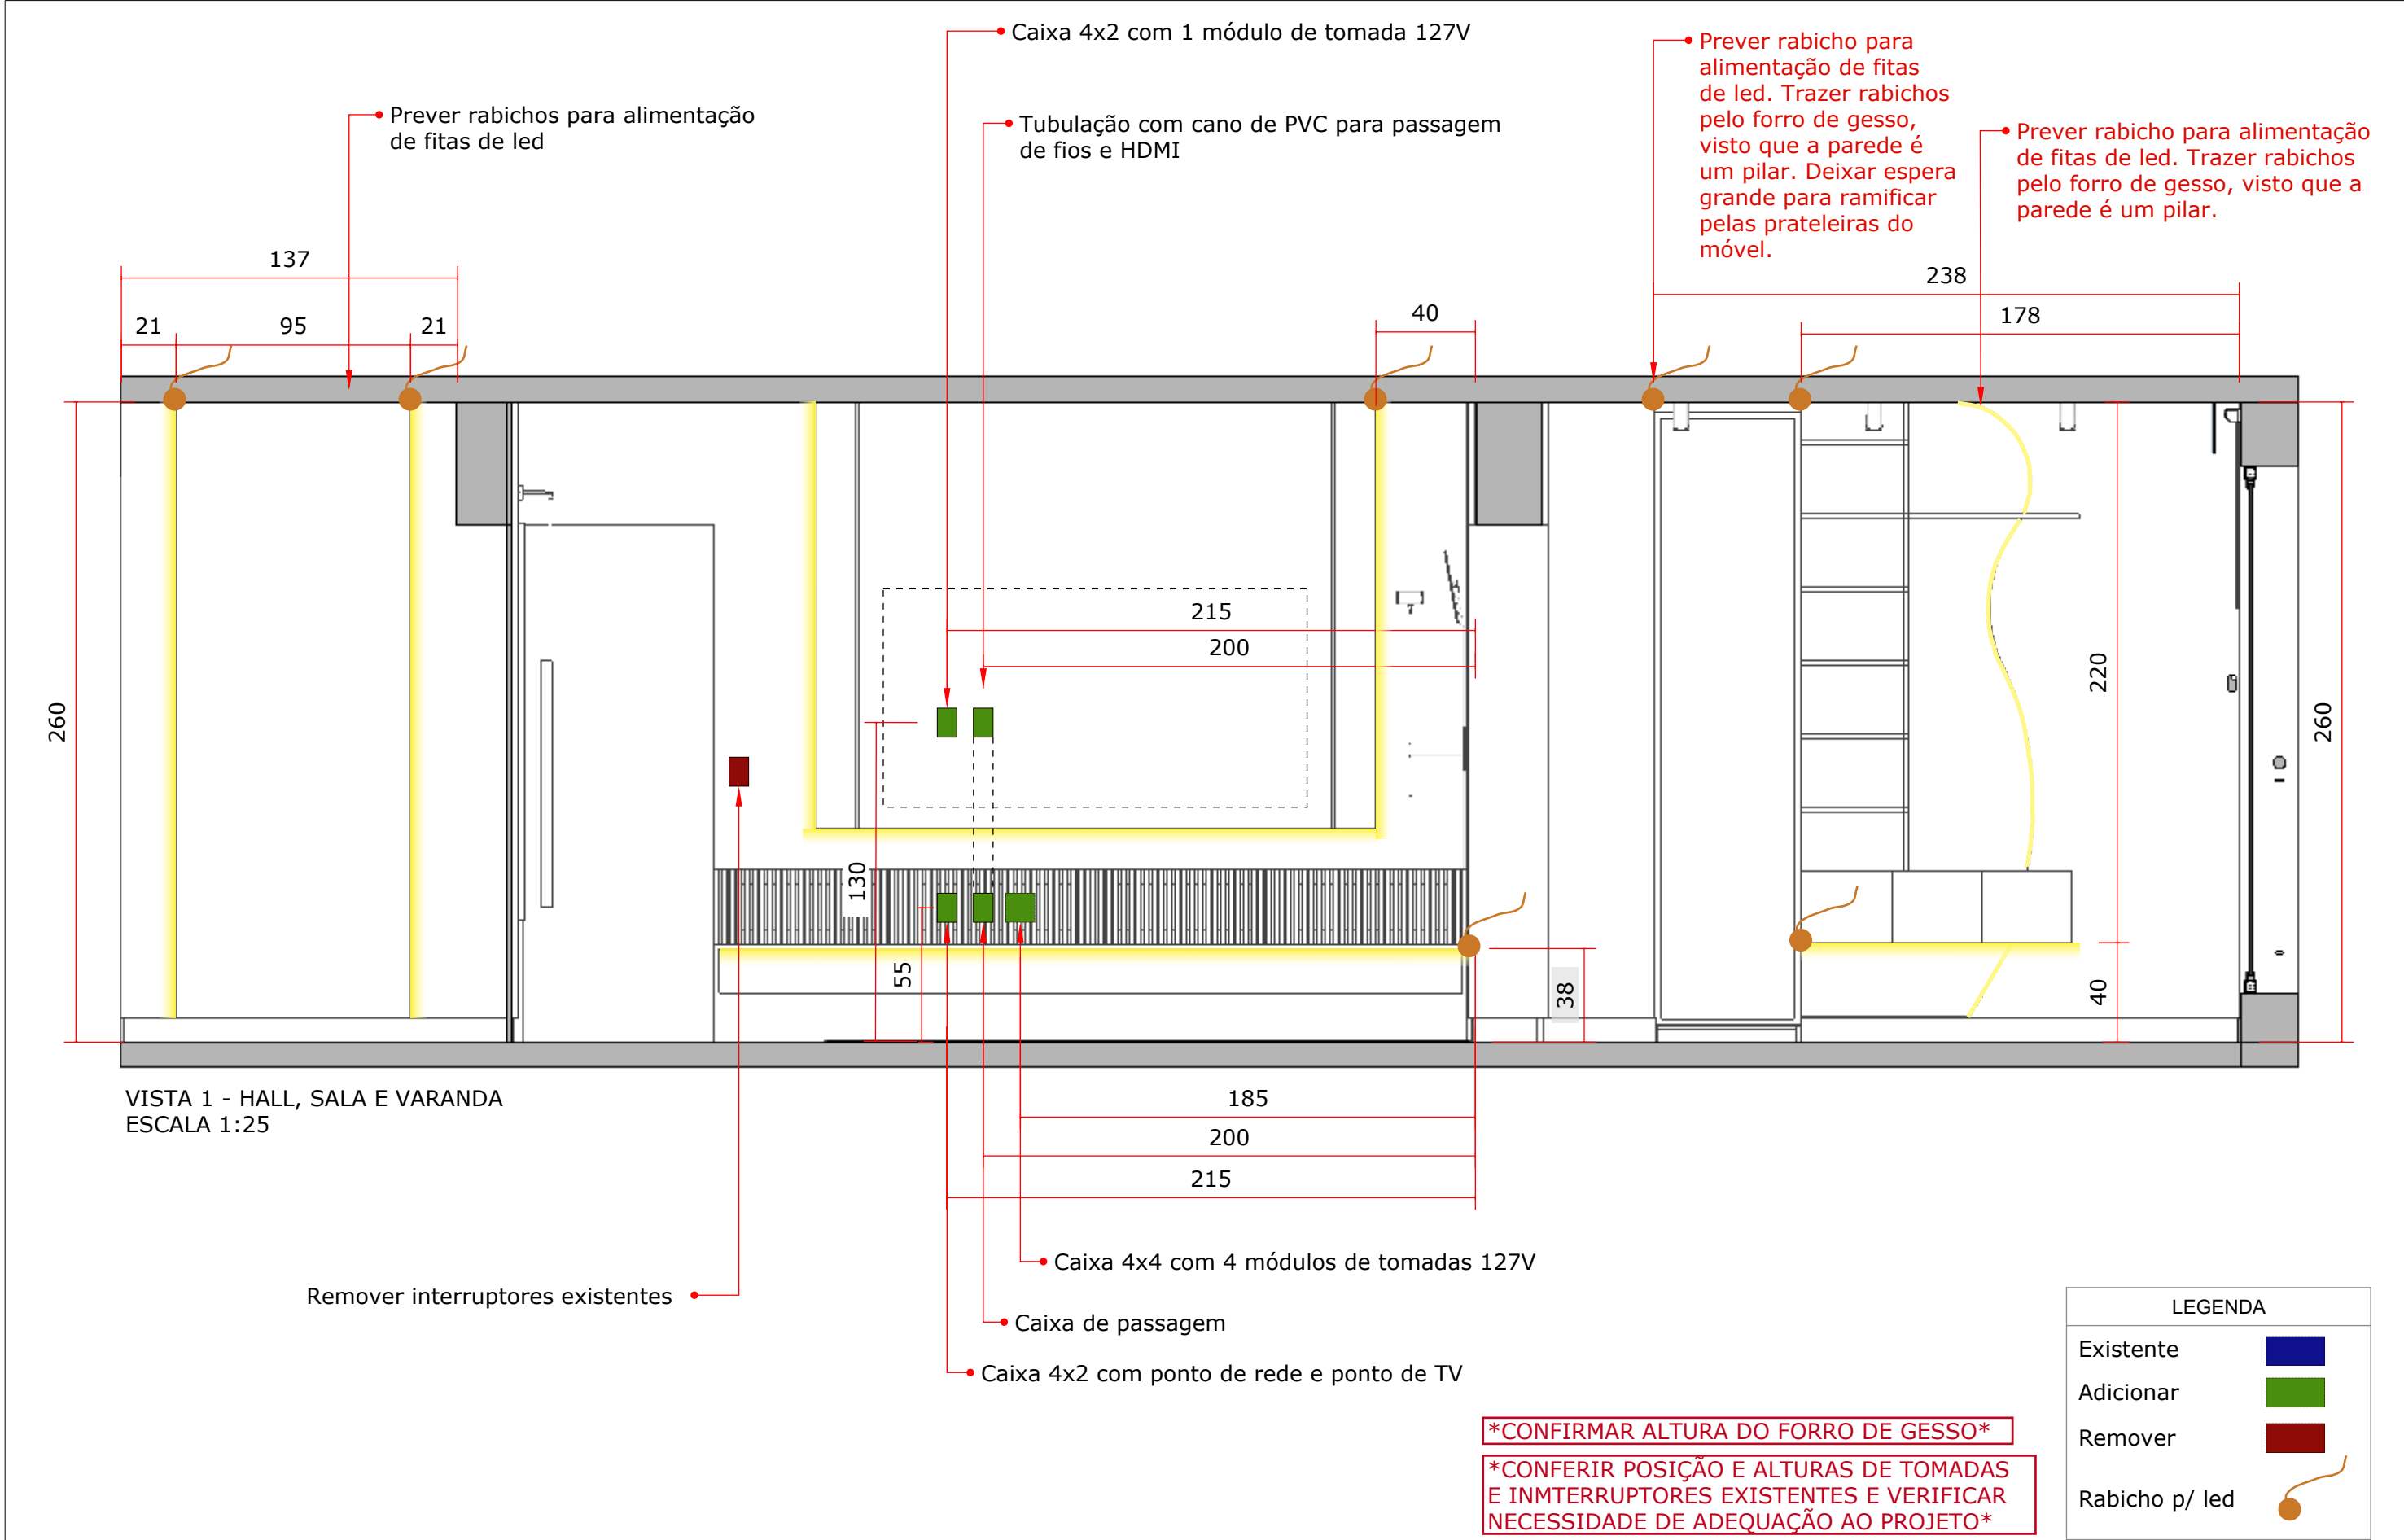

	ESCALA 1:25	CONTEÚDO: VISTA DE ELÉTRICA	RESPONSÁVEL: ARQUITETA BEATRIZ MASSI	FOLHA
		CLIENTE: ALEX E KARINE	DATA: 12/08/2025	7

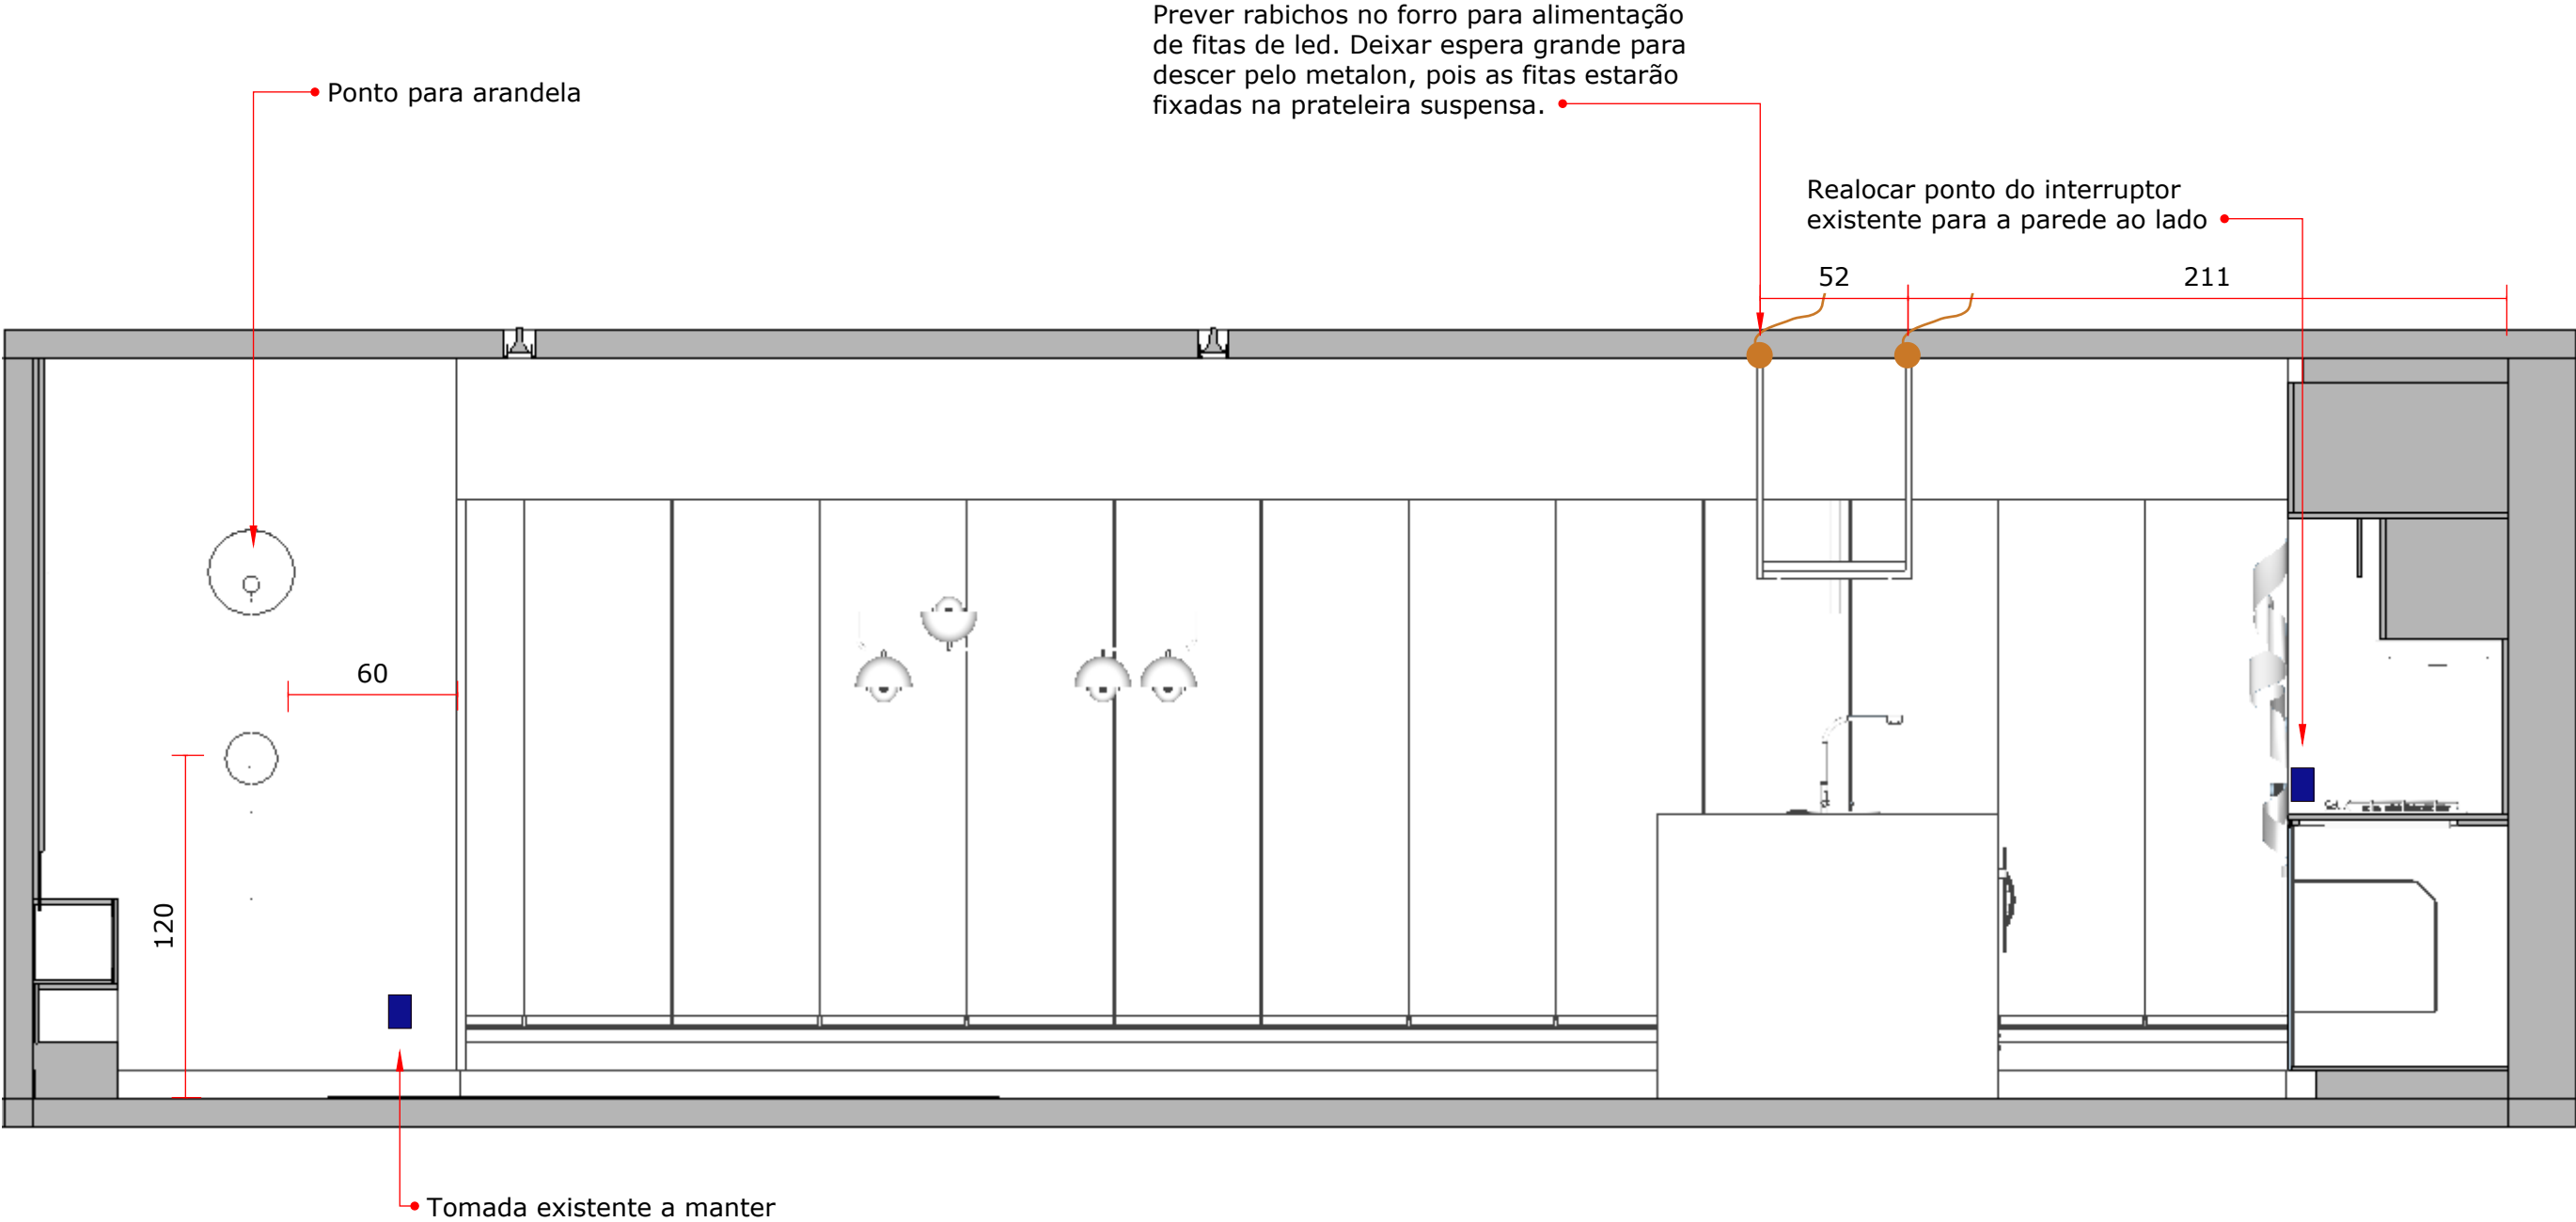


VISTA 2 - PONTOS ELÉTRICOS SALA, VARANDA E COZINHA
ESCALA 1:25

CONFIRMAR ALTURA DO FORRO DE GESSO

CONFERIR POSIÇÃO E ALTURAS DE TOMADAS E INTERRUPTORES EXISTENTES E VERIFICAR NECESSIDADE DE ADEQUAÇÃO AO PROJETO

LEGENDA	
Existente	
Adicionar	
Remover	
Rabicho p/ led	

	ESCALA 1:25	CONTEÚDO: PONTOS ELÉTRICOS SALA, VARANDA E COZINHA	RESPONSÁVEL: ARQUITETA BEATRIZ MASSI	FOLHA
		CLIENTE: ALEX E KARINE	DATA: 12/08/2025	8

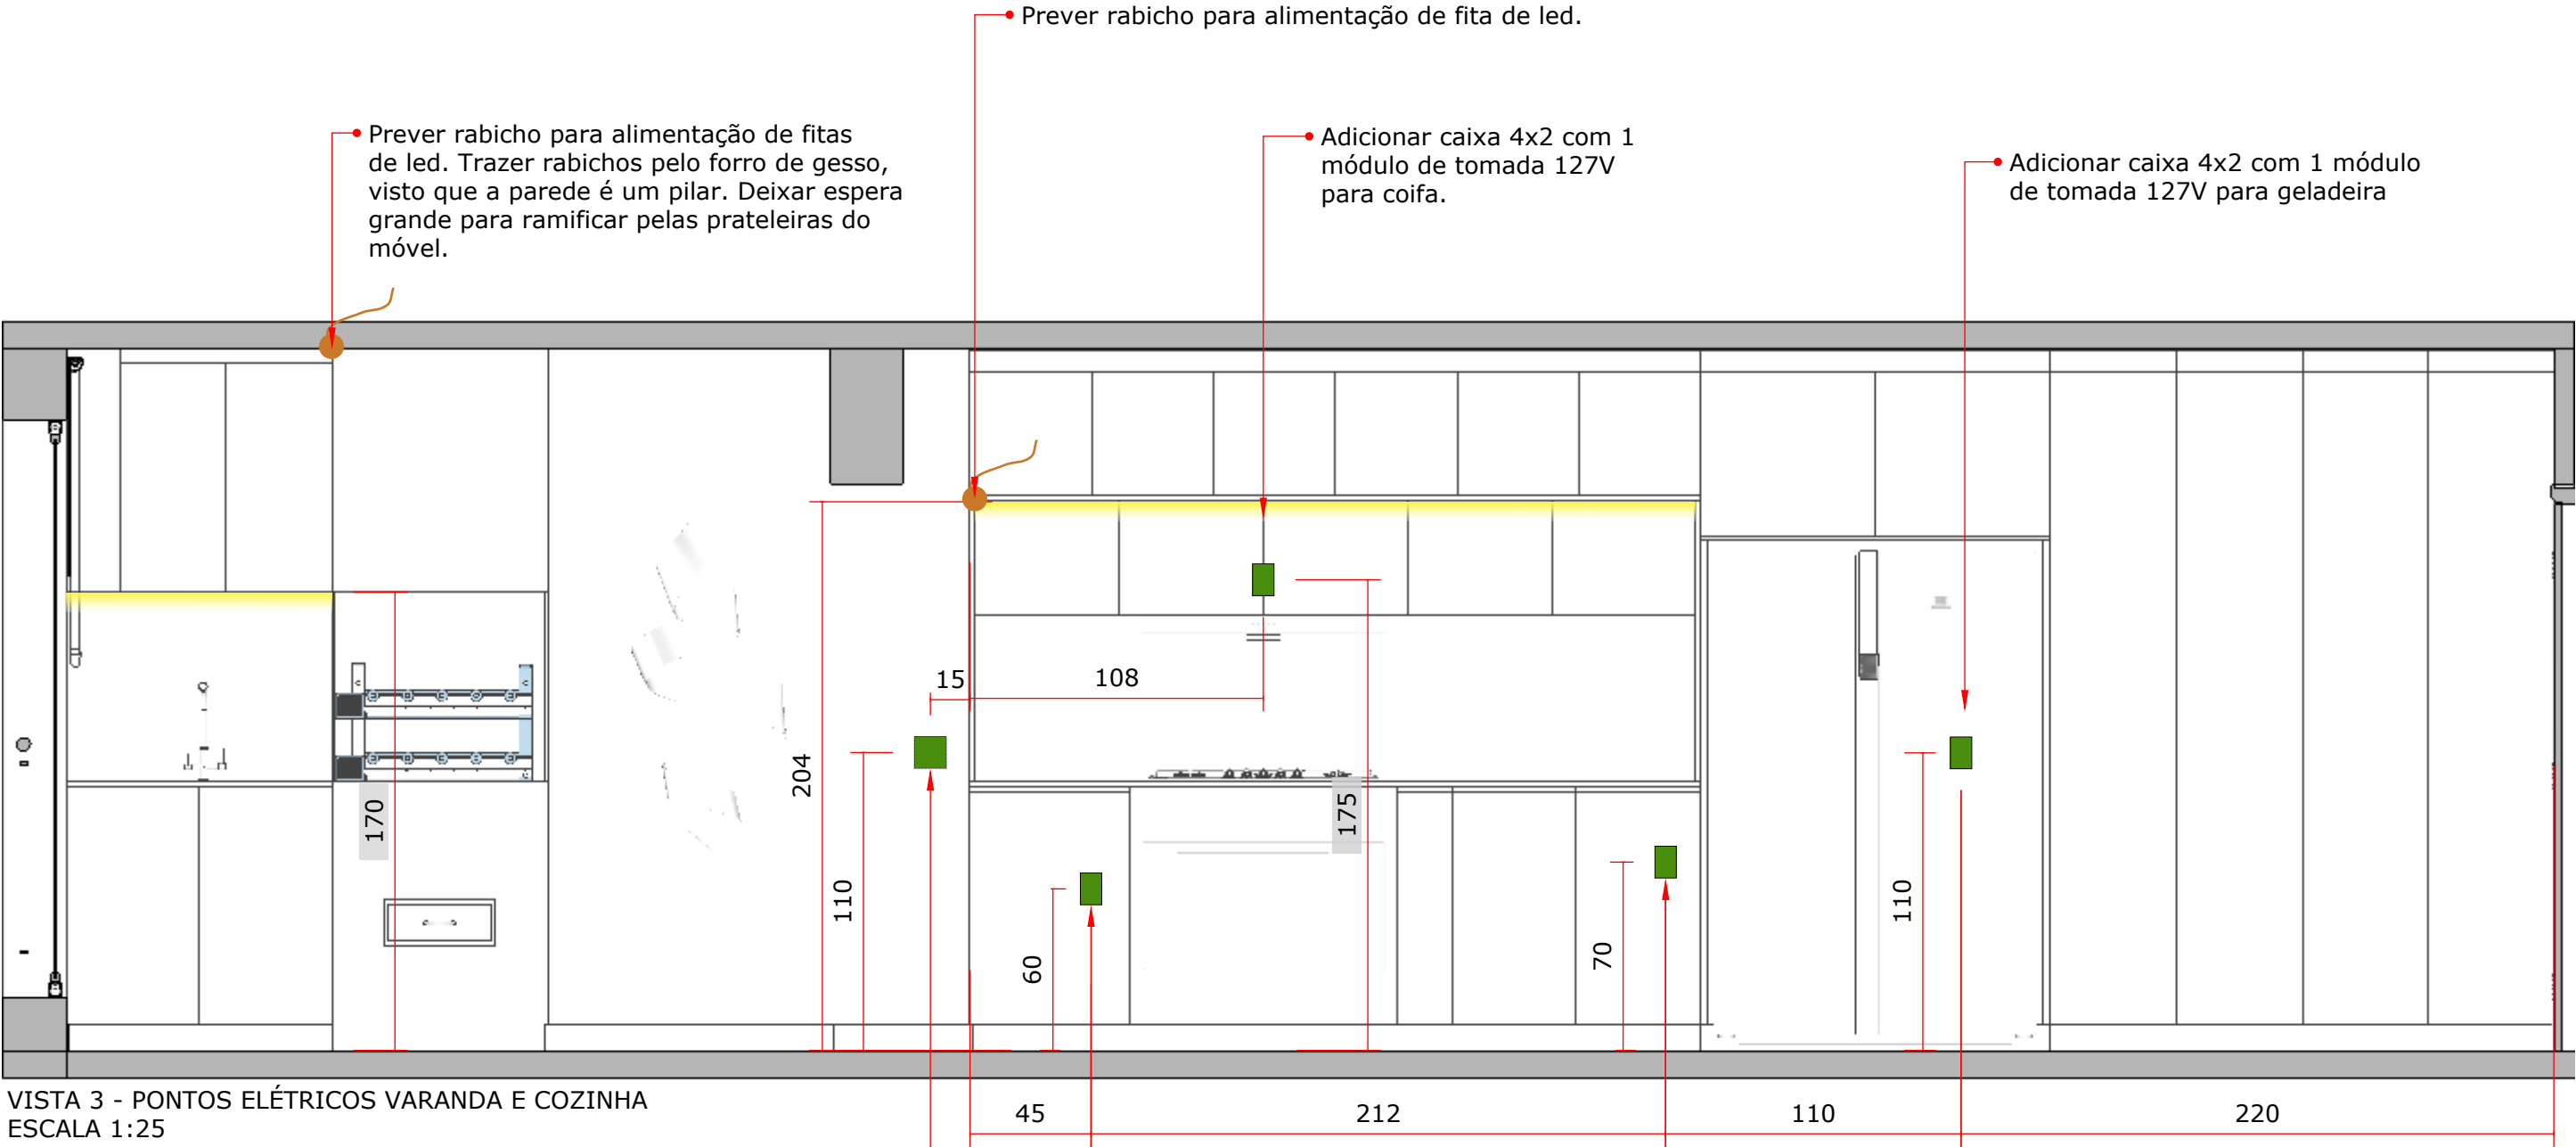

VISTA 3 - PONTOS ELÉTRICOS VARANDA E COZINHA
ESCALA 1:25



ESCALA
1:25

CONTEÚDO: PONTOS ELÉTRICOS VARANDA E COZINHA

CLIENTE: ALEX E KARINE


RESPONSÁVEL: ARQUITETA BEATRIZ MASSI

DATA: 12/08/2025

FOLHA

9

Prever rabicho par alimentação de fitas de led.
Prever espera grande para ramificar pela marcenaria.

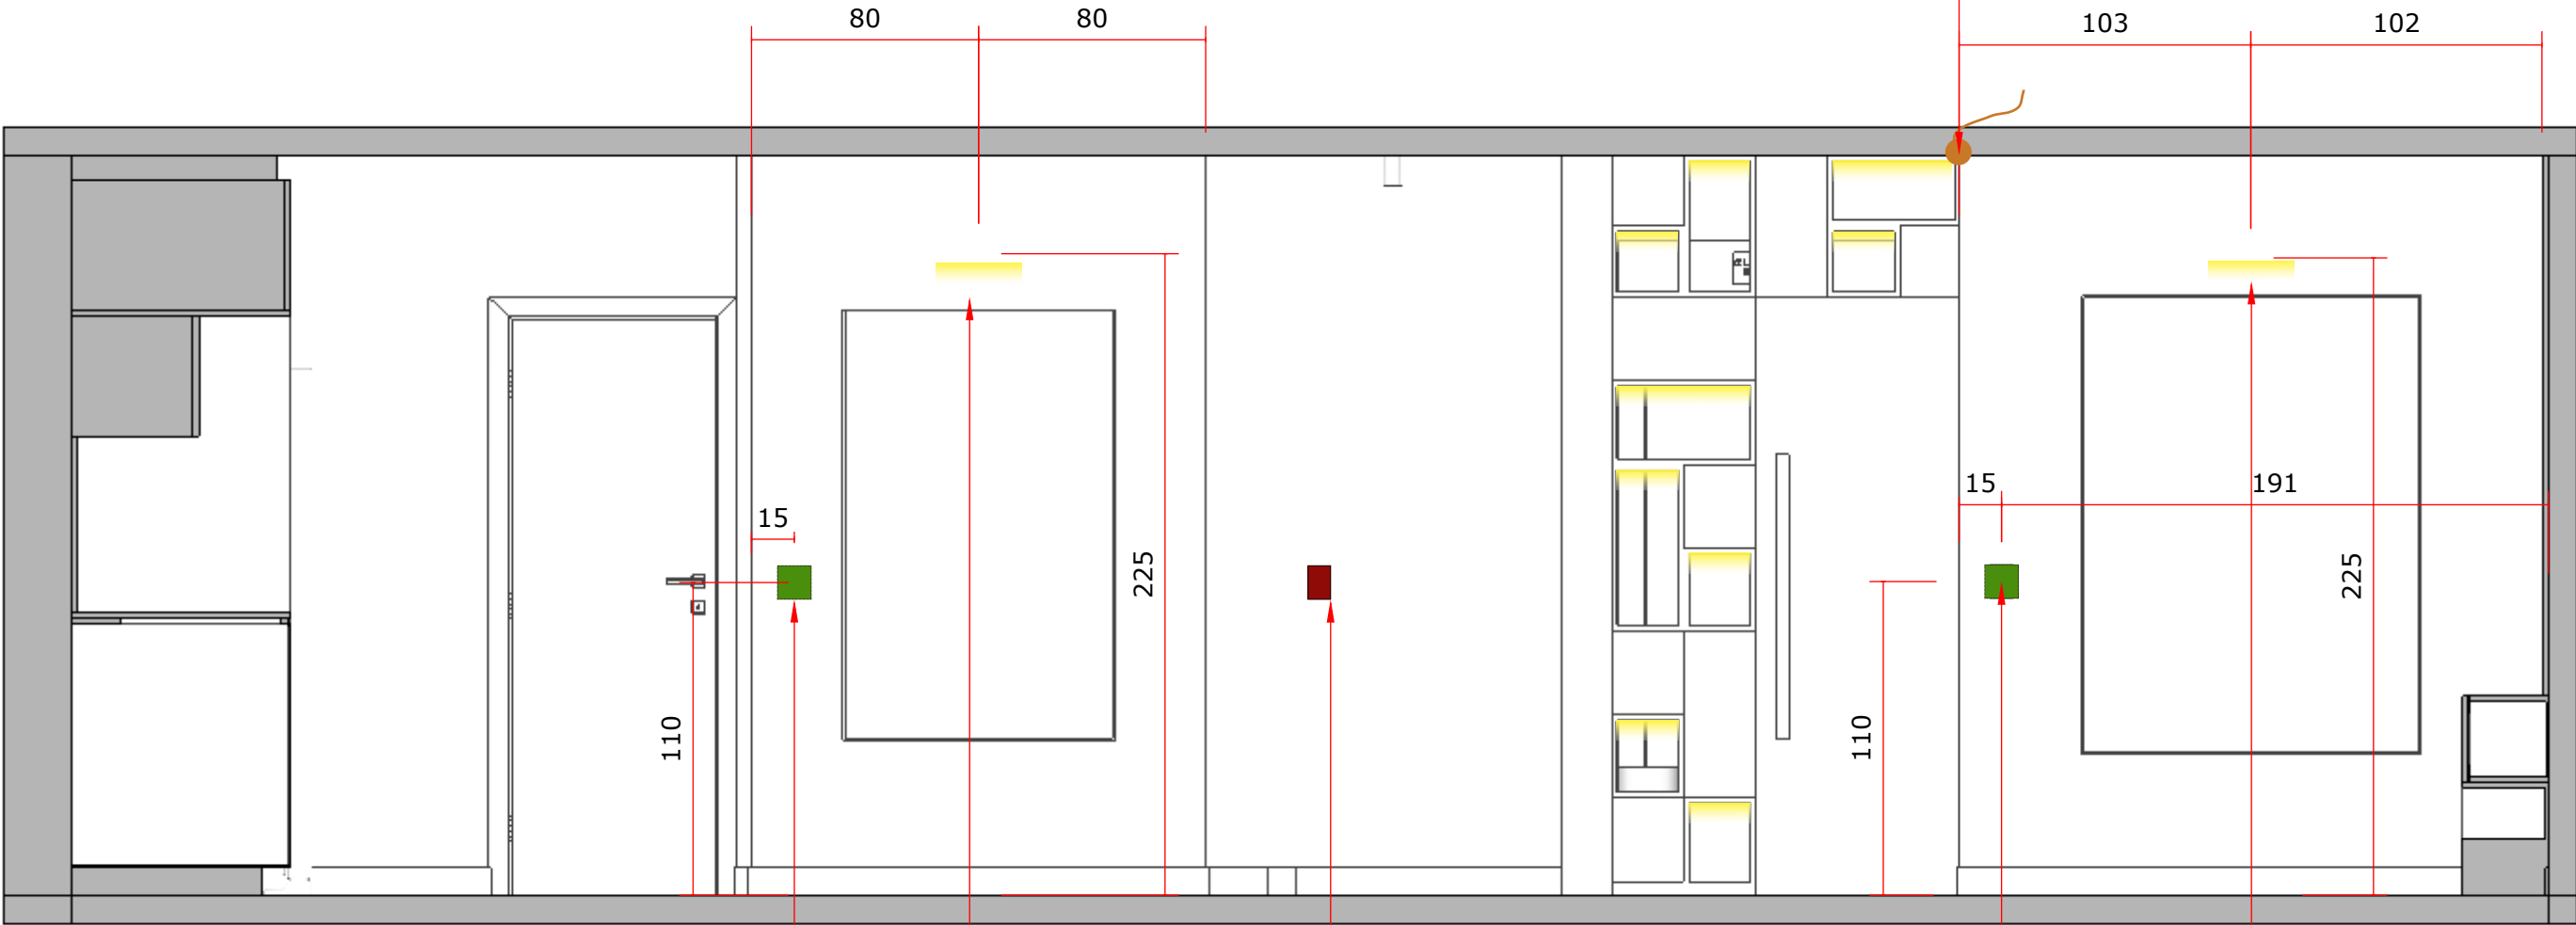


VISTA 4 - PONTOS ELÉTRICOS SALA
ESCALA 1:25

- Ponto para arandela
- Remover interruptores existentes
- Ponto elétrico existente. Acrescentar 2 interruptores totalizando 4, sendo um deles paralelo.
- Adicionar caixa 4x4 com 6 interruptores
- Ponto para arandela

CONFIRMAR ALTURA DO FORRO DE GESSO
CONFERIR POSIÇÃO E ALTURAS DE TOMADAS E INTERRUPTORES EXISTENTES E VERIFICAR NECESSIDADE DE ADEQUAÇÃO AO PROJETO

LEGENDA	
Existente	
Adicionar	
Remover	
Rabicho p/ led	

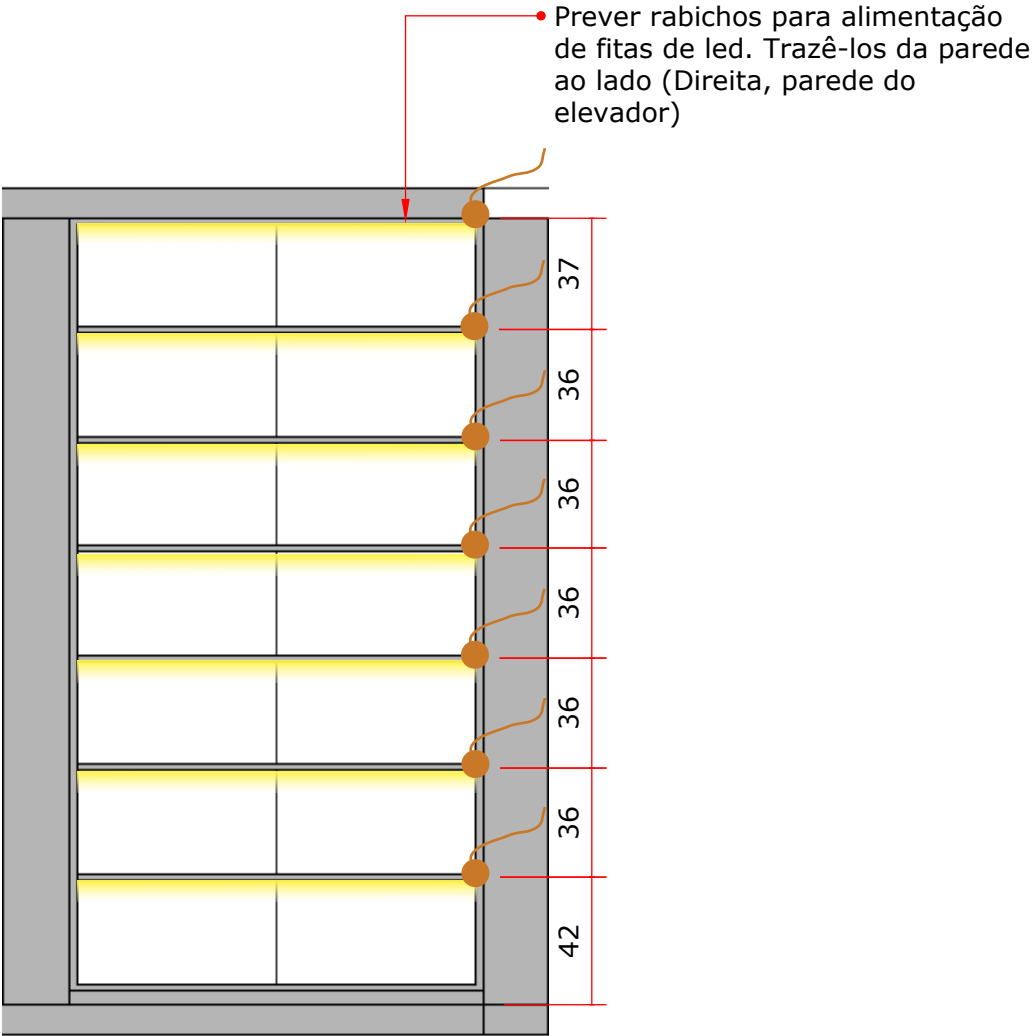


VISTA 5 - PONTOS ELÉTRICOS HALL
ESCALA 1:25

CONFIRMAR ALTURA DO FORRO DE GESSO

*CONFERIR POSIÇÃO E ALTURAS DE TOMADAS
E INMERRUPTORES EXISTENTES E VERIFICAR
NECESSIDADE DE ADEQUAÇÃO AO PROJETO*

LEGENDA	
Existente	
Adicionar	
Remover	
Rabicho p/ led	

	ESCALA 1:25	CONTEÚDO: PONTOS ELÉTRICOS HALL	RESPONSÁVEL: ARQUITETA BEATRIZ MASSI	FOLHA
		CLIENTE: ALEX E KARINE	DATA: 12/08/2025	11

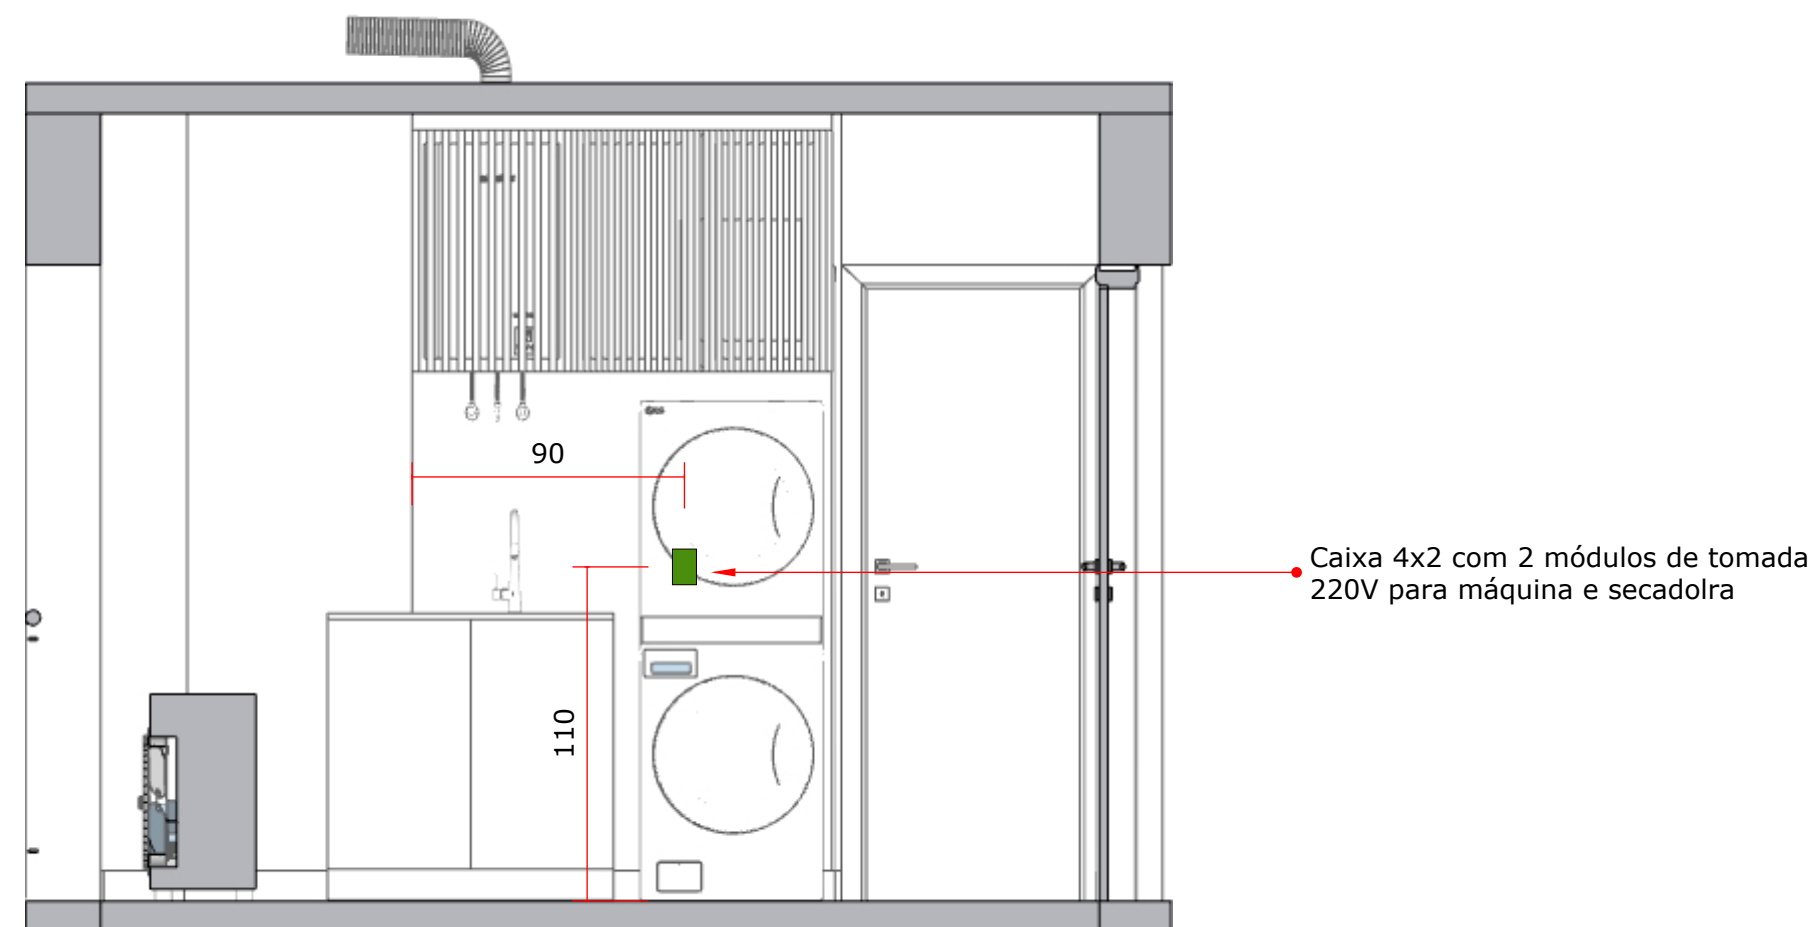

VISTA 1 - PONTOS DE ELÉTRICA LAVANDERIA

CONFIRMAR ALTURA DO FORRO DE GESSO

CONFERIR POSIÇÃO E ALTURAS DE TOMADAS E INTERRUPTORES EXISTENTES E VERIFICAR NECESSIDADE DE ADEQUAÇÃO AO PROJETO

LEGENDA	
Existente	
Adicionar	
Remover	
Rabicho p/ led	



ESCALA
1:25

CONTEÚDO: PONTOS DE ELÉTRICA LAVANDERIA


CLIENTE: ALEX E KARINE


RESPONSÁVEL: ARQUITETA BEATRIZ MASSI

DATA: 12/08/2025


FOLHA

12

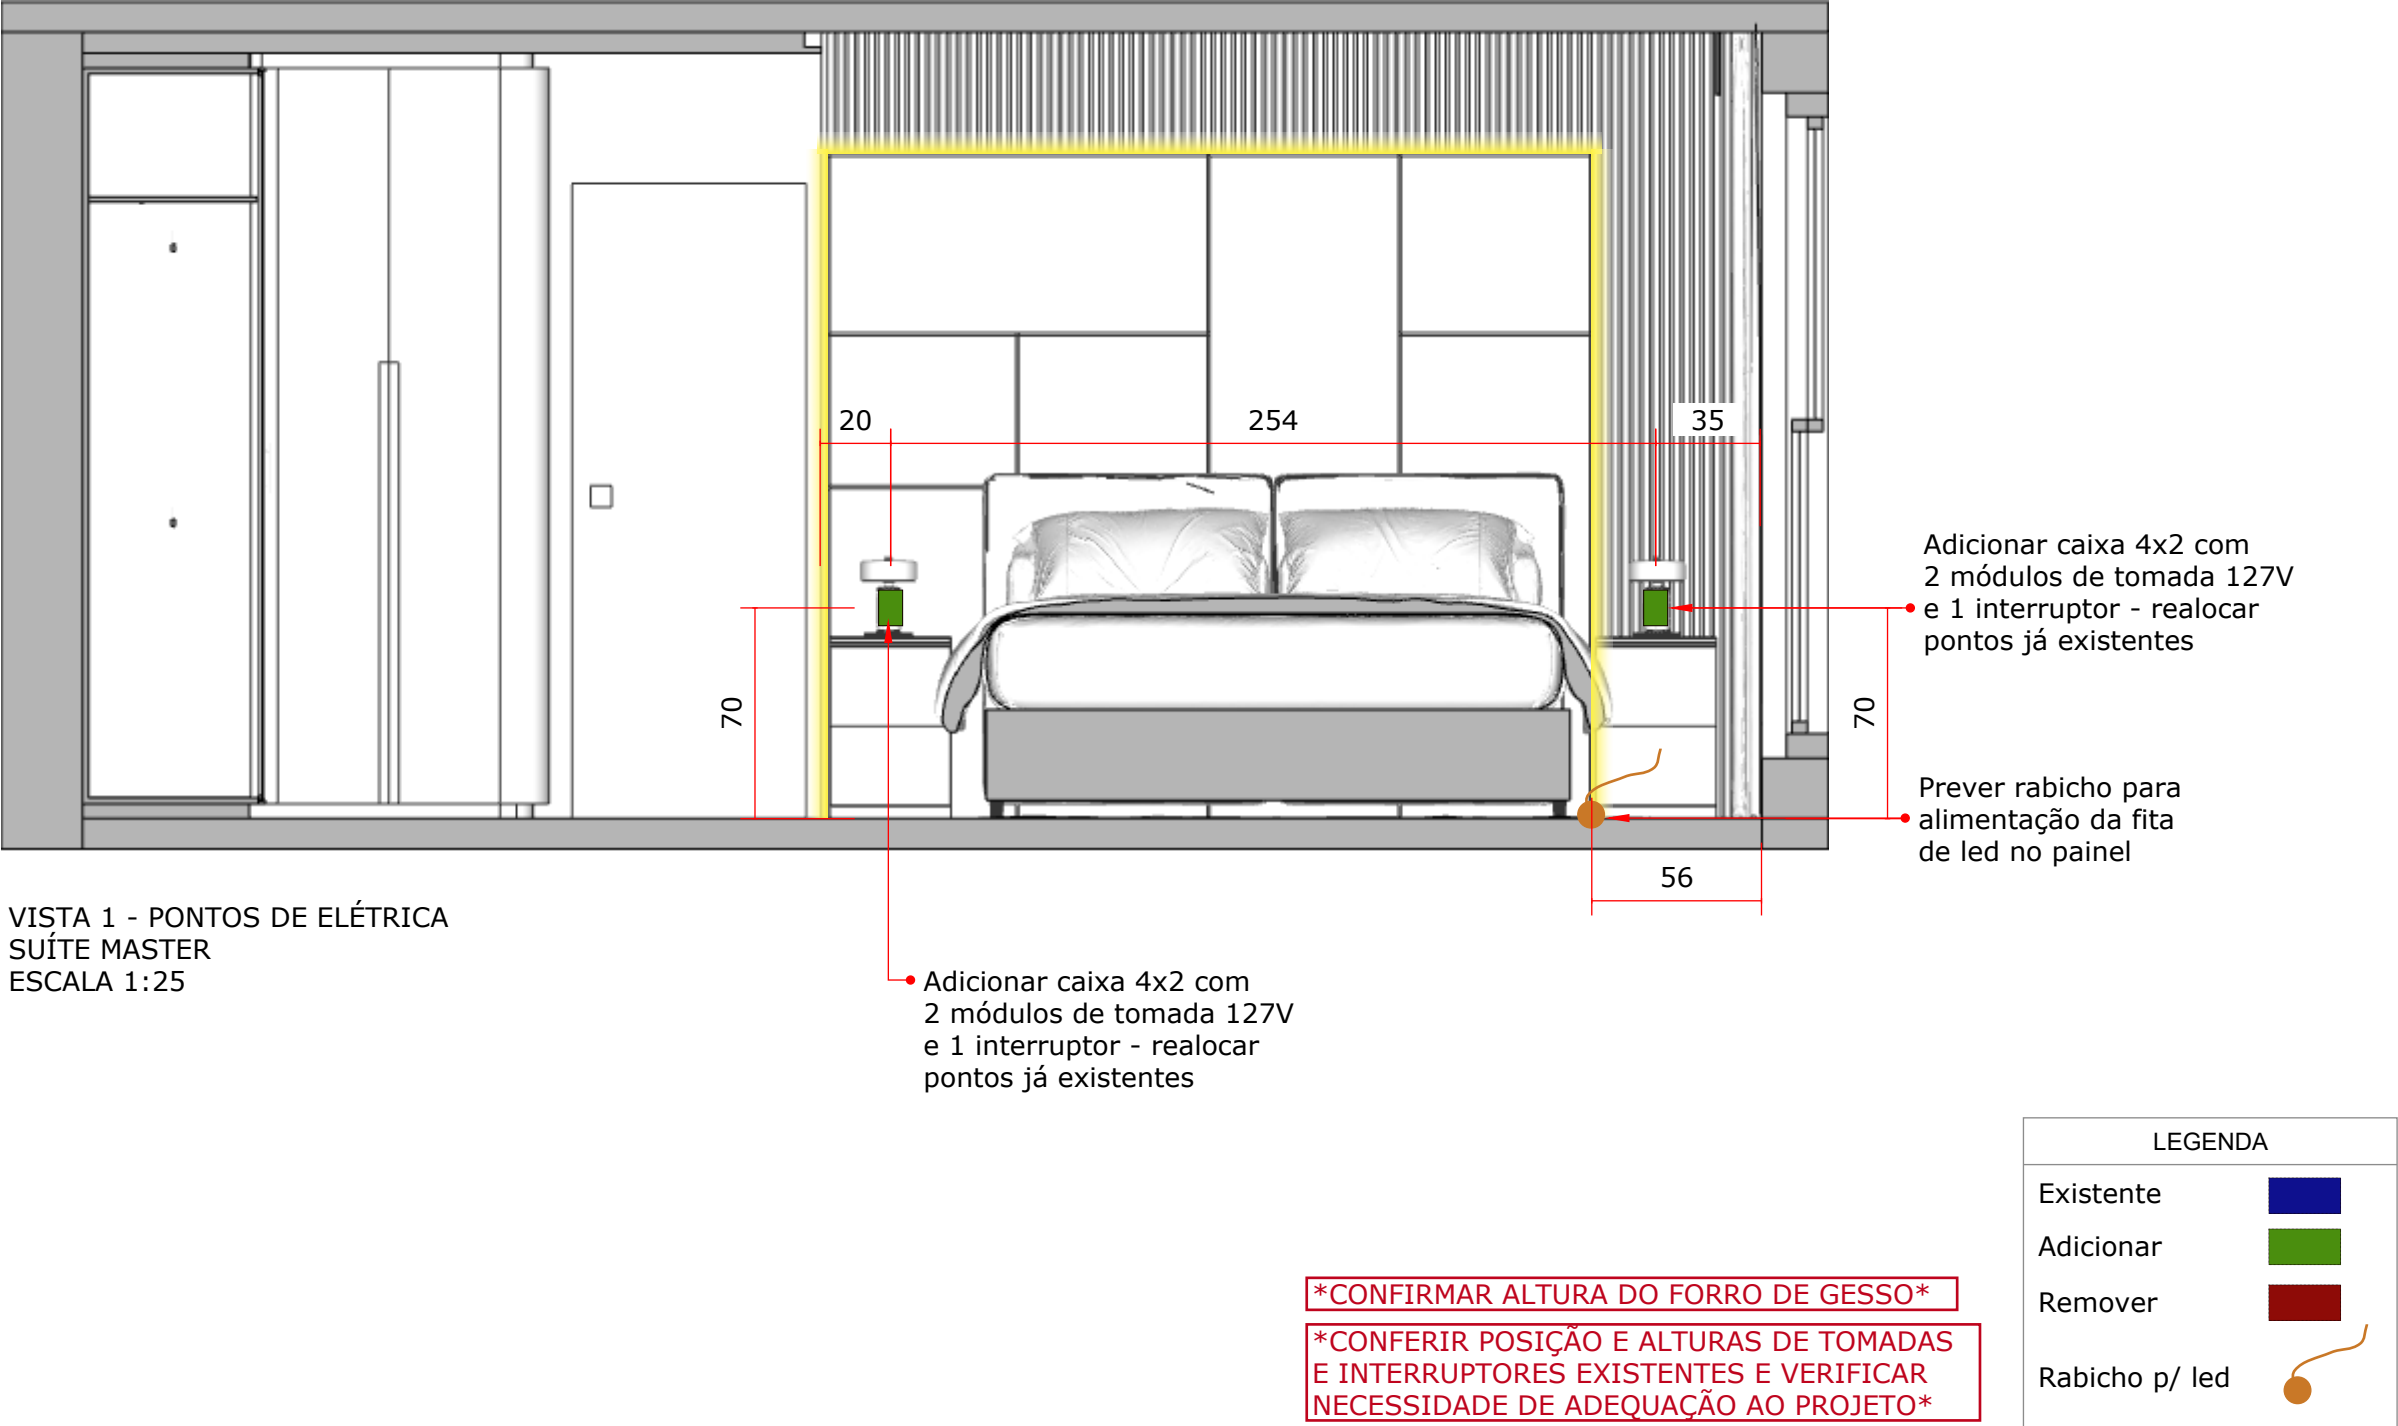

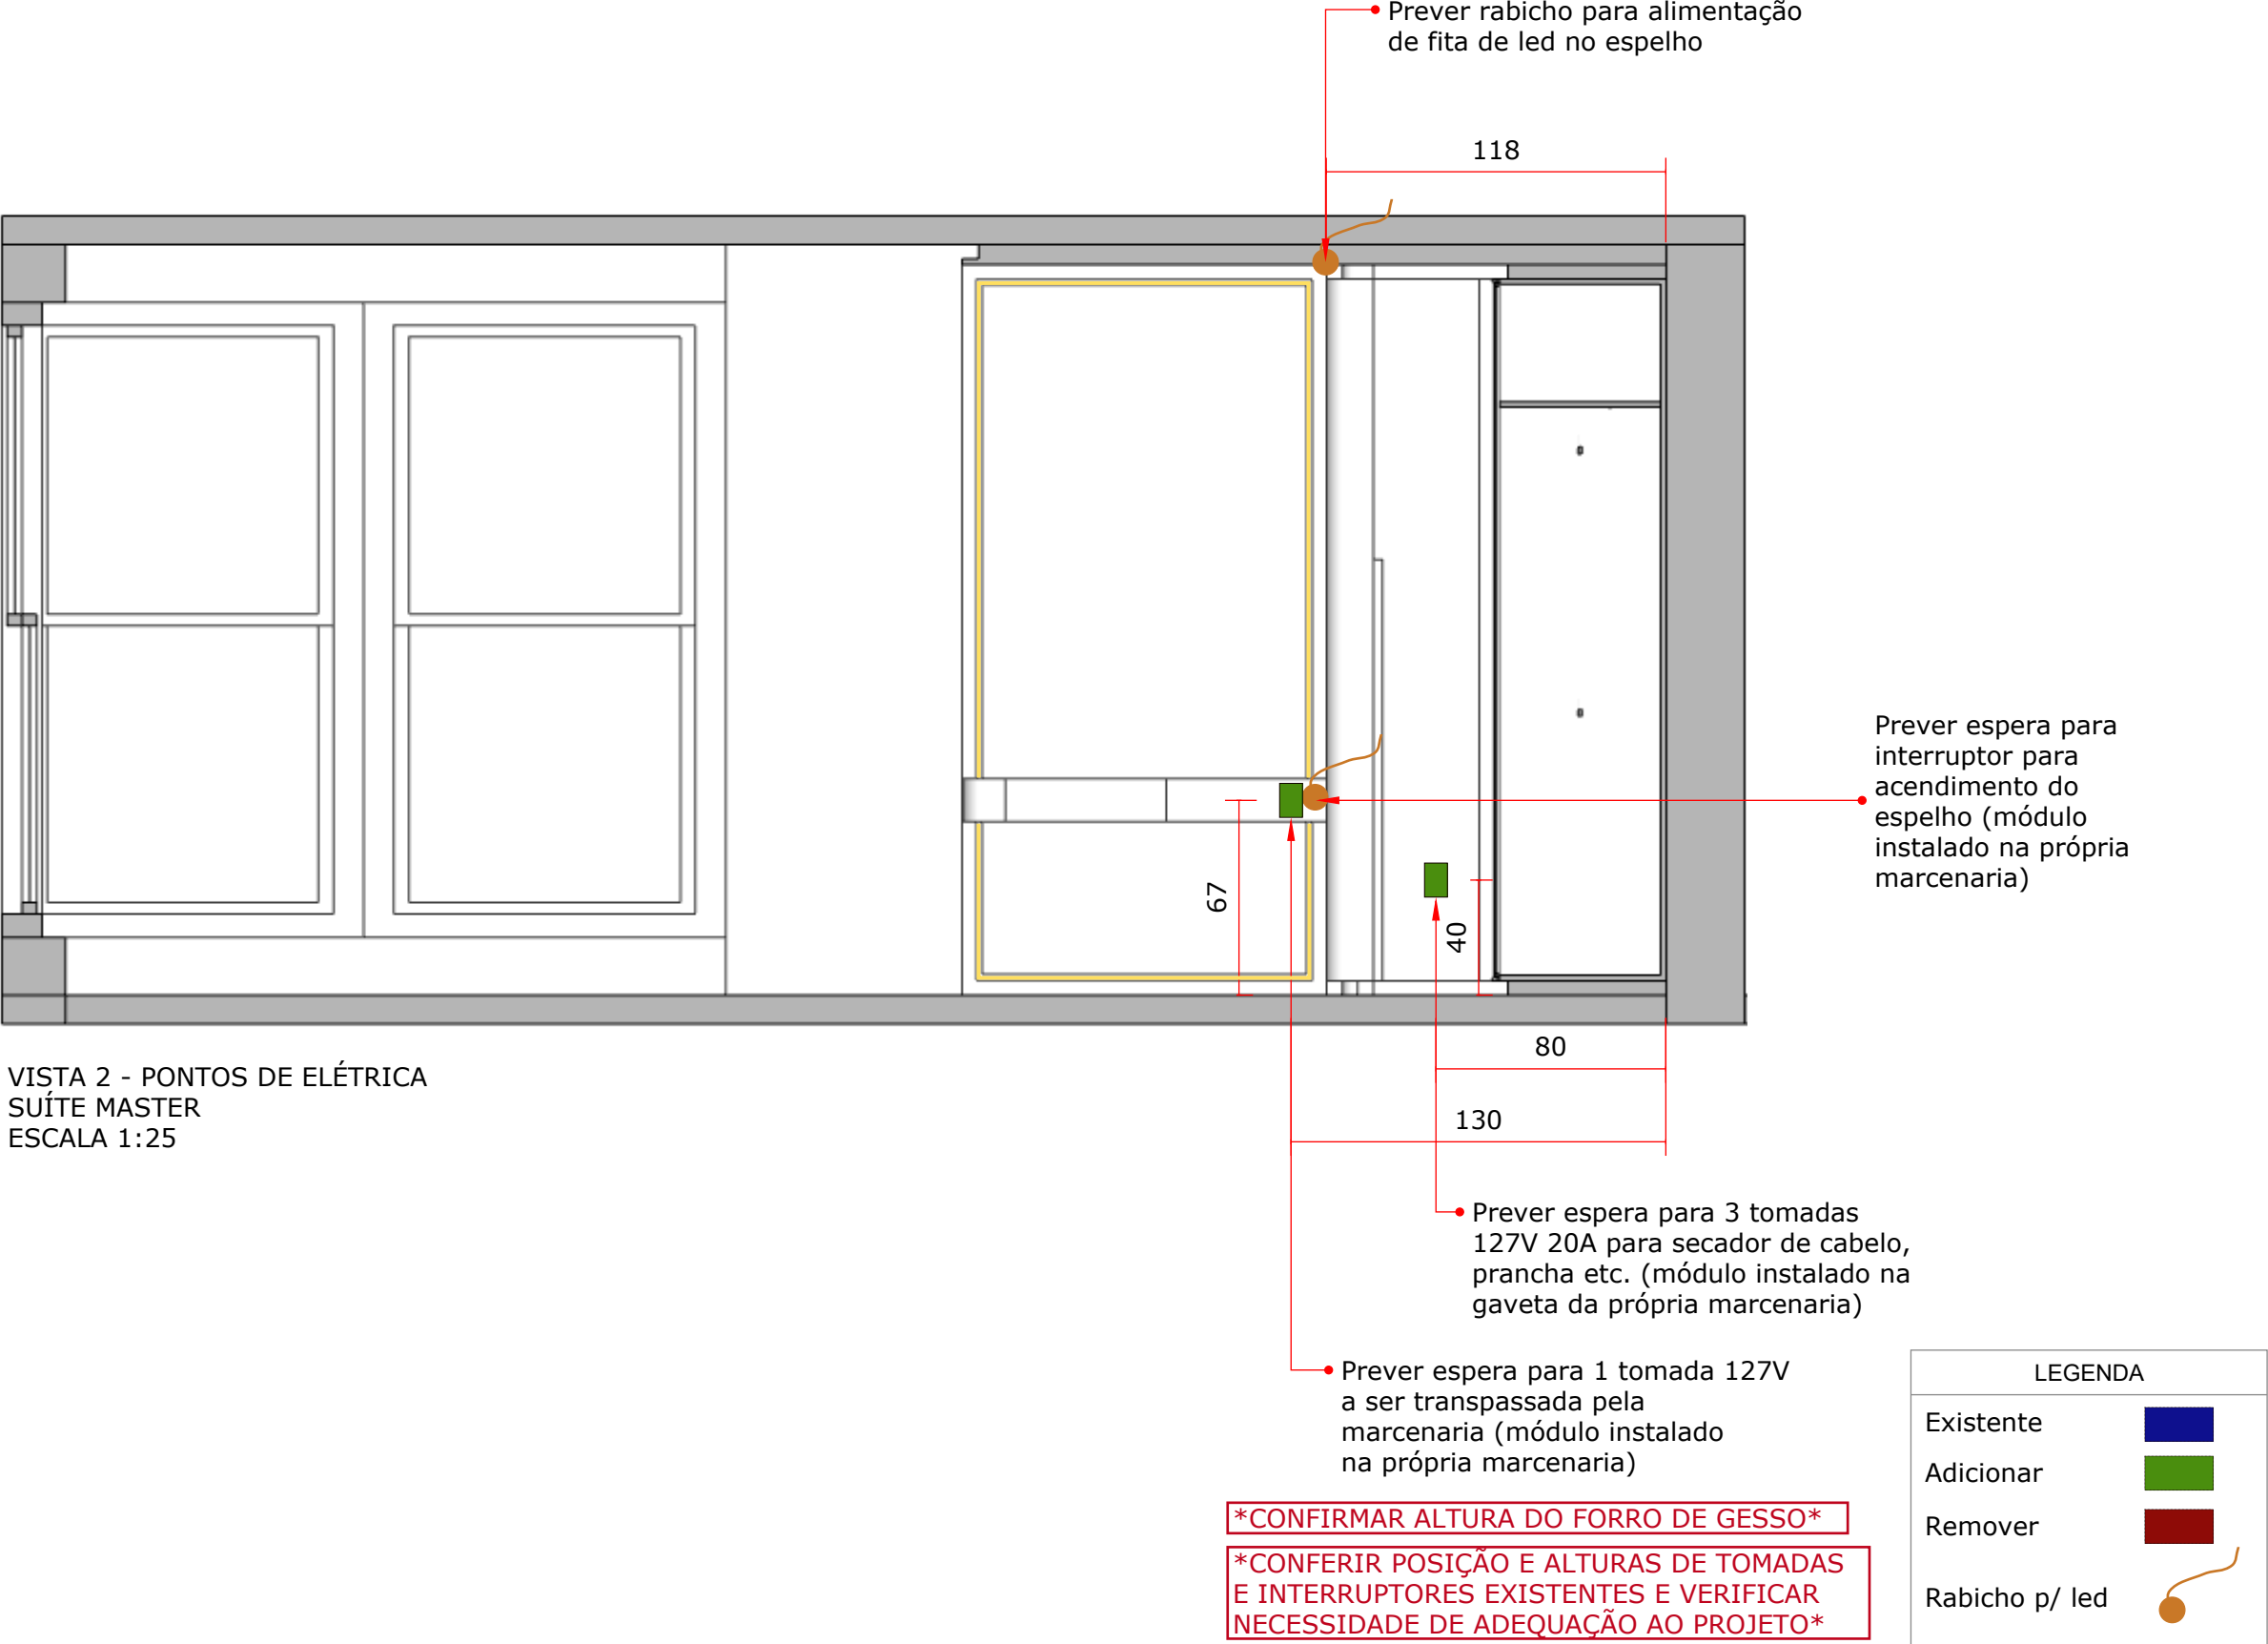

VISTA 2 - PONTOS DE ELÉTRICA
SUÍTE MASTER
ESCALA 1:25

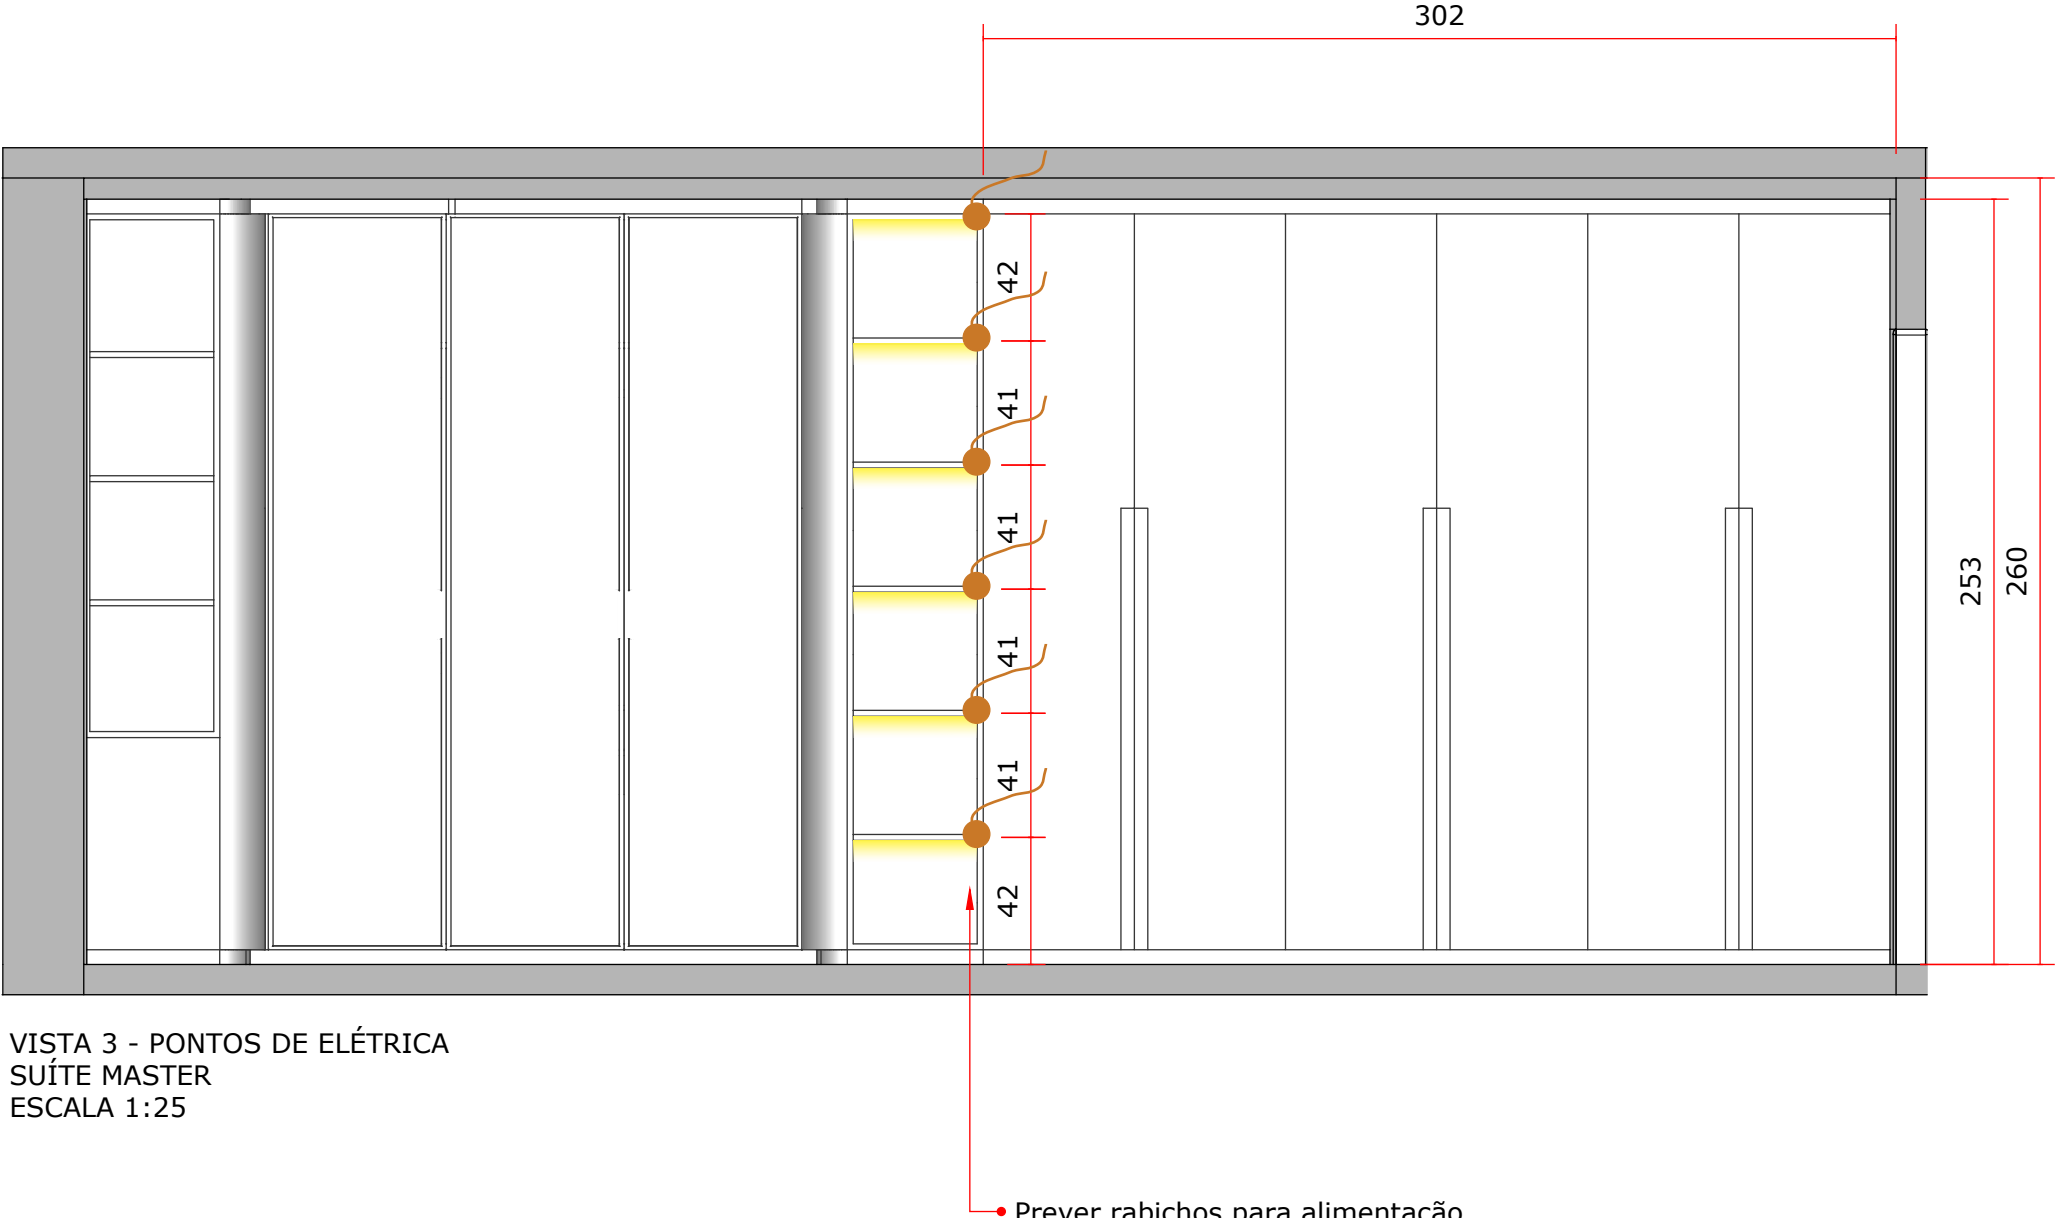

VISTA 3 - PONTOS DE ELÉTRICA
SUÍTE MASTER
ESCALA 1:25



• Prever rabichos para alimentação
de fitas de led na marcenaria

CONFIRMAR ALTURA DO FORRO DE GESSO

*CONFERIR POSIÇÃO E ALTURAS DE TOMADAS
E INTERRUPTORES EXISTENTES E VERIFICAR
NECESSIDADE DE ADEQUAÇÃO AO PROJETO*

LEGENDA	
Existente	
Adicionar	
Remover	
Rabicho p/ led	

	ESCALA 1:25	CONTEÚDO: PONTOS DE ELÉTRICA SUÍTE MASTER	RESPONSÁVEL: ARQUITETA BEATRIZ MASSI	FOLHA
		CLIENTE: ALEX E KARINE	DATA: 12/08/2025	15

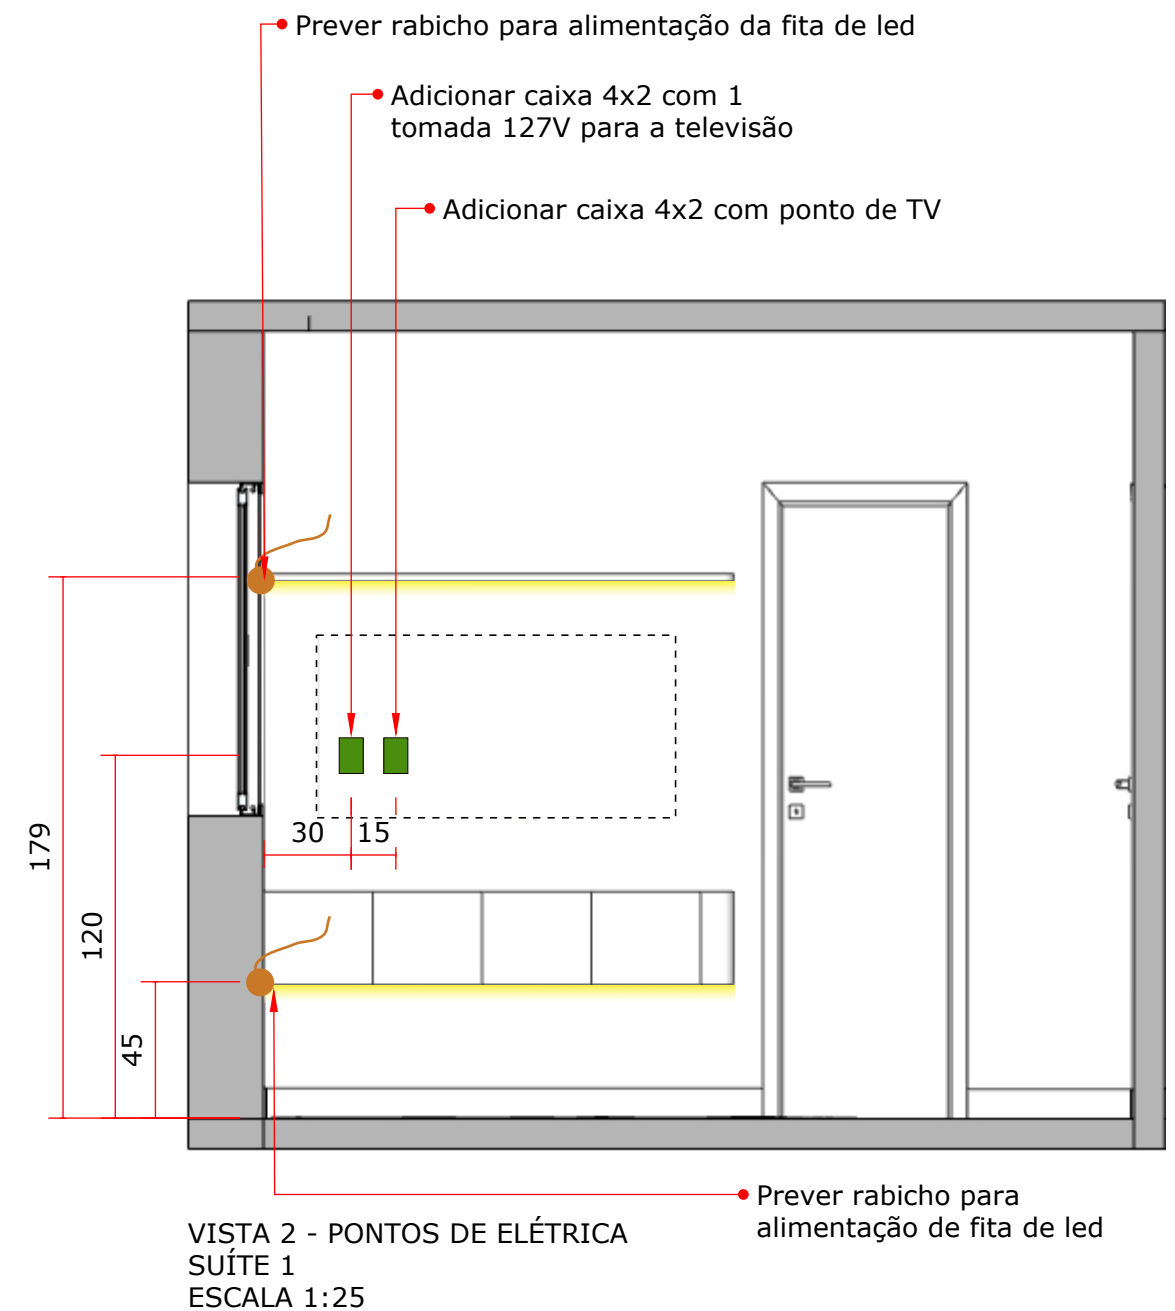
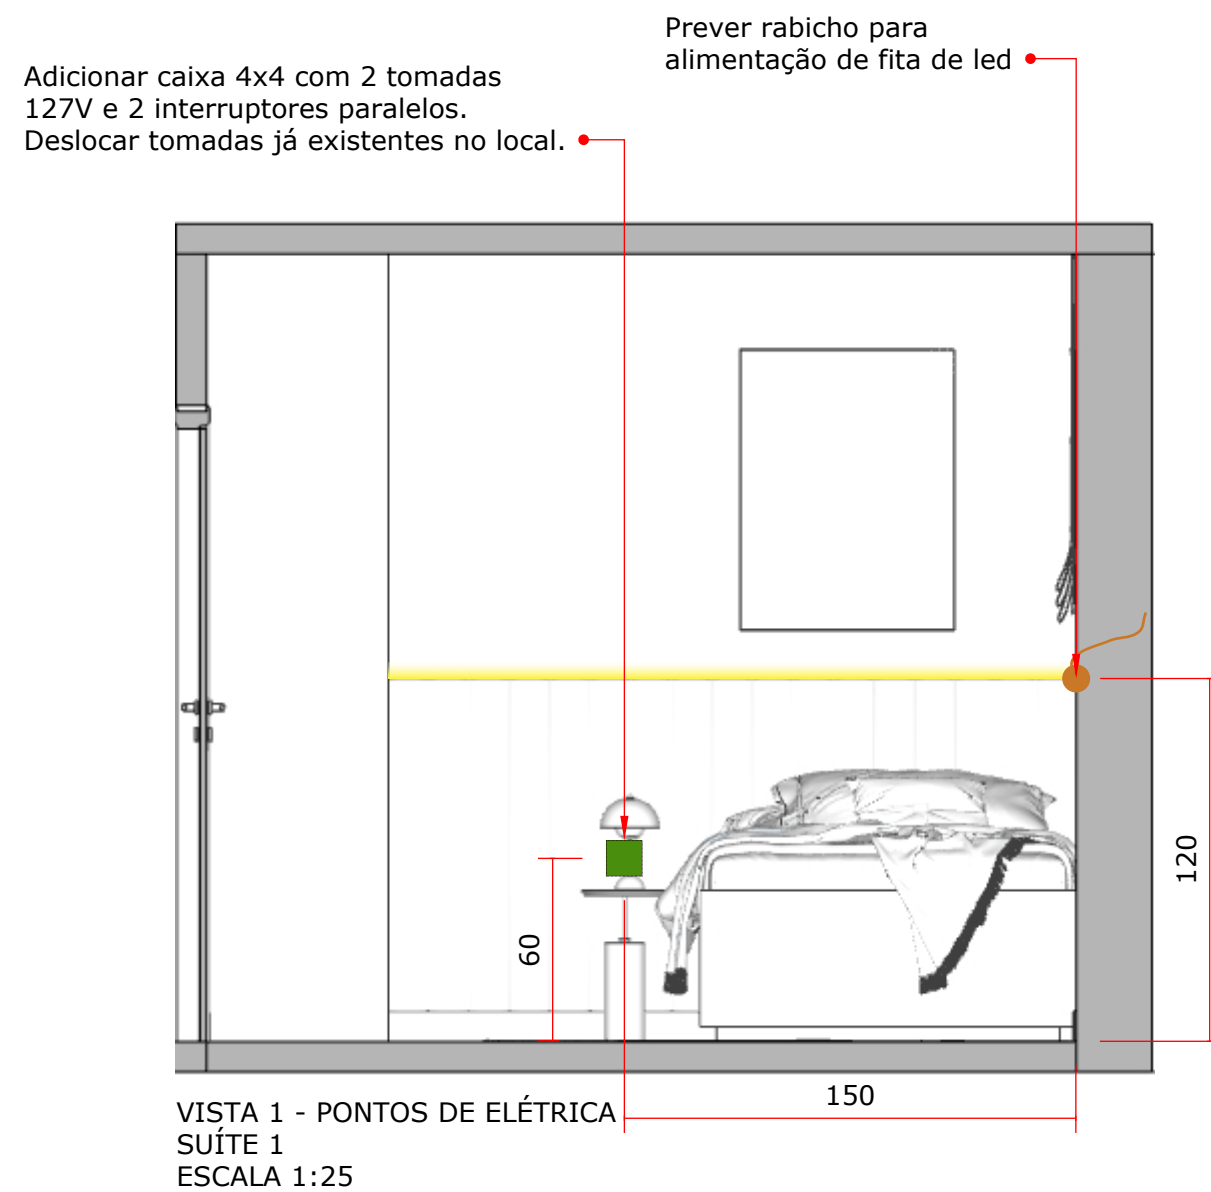


CONFIRMAR ALTURA DO FORRO DE GESSO

CONFERIR POSIÇÃO E ALTURAS DE TOMADAS E INTERRUPTORES EXISTENTES E VERIFICAR NECESSIDADE DE ADEQUAÇÃO AO PROJETO

LEGENDA	
Existente	
Adicionar	
Remover	
Rabicho p/ led	


	ESCALA 1:25	CONTEÚDO: PONTOS DE ELÉTRICA SUÍTE 1	RESPONSÁVEL: ARQUITETA BEATRIZ MASSI	FOLHA
		CLIENTE: ALEX E KARINE	DATA: 12/08/2025	16

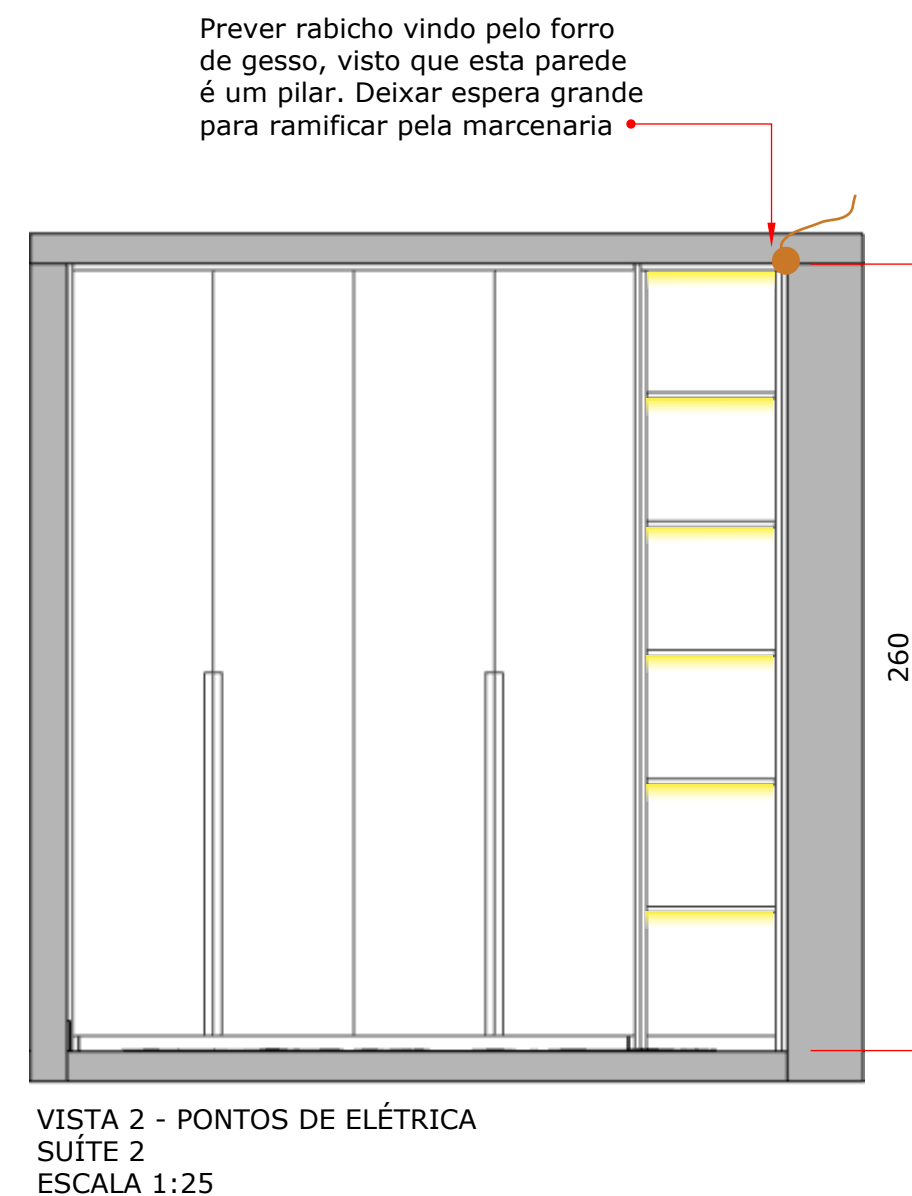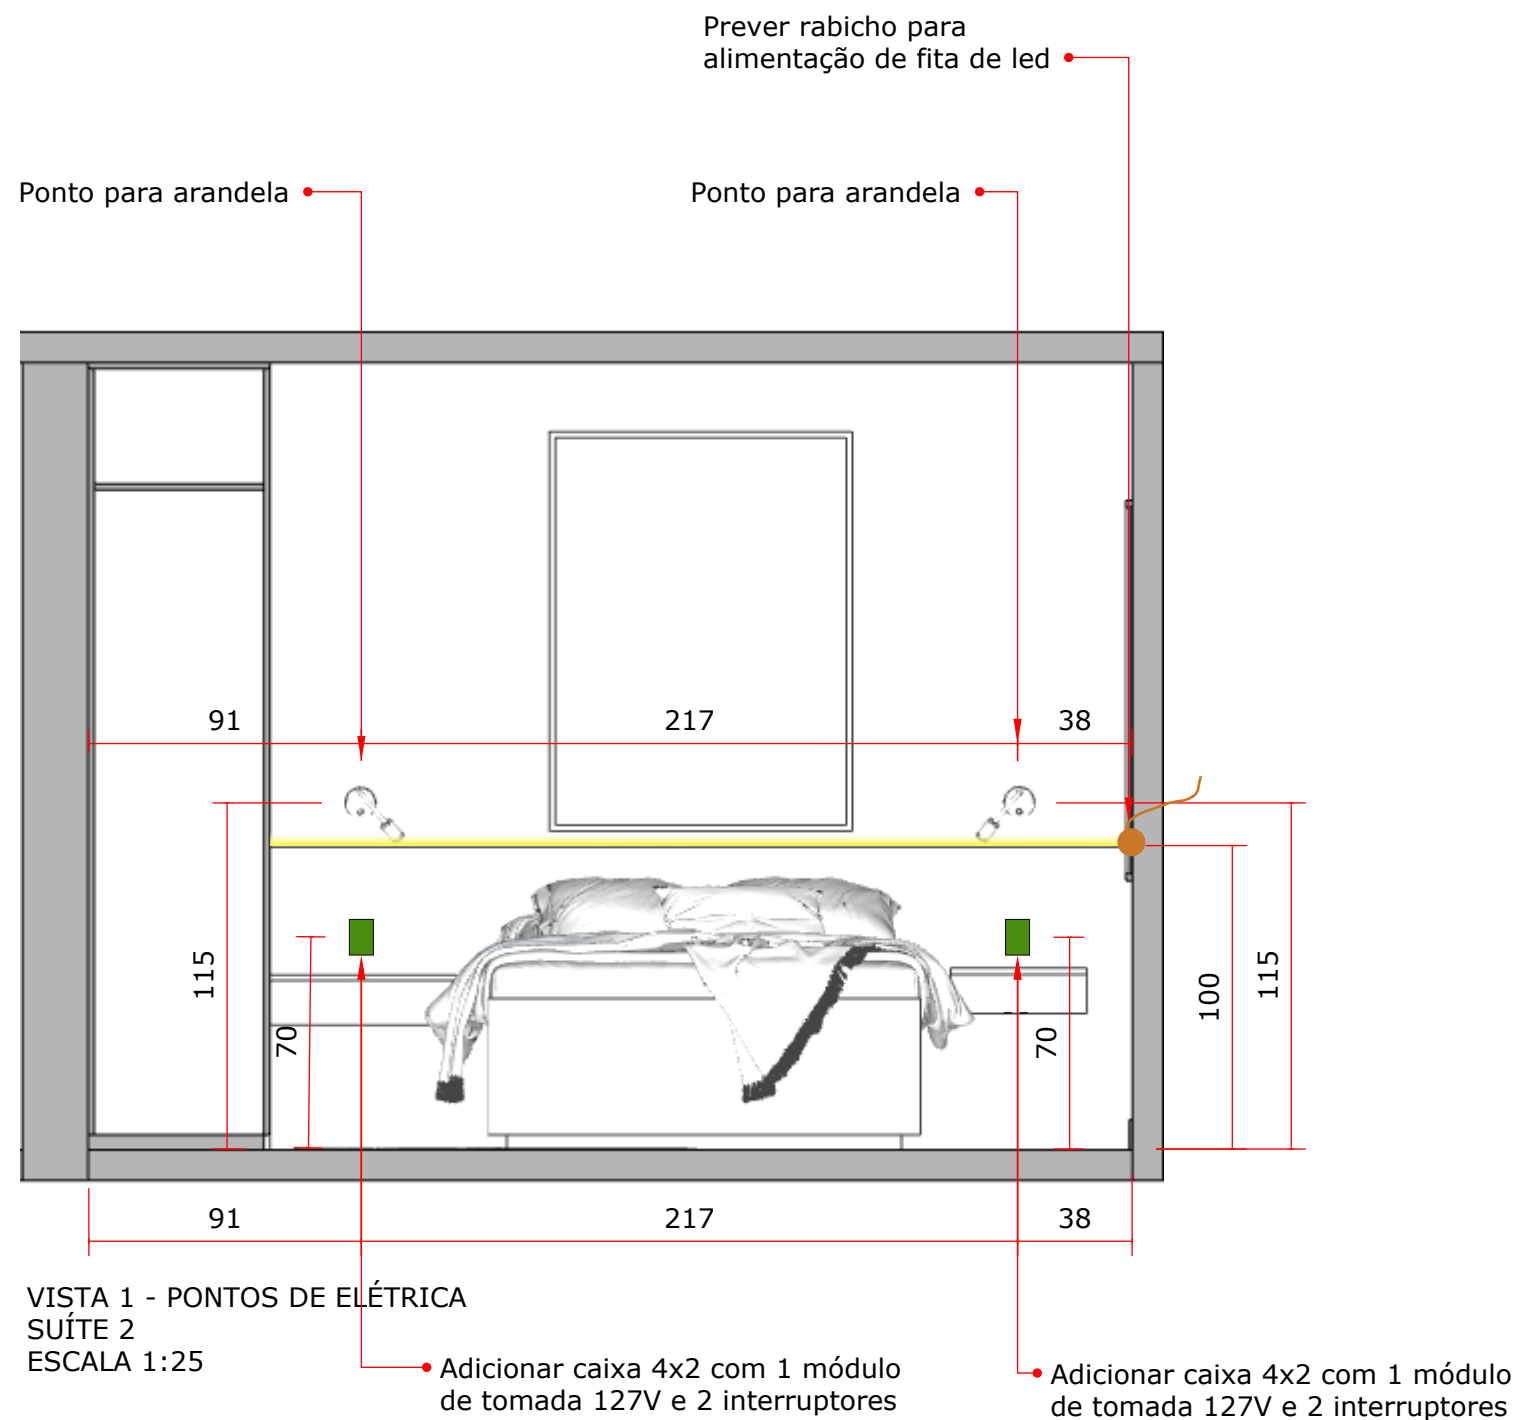

CONFIRMAR ALTURA DO FORRO DE GESSO

CONFERIR POSIÇÃO E ALTURAS DE TOMADAS E INTERRUPTORES EXISTENTES E VERIFICAR NECESSIDADE DE ADEQUAÇÃO AO PROJETO

LEGENDA	
Existente	
Adicionar	
Remover	
Rabicho p/ led	

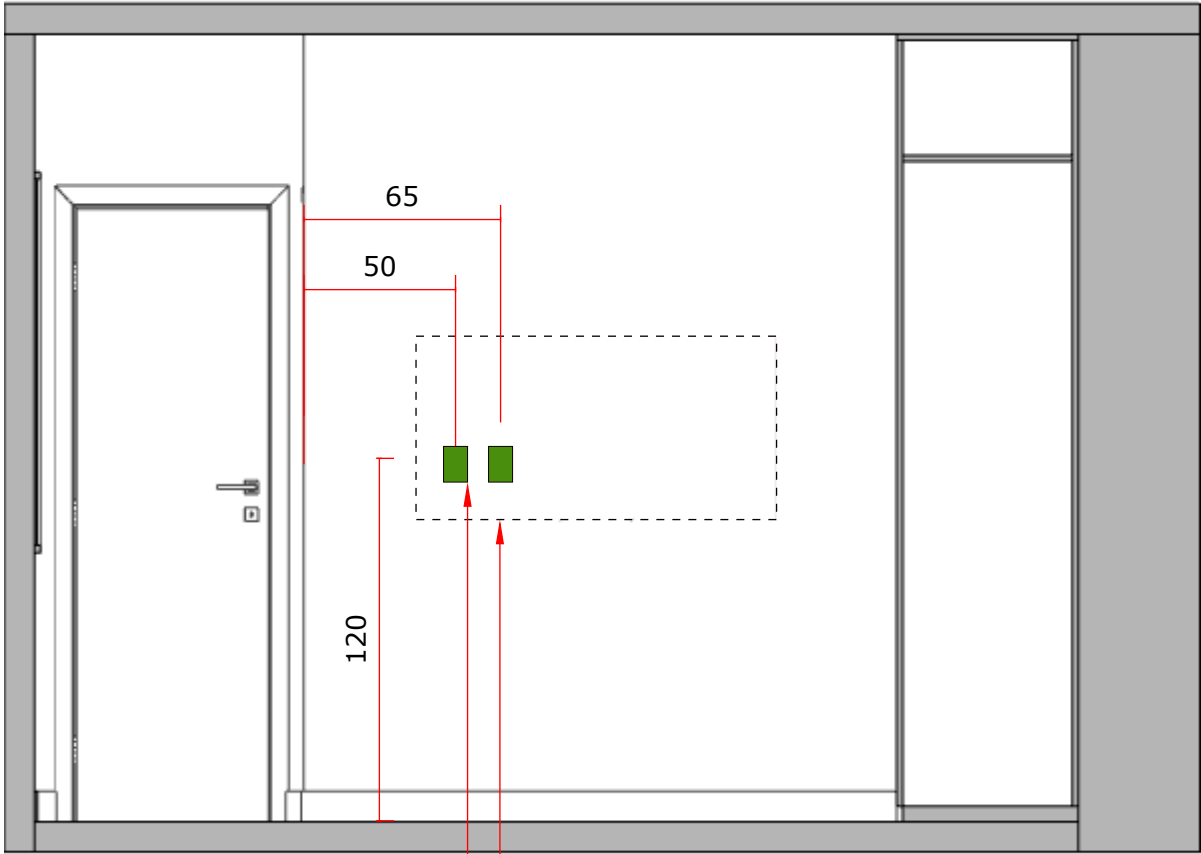

VISTA 3 - PONTOS DE ELÉTRICA
SUÍTE 2
ESCALA 1:25

- Adicionar ponto de antena
- Adicionar caixa 4x2 com 1 módulo de tomada 127V para a televisão

CONFIRMAR ALTURA DO FORRO DE GESSO

CONFERIR POSIÇÃO E ALTURAS DE TOMADAS E INTERRUPTORES EXISTENTES E VERIFICAR NECESSIDADE DE ADEQUAÇÃO AO PROJETO

LEGENDA	
Existente	
Adicionar	
Remover	
Rabicho p/ led	

	ESCALA 1:25	CONTEÚDO: PONTOS DE ELÉTRICA SUÍTE 2	RESPONSÁVEL: ARQUITETA BEATRIZ MASSI	FOLHA
		CLIENTE: ALEX E KARINE	DATA: 12/08/2025	18


Manter o piso existente em todos os ambientes; Fazer complemento nas áreas onde houver demolição de paredes.




PLANTA DE REVESTIMENTOS
ESCALA 1:75

LEGENDA DE ACABAMENTOS

SÍMBOLO	DESCRIÇÃO
P	PISO
P1	PISO EXISTENTE A SER MANTIDO
P2	PISO EXISTENTE A SER MANTIDO
P3	PISO EXISTENTE A SER MANTIDO
T	TETO
T1	PINTURA EM BRANCO NEVE FOSCO
T2	TETO COM ENVELOPAMENTO AMADEIRADO
▲	ACABAMENTO PAREDE
1	ENVELOPAMENTO AMADEIRADO
2	TINTA ACRILICA FOSCA PAPEL PICADO SUVINIL
3	PINTURA BRANCA EXISTENTE
4	PAINEL EM MDF AMADEIRADO
5	REVESTIMENTO EXISTENTE A SER MANTIDO
6	REVESTIMENTO TRAVERTINO SANTORINI
7	TINTA DECORA MATTE SOMBRA DA MONTANHA 90GY 16 / 151 CORAL
8	PAINEL EM MDF

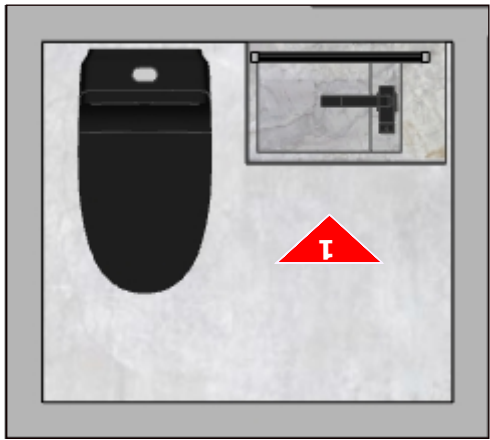

PLANTA DE LOCALIZAÇÃO - LAVABO
ESCALA 1:50

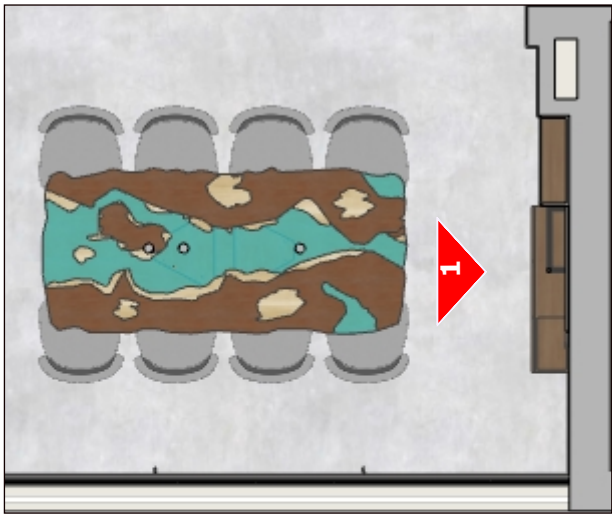


PLANTA DE LOCALIZAÇÃO - VARANDA
ESCALA 1:50



VISTA 1 - REVESTIMENTOS
LAVABO

Aplicação de revestimento Travertino
Santorini Natural - 2,65m²

Conferir capítulo de
envelopamento no
caderno de detalhes

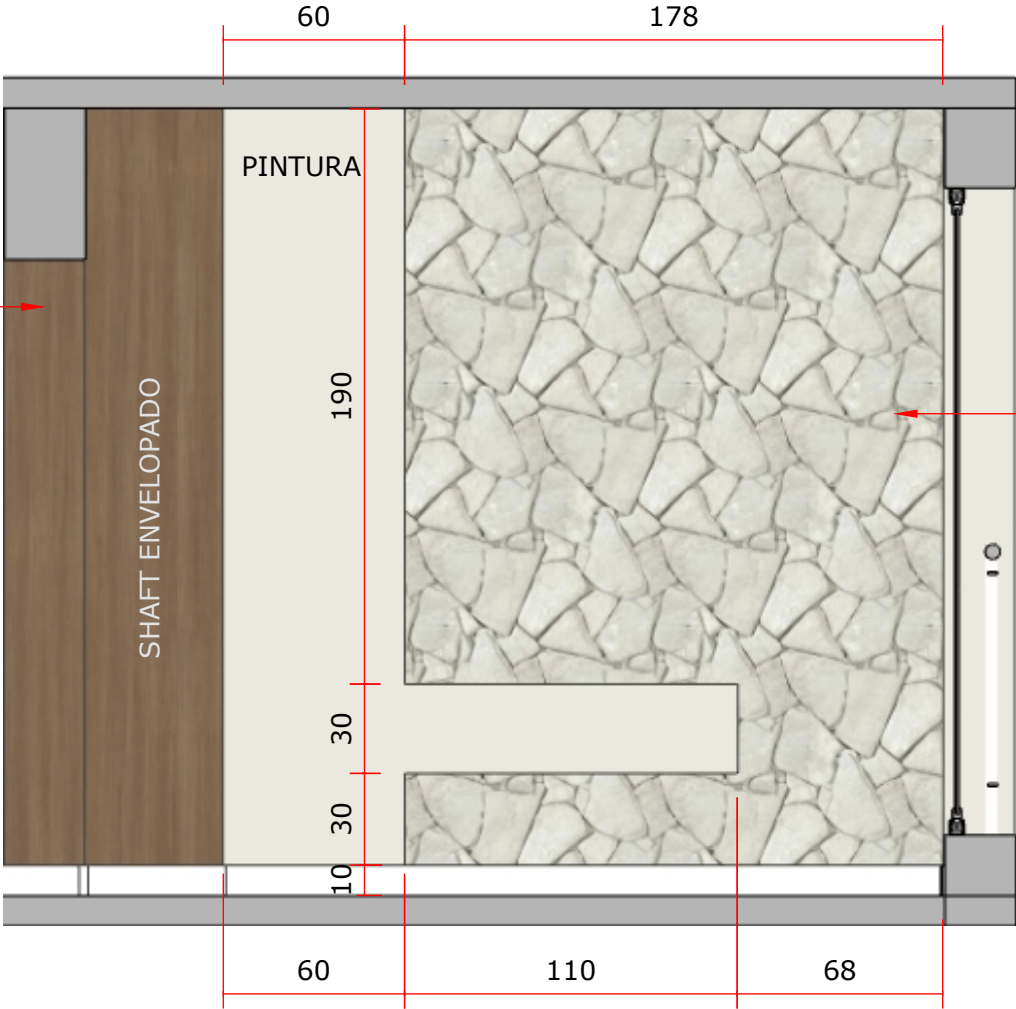

VISTA 1 - VARANDA
ESCALA 1:50

Aplicação de
revestimento Travertino
Santorini Natural - 4,15m²




PLANTA DE FORRO
COM ILUMINAÇÃO
ESCALA 1:75

LEGENDA FORRO

FG1	FORRO DE GESSO 10/15CM ABAIXO DO TETO - EXISTENTE A MANTER
FG2	COMPLEMENTO DE FORRO DE GESSO - SEGUIR ALTURA DO FORRO EXISTENTE
FG3	FORRO DE GESSO NOVO 10/15CM ABAIXO DO TETO - ENVELOPAMENTO AMADEIRADO
FG4	FORRO EM MDF INSTALADO SOBRE O FORRO DE GESSO EXISTENTE
BA	BANDÔ
	LED NO CORTINEIRO


SUGESTÃO: Caso não haja tabica nos forros já existentes, refazer o forro e considerar tabica de alumínio de 3cm.

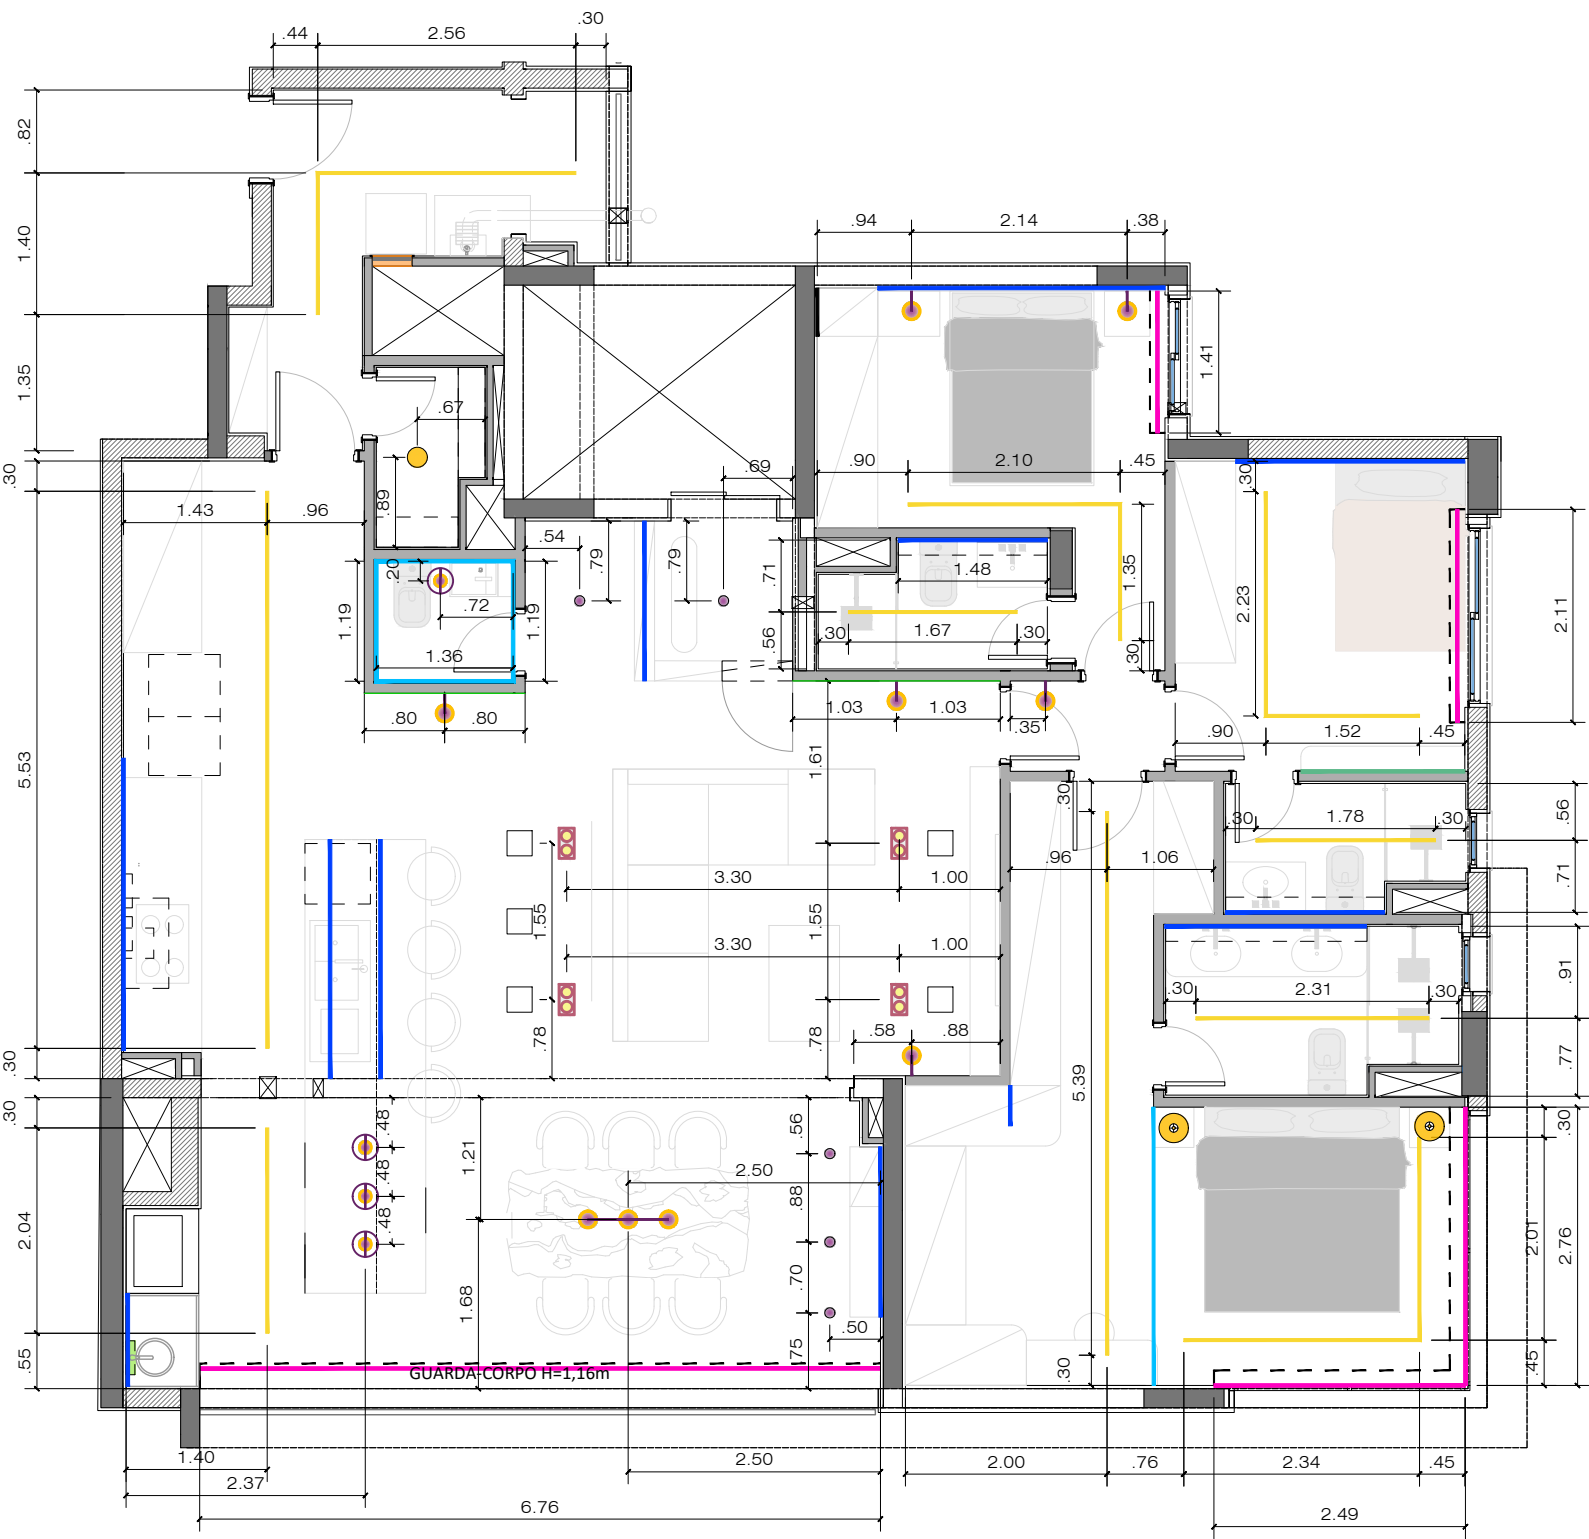

PLANTA DE ILUMINAÇÃO
ESCALA 1:75

LEGENDA ILUMINAÇÃO

SÍMBOLOS	DESCRIÇÃO	QUANT.	SÍMBOLOS	DESCRIÇÃO	QUANT.
HALL			CORREDOR		
	SPOT DE SOBREPOR PIPE 1 PAR20 12XØ7,5CM METAL PRETO - TKS PRELÚDIO 1057	1 UNIDADE		ARANDELA DE PAREDE PRETO LED 2700K 16,5W 110V 100X11X5CM METAL - OLD ARTISAN AR-5665 H INSTALAÇÃO= 1,20M	1 UNIDADE
	FITA DE LED DE EMBUTIR COB P/ MARCENARIA 900LM 3000K	16,15M	SUÍTE MASTER		
SALA				ABAJUR	2 UNIDADES
	SPOT DE EMBUTIR RECUADO DUPLO MINI DICOICA (L) 12,5CM X (P) 7CM X (A) 3,5CM TERMOPLÁSTICO PRETO - SAVE ENERGY SE-330.3128	4 UNIDADES		PERFIL DE LED DE EMBUTIR 2200LM 3000K	7,30M
	ARANDELA DE PAREDE DOT (A) 125CM X (L) 25CM X (P) 24,5CM MADEIRA IMBUÍ E METAL - ACCORD 4127 H INSTALAÇÃO= 1,20M	1 UNIDADE		FITA DE LED P/ CORTINEIRO 2200LM 3000K	5,25M
	ARANDELA DE PAREDE LED NANO LINEAR 3000K 3W BIVOLT (L) 40CM ALUMÍNIO - SPOTLINE 1168 / 40 H INSTALAÇÃO= 2,25M	2 UNIDADES		FITA DE LED P/ SANCAS 2200LM 3000K	2,80M
	SPOT DE SOBREPOR PIPE 1 PAR20 12XØ7,5CM METAL PRETO - TKS PRELÚDIO 1057	1 UNIDADE		FITA DE LED DE EMBUTIR COB P/ MARCENARIA 900LM 3000K	14,5M
	FITA DE LED DE EMBUTIR COB P/ MARCENARIA 900LM 3000K	17,45M	WC SUÍTE MASTER		
COZINHA				PERFIL DE LED DE EMBUTIR 2200LM 3000K	2,35M
	PERFIL DE LED DE EMBUTIR 2200LM 3000K	5,55M		FITA DE LED DE EMBUTIR COB P/ MARCENARIA 900LM 3000K	3,20M
	FITA DE LED DE EMBUTIR COB P/ MARCENARIA 900LM 3000K	7,90M	SUÍTE 1		
	PERFIL DE LED DE EMBUTIR COB P/ MARMORARIA 900LM 3000K	CONFERIR C/ FORNECEDOR		PERFIL DE LED DE EMBUTIR 2200LM 3000K	3,75M
VARANDA				FITA DE LED P/ CORTINEIRO 2200LM 3000K	2,15M
	PENDENTE ROCAILLE DISCO COBRE AVELÁ - VETTRO LUCCI	3 UNIDADES		FITA DE LED DE EMBUTIR COB P/ MARCENARIA 900LM 3000K	2,30M
	PENDENTE MOON RETANGULAR 120CM PRETO - CONCEPTU ILUMINAÇÃO	1 UNIDADE		FITA DE LED DE SOBREPOR COB P/ SERRALHERIA 900LM 3000K	1,65M
	SPOT DE SOBREPOR PIPE 1 PAR20 12XØ7,5CM METAL PRETO - TKS PRELÚDIO 1057	3 UNIDADES	WC SUÍTE 1		
	PERFIL DE LED DE EMBUTIR 2200LM 3000K	2,05M		PERFIL DE LED DE EMBUTIR 2200LM 3000K	1,80M
	FITA DE LED P/ CORTINEIRO 2200LM 3000K	6,80M		FITA DE LED DE EMBUTIR COB P/ MARCENARIA 900LM 3000K	2,55M
	FITA DE LED DE EMBUTIR COB P/ MARCENARIA 900LM 3000K	3,95M	SUÍTE 1		
LAVABO				ARANDELA DE PAREDE LED MAMBA ARTICULÁVEL 3000K 3W BIVOLT ØØX25CM ALUMÍNIO PRETO - OPUS OPS 38834 H INSTALAÇÃO 1,15M	2 UNIDADES
	PENDENTE PÊNDULO DUPLO PRETO (A) 134CM X (L) 27CM X (P) 12CM ALUMÍNIO E VIDRO - USINA 16496/134	1 UNIDADE		PERFIL DE LED DE EMBUTIR 2200LM 3000K	3,35M
	FITA DE LED P/ SANCAS 2200LM 3000K	5,10M		FITA DE LED P/ CORTINEIRO 2200LM 3000K	1,45M
ESPAÇO PET				FITA DE LED DE EMBUTIR COB P/ MARCENARIA 900LM 3000K	4,90M
	PLAFON DE SOBREPOR LED REDONDO 3000K 18W BIVOLT Ø21X2,8CM ALUMÍNIO BRANCO - PIX ILUMINAÇÃO 36504301	1 UNIDADE	ÁREA DE SERVIÇO		
ÁREA DE SERVIÇO				PERFIL DE LED DE EMBUTIR 2200LM 3000K	3M

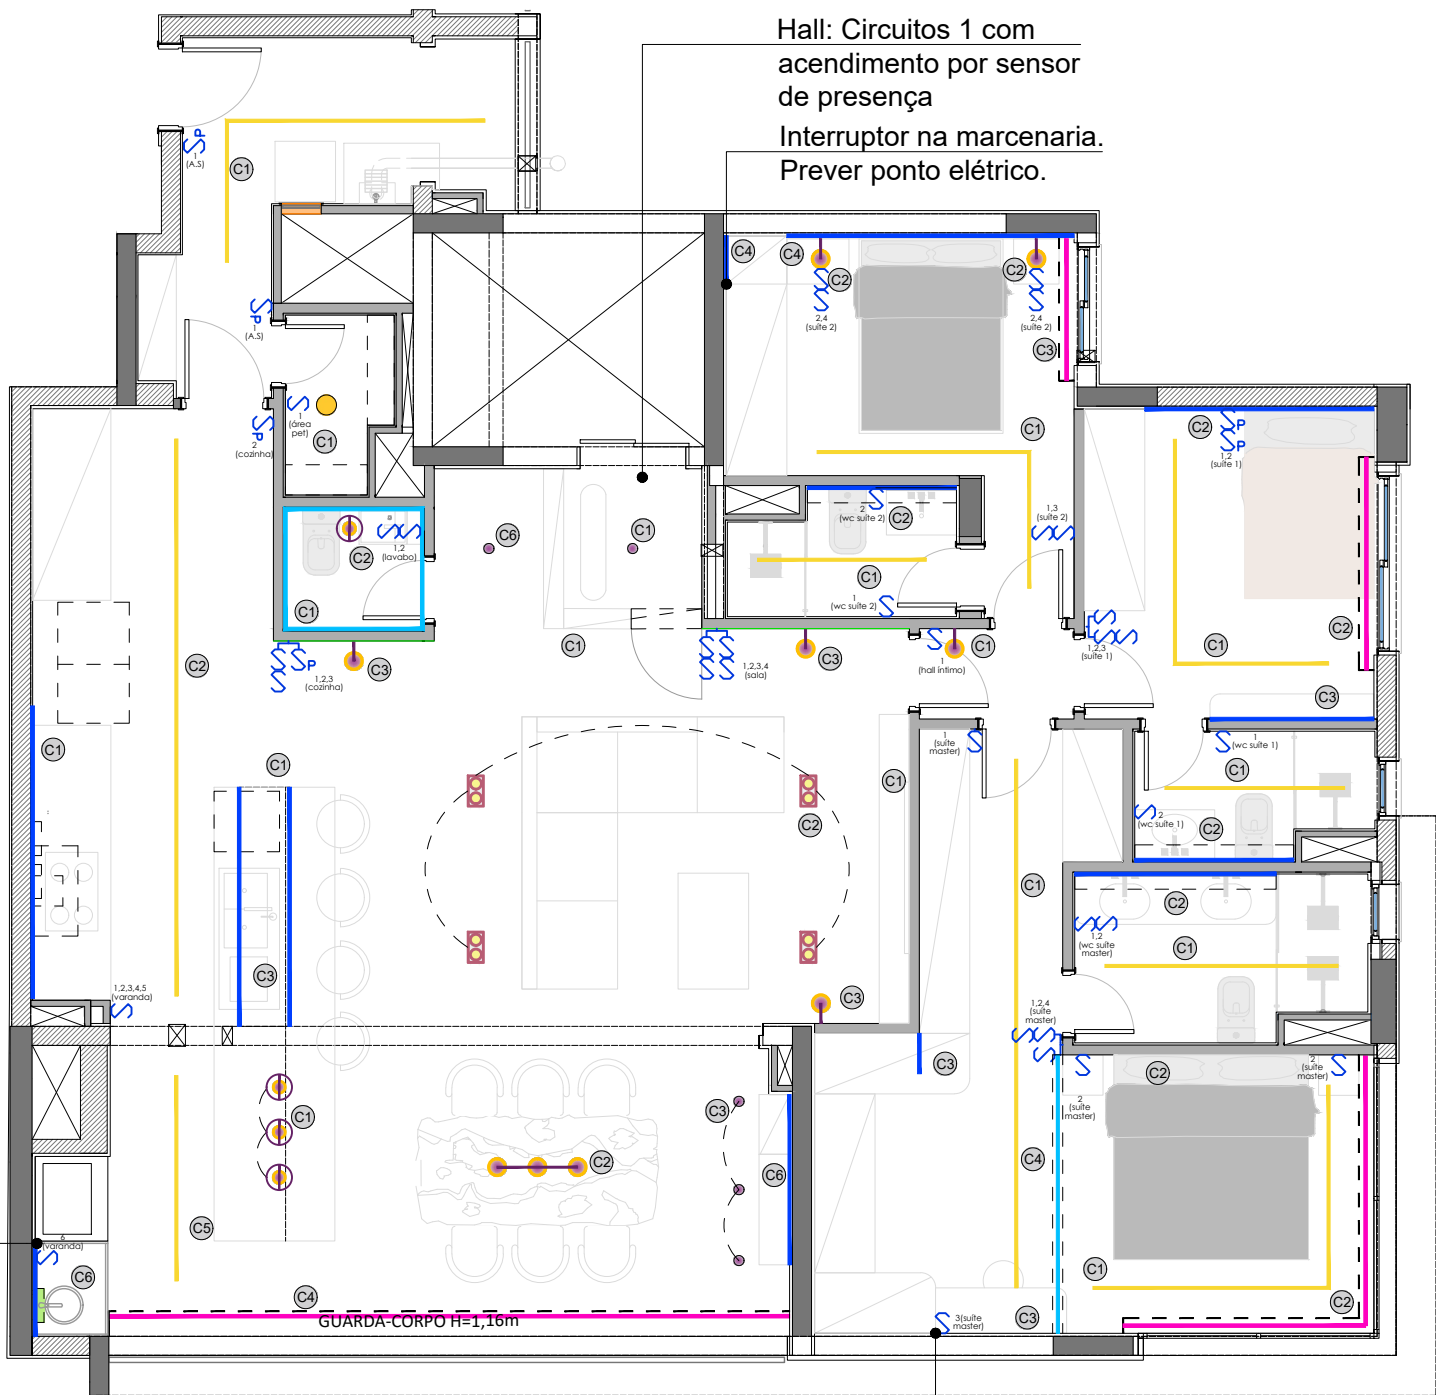

PLANTA DE ILUMINAÇÃO
ESCALA 1:75

Interruptor na marcenaria.
Prever ponto elétrico
vindo pelo forro de gesso.

Hall: Circuitos 1 com
acendimento por sensor
de presença
Interruptor na marcenaria.
Prever ponto elétrico.

Interruptor na marcenaria.
Prever ponto elétrico

LEGENDA DE CIRCUITOS


SÍMBOLOS	HALL
C1	CIRCUITO 1: LED NO ESPELHO, SPOT CILÍNDRICO E LED NA MARCENARIA
SALA DE ESTAR	
C1	CIRCUITO 1: LED NA MARCENARIA
C2	CIRCUITO 2: SPOT DUPLO MINI DICRÓICA
C3	CIRCUITO 3: ARANDELAS
C4	CIRCUITO 4: SPOT CILÍNDRICO
COZINHA	
C1	CIRCUITO 1: LED NA MARCENARIA
C2	CIRCUITO 2: PERFIL DE LED NO FORRO
C3	CIRCUITO 3: LED NA BANCADA EM ÔNIX
VARANDA	
C1	CIRCUITO 1: PENDENTES
C2	CIRCUITO 2: PENDENTE
C3	CIRCUITO 3: SPOTS CILÍNDRICOS
C4	CIRCUITO 4: LED NO CORTINEIRO (BANDÓ)
C5	CIRCUITO 5: PERFIL DE LED NO FORRO
C6	CIRCUITO 6: PERFIL DE LED NA MARCENARIA + ESPELHO
LAVABO	
C1	CIRCUITO 1: LED NA TABICA
C2	CIRCUITO 2: PENDENTE
ESPAÇO PET	
C1	CIRCUITO 1: PLAFON DE EMBUTIR
ÁREA DE SERVIÇO	
C1	CIRCUITO 1: PERFIL DE LED NO FORRO

SÍMBOLOS	HALL ÍNTIMO
C1	CIRCUITO 1: ARANDELA
SUÍTE MASTER	
C1	CIRCUITO 1: PERFIL DE LED NO FORRO
C2	CIRCUITO 2: LED NO CORTINEIRO (BANDÓ) + LED NO PAINEL EM MARCENARIA
C3	CIRCUITO 3: LED NO ESPELHO + NICHOS GUARDA ROUPA
C4	CIRCUITO 4: PERFIL DE LED NA SANCA
WC MASTER	
C1	CIRCUITO 1: PERFIL DE LED NO FORRO
C2	CIRCUITO 2: LED NA MARCENARIA
SUÍTE 1	
C1	CIRCUITO 1: PERFIL DE LED NO FORRO
C2	CIRCUITO 2: LED NA MARCENARIA + CORTINEIRO (BANDÓ)
C3	CIRCUITO 3: LED NA PRATELEIRA
WC SUÍTE 1	
C1	CIRCUITO 1: PERFIL DE LED NO FORRO
C2	CIRCUITO 2: LED NA MARCENARIA
SUÍTE 2	
C1	CIRCUITO 1: PERFIL DE LED NO FORRO
C2	CIRCUITO 2: ARANDELAS
C3	CIRCUITO 3: LED NO CORTINEIRO (BANDÓ)
C4	CIRCUITO 4: LED NA MARCENARIA + CABECEIRA
WC SUÍTE 2	
C1	CIRCUITO 1: PERFIL DE LED NO FORRO
C2	CIRCUITO 2: LED NA MARCENARIA

LEGENDA

SIMBOLOS	DESCRIÇÃO
	EVAPORADORA HI WALL
	EVAPORADORA CASSETE

Prever dreno para ar condicionado. Conferir posicionamentos das máquinas.

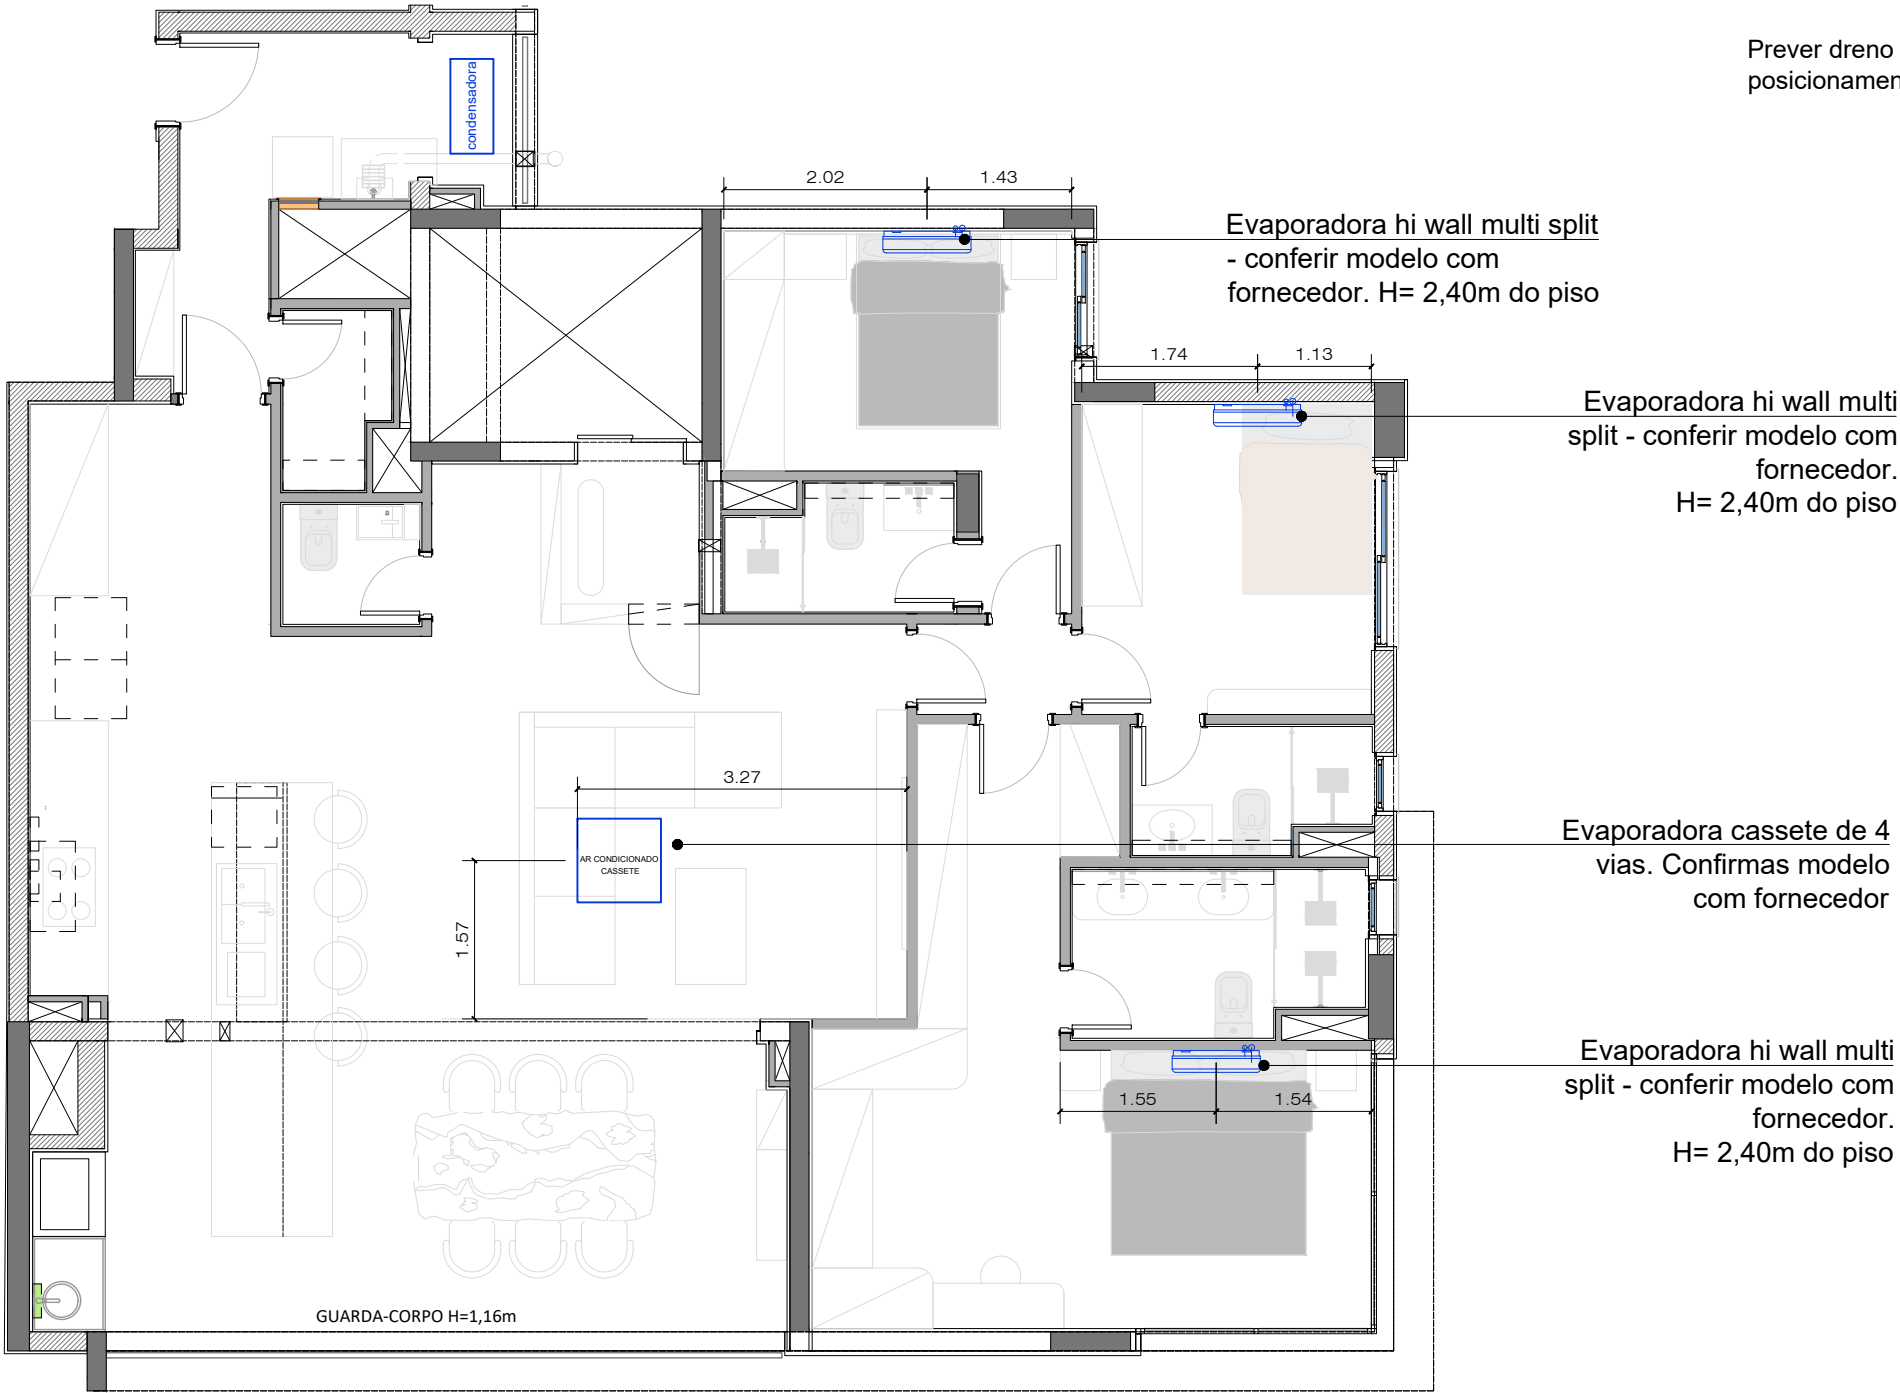

PLANTA DE AR CONDICIONADO
ESCALA 1:75



ESCALA
1:75

CONTEÚDO: AR CONDICIONADO

CLIENTE: ALEX E KARINE

RESPONSÁVEL: ARQUITETA BEATRIZ MASSI

DATA: 12/08/2025

FOLHA

25