




PLANTA SITUAÇÃO EXISTENTE

esc. 1:25

OBS: CONFERIR AS MEDIDAS NO LOCAL

REMOVER PISO E RODAPÉ

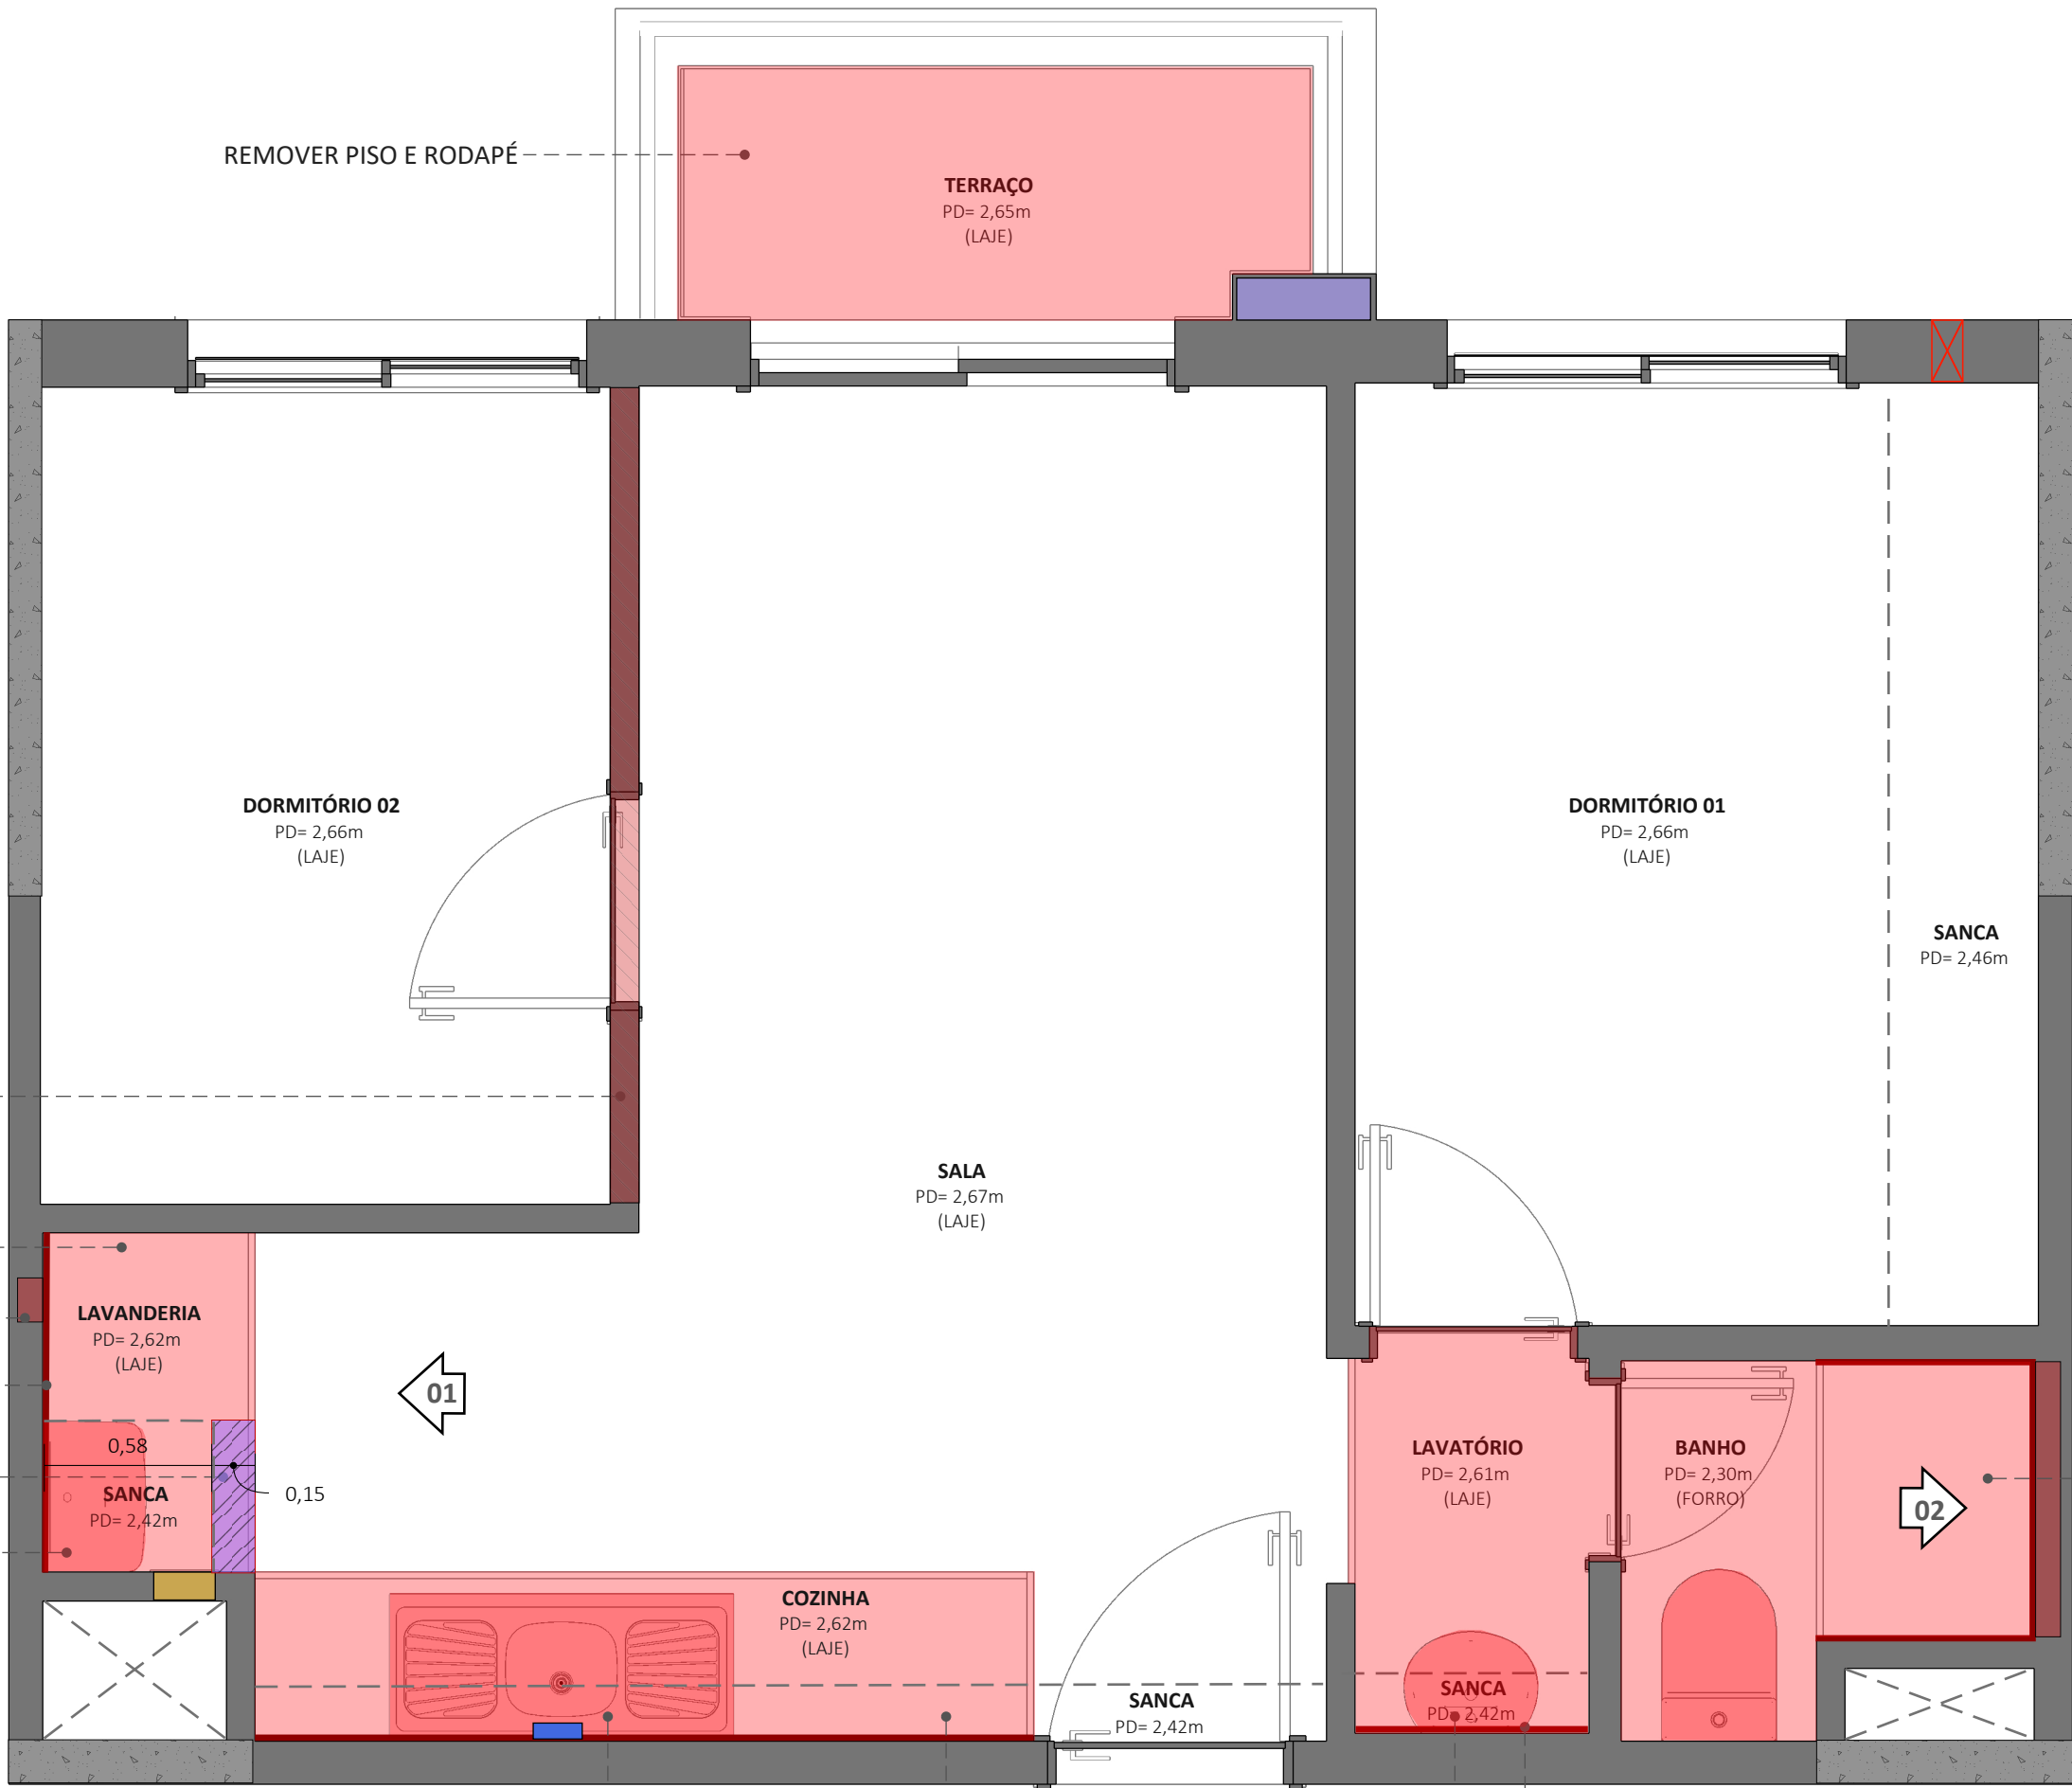

PLANTA DEMOLIR

esc. 1:25

OBS: CONFERIR AS MEDIDAS NO LOCAL


BANHEIRO:
- REMOVER BACIA SANITÁRIA;
- REMOVER PISO, BAGUETE E RODAPÉ;
- REMOVER REVESTIMENTO;
- REMOVER REGISTROS DO CHUVEIRO;
- ABERTURA DE VÃO PARA NICHOS - VER VISTA 02
(SE APROVADO PELO CONDOMÍNIO)
- **MANTER** FORRO DE GESSO;

LEGENDA ALVENARIA ORIGINAL	
	ALVENARIA DE VEDAÇÃO
	ALVENARIA ESTRUTURAL
	PISO EXISTENTE
	CARENAGEM PARA PONTOS DE ÁGUA FRIA E ESGOTO
	RALO EXISTENTE
	GÁS
	PONTO DE DRENO NA PAREDE EXISTENTE
	EXAUSTÃO MECÂNICA
	FURO NA VIGA / PAREDE
	TUBULAÇÃO EXAUSTÃO MECÂNICA
	ENCHIMENTO
	VENTILAÇÃO PERMANENTE
	BAGUETE EXISTENTE

LEGENDA DEMOLIR	
	REMOVER BANCADA/LOUÇA/METAL
	DEMOLIR REVESTIMENTO DE PAREDE
	DEMOLIR PISO, RODAPÉ E BAGUETE
	DEMOLIR PORTA/PAREDE

RESUMO DE DEMOLIÇÕES	
ITEM	QUANTIDADE
DEMOLIÇÃO DE PISO + RODAPÉ	COZINHA: 1,60M² LAVANDERIA: 0,88M² LAVATÓRIO: 1,25M² BANHEIRO: 1,64M² TERRAÇO: 1,91M²
DEMOLIÇÃO DE REVESTIMENTO PAREDE	COZINHA: 6,58M² LAVANDERIA: 3,08M² LAVATÓRIO: 1,23M² BANHEIRO: 5,75M²
REMOÇÃO DE PORTAS	1 unid. - ENTRE SALA E DORMITÓRIO 01
DEMOLIR PAREDES	PAREDE ENTRE SALA E DORMITÓRIO 01
REMOVER BANCADA/ TANQUE + CUBA E TORNEIRA + BACIA SANITÁRIA	1 unid.- COZINHA 1 unid. - LAVANDERIA 1 unid. -LAVATÓRIO 1 unid. -BANHEIRO


ATENÇÃO!
MEDIDAS
CONSIDERANDO
NICHOS ACABADOS

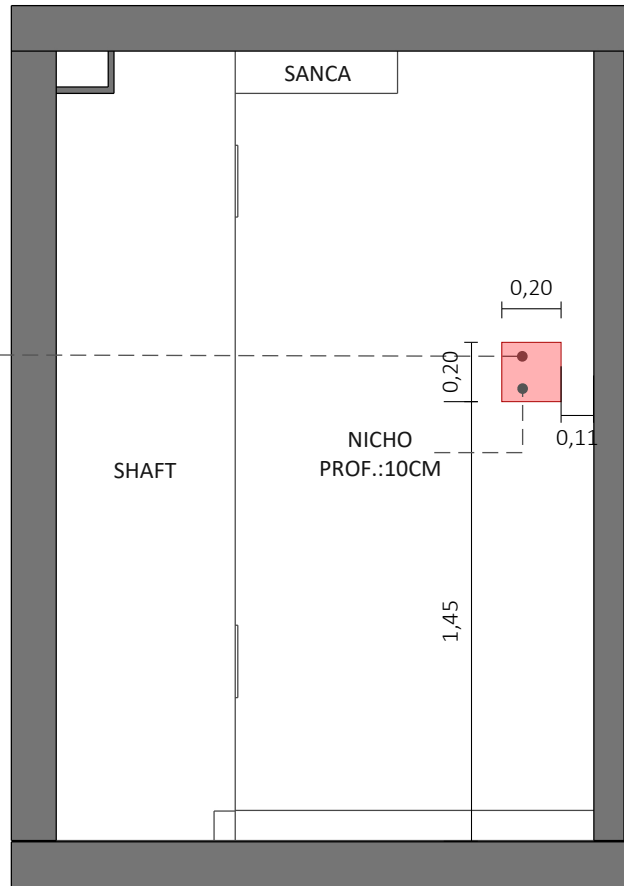

VISTA 01 - NICHOS DA LAVANDERIA

esc. 1:25

OBS: CONFERIR AS MEDIDAS NO LOCAL

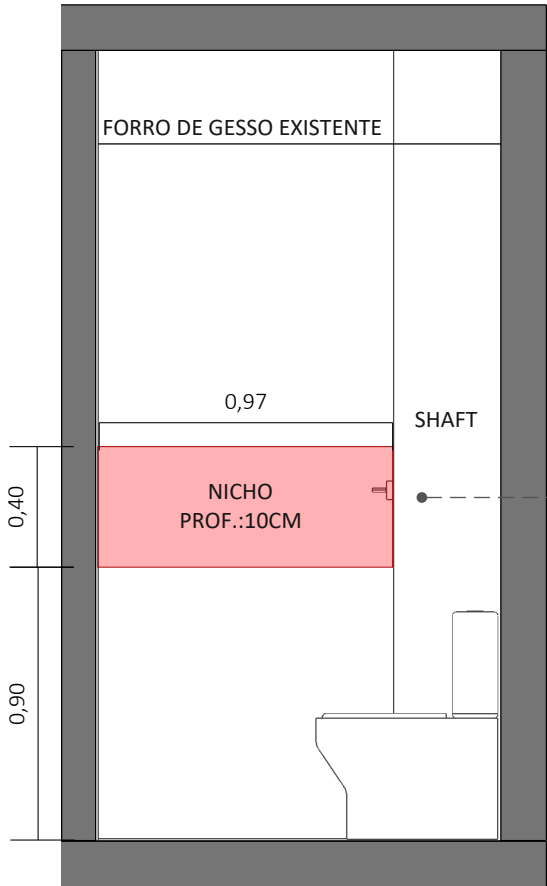

VISTA 02 - NICHOS DO BANHEIRO

esc. 1:25

OBS: CONFERIR AS MEDIDAS NO LOCAL

ATENÇÃO!
MEDIDAS CONSIDERANDO
NICHOS ACABADOS/ REVESTIDOS
EM PORCELANATO

DEMOLIR PAREDE E
REMOVER PORTA,
GUARNIÇÃO E BATENTE

REMOVER DE PISO, BAGUETE
E RODAPÉ
ABERTURA DE VÃO PARA NICHOS
VER VISTA 01

REMOVER DE REVESTIMENTO

ABRIR SANCA E VERIFICAR A POSSIBILIDADE
DE REDUZÍ-LA EM PELA MENOS 15CM

REMOVER TANQUE DE LOUÇAS

01


02




ARQUITETA
NATHÁLIA SIMÕES

ALAMEDA GRAJAÚ, 60 -
BARUERI, SP.
(11) 99778-9234

DESENHO	PROJETO EXECUTIVO
ASSUNTO	PROJETO CIVIL
LOCAL	RUA APA, Nº 164 – APARTAMENTO 815, CAMPOS ELÍSEOS, SÃO PAULO CEP.: 01201-030
ESCALA	1:25
PROJETO	TF815 THAYANE LINHARES
DATA	13/06/25
REVISÃO	R00

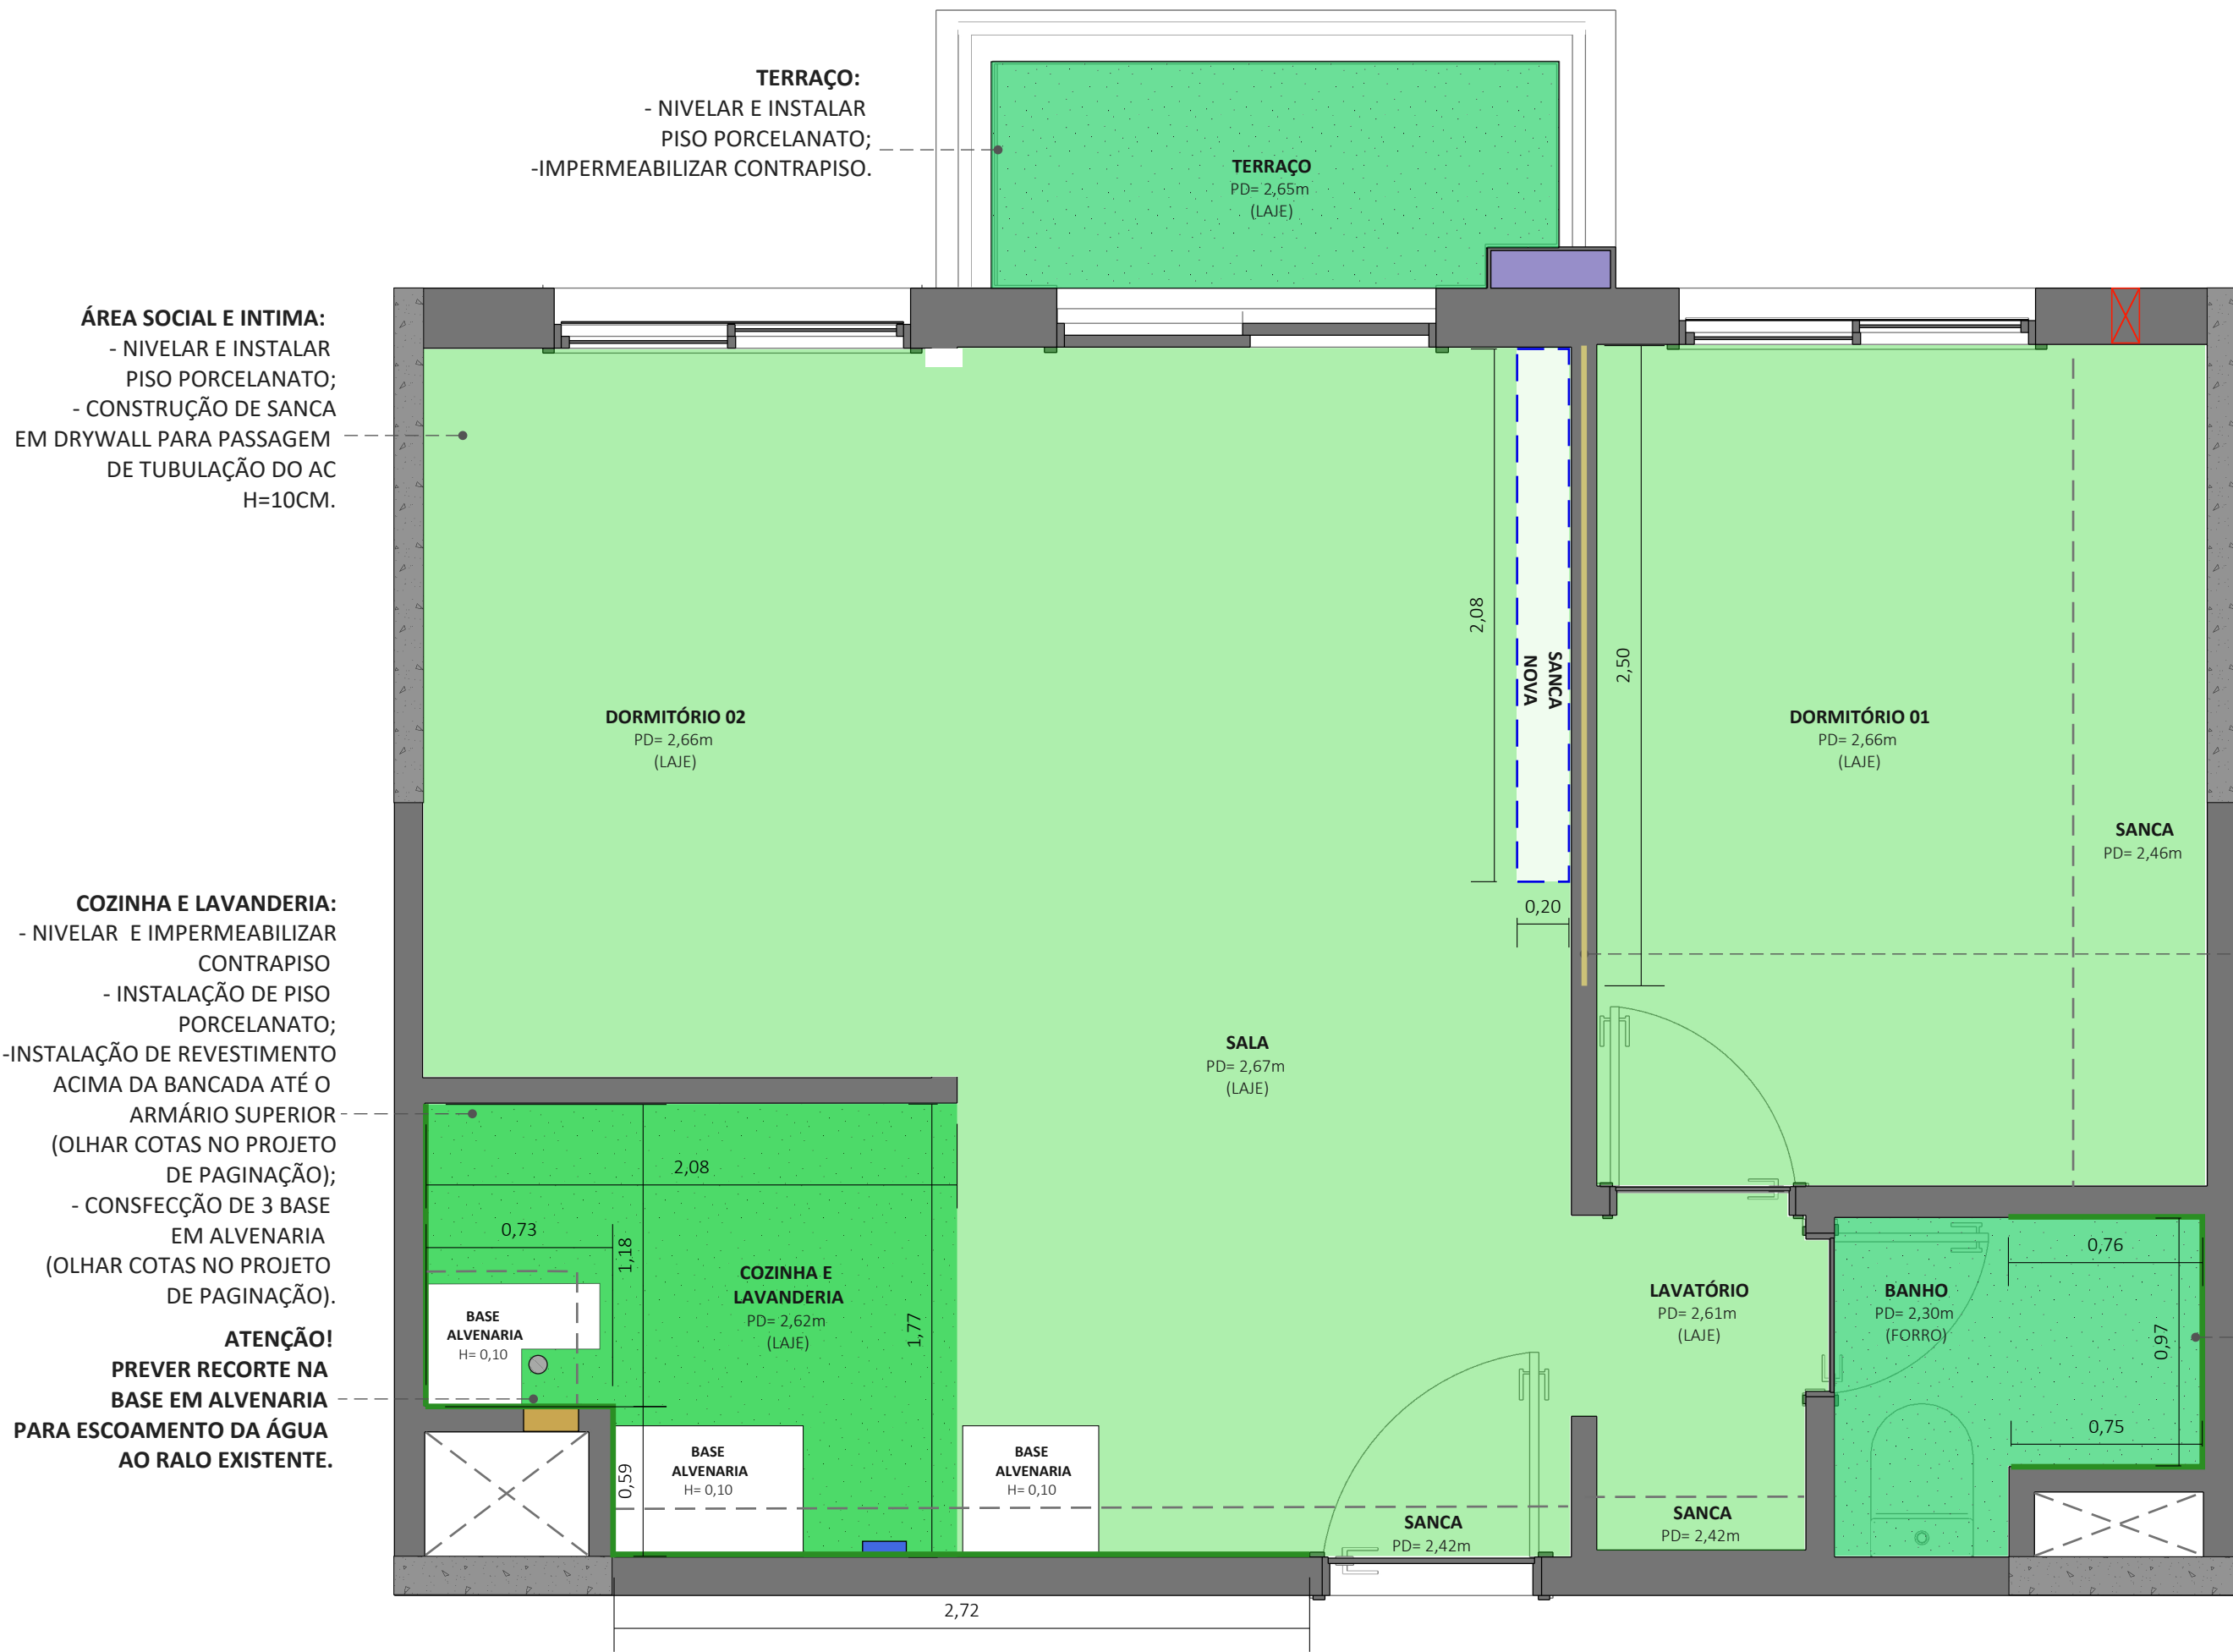

PLANTA CONSTRUIR
esc. 1:25
OBS: CONFERIR AS MEDIDAS NO LOCAL

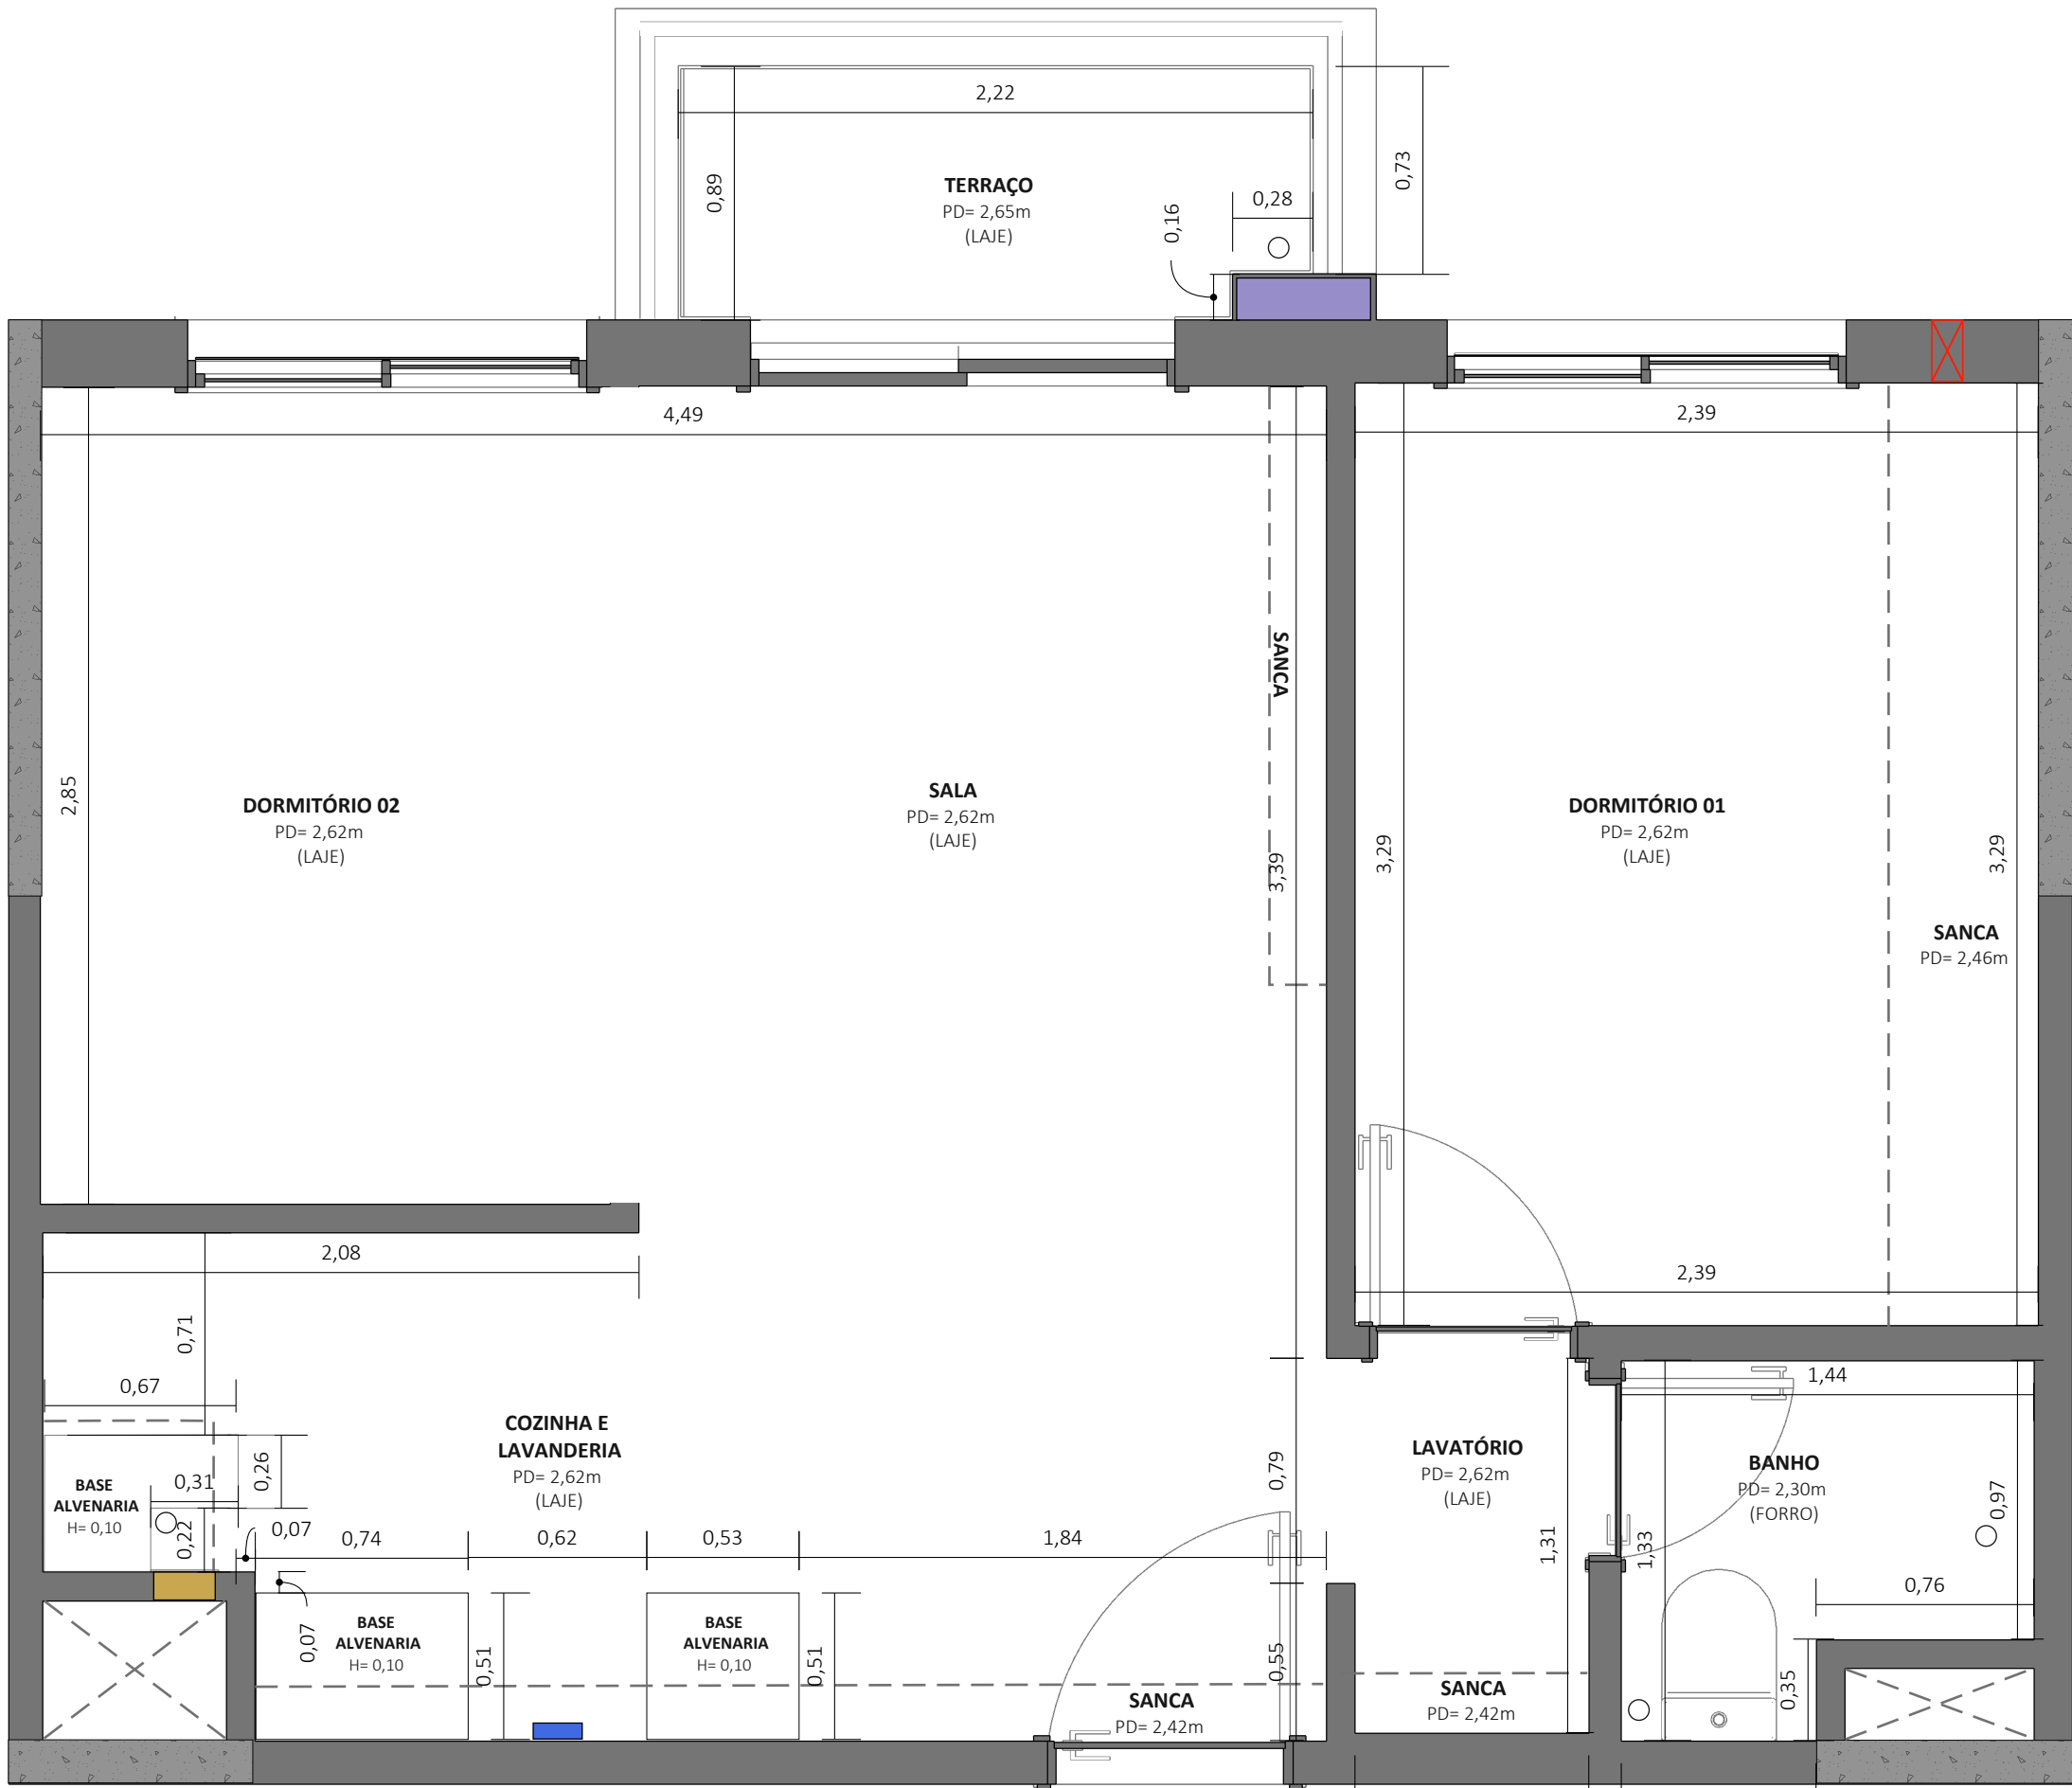

PLANTA ALVENARIA FINAL
esc. 1:25
OBS: CONFERIR AS MEDIDAS NO LOCAL

LEGENDA ALVENARIA	
	ALVENARIA DE VEDAÇÃO
	ALVENARIA ESTRUTURAL
	CARENAGEM PARA PONTOS DE ÁGUA QUENTE E FRIA E ESGOTO
	FURO NA VIGA / PAREDE

LEGENDA CONSTRUIR	
	CONSTRUÇÃO DE BASE DE ALVENARIA. h = 10 cm.
	NIVELAR PISO E IMPERMEABILIZAR PARA INSTALAÇÃO DE PISO PORCELANATO
	INSTALAÇÃO DE PISO PORCELANATO
	INSTALAÇÃO DE REVESTIMENTO
	REFORÇO DE MADEIRA
	CONSTRUÇÃO DE SANÇAS PARA PASSAGEM DE TUBULAÇÃO DO AR-CONDICIONADO COMPRIMENTO INDICADO EM PLANTA / PROFUNDIDADE E ALTURA A SEREM DEFINIDAS PELA EMPRESA DE AR-CONDICIONADO

RESUMO CONSTRUÇÃO	
ITEM	QUANTIDADE
NIVELAMENTO E INSTALAÇÃO DE PISO PORCELANATO	SALA E DORMITÓRIO 02: 18,08 M² DORMITÓRIO 01: 7,86 M²
NIVELAMENTO E IMPERMEABILIZAÇÃO DE PISO BANHOS PAREDES ATÉ 50cm	COZINHA: 2,46M² LAVANDERIA: 0,88M² LAVATÓRIO: 1,25M² BANHEIRO: 1,54M² TERRAÇO: 1,93m²
INSTALAÇÃO DE REVESTIMENTO DE PAREDE	COZINHA: 2,16 M² LAVANDERIA: 1,73M² BANHEIRO: 5,75M²
CONFEÇÃO DE BASE EM ALVENARIA	2 UNID. - COZINHA 1 UNID. - LAVANDERIA

OBSERVAÇÕES GERAIS:
- PREVER REFORÇOS EM PAREDES E FORRO/TETO QUANDO NECESSÁRIO, PRINCIPALMENTE EM DRYWALL
- PONTOS DE GÁS: SEGUIR SEMPRE AS NORMAS TÉCNICAS E DEIXAR REGISTROS COM ACESSO FACILITADO

OBS.: CONFERIR TODAS AS MEDIDAS IN LOCO, INCLUINDO MODELOS DE ELETROS, LOUÇAS E METAIS

- Medidas em metros.
- Desenho de propriedade de LOFT7 ARQUITETURA: Todos os direitos reservados, é vedada cópia, reprodução ou utilização das informações constantes neste documento sem a autorização por escrito dos autores.


 ARQUITETA NATHÁLIA SIMÕES ALAMEDA GRAJAÚ, 60 - BARUERI, SP. (11) 99778-9234	DESENHO	PROJETO EXECUTIVO
	ASSUNTO	PROJETO CIVIL
	LOCAL	RUA APA, Nº 164 – APARTAMENTO 815, CAMPOS ELÍSEOS, SÃO PAULO CEP.: 01201-030
	ESCALA	1:25
	PROJETO	TF815 THAYANE LINHARES
	DATA	13/06/25
	REVISÃO	R00
	02 / 04	

ATENÇÃO!
O PONTO DO DRENO É EXISTENTES. A CAPACIDADE DA EVAPORADORAS É UMA PREVISÃO, NECESSÁRIO APROVAÇÃO JUNTO AO CONDOMÍNIO.

ORÇAR:
-TUBULAÇÃO DE COBRE
-01 EVAPORADORAS 12.000 BTU'S (SALA) QUENTE E FRI
-EQUIPAMENTO CONDENSADORA MULTISPLIT COM CAPACIDADE PROPORCIONAL AS MÁQUINAS

LAVANDERIA:
- NOVO PONTO DE ÁGUA PARA B.BLEND;
- RAMIFICAR PONTO DE ESGOTO PARA MÁQUINA LAVA E SECA;
-MANTER PONTO DE ÁGUA FRIA E ESGOTO PARA TANQUE E TORNEIRA.

COZINHA:
- RAMIFICAR PONTO DE ÁGUA FRIA E ESGOTO PARA CUBA E TORNEIRA;
-MANTER PONTO DE ÁGUA FRIA E ESGOTO PARA LAVA LOUÇAS.
-MANTER PONTO DE GÁS.

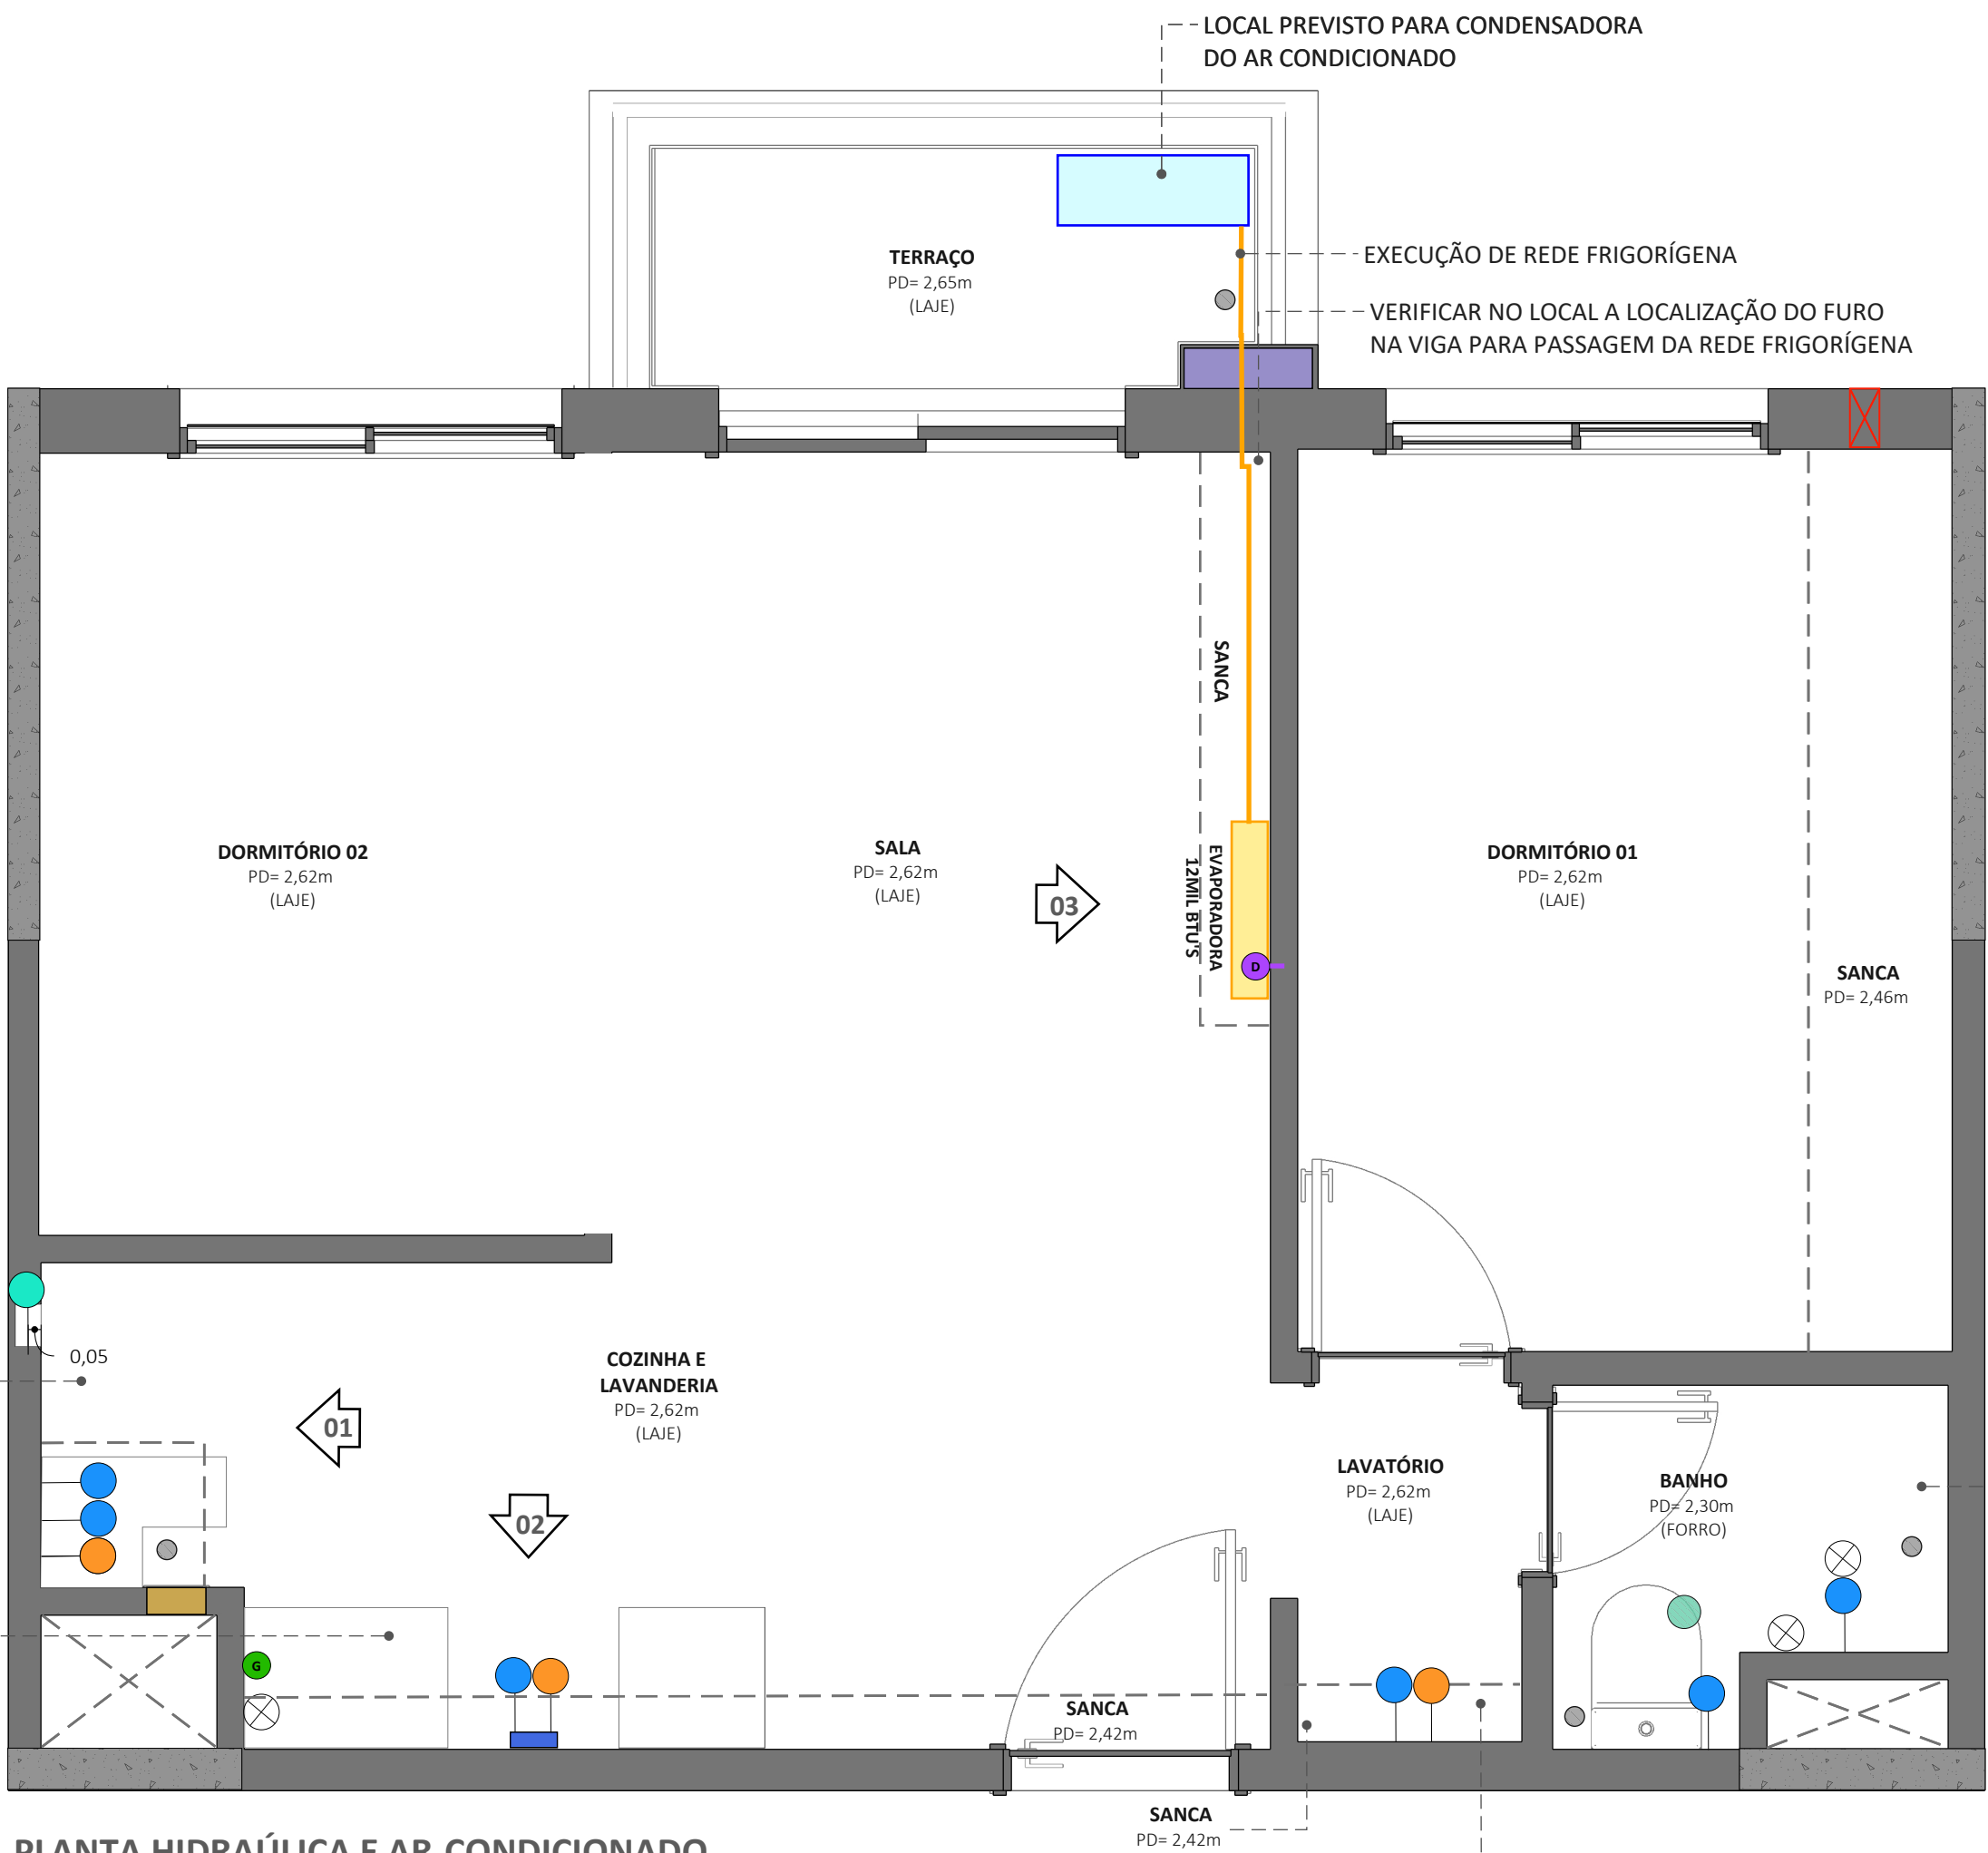

PLANTA HIDRÁULICA E AR-CONDICIONADO


esc. 1:25
OBS: CONFERIR AS MEDIDAS NO LOCAL

BANHEIRO:
- PREVER A TROCA DO MODELO DA BACIA SANITÁRIA (NO MESMO LOCAL);
- MANTER RALOS E TROCAR ACABAMENTOS;
- MANTER TODOS OS PONTOS HIDRÁULICOS EXISTENTES;
- MANTER ACABAMENTOS DE REGISTRO;
- INSTALAÇÃO DE CHUVEIRO ELÉTRICO MODELO A DEFINIR (VERIFICAR CAPACIDADE DO QUADRO DE LUZ)


LAVATÓRIO:
- MANTER TODOS OS PONTOS HIDRÁULICOS EXISTENTES;
- PREVER TROCA DA TORNEIRA, CUBA E SIFÃO.

LEGENDA ALVENARIA ORIGINAL	
	ALVENARIA DE VEDAÇÃO
	ALVENARIA ESTRUTURAL
	CARENAGEM PARA PONTOS DE ÁGUA FRIA E ESGOTO
	EXAUSTÃO MECÂNICA
	FURO NA VIGA / PAREDE
	ENCHIMENTO
	VENTILAÇÃO PERMANENTE


LEGENDA HIDRÁULICA E AR-CONDICIONADO	
	PONTO DE ÁGUA FRIA OBS.: ALTURA ESPECIFICADA EM VISTA
	PONTO DE ESGOTO OBS.: ALTURA ESPECIFICADA EM VISTA
	NOVO PONTO DE ÁGUA FRIA OBS.: ALTURA ESPECIFICADA EM VISTA
	REGISTRO DE PRESSÃO E GAVETA
	DRENO EXISTENTE
	CAMINHO PREVISTO PARA TUBULAÇÃO DRENO
	CAMINHO PREVISTO PARA TUBULAÇÃO FRIGORÍGENA
	APARELHO DE AR-CONDICIONADO OBS.: CAPACIDADE PREVISTA, DESCRITA EM CADA APARELHO
	CONDENSADORA

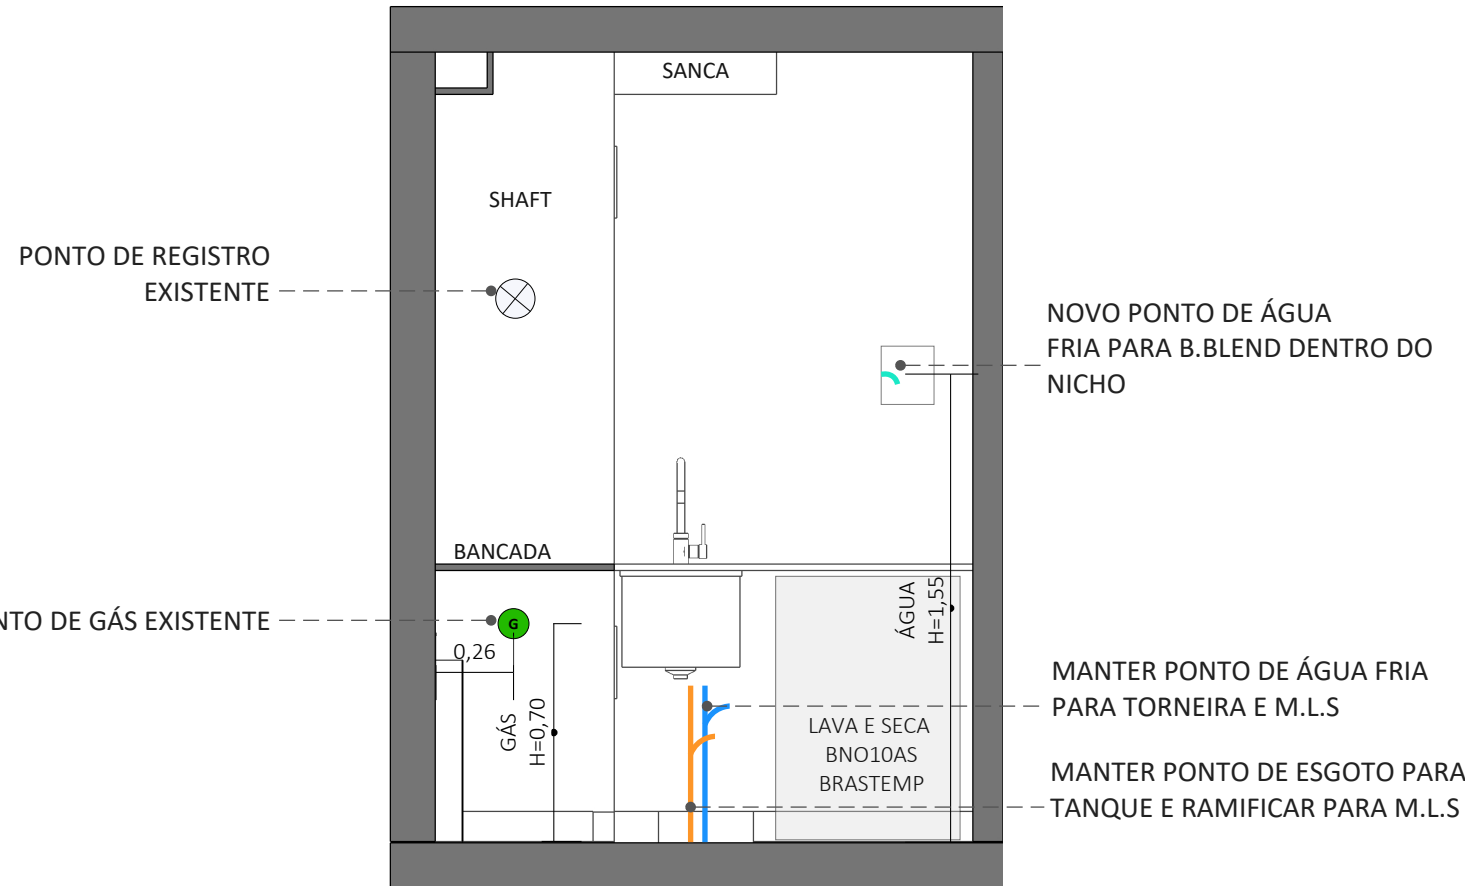

VISTA 01 - HIDRÁULICA DA LAVANDERIA
ESC. 1:25

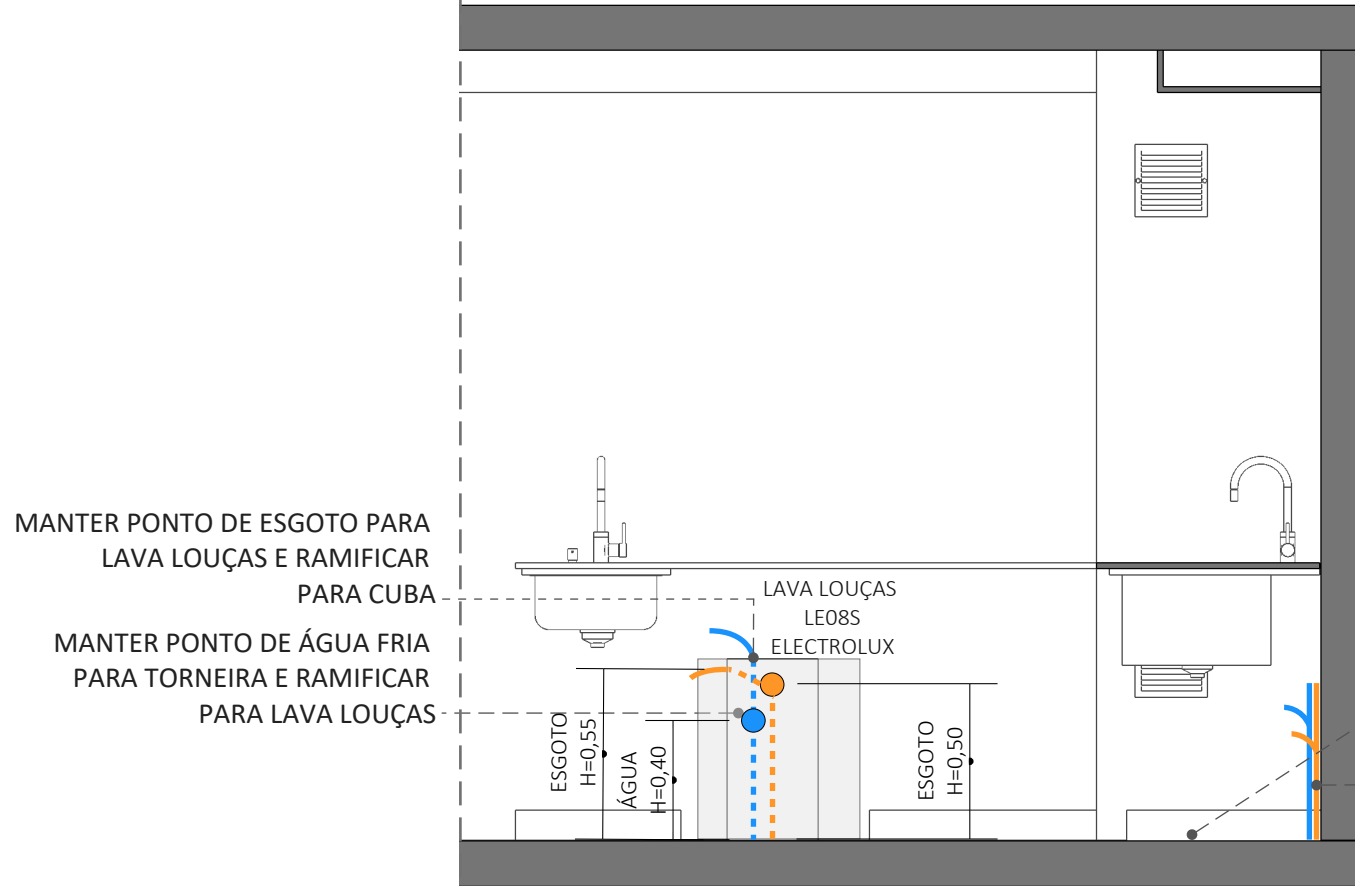

VISTA 02 - HIDRÁULICA DA LAVANDERIA
ESC. 1:25

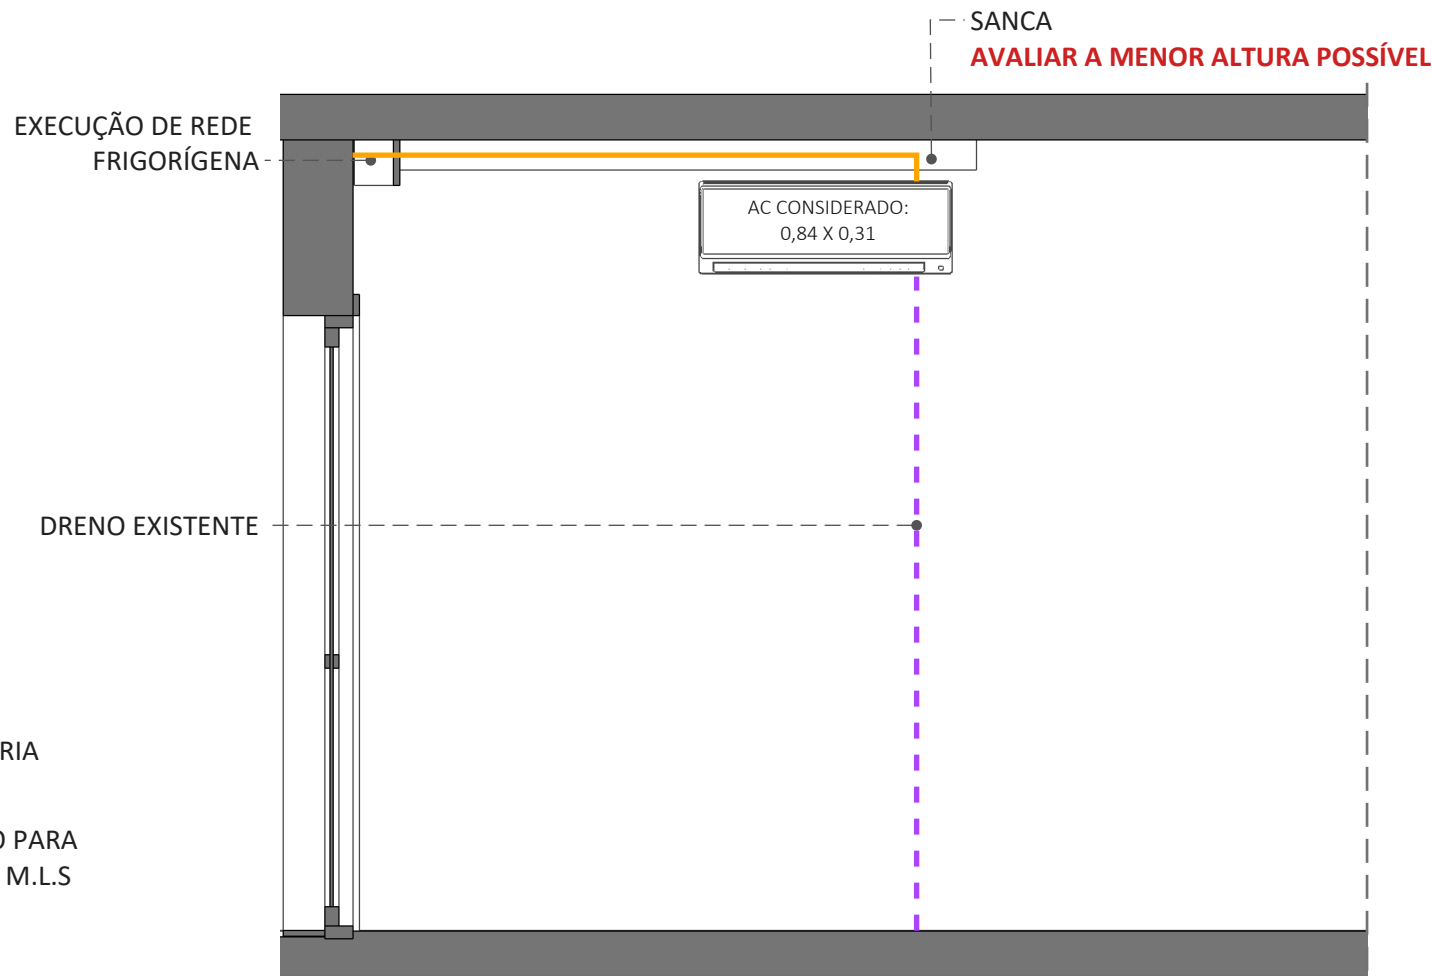


VISTA 03 - AR-CONDICIONADO
ESC. 1:25
CONFIRMAR DIMENSÕES DE ACORDO COM EQUIPAMENTOS DE AR-CONDICIONADO COMPRADOS

OBSERVAÇÕES GERAIS:
- PREVER REFORÇOS EM PAREDES E FORRO/TETO QUANDO NECESSÁRIO, PRINCIPALMENTE EM DRYWALL
- PONTOS DE GÁS: SEGUIR SEMPRE AS NORMAS TÉCNICAS E DEIXAR REGISTROS COM ACESSO FACILITADO

OBS.: CONFERIR TODAS AS MEDIDAS IN LOCO, INCLUINDO MODELOS DE ELETROS, LOUÇAS E METAIS


- Medidas em metros.
- Desenho de propriedade de LOFT7 ARQUITETURA: Todos os direitos reservados, é vedada cópia, reprodução ou utilização das informações constantes neste documento sem a autorização por escrito dos autores.

 ARQUITETA NATHÁLIA SIMÕES ALAMEDA GRAJAÚ, 60 - BARUERI, SP. (11) 99778-9234	DESENHO	PROJETO EXECUTIVO
	ASSUNTO	PROJETO CIVIL
	LOCAL	RUA APA, Nº 164 – APARTAMENTO 815, CAMPOS ELÍSEOS, SÃO PAULO CEP.: 01201-030
	ESCALA	1:25
	PROJETO	TF815 THAYANE LINHARES
	DATA	13/06/25
	REVISÃO	R00

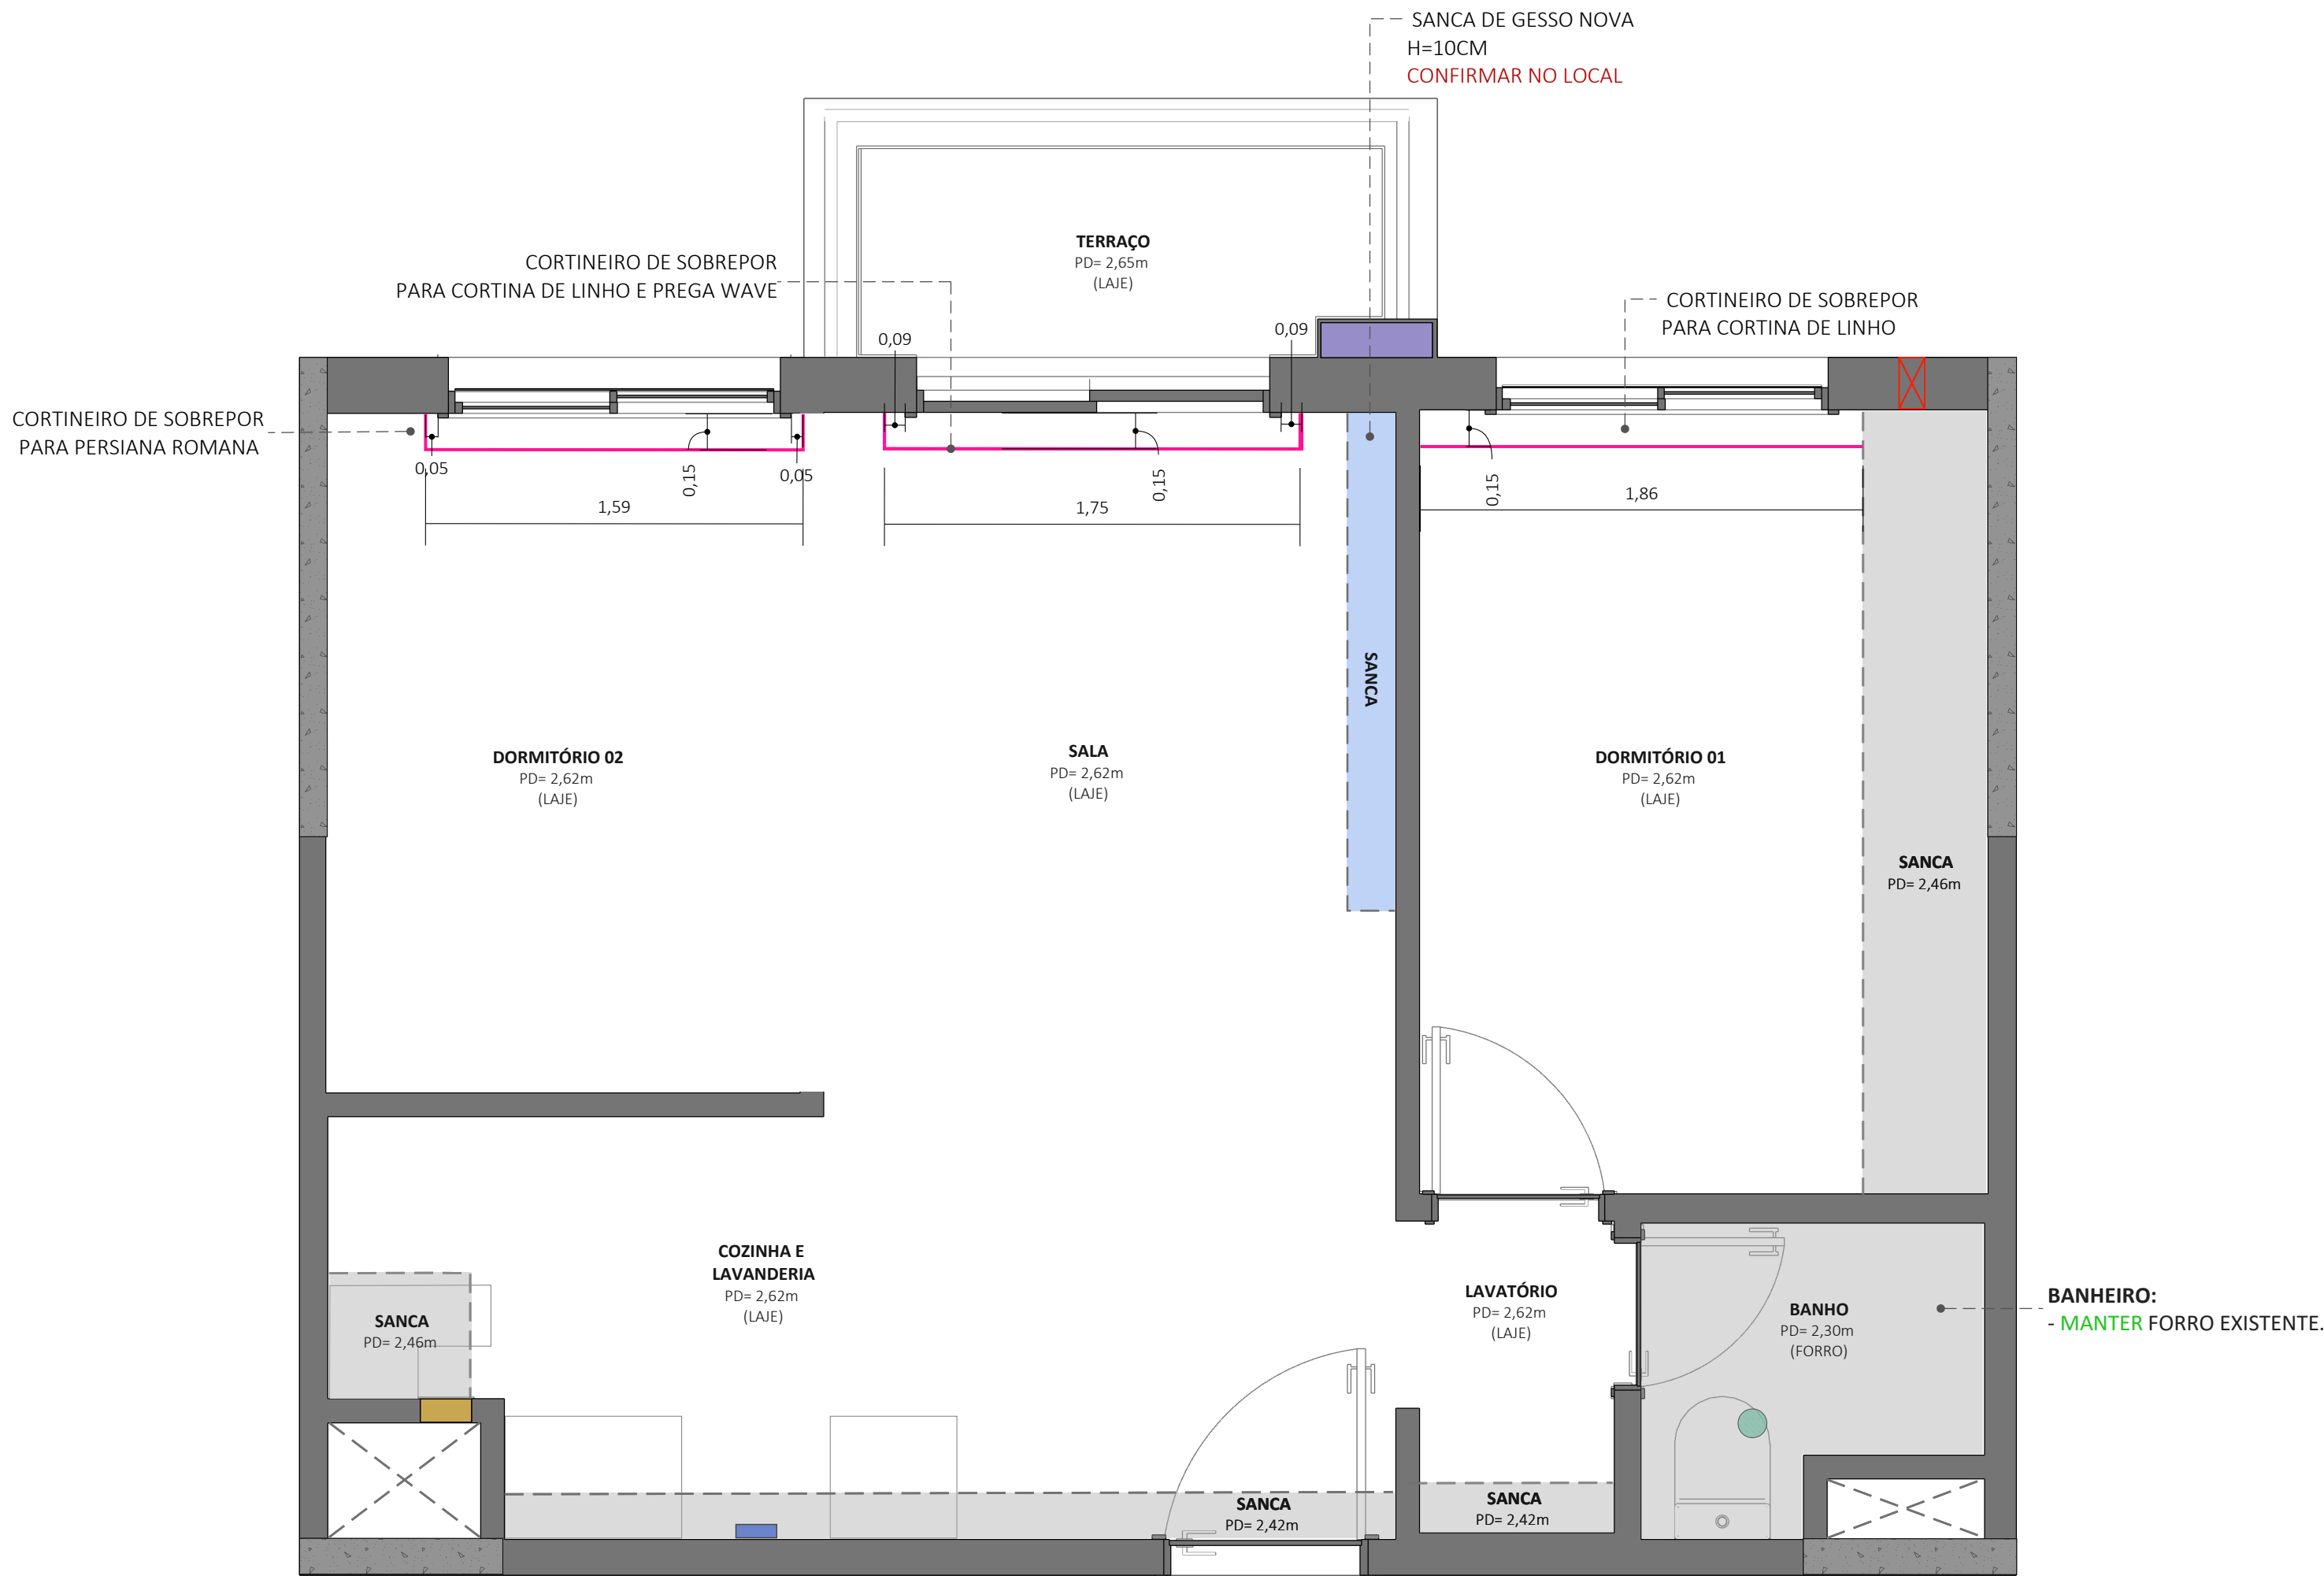

PLANTA FORRO

esc. 1:25
OBS: CONFERIR AS MEDIDAS NO LOCAL

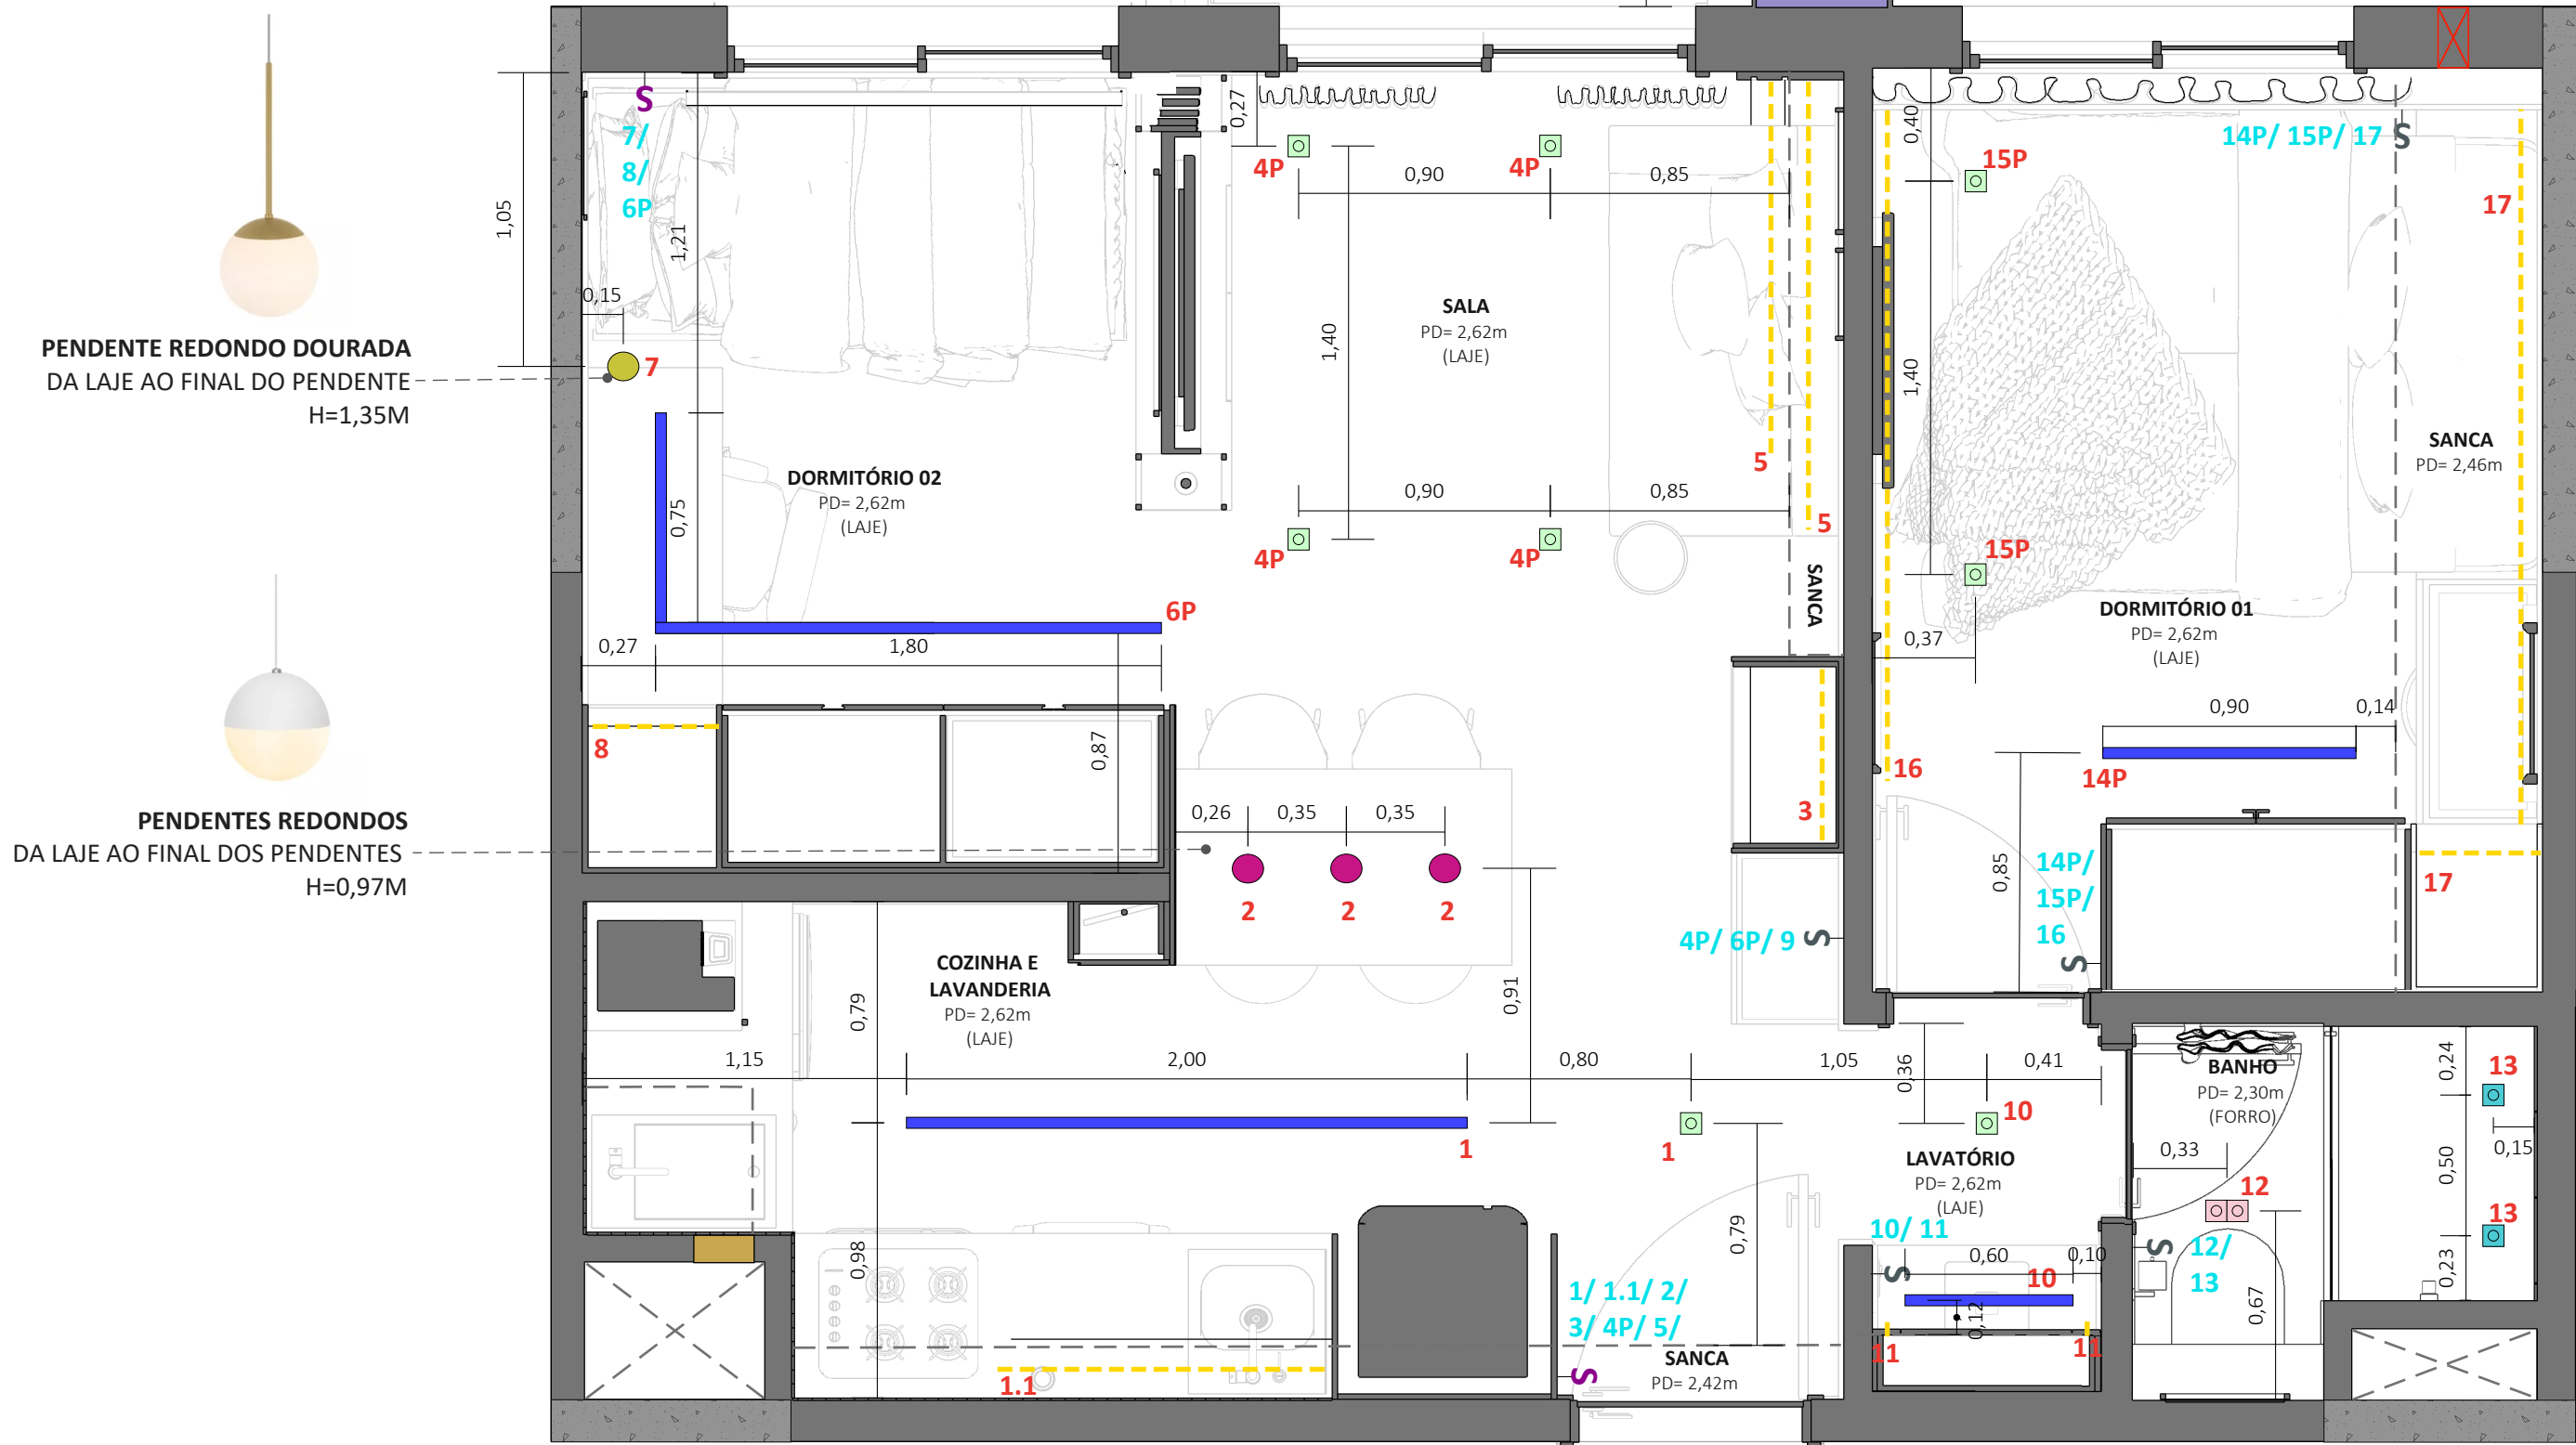

PLANTA ILUMINAÇÃO

esc. 1:25
OBS: CONFERIR AS MEDIDAS NO LOCAL

ATENÇÃO! PREVER PONTO NEUTRO EM TODOS OS INTERRUPTORES PARA USO DE INTERRUPTORES INTELIGENTES

LEGENDA ALVENARIA ORIGINAL	
	ALVENARIA DE VEDAÇÃO
	ALVENARIA ESTRUTURAL
	CARENAGEM PARA PONTOS DE ÁGUA FRIA E ESGOTO
	EXAUSTÃO MECÂNICA
	FURO NA VIGA / PAREDE
	ENCHIMENTO
	VENTILAÇÃO PERMANENTE

LEGENDA FORRO	
	FORRO DE GESSO / SANCA EXISTENTE
	SANCA NOVA
	CORTINEIRO DE SOBREPOR SEM ILUMINAÇÃO

LEGENDA INTERRUPTOR E CIRCUÍTO	
	INTERRUPTOR NOVO
	INTERRUPTOR EXISTENTE
	NÚMERO DO CIRCUITO NO INTERRUPTOR
	NÚMERO DO CIRCUITO NA LUMINÁRIA

LEGENDA ILUMINAÇÃO - ÁREA SOCIAL (COZINHA, SALA, OFFICE E LAV.)		
	SPOT SOBREPOR LED QUADRADO SW ALUMÍNIO BRANCO 3000K - 500 lm - IRC 70+	06 UNID.
	PERFIL DE LED DE SOBREPOR BRANCO C/ FITA DE LED - 3000K - 1500 lm - IRC 90+ 60mm COM FONTE NA PEÇA	2ml+ 2ml+ 1ml+ 1ml
	PENDENTE REDONDO DOURADO- LÂMPADA 2700K	1 UNID.
	PENDENTE REDONDO ALUMÍNIO BRANCO-LÂMPADA 2700K	3 UNID.
	FITA DE LED PARA MARCENARIA - 2700K - 900 lm - IRC 90+	VER EM PROJETO DE MARCENARIA

LEGENDA ILUMINAÇÃO - TERRAÇO		
	SPOT SOBREPOR LED QUADRADO 5W ALUMÍNIO BRANCO 3000K - 500 lm - IRC 70+	02 UNID.

LEGENDA ILUMINAÇÃO - BANHEIRO		
	PLAFON DE EMBUTIR ALUMÍNIO 7,5X7,5CM FLAT LÂMPADA 2700K - 900 lm - IRC 90+	2 UNID
	PLAFON DE EMBUTIR ALUMÍNIO 7,5X9CM FLAT LÂMPADA 2700K - 900 lm - IRC 90+	1 UNID

LEGENDA ILUMINAÇÃO - DORMITÓRIO		
	SPOT SOBREPOR LED QUADRADO SW ALUMÍNIO BRANCO 3000K - 500 lm - IRC 70+	02 UNID.
	PERFIL DE LED DE SOBREPOR BRANCO C/ FITA DE LED - 3000K - 1500 lm - IRC 90+ 60mm COM FONTE NA PEÇA	1ml
	FITA DE LED PARA MARCENARIA - 2700K - 900 lm - IRC 90+	VER EM PROJETO DE MARCENARIA

OBSERVAÇÕES GERAIS:
- PREVER REFORÇOS EM PAREDES E FORRO/TETO QUANDO NECESSÁRIO, PRINCIPALMENTE EM DRYWALL
- PONTOS DE GÁS: SEGUIR SEMPRE AS NORMAS TÉCNICAS E DEIXAR REGISTROS COM ACESSO FACILITADO

OBS.: CONFERIR TODAS AS MEDIDAS IN LOCO, INCLUINDO MODELOS DE ELETROS, LOUÇAS E METAIS


- Medidas em metros.

- Desenho de propriedade de LOFT7 ARQUITETURA: Todos os direitos reservados, é vedada cópia, reprodução ou utilização das informações constantes neste documento sem a autorização por escrito dos autores.

ARQUITETA
NATHÁLIA SIMÕES

ALAMEDA GRAJAÚ, 60 -
BARUERI, SP.
(11) 99778-9234

DESENHO	PROJETO EXECUTIVO
ASSUNTO	PROJETO CIVIL
LOCAL	RUA APA, Nº 164 – APARTAMENTO 815, CAMPOS ELÍSEOS, SÃO PAULO CEP.: 01201-030
ESCALA	1:25
PROJETO	TF815 THAYANE LINHARES
DATA	13/06/25
REVISÃO	R00

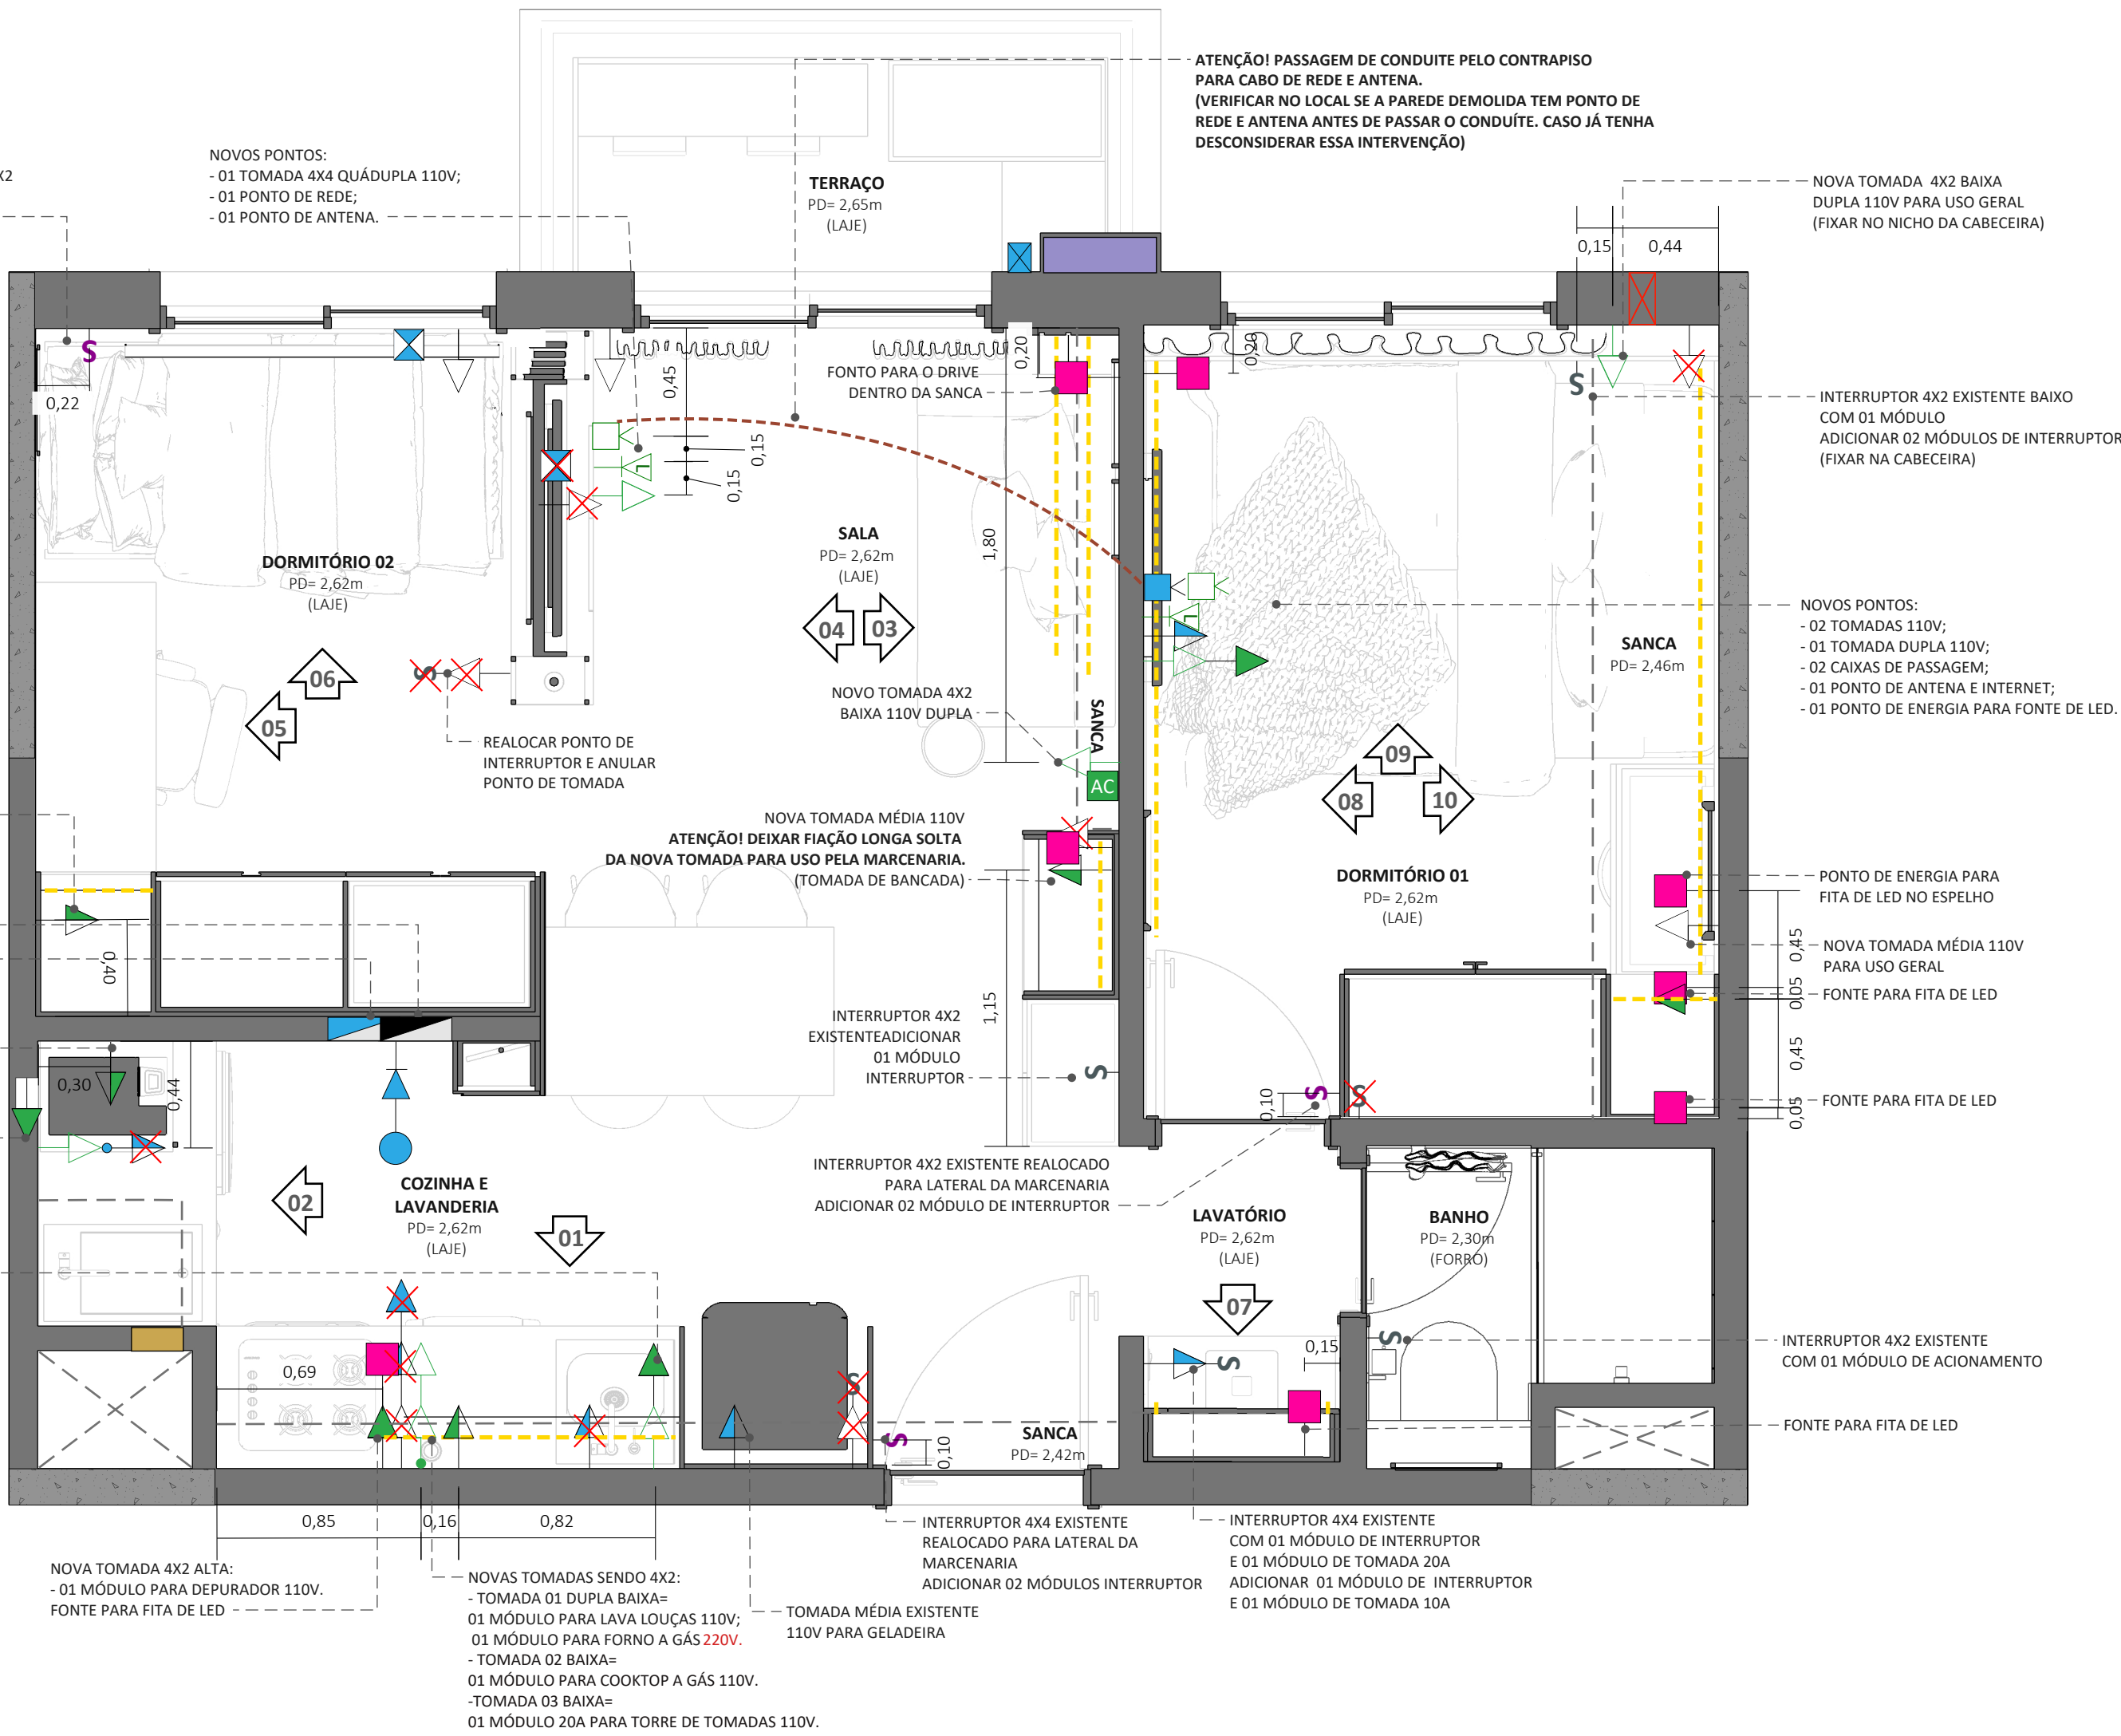

PLANTA ELÉTRICA
esc. 1:25
OBS: CONFERIR AS MEDIDAS NO LOCAL

ATENÇÃO! PREVER PONTO NEUTRO EM TODOS OS INTERRUPTORES PARA USO DE INTERRUPTORES INTELIGENTES




LEGENDA ALVENARIA ORIGINAL	
	ALVENARIA DE VEDAÇÃO
	ALVENARIA ESTRUTURAL
	CARENAGEM PARA PONTOS DE ÁGUA FRIA E ESGOTO
	EXAUSTÃO MECÂNICA
	FURO NA VIGA / PAREDE
	ENCHIMENTO
	VENTILAÇÃO PERMANENTE

× PONTO EXISTENTE A SER ANULADO OU REALOCADO

LEGENDA ELÉTRICA - NOVOS PONTOS	
	TOMADA BAIXA 2P+T (127 V)
	TOMADA MÉDIA 2P+T (127 V)
	TOMADA ALTA 2P+T (127 V)
	TOMADA BAIXA 2P+T (220 V)
	PONTO ESPECÍFICO PARA INSTALAÇÃO DE AR CONDICIONADO OBS.: VERIFICAR AS ESPECIFICAÇÕES COM FORNECEDOR DO EQUIPAMENTO
	PONTO PARA TV
	PONTO PARA TELEFONE/INTERNET E LÓGICA
	PONTO PARA TELEFONE/INTERFONE INTERNO
	CAIXA DE PASSAGEM
	PONTO ELÉTRICO PARA FITA DE LED
	PONTO ENERGIZADO ACIMA DO FORRO PARA PERSIANAS MOTORIZADAS E COFEIA (110V)
	INTERRUPTOR

LEGENDA ELÉTRICA - PONTOS EXISTENTES	
	TOMADA BAIXA 2P+T (127 V)
	TOMADA MÉDIA 2P+T (127 V)
	TOMADA ALTA 2P+T (127 V)
	TOMADA BAIXA 2P+T (220 V)
	PONTO PARA TV
	PONTO PARA TELEFONE/INTERFONE E LÓGICA
	PONTO PARA TELEFONE/INTERFONE INTERNO OBS.: ALTURA ESPECIFICADA EM PLANTA
	INTERFONE / CIGARRA
	INTERRUPTOR
	QUADRO DE SISTEMAS
	QUADRO DE LUZ E FORÇA
	PONTO PARA CONDENSADORA (AR CONDICIONADO)

OBSERVAÇÕES:
1) PARA MAIS DETALHES DE ELÉTRICA VER VISTAS DOS AMBIENTES.
2) EM CASO DE CONSTRUÇÃO EM ALVENARIA ESTRUTURAL: OS NOVOS PONTOS DE ELÉTRICA INDICADOS DEVEM SER PASSADOS POR FORRO DE GESSO, MARCENARIA OU DRYWALL.

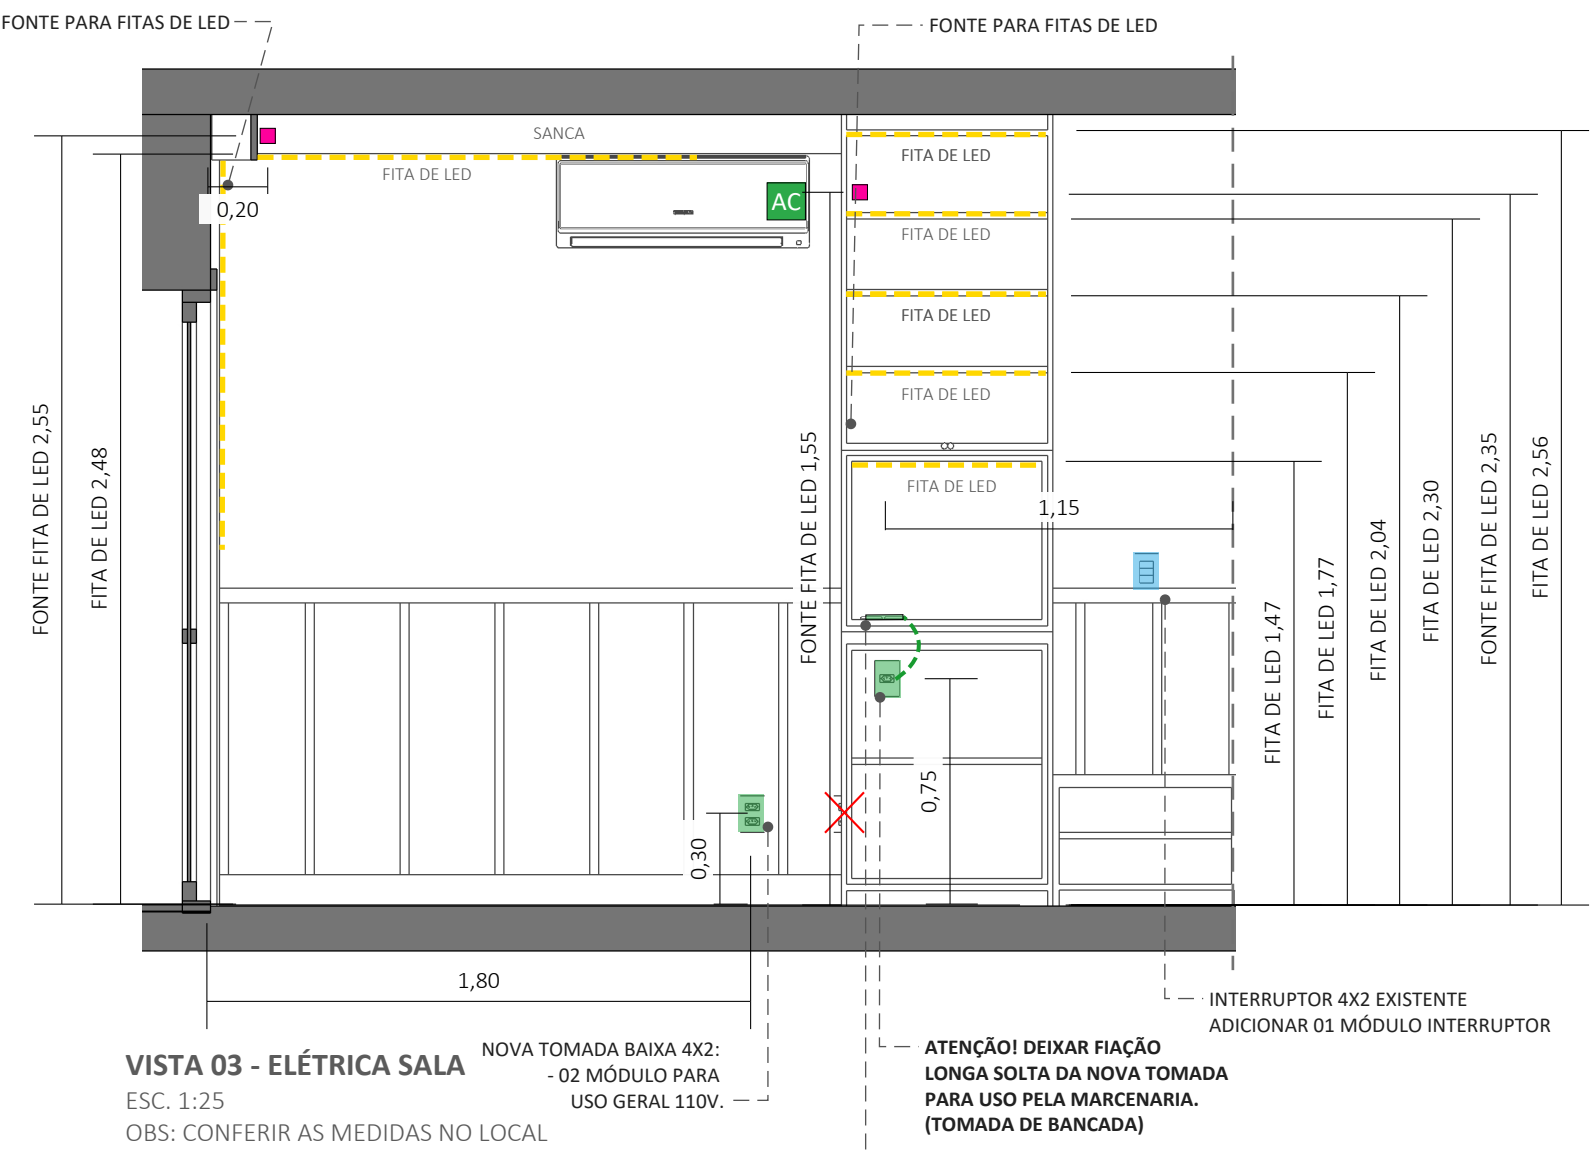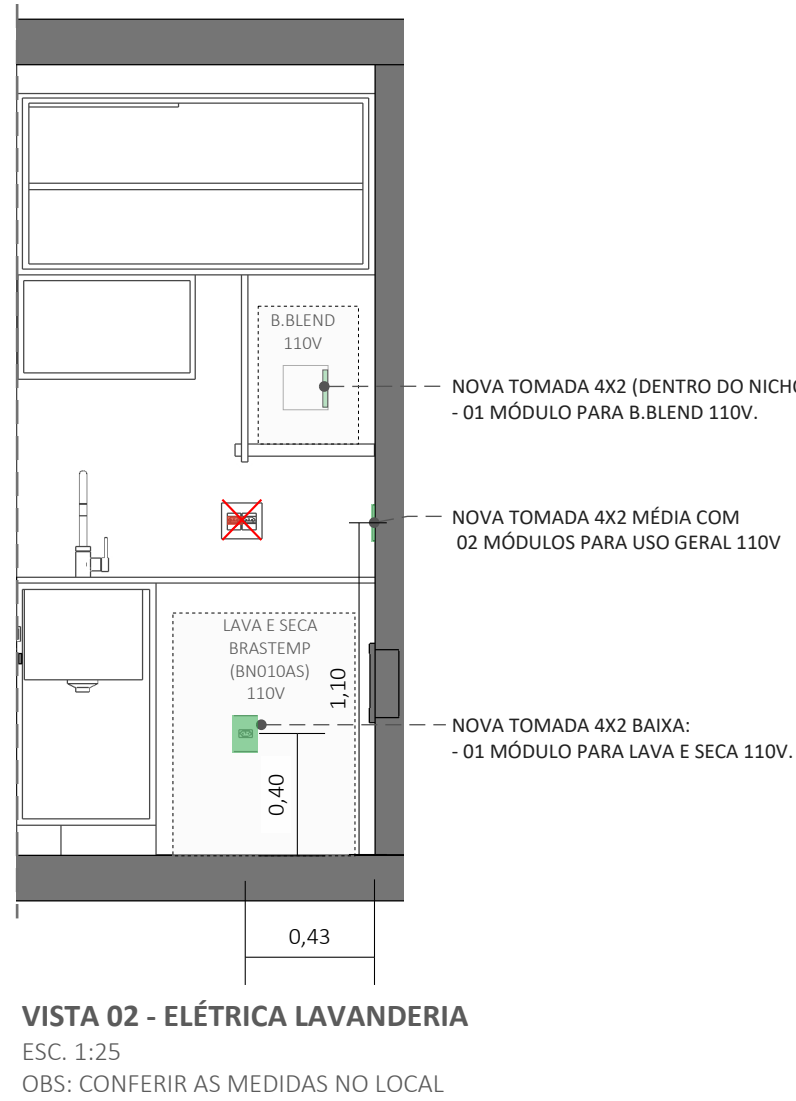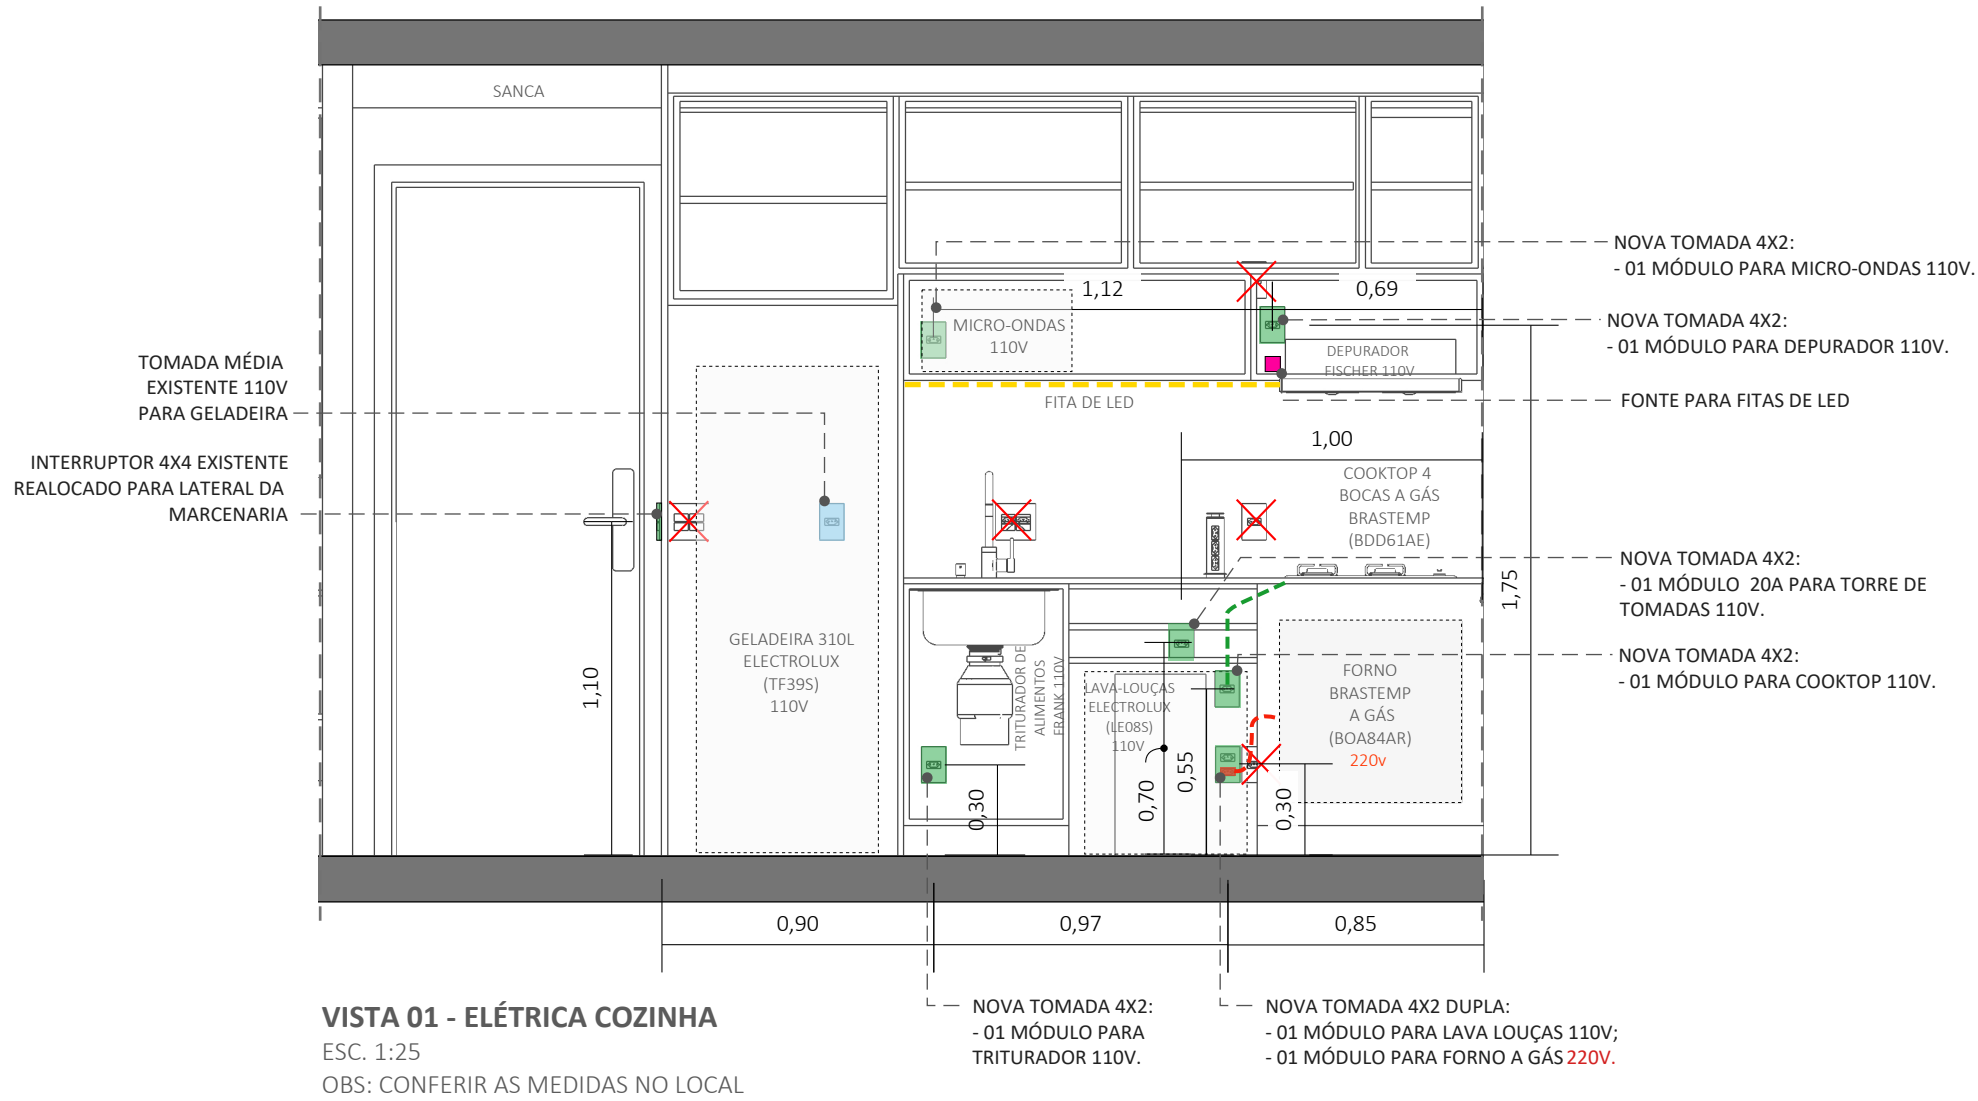

OBSERVAÇÕES GERAIS:
- PREVER REFORÇOS EM PAREDES E FORRO/TETO QUANDO NECESSÁRIO, PRINCIPALMENTE EM DRYWALL
- PONTOS DE GÁS: SEGUIR SEMPRE AS NORMAS TÉCNICAS E DEIXAR REGISTROS COM ACESSO FACILITADO


OBS.: CONFERIR TODAS AS MEDIDAS IN LOCO, INCLUINDO MODELOS DE ELETROS, LOUÇAS E METAIS

- Medidas em metros.

- Desenho de propriedade de LOFT7 ARQUITETURA: Todos os direitos reservados, é vedada cópia, reprodução ou utilização das informações constantes neste documento sem a autorização por escrito dos autores.


LOFT7
arquitetura
ARQUITETA
NATHÁLIA SIMÕES
ALAMEDA GRAJAÚ, 60 -
BARUERI, SP.
(11) 99778-9234

DESENHO	PROJETO EXECUTIVO
ASSUNTO	PROJETO CIVIL
LOCAL	RUA APA, Nº 164 – APARTAMENTO 815, CAMPOS ELÍSEOS, SÃO PAULO CEP.: 01201-030
ESCALA	1:25
PROJETO	TF815 THAYANE LINHARES
DATA	13/06/25
REVISÃO	R00

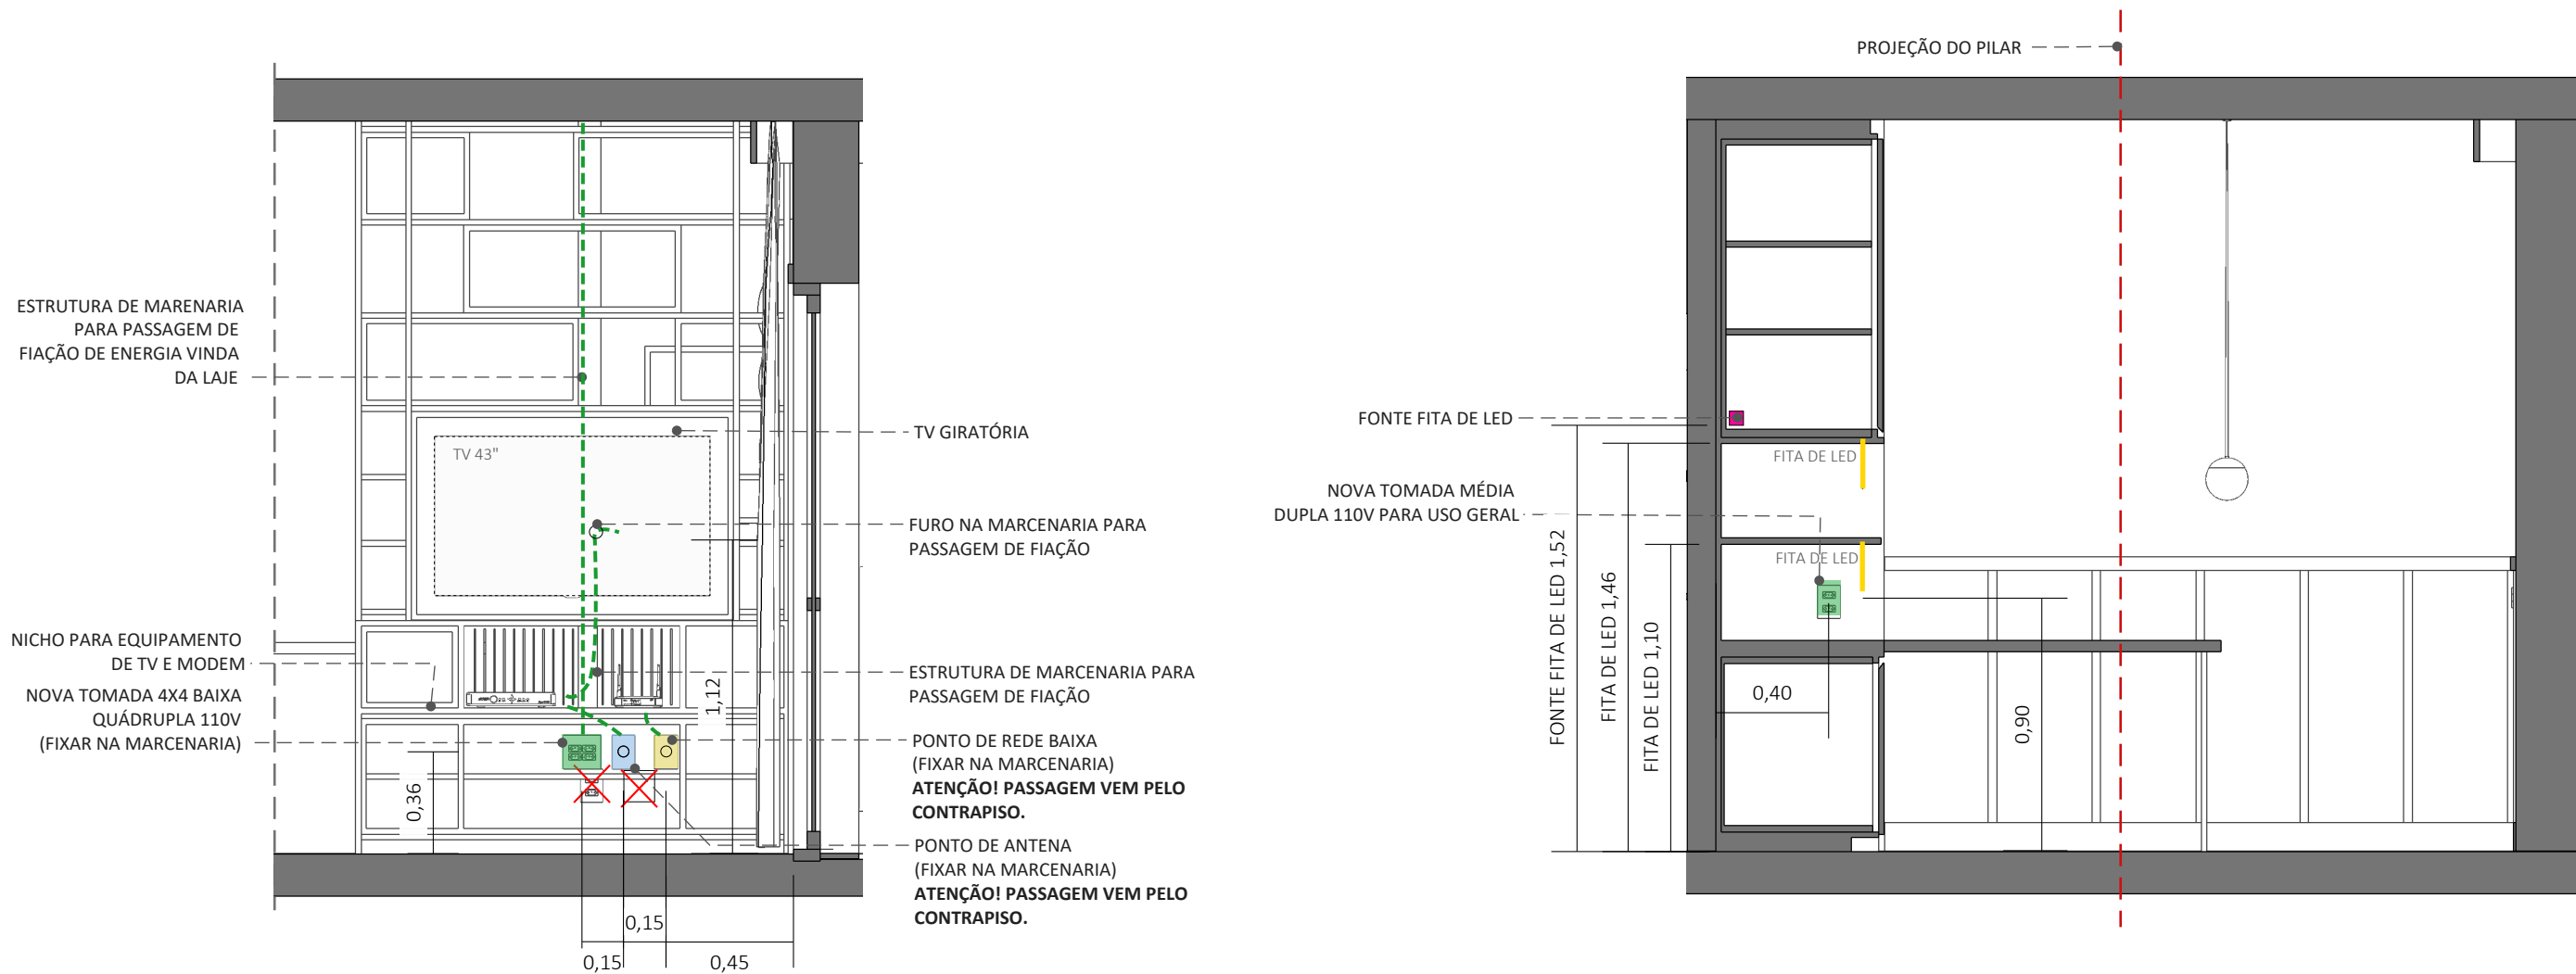


VISTA 04 - ELÉTRICA SALA
ESC. 1:25
OBS: CONFERIR AS MEDIDAS NO LOCAL


VISTA 05 - ELÉTRICA DORMITÓRIO 02
ESC. 1:25
OBS: CONFERIR AS MEDIDAS NO LOCAL

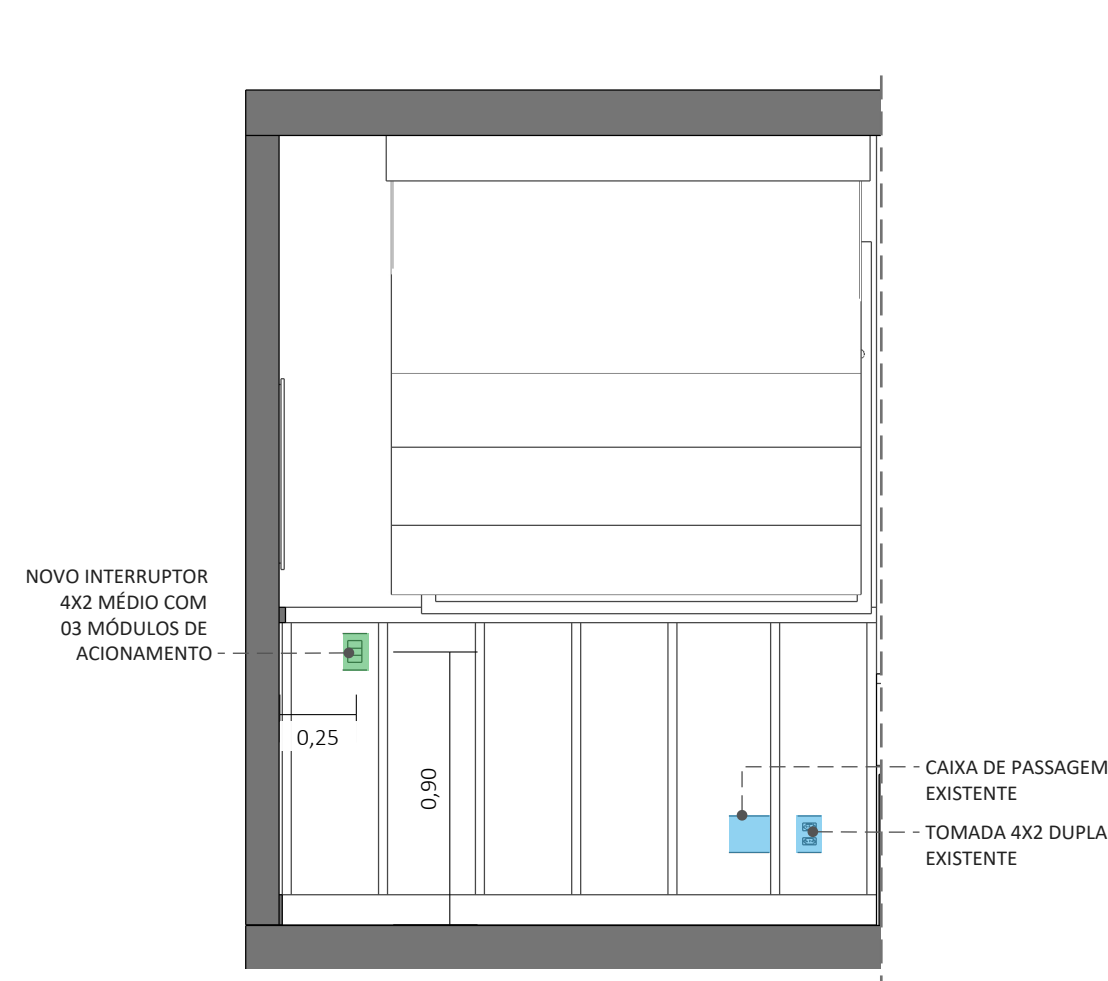


VISTA 06 - ELÉTRICA DORMITÓRIO 02
ESC. 1:25
OBS: CONFERIR AS MEDIDAS NO LOCAL

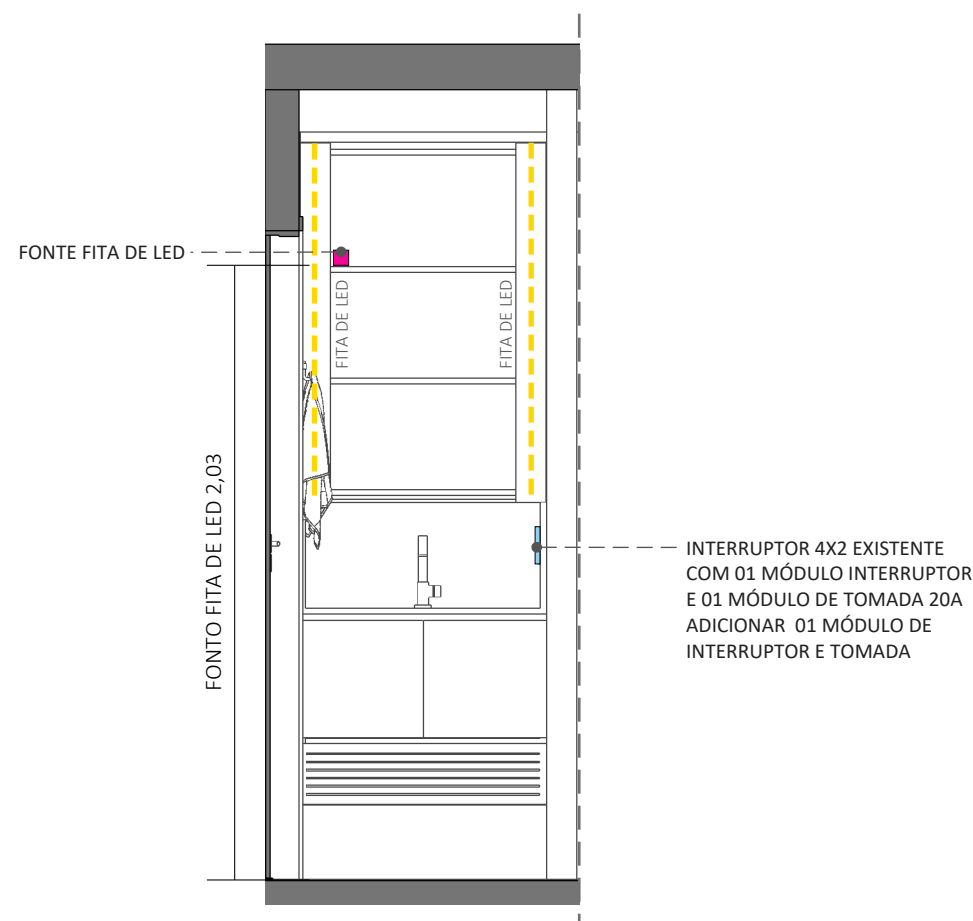


VISTA 07 - ELÉTRICA LAVATÓRIO
ESC. 1:25
OBS: CONFERIR AS MEDIDAS NO LOCAL

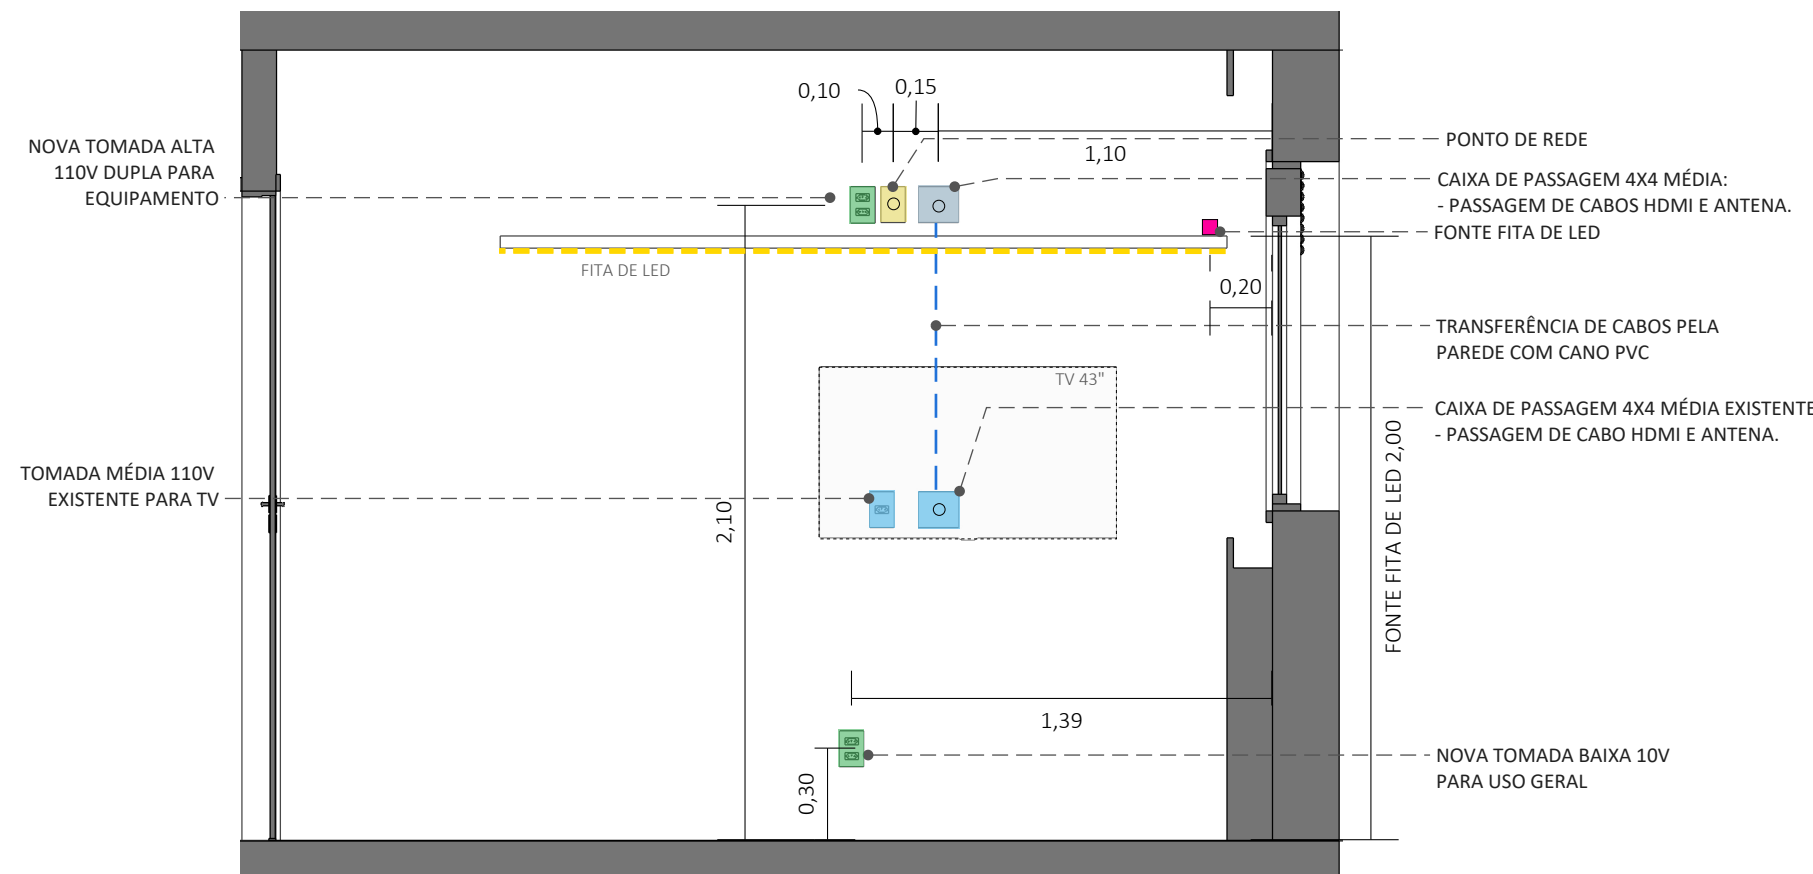

VISTA 08 - ELÉTRICA DORMITÓRIO 01
ESC. 1:25
OBS: CONFERIR AS MEDIDAS NO LOCAL

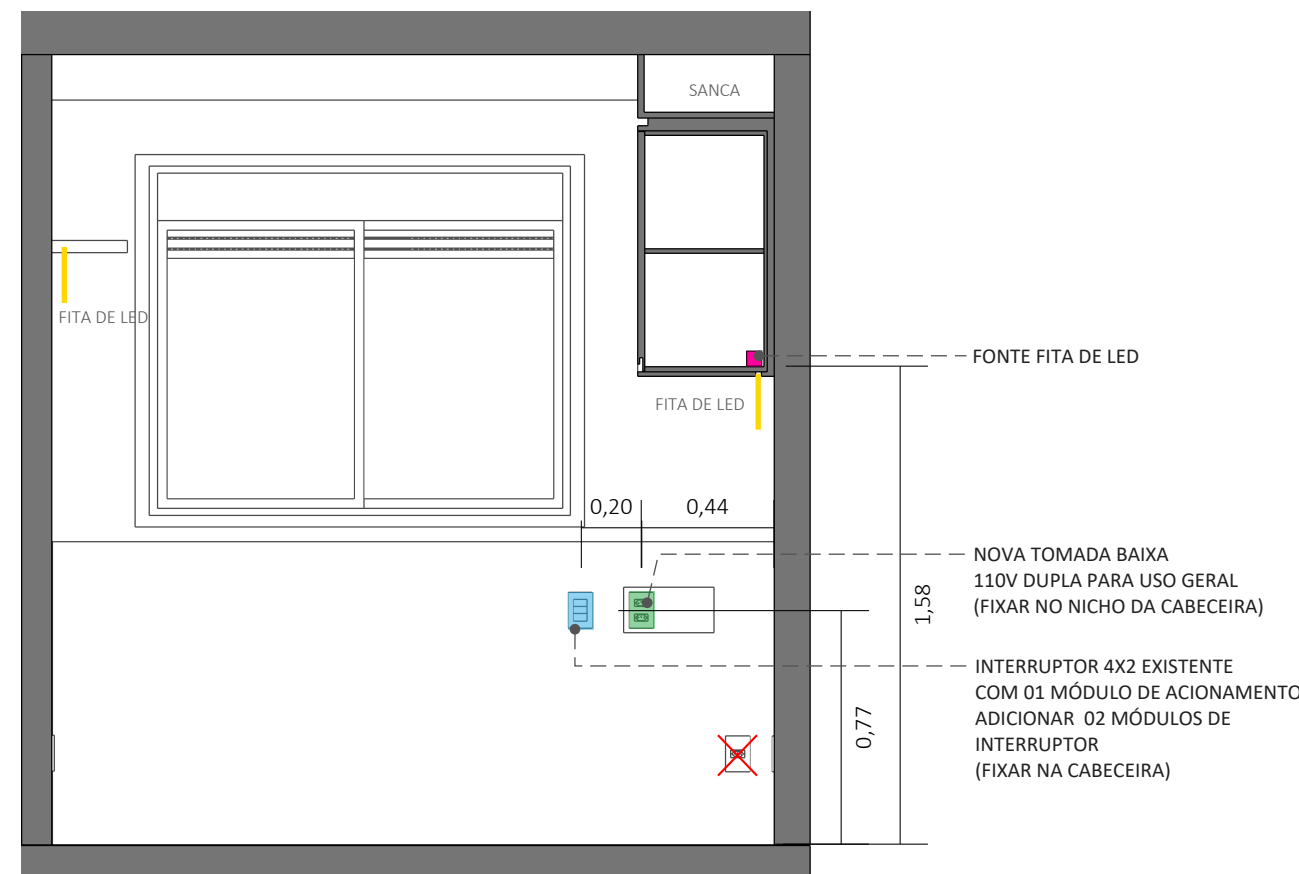

VISTA 09 - ELÉTRICA DORMITÓRIO 01
ESC. 1:25
OBS: CONFERIR AS MEDIDAS NO LOCAL

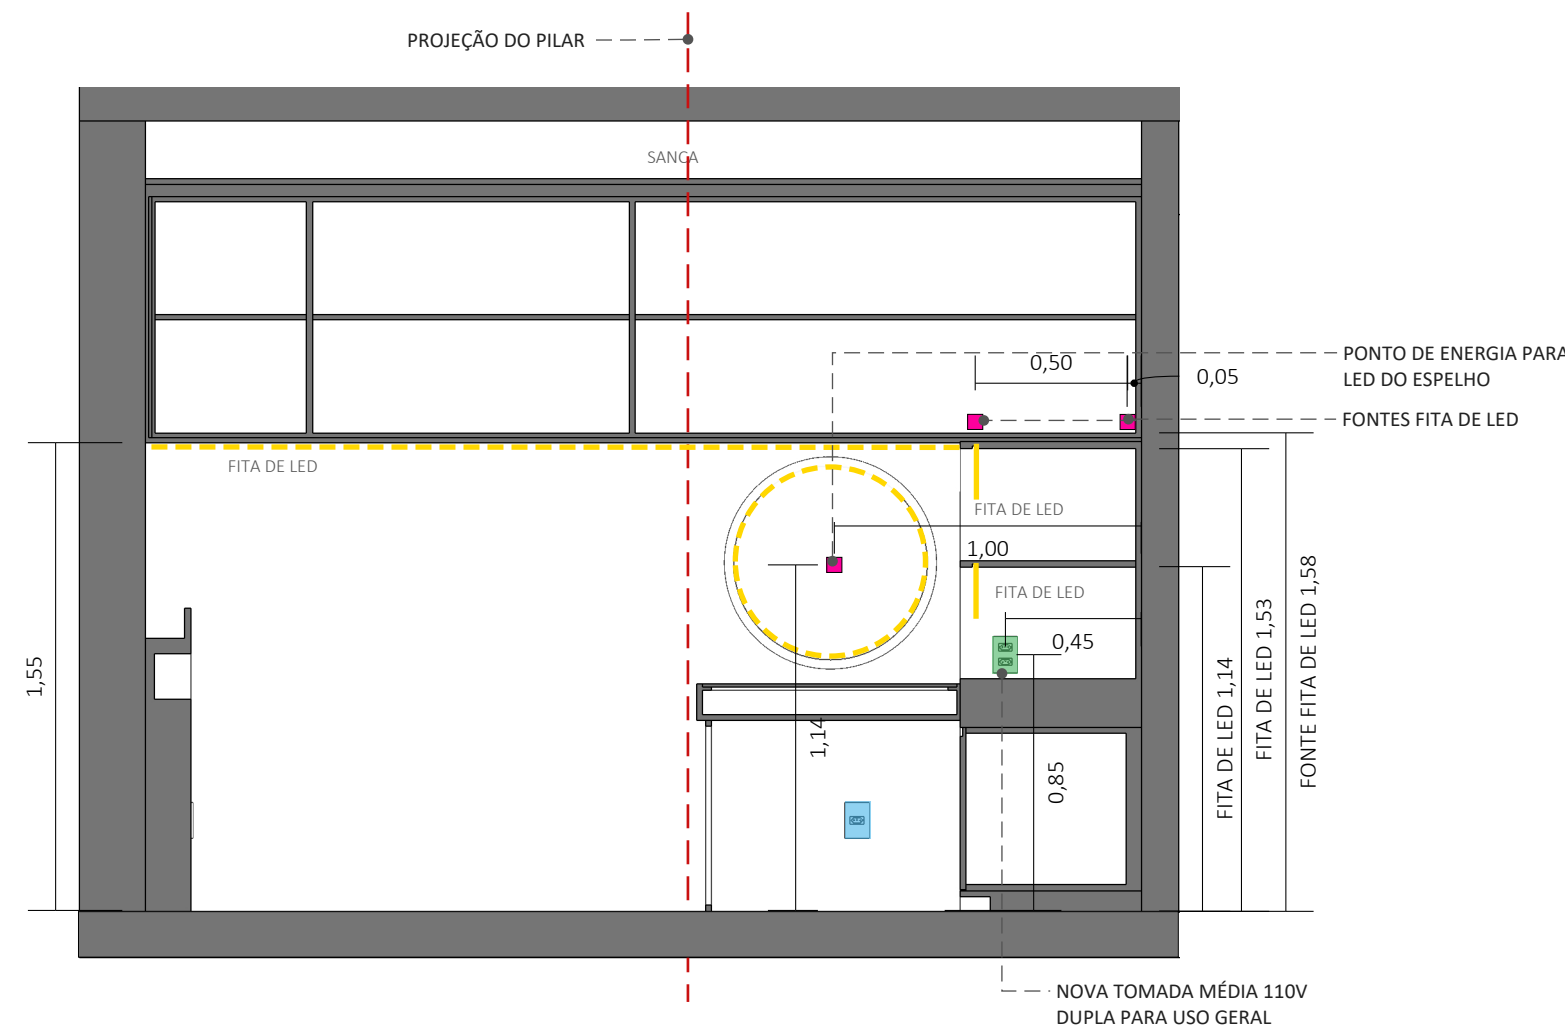

VISTA 10 - ELÉTRICA DORMITÓRIO 01
ESC. 1:25
OBS: CONFERIR AS MEDIDAS NO LOCAL

LEGENDA ALVENARIA ORIGINAL	
	ALVENARIA DE VEDAÇÃO
	ALVENARIA ESTRUTURAL
	CARENAGEM PARA PONTOS DE ÁGUA FRIA E ESGOTO
	EXAUSTÃO MECÂNICA
	FURO NA VIGA / PAREDE
	ENCHIMENTO
	VENTILAÇÃO PERMANENTE

PONTO EXISTENTE A SER **ANULADO OU REALOCADO**

LEGENDA ELÉTRICA - NOVOS PONTOS	
	TOMADA BAIXA 2P+T (127 V)
	TOMADA MÉDIA 2P+T (127 V)
	TOMADA ALTA 2P+T (127 V)
	TOMADA BAIXA 2P+T (220 V)
	PONTO ESPECÍFICO PARA INSTALAÇÃO DE AR CONDICIONADO OBS.: VERIFICAR AS ESPECIFICAÇÕES COM FORNECEDOR DO EQUIPAMENTO
	PONTO PARA TV
	PONTO PARA TELEFONE/INTERNET E LÓGICA
	PONTO PARA TELEFONE/INTERFONE INTERNO
	CAIXA DE PASSAGEM
	PONTO ELÉTRICO PARA FITA DE LED
	PONTO ENERGIZADO ACIMA DO FORRO PARA PERSIANAS MOTORIZADAS E COIFA (110V)
	INTERRUPTOR


LEGENDA ELÉTRICA - PONTOS EXISTENTES	
	TOMADA BAIXA 2P+T (127 V)
	TOMADA MÉDIA 2P+T (127 V)
	TOMADA ALTA 2P+T (127 V)
	TOMADA BAIXA 2P+T (220 V)
	PONTO PARA TV
	PONTO PARA TELEFONE/INTERFONE E LÓGICA
	PONTO PARA TELEFONE/INTERFONE INTERNO OBS.: ALTURA ESPECIFICADA EM PLANTA
	INTERFONE / CIGARRA
	INTERRUPTOR
	QUADRO DE SISTEMAS
	QUADRO DE LUZ E FORÇA
	PONTO PARA CONDENSADORA (AR CONDICIONADO)
OBSERVAÇÕES: 1) PARA MAIS DETALHES DE ELÉTRICA VER VISTAS DOS AMBIENTES. . 2) EM CASO DE CONSTRUÇÃO EM ALVENARIA ESTRUTURAL: OS NOVOS PONTOS DE ELÉTRICA INDICADOS DEVEM SER PASSADOS POR FORRO DE GESSO, MARCENARIA OU DRYWALL.	

OBSERVAÇÕES GERAIS:
- PREVER REFORÇOS EM PAREDES E FORRO/TETO QUANDO NECESSÁRIO, PRINCIPALMENTE EM DRYWALL
- PONTOS DE GÁS: SEGUIR SEMPRE AS NORMAS TÉCNICAS E DEIXAR REGISTROS COM ACESSO FACILITADO

OBS.: CONFERIR TODAS AS MEDIDAS IN LOCO, INCLUINDO MODELOS DE ELETROS, LOUÇAS E METAIS

- Medidas em metros.


- Desenho de propriedade de LOFT7 ARQUITETURA: Todos os direitos reservados, é vedada cópia, reprodução ou utilização das informações constantes neste documento sem a autorização por escrito dos autores.

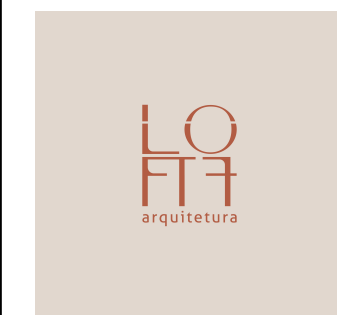


ARQUITETA
NATHÁLIA SIMÕES

ALAMEDA GRAJAÚ, 60 -
BARUERI, SP.
(11) 99778-9234

DESENHO	PROJETO EXECUTIVO
ASSUNTO	PROJETO CIVIL
LOCAL	RUA APA, Nº 164 – APARTAMENTO 815, CAMPOS ELÍSEOS, SÃO PAULO CEP.: 01201-030
ESCALA	1:25
PROJETO	TF815 THAYANE LINHARES
DATA	13/06/25
REVISÃO	R00

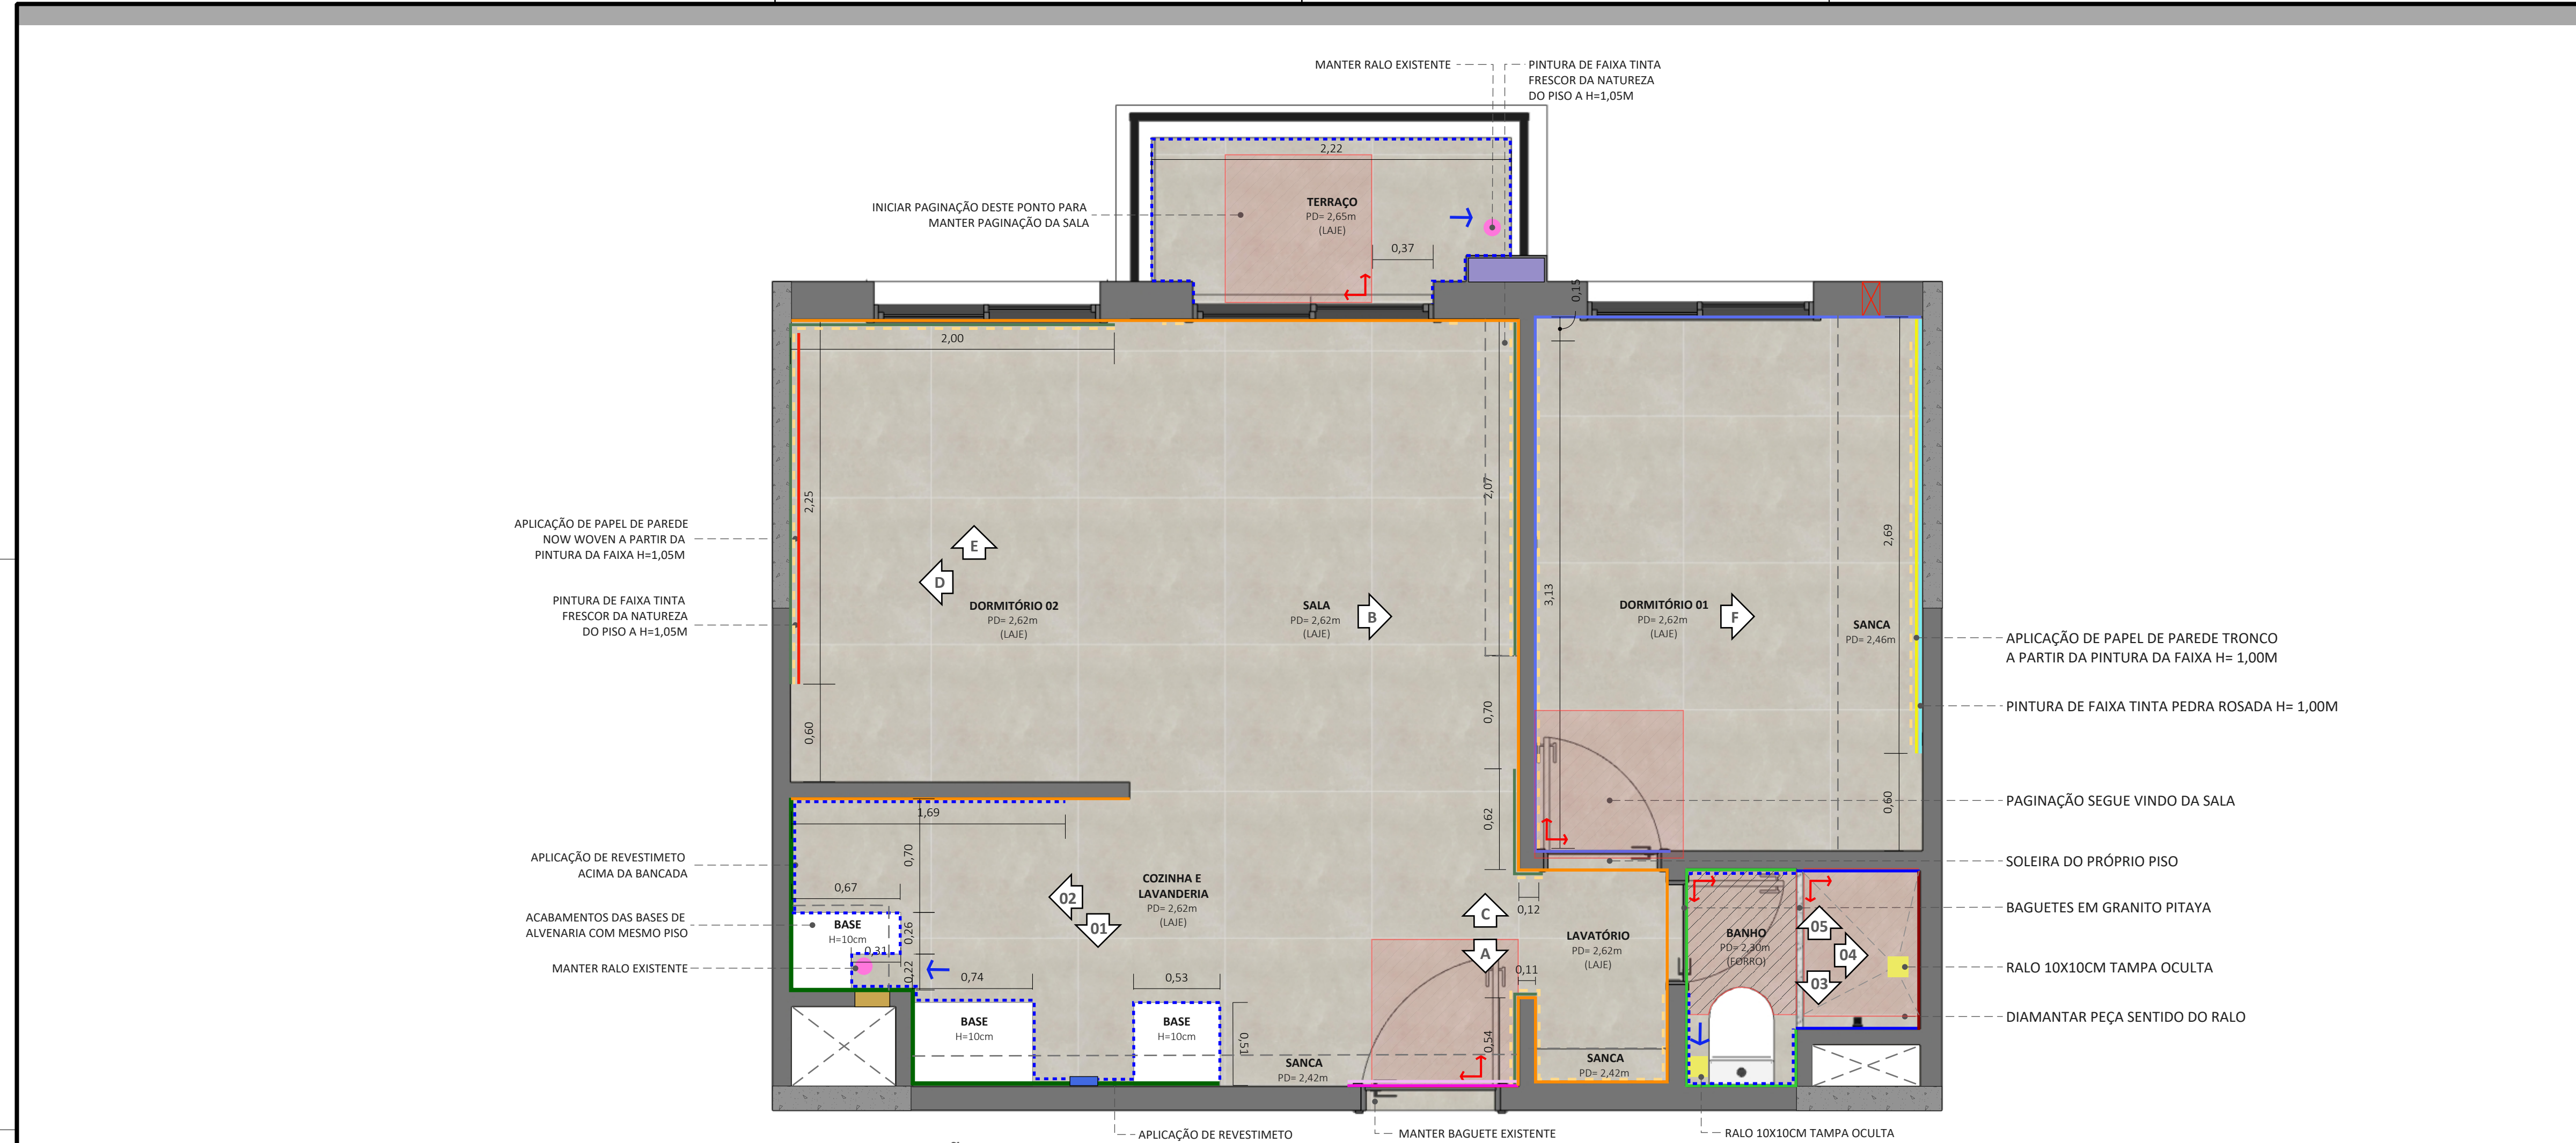

PLANTA PAGINAÇÃO
esc. 1:25
OBS: CONFERIR AS MEDIDAS NO LOCAL
OBS: BASE DE ALVENARIA DIMENSÃO ACABADA (COM REVESTIMENTO)

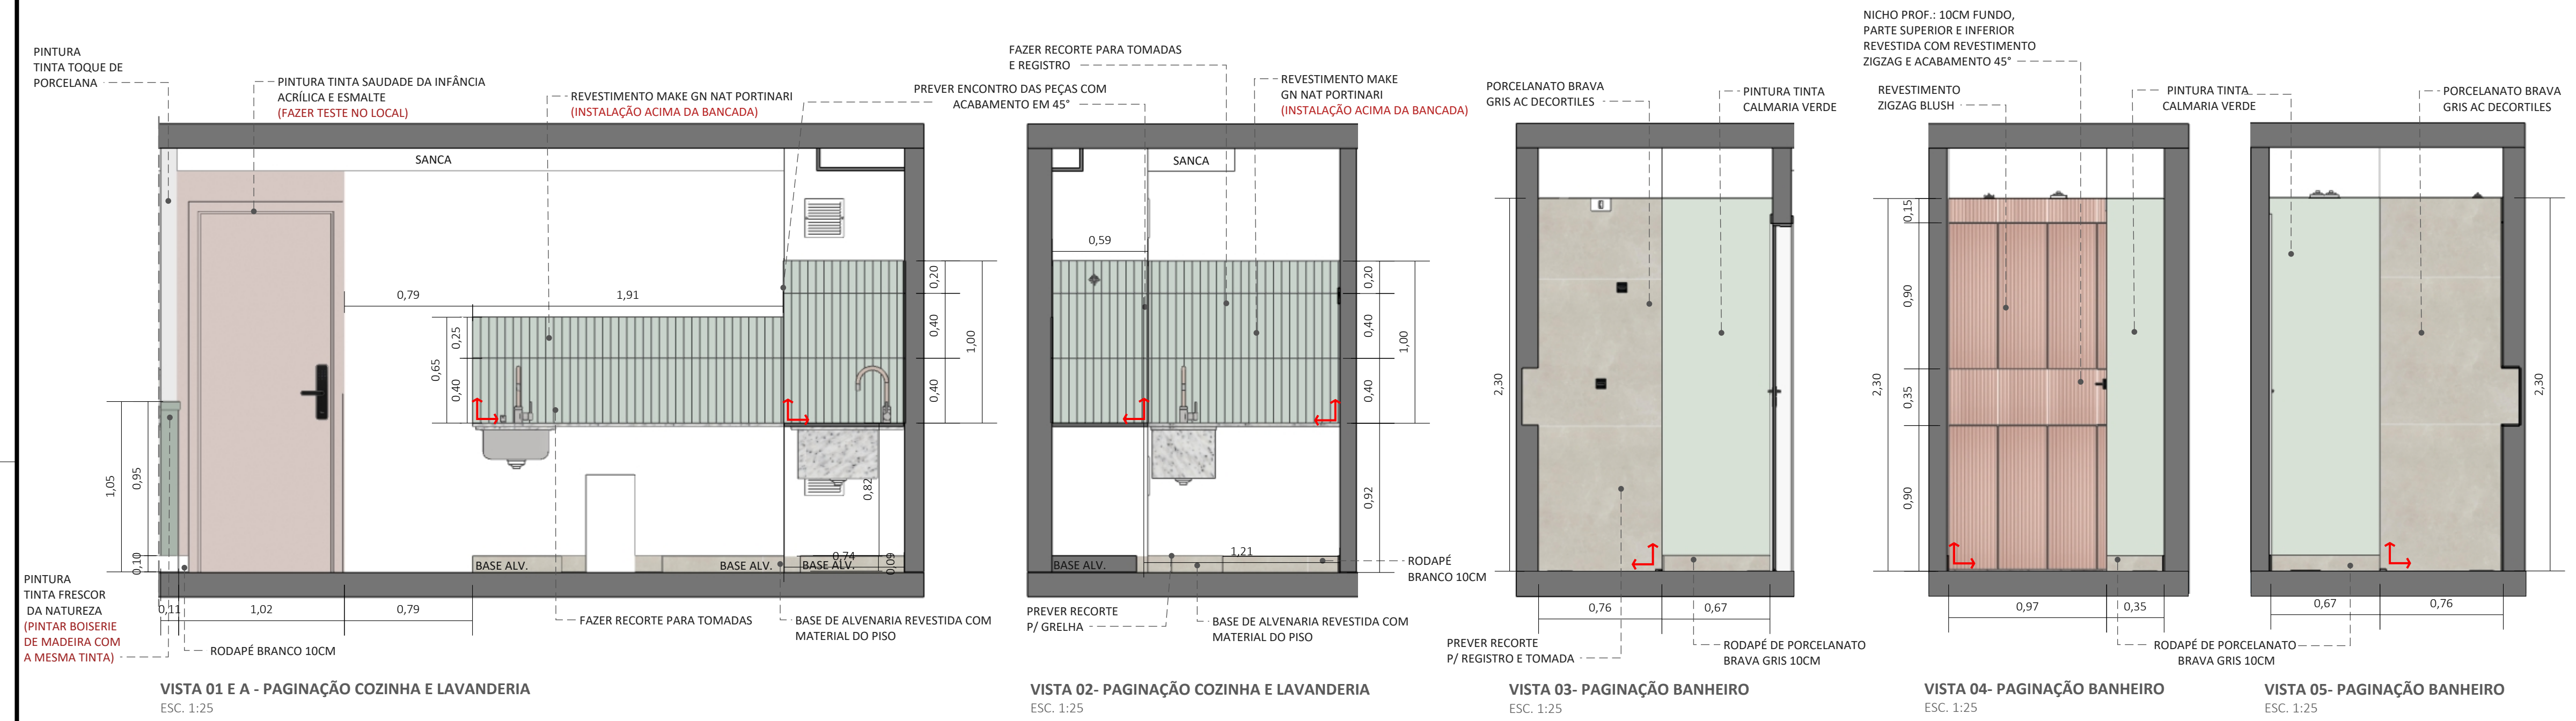

LEGENDA ALVENARIA ORIGINAL	
	ALVENARIA DE VEDAÇÃO
	ALVENARIA ESTRUTURAL
	CARENAGEM PARA PONTOS DE ÁGUA FRIA E ESGOTO
	EXAUSTÃO MECÂNICA
	FURO NA VIGA / PAREDE
	ENCHIMENTO
	VENTILAÇÃO PERMANENTE

LEGENDA PAGINAÇÃO	
	SENTIDO DE INÍCIO DA PAGINAÇÃO
	INDICAÇÃO SENTIDO DE CAÍDA DE PISO
	RALO - TAMPA INOX CONVENCIONAL
	RALO OCULTO - TAMPA PORCELANATO

	INDICAÇÃO DE VISTA PARA PAPEL DE PAREDE E PINTURAS ESPECIAIS
	INDICAÇÃO DE VISTA PARA REVESTIMENTOS

REVESTIMENTOS UTILIZADOS	
	PORCELANATO BRAVA GRIS AC 90x90CM DECORTILES QUANTIDADE (SEM PERCA): 53 PEÇAS + 15,02 METROS LINEARES PARA RODAPÉ 10cm (CERCA DE 2 PEÇAS) TOTAL: 55 PEÇAS QUANTIDADE DE COMPRA: 61 PEÇAS / 31 CAIXAS (55 PEÇAS USO + 5% PERCA + 5% DE SOBRA) (02 PEÇA POR CAIXA) REJUNTE INDICADO: CINZA PLATINA
	REVESTIMENTO MAKE GN NAT 5x40CM PORTINARI QUANTIDADE (SEM PERCA): 231 PEÇAS QUANTIDADE DE COMPRA: 254 PEÇAS / 26 CAIXAS (231 PEÇAS USO + 5% PERCA + 5% DE SOBRA) (10 PEÇAS POR CAIXA) REJUNTE INDICADO: HORTELÃ
	REVESTIMENTO ZIGZAG BLUSH 30x90CM PORTOBELLO QUANTIDADE (SEM PERCA): 10 PEÇAS QUANTIDADE DE COMPRA: 10 OU 15 PEÇAS / 2 OU 3 CAIXAS (CADA CAIXA SÃO 5 PEÇAS, COMPRAR 2 CAIXAS E SE NECESSÁRIO + 1) (5 PEÇAS POR CAIXA) REJUNTE INDICADO: BEGE ROSA OU MARFIM
	RODAPÉ BRANCO LISO POLIESTIRENO 10CM QUANTIDADE (SEM PERCA): 15,00m.l. QUANTIDADE DE COMPRA: 19,2m.l. / 8 BARRAS DE 2,40 CADA UTILIZAR COLA PU

LEGENDA TINTAS E PAPEL DE PAREDE	
	PINTURA COM TINTA ACRÍLICA FOSCA TOQUE DE PORCELANA - SUVINIL
	PINTURA COM TINTA ACRÍLICA FOSCA SAUDE DA INFÂNCIA- CORAL (FAZER TESTE DE TINTA PARA DEFINIR A COR NO LOCAL COM A MARCENARIA)
	PINTURA COM TINTA ESMALTE SAUDE DA INFÂNCIA- CORAL (FAZER TESTE DE TINTA PARA DEFINIR A COR NO LOCAL COM A MARCENARIA)
	PINTURA COM TINTA ACRÍLICA FOSCA CALMARIA VERDE- CORAL
	PINTURA COM TINTA ACRÍLICA FOSCA FRESCOR DA NATUREZA - SUVINIL
	PINTURA COM TINTA ACRÍLICA FOSCA BERÇO- SUVINIL
	PINTURA COM TINTA ACRÍLICA FOSCA PEDRA ROSADA- SUVINIL
	PAPEL DE PAREDE NOW WOVEN (3,51M²)
	PAPEL E PAREDE TRONCO BEGE - BRANCO CASA (1,40M²)

OBS: - REALIZAR TESTES DE COR NO LOCAL;
- QUANTITATIVOS DE PAPEL DE PAREDE SEM PERCA;
- CONFERIR COR DO REJUNTE COM PEDIDO DO REVESTIMENTO;
- CONSIDERAR ACABAMENTO NAS QUINAS EM 45° GRAUS;
- SEGUIR INSTALAÇÃO/ ESPACAMENTO MÍNIMO INDICADO PELO FABRICANTE;
- MANTER LOCALIZAÇÃO DOS RALOS EXISTENTES.

PAPEL DE PAREDE NOW WOVEN A: 3,51M² (DORMITÓRIO 02)	PAPEL E PAREDE TRONCO BEGE - BRANCO CASA A: 1,40M² (DORMITÓRIO 01)

OBSERVAÇÕES GERAIS:
- PREVER REFORÇOS EM PAREDES E FORRO/TETO QUANDO NECESSÁRIO, PRINCIPALMENTE EM DRYWALL
- PONTOS DE GÁS: SEGUIR SEMPRE AS NORMAS TÉCNICAS E DEIXAR REGISTROS COM ACESSO FACILITADO
OBS.: CONFERIR TODAS AS MEDIDAS IN LOCO, INCLUINDO MODELOS DE ELETROS, LOUÇAS E METAIS

- Medidas em metros.
- Desenho de propriedade de LOFT7 ARQUITETURA: Todos os direitos reservados, é vedada cópia, reprodução ou utilização das informações constantes neste documento sem a autorização por escrito dos autores.

 ARQUITETA NATHÁLIA SIMÕES ALAMEDA GRAJAÚ, 60 - BARUERI, SP. (11) 99778-9234	DESENHO	PROJETO EXECUTIVO
	ASSUNTO	PROJETO CIVIL
	LOCAL	RUA APA, Nº 164 – APARTAMENTO 815, CAMPOS ELÍSEOS, SÃO PAULO CEP.: 01201-030
	ESCALA	1:25
	PROJETO	TF815 THAYANE LINHARES
	DATA	24/06/25
	REVISÃO	R00
	01 / 02	

LEGENDA PAGINAÇÃO	
	SENTIDO DE INÍCIO DA PAGINAÇÃO
	INDICAÇÃO SENTIDO DE CAÍDA DE PISO
	RALO -TAMPA INOX CONVENCIONAL
	RALO OCULTO -TAMPA PORCELANATO



OBS: - REALIZAR TESTES DE COR NO LOCAL;

- QUANTITATIVOS DE PAPEL DE PAREDE SEM PERCA;
- CONFERIR COR DO REJUNTE COM PEDIDO DO REVESTIMENTO;
- CONSIDERAR ACABAMENTO NAS QUINAS EM 45° GRAUS;
- SEGUIR INSTALAÇÃO/ ESPAÇAMENTO MÍNIMO INDICADO PELO FABRICANTE;
- MANTER LOCALIZAÇÃO DOS RALOS EXISTENTES.

FERIR TODAS AS MEDIDAS IN LOCO, INCLUINDO MODELOS DE ELETROS, LOU

de propriedade de LOFT7 ARQUITETURA: Todos os direitos reservados, e
ou utilização das informações constantes neste documento sem a au-
escrito dos autores.

02 / 02