


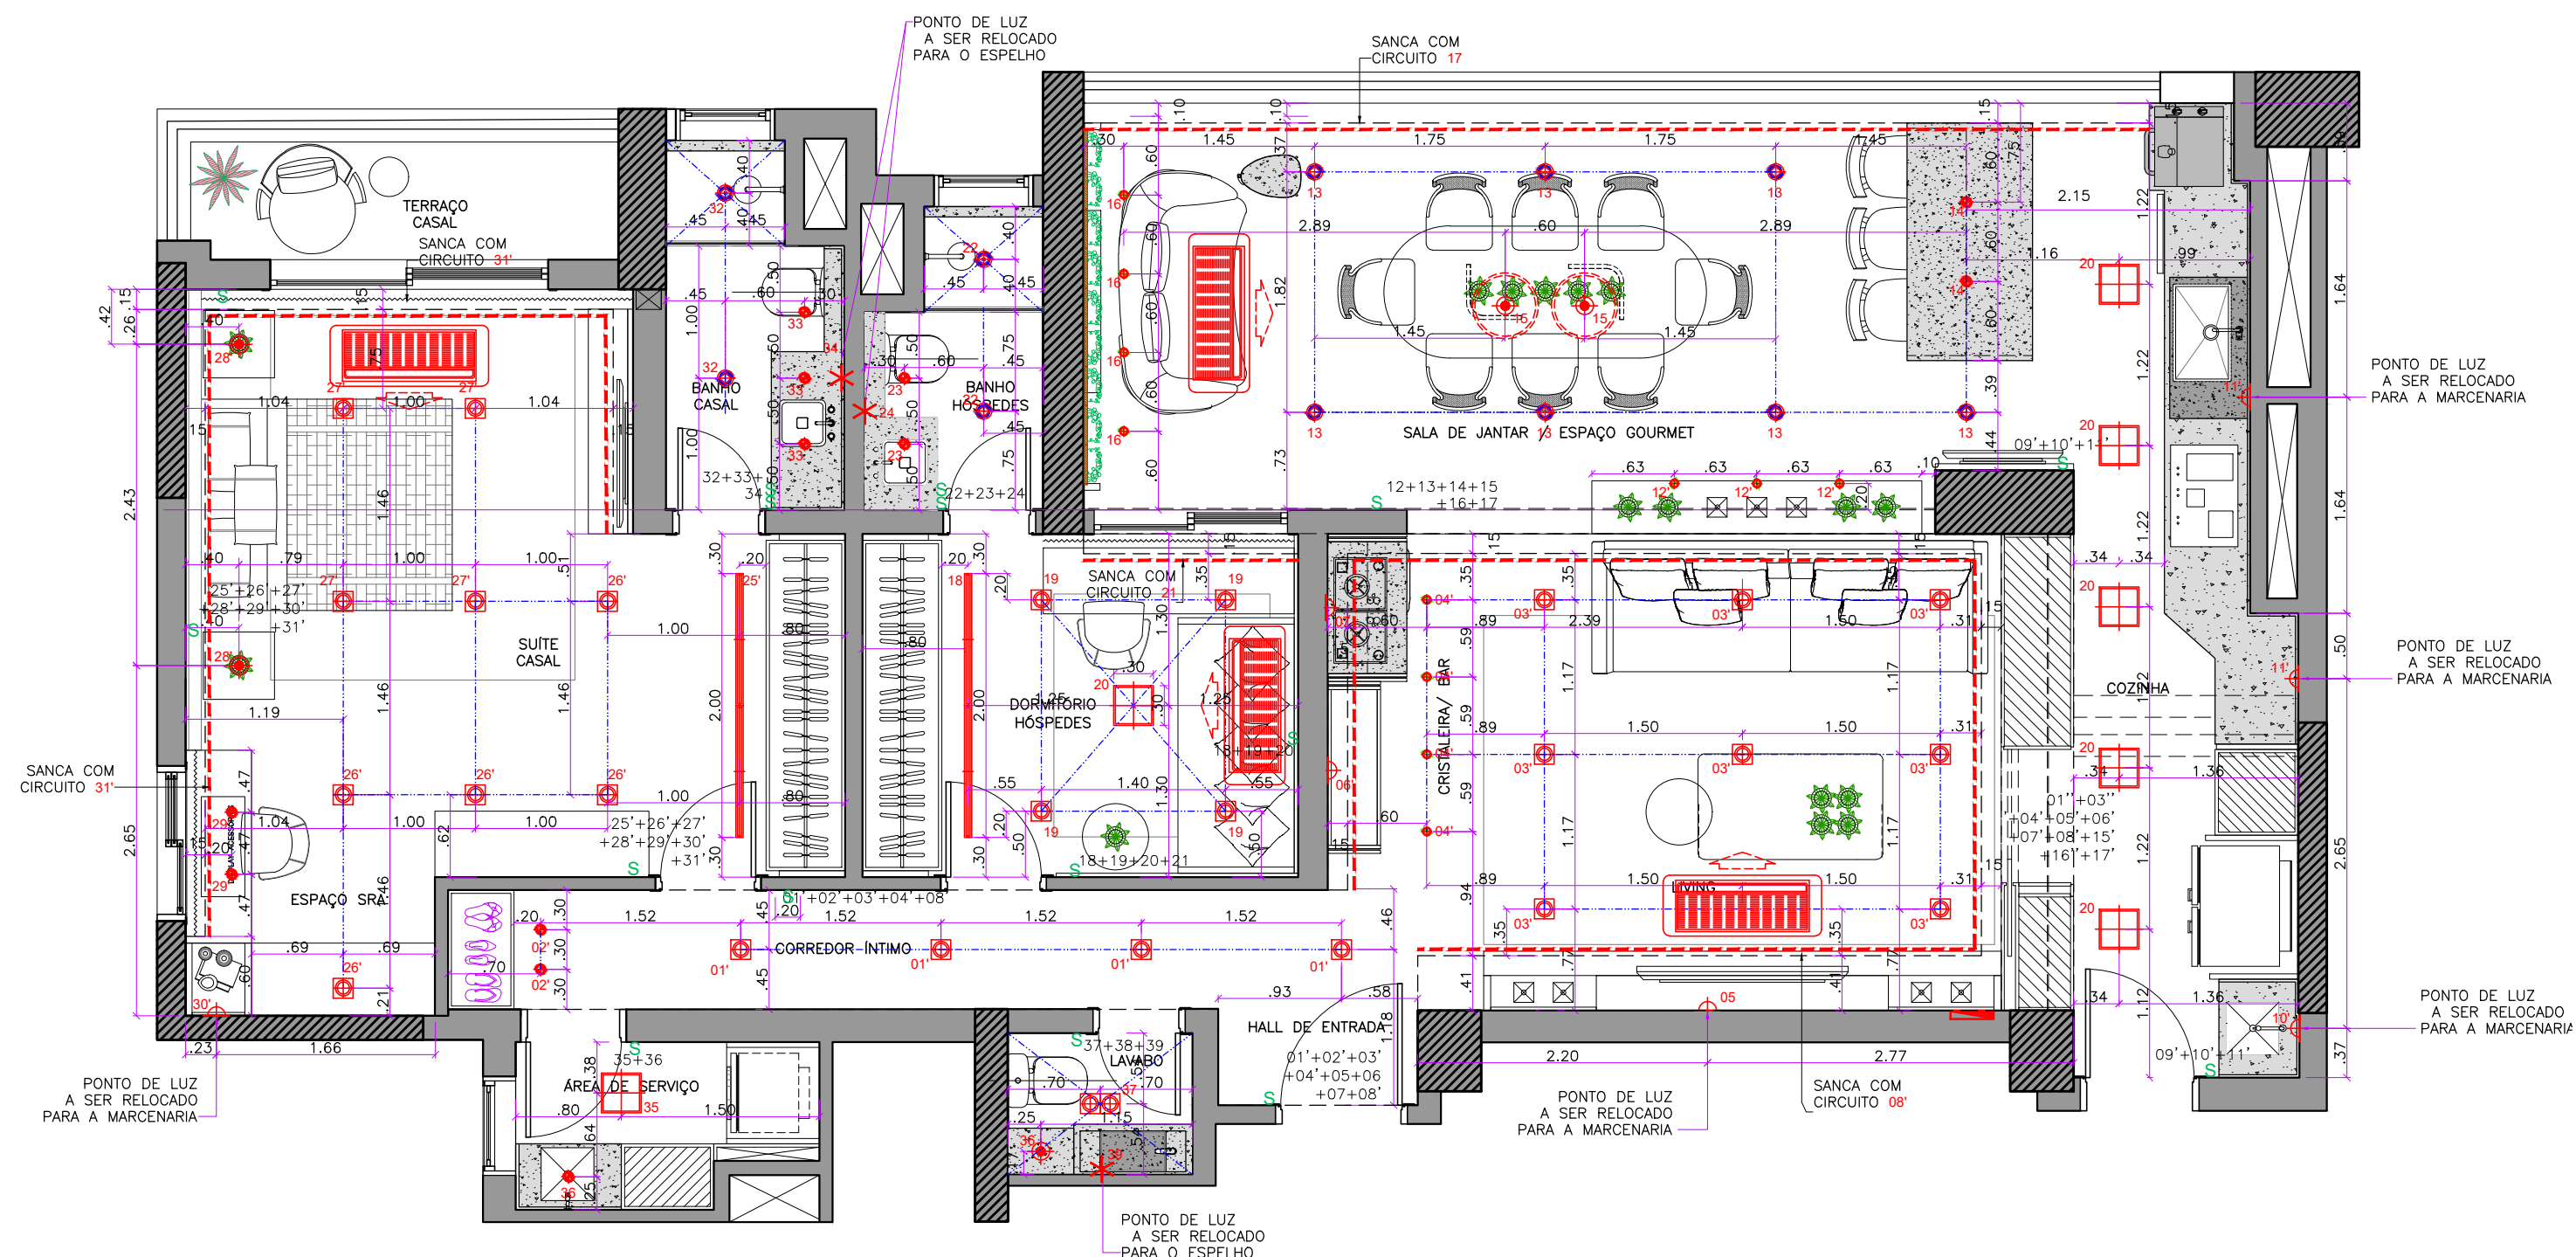

PLANTA DE ILUMINAÇÃO
esc 1:50

TABELA DE ILUMINAÇÃO	
LEGENDA dos SIMBOLOS: (medidas de eixo)	
	PONTO PARA LUMINÁRIA EMBUTIDA (MINI DICRÓICA/LED)
	PONTO PARA LUMINÁRIA EMBUTIDA (DICRÓICA/LED)
	PONTO PARA LUMINÁRIA EMBUT. QUADRADA (AR 70/LED)
	PONTO PARA LUMINÁRIA EMBUTIDA (PAR 20/LED)
	PONTO PARA LUMINÁRIA PENDENTE DECORATIVO
	PONTO DE LUZ MARCENARIA(H=VIDE PROJETO MARCENARIA)
	PONTO PARA LUMINÁRIA (PLAFON ILUMINAÇÃO REBATIDA)
	PONTO P/ LUMI. EMBUT. (PERFIL DE LED DE 2000x35mm)
	ILUMINAÇÃO EMBUTIDA NA SANCA DE GESSO (FITA LED)
	PONTO PARA AUTO FALANTE EMBUTIDO NO GESSO
	PONTO DE LUZ PARA ESPELHO

TABELA DE ILUMINAÇÃO	
LEGENDA dos SIMBOLOS:	
	INTERRUPTOR

02	08/06/25	REVISÃO
01	02/06/25	REVISÃO
00	26/05/25	EMIÇÃO INICIAL

TFZ
THAIS ZICATTI
ARQUITETURA & DECORAÇÃO

ALPHAVILLE – SANTANA DE PARNAÍBA – SP
FONE: 11 99565–7566
tfz.arq@gmail.com
instagram: tfzarquitetura

CHECAR MEDIDAS NO LOCAL

OBRA	
PROJETO DE ARQUITETURA E INTERIORES	
LOCAL	
RUA FORTUNATO FERRAZ 280–APTO 181– TORRE 02 VILA ANASTÁCIO – LAPA – SP	
CLIENTE	
SRA. VALDIRENE CARDOSO	

ASSUNTO			FOLHA Nº
VALDIRENE CARDOSO_LAPA_EX_06_REV_02 PLANTA ILUMINAÇÃO			EX_06
DESENHO	DATA	ESCALA	REVISÃO
THAIS	08/06/25	1:50	REV_02