


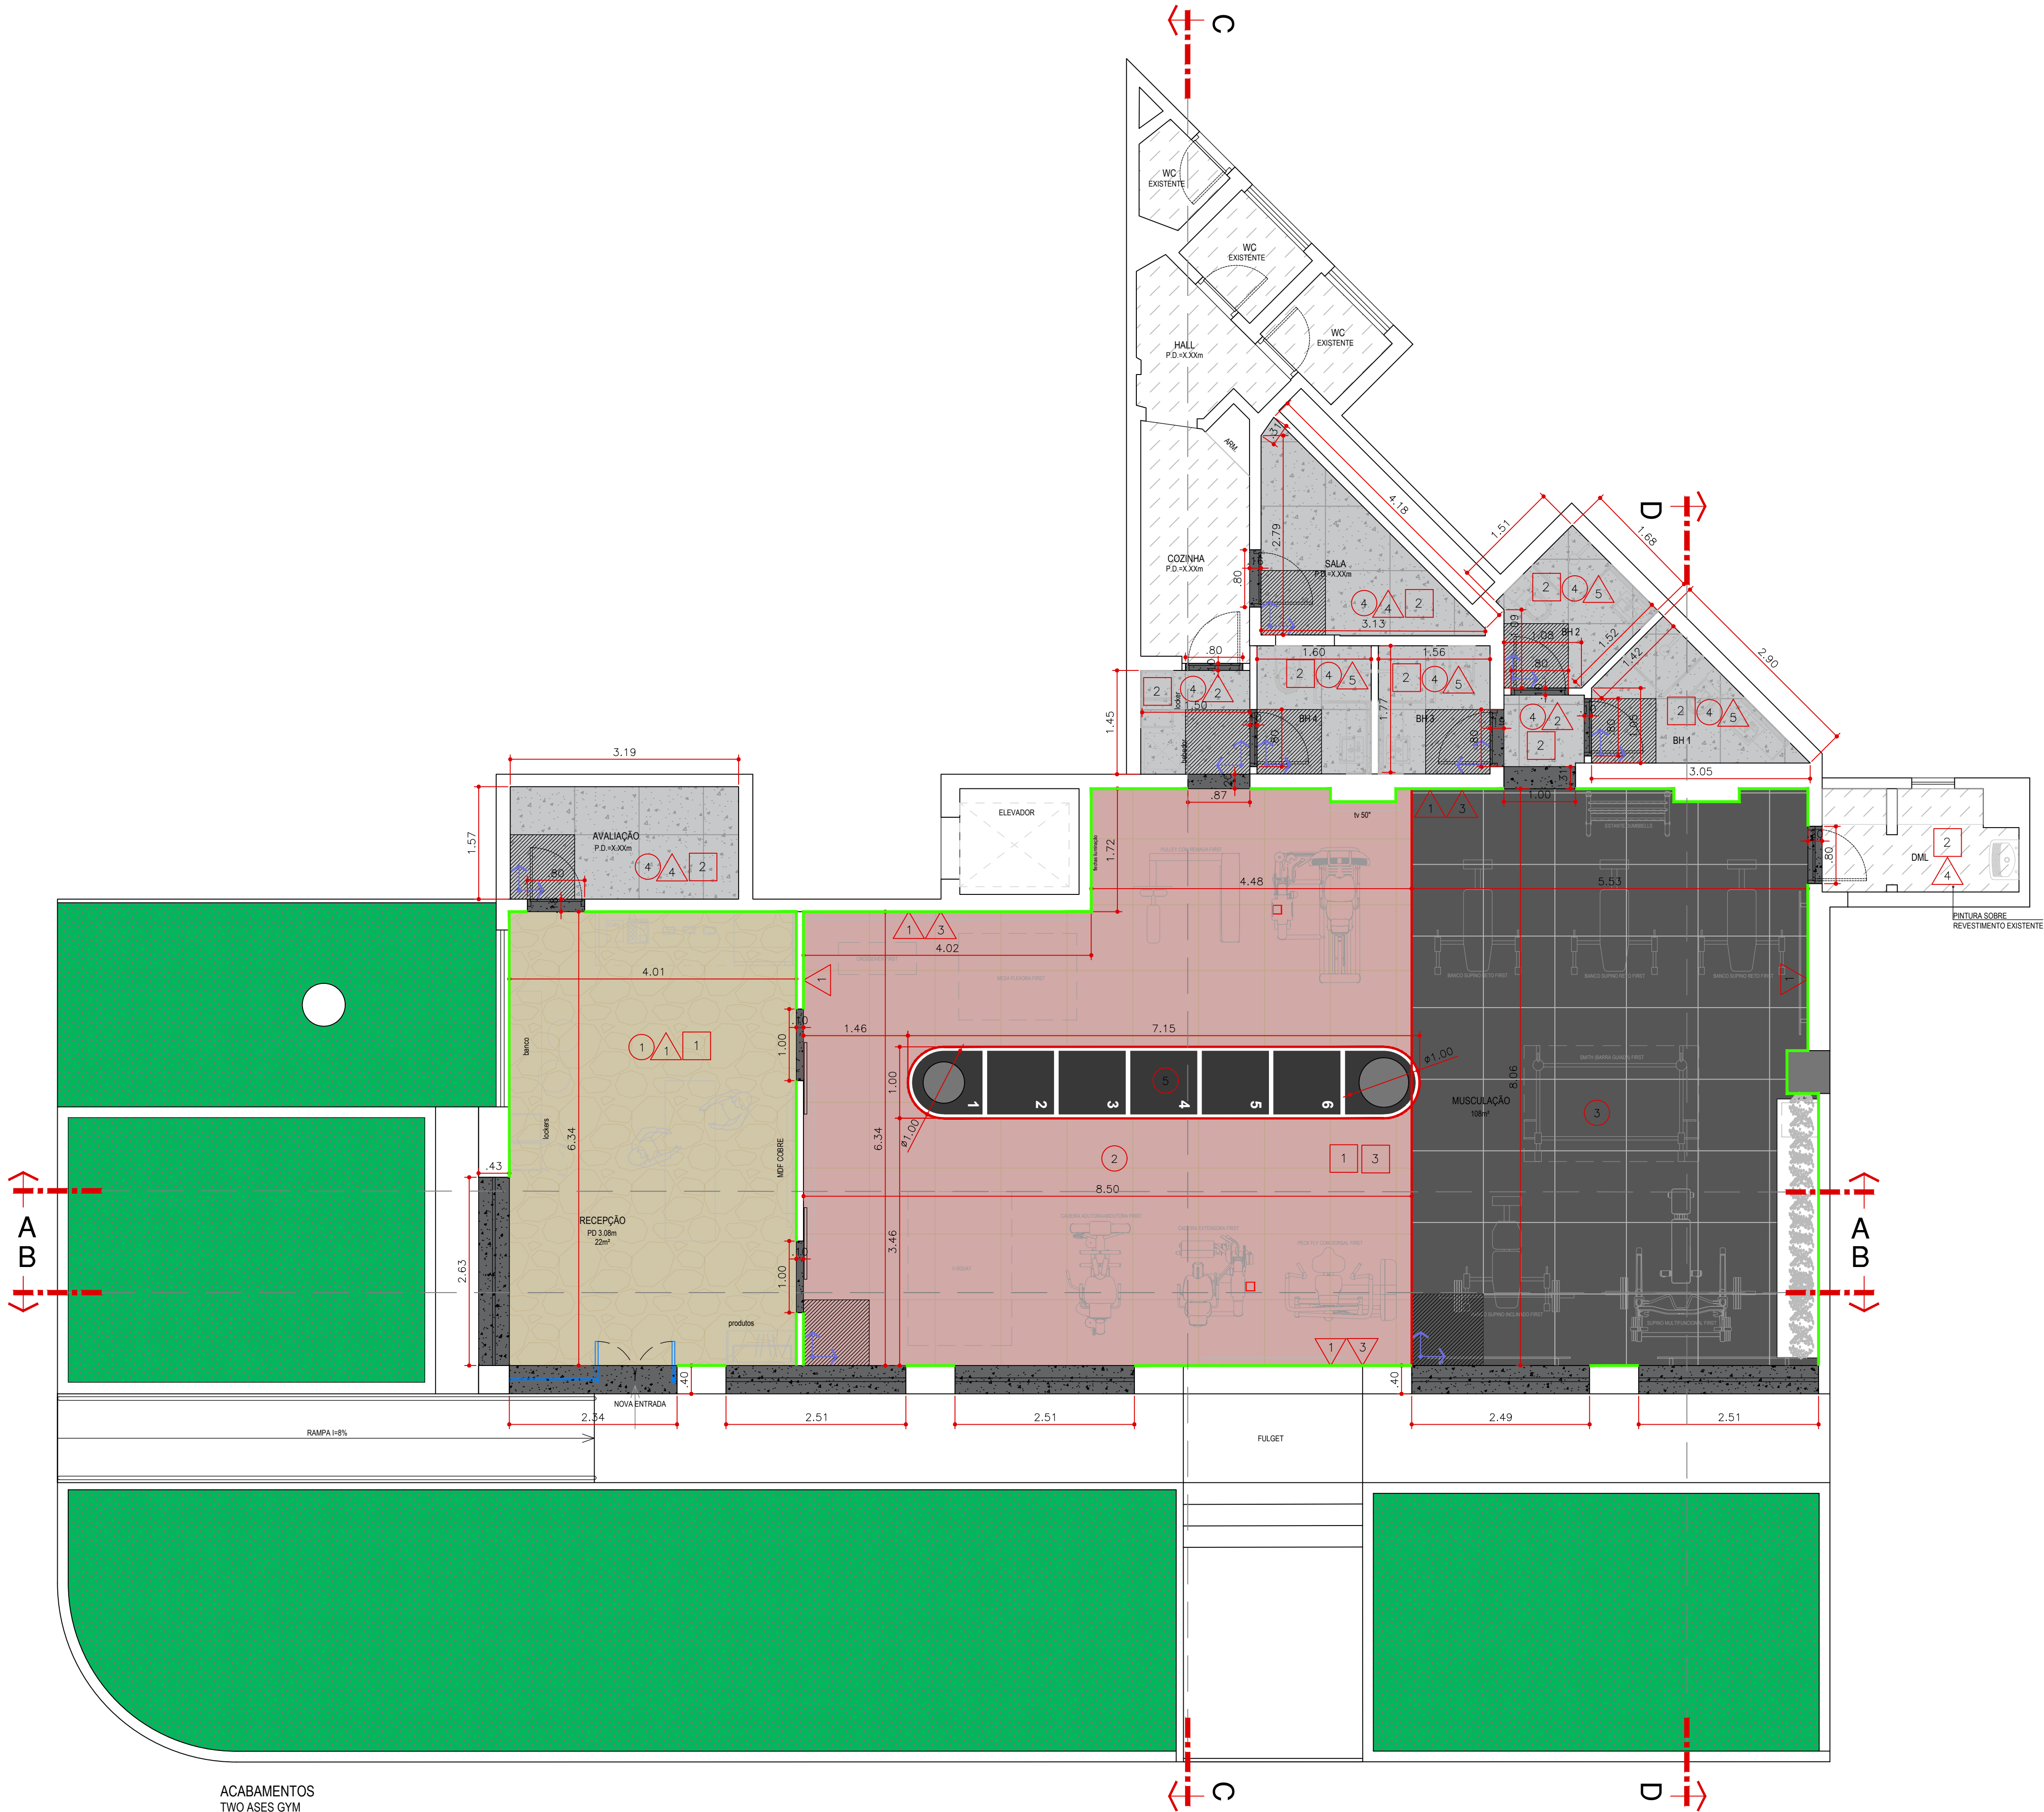

ACABAMENTOS
TWO ASES GYM
UNID ANGÉLICA
ESCALA 1:50

LEGENDA		
↔ Início de paginação → Continuar paginação do ambiente vizinho		
ACABAMENTOS		
PISO		
1		PISO ORGÂNICO QUARTZITO - COLORMIX - 28m²
2		PISO VINÍLICO ACERO - TARKETT 92x92 - 60m²
3		PISO EMBORRAVHADO PRETO 1x1 PLACAS DE 15mm DE ESPESURA - 47m²
4		PORCELANATO MOSS GRAY - PORTOBELLO 90x90 - 29m²
5		PISTA DE CORRIDA EM PISO EMBORRACHADO DE ROLO 5mm COM MARCAÇÕES EM PINTURA EPOXI OU ADESIVO - 8m²
6		MANTER EXISTENTE
		SOLEIRA GRANITO SÃO GABRIEL - 28m
		RODAPE SANTA LUZIA PRETO 7cm - 47m
		PERFIL DE ARREMATE PARA PISOS VINÍLICOS EM T COM 3.3CM DE LARGURA E 1MM DE ESPESURA - 28m
PAREDE		
1		PINTURA EFEITO AÇO CORTEN - KIT MAZA CORTEN - MAZA (SEGUIR INSTRUÇÕES DO FABRICANTE)
2		PINTURA EFEITO CIMENTO QUEIMADO TÚNEL DE CONCRETO SUVINIL
3		RIPADO EM METALON PRETO (VER MEDIDAS EM PROJETO)
4		PINTURA CALOPSITA - SUVINIL
5		PORCELANATO MOSS GRAY - PORTOBELLO 90x90
FORRO		
1		PINTURA CINZA ESCURO NANQUIM SUVINIL
2		PINTURA BRANCO PURO SUVINIL
3		ESTRUTURA TUBO METALON QUADRADO 3x3cm - PINTURA PRETO

OBS:
1. ACABAMENTOS ACRESCIDOS COM 10% DE PERDA

DATA	ALTERAÇÕES	RESPONSÁVEL
27/06/2025	EMISSION INICIAL	RAQUEL
		COORDENADOR: ARQTA. RAQUEL KABBANI
		DESENHO: Arq. RAQUEL KABBANI
		FASE: EXECUTIVO
DATA: JUNHO/2025	CLIENTE: TWO ASES GYM	ESPECIALIDADE: ARQUITETURA
ESCALA: 1:50	LOCAL: UNIDADE AV. ANGELICA	FOLHA: 007
DIMENSÕES: METROS	TÍTULO: ACABAMENTOS	REVISÃO: 01