


LEGENDA DE PONTOS HIDRÁULICOS EXISTENTES

	RALO SIMPLES D=0,10m
	PONTO DE ÁGUA FRIA (AF)
	PONTO DE ÁGUA QUENTE (AQ)
	PONTO DE GÁS
	PONTO DE ESGOTO(ESG)

LEGENDA DE PONTOS ELÉTRICOS EXISTENTES

TOMADA BAIXA 110V	PLACA CEGA
TOMADA BAIXA 220V	USB
TOMADA MÉDIA 110V	REDE
TOMADA MÉDIA 220V	TV
TOMADA INDICADA 110V	TELEFONE
TOMADA INDICADA 220V	INTERFONE
QUADRO DE ENERGIA	BOTÃO DA CAMPAINHA
QUADRO DE REDE	CAMPAINHA
CAIXINHA 4x2	INTERRUPTOR
CAIXINHA 4x4	

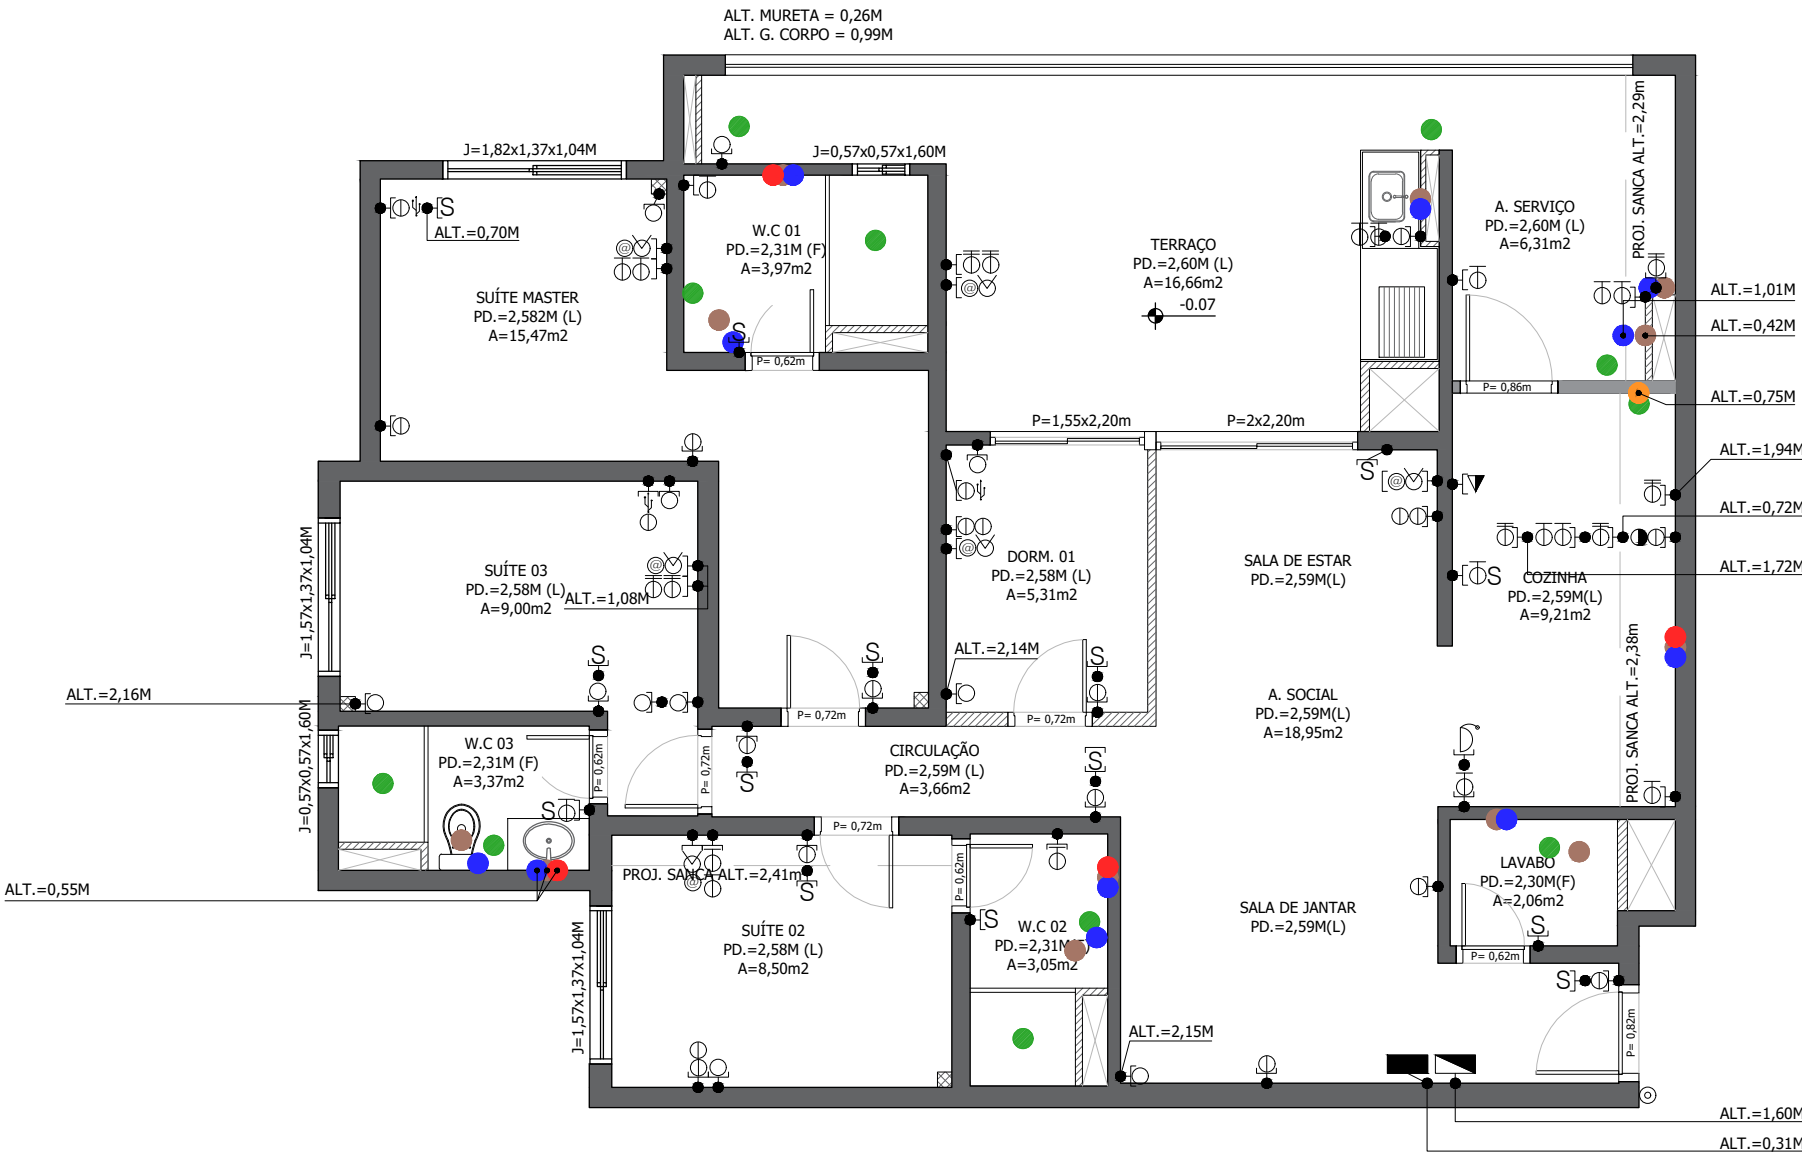

PLANTA BAIXA - LEVANTAMENTO TÉCNICO
ESC.: 1:75
ÁREA.:114,00m2

R02	01/07/2025	EMIÇÃO FINAL	JESSICA ALVES	VENILMA OLIVEIRA
R01	24/06/2024	EMIÇÃO FINAL	JESSICA ALVES	VENILMA OLIVEIRA
R00	06/03/2024	EMIÇÃO INICIAL	JESSICA ALVES	VENILMA OLIVEIRA
Nº de Revisão:	Data:	Descrição:	Responsável:	Desenhista:

Ciente:	ALEXANDRE E CÁTIA	Studio Mies arquitetura e interiores
Local:	RUA ANTÔNIO BLASQUES, Nº 122, AP 42 - TORRE A - FREGUESIA DO Ó - SÃO PAULO/SP	
Assunto:	LEVANTAMENTO TÉCNICO	
		Projeto: 91424-PRAC


DIREITOS RESERVADOS - LEI: 5772 DE 21/DEZEMBRO/1971. A ALTERAÇÃO SEM AUTORIZAÇÃO DE SEU AUTOR, FICARÁ SUJEITA AS MEDIDAS LEGAIS CABÍVEIS. A ALTERAÇÃO DESTA PROJETO EXIME SEU AUTOR DE QUAISQUER RESPONSABILIDADES POSTERIORES. TODO ESTE PROJETO FOI ELABORADO COM UNIDADE DE MEDIDAS EM M (METROS). TODAS AS MEDIDAS, ABERTURAS, PRUMOS E PÉ DIREITO, DEVEM SER CONFERIDAS NO LOCAL, ANTES DA REALIZAÇÃO DE QUALQUER ATIVIDADE. DEFINIÇÕES NÃO DESCRITAS OU DIVERGÊNCIAS ENCONTRADAS, DEVERÃO SER SUBMETIDAS A APROVAÇÃO DO COORDENADOR DO PROJETO ANTES DE ORÇAMENTOS E/OU EXECUÇÕES. ESTE PROJETO FOI CONFIGURADO EM FOLHA A3.	Fase: ☐ LT ☐ EP ☐ AP ☒ EX	Escala: 1:75 Revisão: 2	Folha: 01 16
--	---	----------------------------------	--------------------

	DEMOLIR PAREDE DE ALVENARIA 4,00m2 (NÃO ESTRUTURAL)
	DEMOLIR PAREDE DE DRYWALL 2,00m2 (VIDE PROJETO)
	DEMOLIR FORRO/SANCA DE GESSO 15,00m2 (VIDE PROJETO)
	RETIRAR BANCADA EM MARMORARIA 01 unid. DESCARTE
	DEMOLIR REVESTIMENTO PISO 42,00m2 (VIDE PROJETO)
	RETIRAR PORTA COMPLETA DE MADEIRA 01 unid. DESCARTE
	RETIRAR PORTA COMPLETA DE VIDRO E ALUMÍNIO 01 unid. DESCARTE
	RETIRAR PORTA BALCÃO DE VIDRO E ALUMÍNIO 02 unid. DESCARTE
	RETIRAR BAGUETE/SOLEIRA 13 unid.
	RETIRAR VASO SANITÁRIO 01 unid. DESCARTE
	RETIRAR CUBA DE LOUÇA E INOX 01 unid. DESCARTE
	RETIRAR RODAPÉ EM MDF 50,00m DESCARTE
	DEMOLIR REVESTIMENTO DE PAREDE 6,50m2
	RETIRAR FOLHA DE PORTA DE MADEIRA 07 unid. REUTILIZAR
	RETIRAR TORNEIRA/MISTURADOR 01 unid. DESCARTE
	FAZER A TROCA DO EXAUSTOR 02 unid. (VIDE PROJETO)


1. Prever a retirada de rodapé existente.

LAVABO, W.C MASTER, W.C 02, COZINHA: OS REVESTIMENTOS DE PISO E PAREDE, BANCADA, CUBAS, LOUÇAS E METAIS E BACIAS SANITÁRIAS SERÃO FORNECIDOS PELA CONSTRUTORA, PORÉM NÃO HAVERÁ A INSTALAÇÃO DOS MESMOS.

TERRAÇO E ÁREA DE SERVIÇO: OS REVESTIMENTOS DE PISO E PAREDE SERÃO FORNECIDOS PELA CONSTRUTORA, PORÉM NÃO HAVERÁ A INSTALAÇÃO DOS MESMOS.

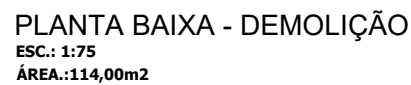

Cliente:	ALEXANDRE E CÁTIA	 arquitetura e interiores
Local:	RUA ANTÔNIO BLASQUES, Nº 122, AP 42 - TORRE A - FREGUESIA DO Ó - SÃO PAULO/SP	
Assunto:	DEMOLIÇÃO	
	Projeto:	91424-PRAC
DIREITOS RESERVADOS - LEI: 5772 DE 21/DEZEMBRO/1971. A ALTERAÇÃO SEM AUTORIZAÇÃO DE SEU AUTOR, FICARÁ SUJEITA AS MEDIDAS LEGAIS CABÍVEIS. A ALTERAÇÃO DESTA PROPOSTA ENTRA SEU AUTOR DE QUALQUER RESPONSABILIDADE POSTERIORES. TODOS ESTE PROJETO FOI ELABORADO COM UNIDADE DE MEDIDAS EM M (METROS). TODAS AS MEDIDAS, ABERTURAS, PRUMOS E PÉ DIREITO, DEVEM SER CONFERIDAS NO LOCAL, ANTES DA REALIZAÇÃO DE QUALQUER ATIVIDADE. DEFINIÇÕES NÃO DESCRITAS OU DIVERGÊNCIAS ENCONTRADAS, DEVERÃO SER SUBMETIDAS À APROVAÇÃO DO COORDENADOR DO PROJETO ANTES DE ORÇAMENTOS E/OU EXECUÇÕES. ESTE PROJETO FOI CONFIGURADO EM FOLHA A3.		
Fase:		Escala:
☐ LT		1:75
☐ EP		Revisão:
☐ AP		2
☒ EX		02 / 16

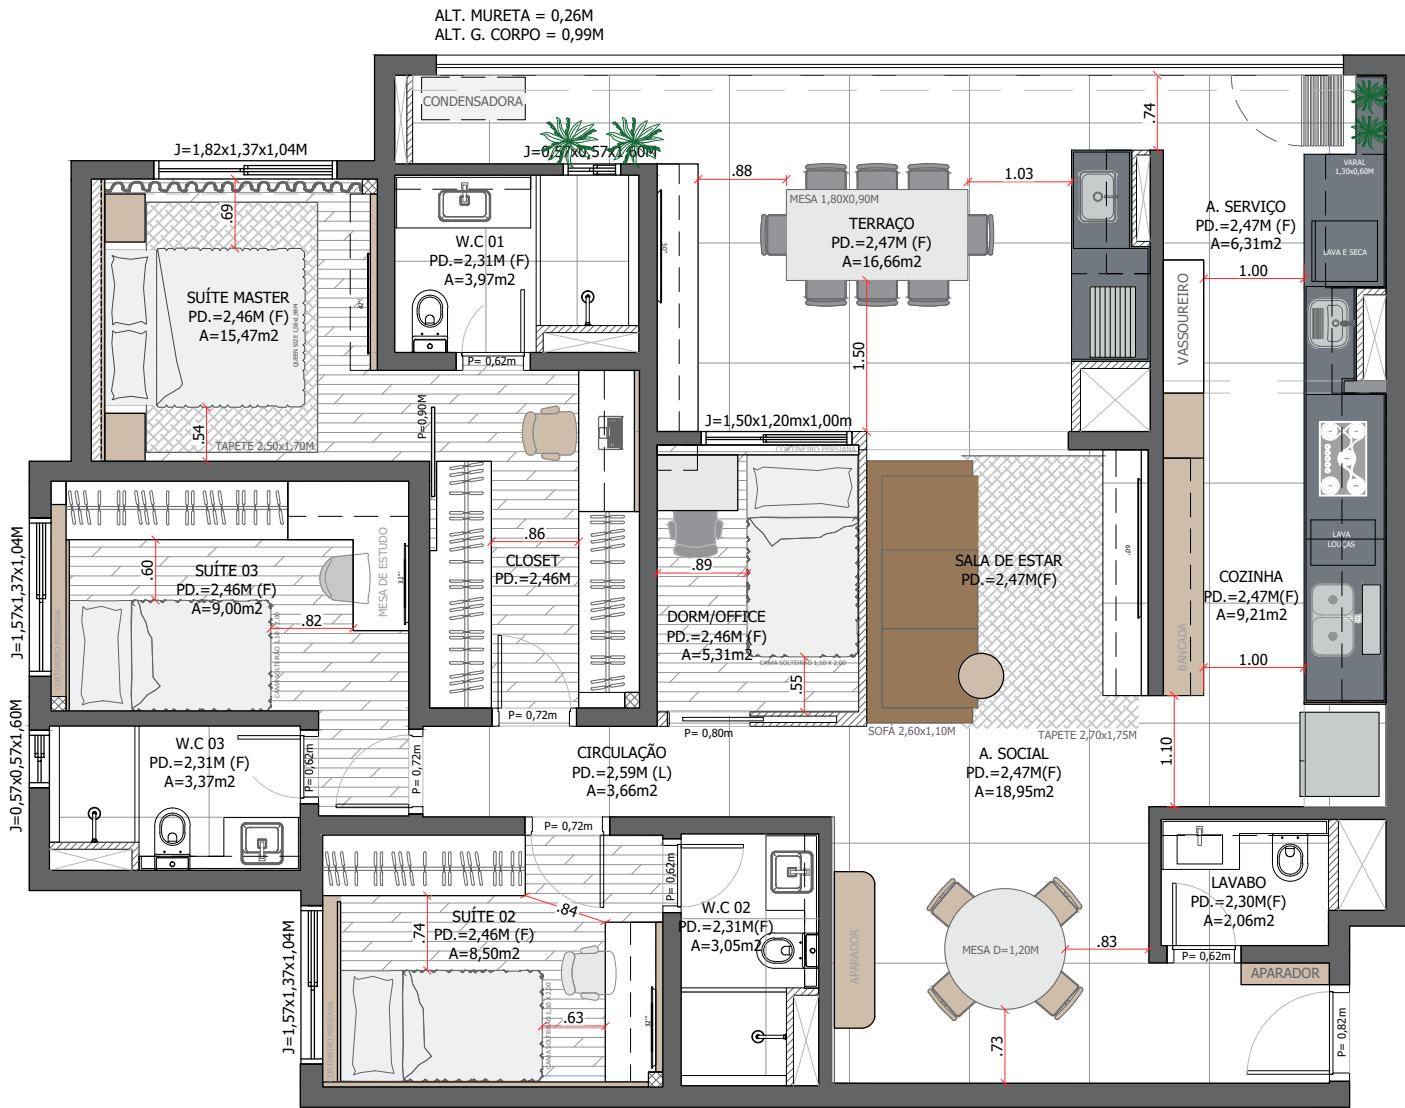

PLANTA BAIXA - LAYOUT
ESC.: 1:75
ÁREA.:114,00m2

LISTA DE ELETROS INDICADOS EM PROJETO

LOCAL	ELETROS (LxPx)	VOLTAGEM
COZINHA	GELADEIRA FROST FREE 554 LITROS INOX - BRO85AK 0,84x0,79x1,87M - BRASTEMP	110V
COZINHA	LAVA-LOUÇA 10 SERVIÇOS BLF10BR 0,45x0,64x0,85M - BRASTEMP	110V
COZINHA	COOKTOP 5 BOCAS BDD75AE 0,73x0,46x0,09M - BRASTEMP	BIVOLT
COZINHA	FORNO DE EMBUTIR ELÉT. 84L PRETO BOC84AE 0,61x0,62x0,58M - BRASTEMP	220V
COZINHA	MICRO-ONDAS 20L COR INOX ESPELHADO BMS20AR 0,455x0,352x0,262M -BRASTEMP	110V
COZINHA	AIR FRYER (MARCA E MODELO A DEFINIR)	110V
COZINHA	DEPURADOR SLIM INOX 60CM - FISHER	110V
A. SERVIÇO	LAVA E SECA INOX 11 KG WW4000 0,60x0,60x0,85M - SAMSUNG	127V
A. SERVIÇO	ASPIRADOR DE PÓ ROBÔ (MARCA E MODELO A DEFINIR)	110V
S. ESTAR	TV 60" (MARCA E MODELO A DEFINIR)	BIVOLT
TERRAÇO	TV 50" (MARCA E MODELO A DEFINIR)	BIVOLT
S. MASTER	TV 42" (MARCA E MODELO A DEFINIR)	BIVOLT
SUÍTE 02	TV 32" (MARCA E MODELO A DEFINIR)	BIVOLT
SUÍTE 03	TV 32" (MARCA E MODELO A DEFINIR)	BIVOLT

NOTAS

ATENÇÃO: OS ELETROS SÃO INDICAÇÕES, CASO HAJA A TROCA DOS MESMOS INDICAMOS QUE AS MEDIDAS E VOLTAGEM INDICADAS EM PROJETOS SEJA SEGUIDAS PARA QUE NÃO HAJA DIVERGÊNCIA.

R02	01/07/2025	EMIÇÃO FINAL	JESSICA ALVES	VENILMA OLIVEIRA
R01	24/06/2024	EMIÇÃO FINAL	JESSICA ALVES	VENILMA OLIVEIRA
R00	06/03/2024	EMIÇÃO INICIAL	JESSICA ALVES	VENILMA OLIVEIRA
Nº de Revisão:	Data:	Descrição:	Responsável:	Desenhista:

Cliente:	ALEXANDRE E CÁTIA	Projeto:	91424-PRAC	
Local:	RUA ANTÔNIO BLASQUES, Nº 122, AP 42 - TORRE A - FREGUESIA DO Ó - SÃO PAULO/SP			
Assunto:	LAYOUT			

DIREITOS RESERVADOS - LEI: 5772 DE 21/DEZEMBRO/1971.
A ALTERAÇÃO SEM AUTORIZAÇÃO DE SEU AUTOR, FICARÁ SUJEITA AS MEDIDAS LEGAIS CABÍVEIS.
A ALTERAÇÃO DESTA PROJETO EXIME SEU AUTOR DE QUALQUER RESPONSABILIDADES POSTERIORES.
TODO ESTE PROJETO FOI ELABORADO COM UNIDADE DE MEDIDAS EM M (METROS).
TODAS AS MEDIDAS, ABERTURAS, PRUMOS E PÉ DIREITO, DEVEM SER CONFERIDAS NO LOCAL, ANTES DA REALIZAÇÃO DE QUALQUER ATIVIDADE.
DEFINIÇÕES NÃO DESCRITAS OU DIVERGÊNCIAS ENCONTRADAS, DEVERÃO SER SUBMETIDAS A APROVAÇÃO DO COORDENADOR DO PROJETO ANTES DE ORÇAMENTOS E/OU EXECUÇÕES.
ESTE PROJETO FOI CONFIGURADO EM FOLHA A3.

Fase:	Escala:	Folha:
☐ LT ☐ EP ☐ AP ☒ EX	1:75 Revisão: 2	03 16

CONSTRUIR PAREDE DE DRYWALL PARA INSERIR JANELA | PEITORIL = 1,00M

INSTALAR PERSIANA DE ROLO

INSTALAR CUBA DE LOUÇA + TORNEIRA/MISTURADOR DE BANCADA | **NOVO**

INSTALAR TRILHO/VARÃO E CORTINA DE TECIDO

INSTALAR DUCHA DE PAREDE | **NOVO**

CONSTRUIR PAREDE DE DRYWALL ATÉ A LAJE PARA INSERIR NOVA POSIÇÃO DO AR CONDICIONADO

INSTALAR VASO SANITÁRIO APÓS O REVESTIMENTO | **NOVO**

INSTALAR PERSIANA DE ROLO

REINSTALAR FOLHA DE PORTA DE MADEIRA APÓS O REVSTIMENTO E PINTURA | **EXISTENTE**

INSTALAR DUCHA DE PAREDE | **NOVO**

INSTALAR VASO SANITÁRIO APÓS O REVESTIMENTO | **NOVO**

INSTALAR CUBA DE LOUÇA + TORNEIRA/MISTURADOR DE BANCADA | **NOVO**

INSTALAR EXAUSTOR (VENTOKIT) | **NOVO**

INSTALAR PERSIANA DE ROLO

PLANTA BAIXA - CONSTRUÇÃO
ESC.: 1:75
ÁREA.:114,00m2

LEGENDA DE CONSTRUÇÕES

	NIVELAR PISO COM EPS OU CINASITA 26,00m2
	CONSTRUIR PAREDE DE DRYWALL 11,00m2 (VIDE PROJETO)
	CONSTRUIR PAREDE DE TIJOLINHO 2,00m2 (VIDE PROJETO)
	CONSTRUIR FECHAMENTO DE DRYWALL P/ CHURRASQ. 3,50m2 PLACA RF - ROSA (VIDE PROJ. E ELEVACÃO)
	INSTALAR PORTA DE MADEIRA DE CORRER EMBUTIDA 01 unid. (NOVO) 0,80x2,10M LARG. VÃO = 1,68M
	INSTALAR VASO SANITÁRIO APÓS O REVESTIMENTO 04 unid. (NOVO)
	INSTALAR CUBA DE LOUÇA 03 unid. (NOVO) COM SIFÃO SIMPLES
	INSTALAR CUBA EM AÇO INOX E CALHA ÚMIDA 02 unid. (NOVO) COM SIFÃO SIMPLES
	INSTALAR TANQUE EM AÇO INOX 01 unid. (NOVO) COM SIFÃO SIMPLES
	INSTALAR DEPURADOR 01 unid. (NOVO)
	INSTALAR VARAL COM CORDAS INDIVIDUAIS 01 unid. (NOVO) 0,60x1,30M FIXAR NO FORRO
	INSTALAR TRILHO /VARÃO E CORTINAS DE TECIDO 01 unid. (VIDE PROJETO)
	INSTALAR PERSIANA DE ROLO 04 unid. (VIDE PROJETO)
	INSTALAR JANELA DE CORRER ALUMINIO E VIDRO 01 unid. (NOVO) 1,50x1,20M 2 FOLHAS
	REINSTALAR FOLHA DE PORTA DE MADEIRA 07 unid. (EXISTENTE)
	INSTALAR TORNEIRA/MISTURADOR 06 unid. (VIDE PROJETO)
	INSTALAR DUCHA/CHUVEIRO DE PAREDE 03 unid. (NOVO)
	INSTALAR PRENDE/BATE PORTA 08 unid.
	INSTALAR VENTOKIT 03 unid. (NOVO)

NOTAS

TODAS AS MEDIDAS INDICADAS EM PROJETO SÃO MEDIDAS ACABADAS.

TODAS AS ÁREAS MOLHADAS DEVERÃO SER IMPERMEABILIZADAS.

ÁREAS: COZINHA, VARANDA, LAVANDERIA E BANHEIRO (FORA DO BOX) DEVERÃO TER ALTURA DE 0,50m E INTERNO DO BOX 1,50m.


R02	01/07/2025	EMIÇÃO FINAL	JESSICA ALVES	VENILMA OLIVEIRA
R01	24/06/2024	EMIÇÃO FINAL	JESSICA ALVES	VENILMA OLIVEIRA
R00	06/03/2024	EMIÇÃO INICIAL	JESSICA ALVES	VENILMA OLIVEIRA
Nº de Revisão:	Data:	Descrição:	Responsável:	Desenhista:

Ciente:
ALEXANDRE E CÁTIA
Local:
RUA ANTÔNIO BLASQUES, Nº 122, AP 42 - TORRE A - FREGUESIA DO Ó - SÃO PAULO/SP
Assunto:
CONSTRUÇÃO
Projeto:
91424-PRAC

Studio Mies
arquitetura e interiores

DIREITOS RESERVADOS - LEI: 5772 DE 21/DEZEMBRO/1971.
A ALTERAÇÃO SEM AUTORIZAÇÃO DE SEU AUTOR, FICARÁ SUJEITA AS MEDIDAS LEGAIS CABÍVEIS.
A ALTERAÇÃO DESTA PROJETO EXIME SEU AUTOR DE QUAISQUER RESPONSABILIDADES POSTERIORES.
TODO ESTE PROJETO FOI ELABORADO COM UNIDADE DE MEDIDAS EM M (METROS).
TODAS AS MEDIDAS, ABERTURAS, PRUMOS E PÉ DIREITO, DEVEM SER CONFERIDAS NO LOCAL, ANTES DA REALIZAÇÃO DE QUALQUER ATIVIDADE.
DEFINIÇÕES NÃO DESCRITAS OU DIVERGÊNCIAS ENCONTRADAS, DEVERÃO SER SUBMETIDAS A APROVAÇÃO DO COORDENADOR DO PROJETO ANTES DE ORÇAMENTOS E/OU EXECUÇÕES.
ESTE PROJETO FOI CONFIGURADO EM FOLHA A3.

Fase:
☐ LT
☐ EP
☐ AP
☒ EX
Escala:
1:75
Revisão:
2
Folha:
04
16

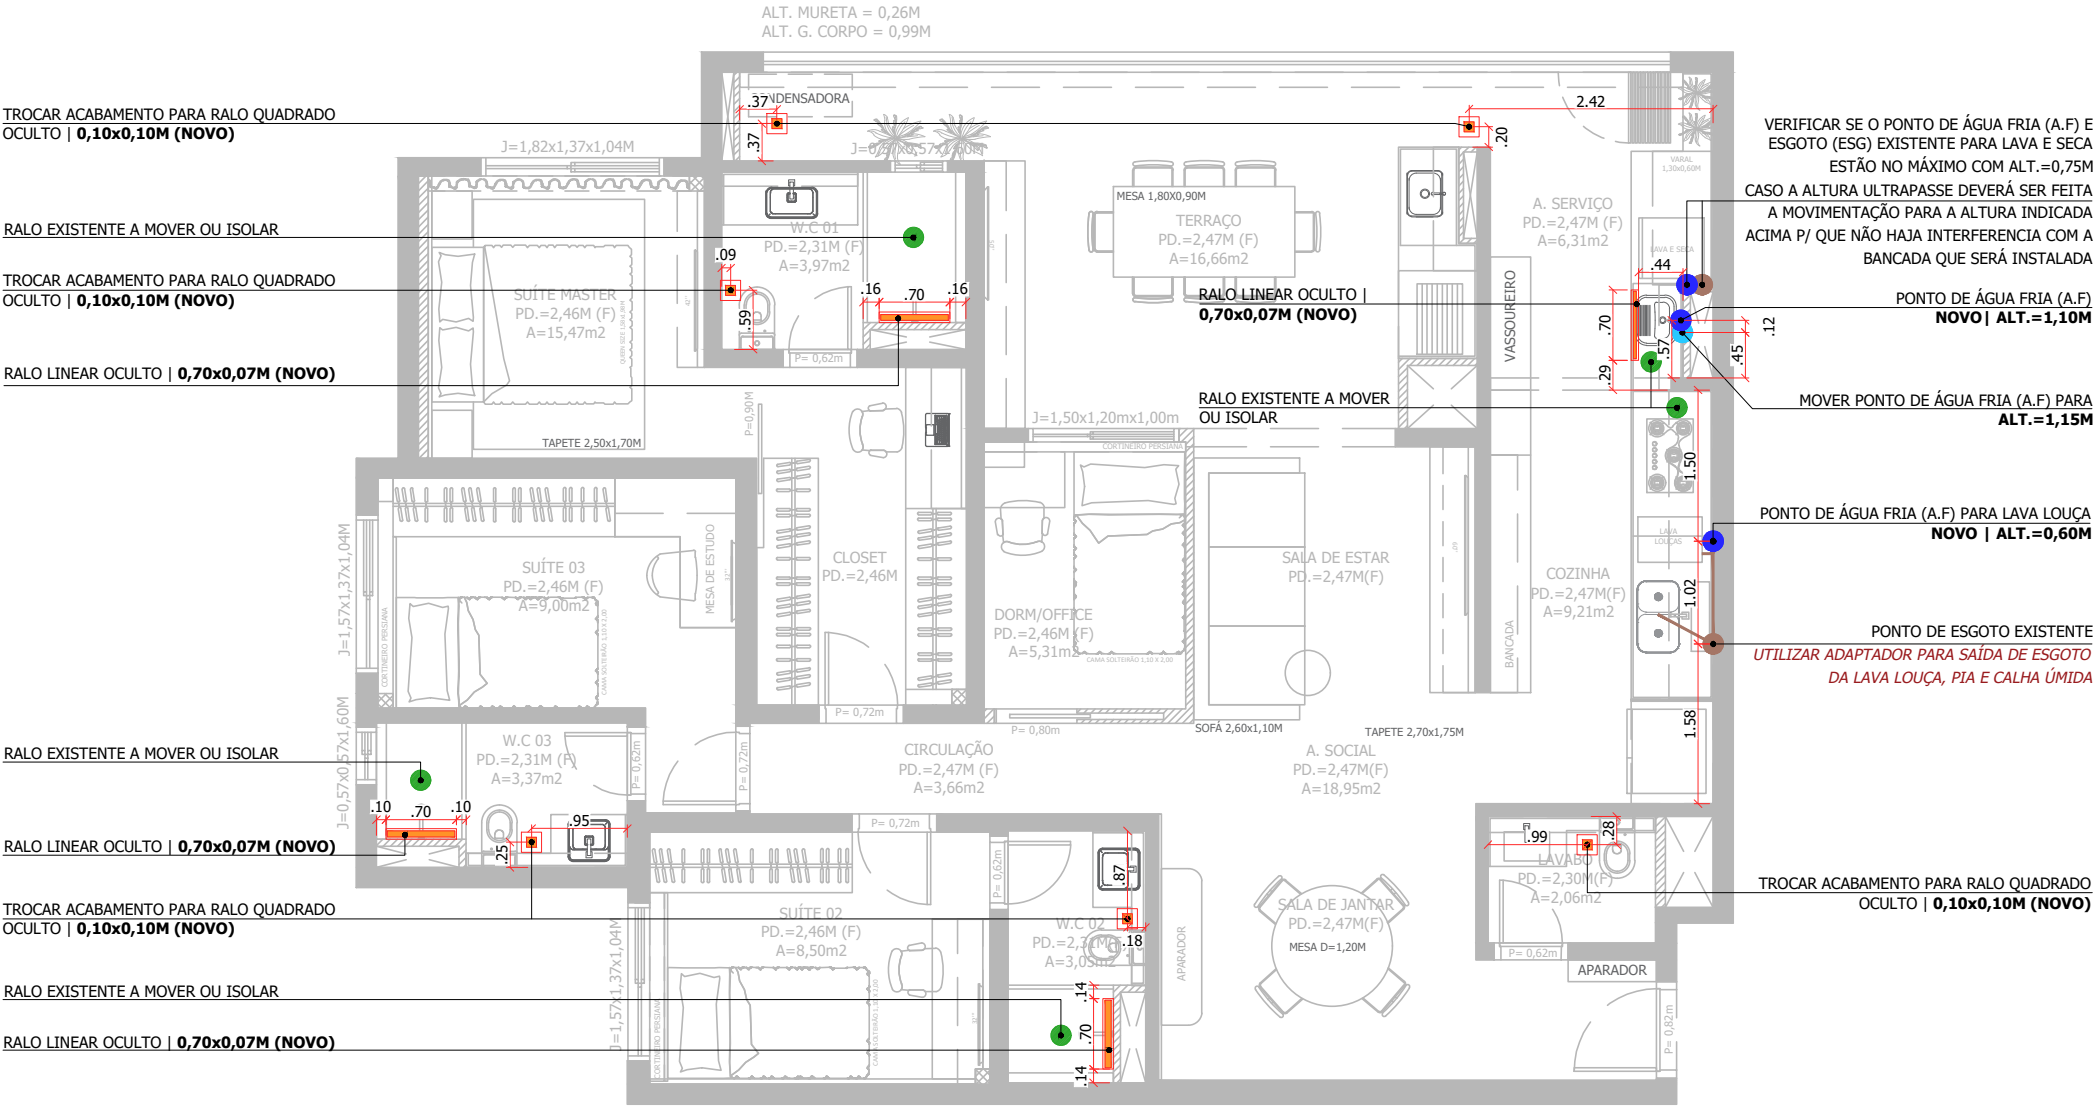

PLANTA BAIXA - PONTOS HIDRÁULICOS
ESC.: 1:75
ÁREA.:114,00m2

NOTAS

- TODAS AS ÁREAS MOLHADAS DEVERÃO SER IMPERMEABILIZADAS.

ÁREAS: COZINHA, VARANDA, LAVANDERIA E BANHEIRO (FORA DO BOX) DEVERÃO TER ALTURA DE 0,50m E INTERNO DO BOX 1,50m.
- TODOS OS REGISTROS DE PRESSÃO E GAVETAS DEVERÃO SER QUANTIFICADOS E DEFINIDOS OS MODELOS "IN LOCO" PARA A COMPRA DE ACORDO COM O ACABAMENTO INTERNO.

LEGENDA DE PONTOS HIDRÁULICOS

	RALO SIMPLES 05 unid. MOVER OU ISOLAR
	RALO OCULTO 06 unid. 0,10x0,10m NOVO
	RALO OCULTO LINEAR 04 unid. 0,70x0,07m NOVO
	PONTO DE ÁGUA FRIA (AF) 03 unid. NOVO
	PONTO DE ÁGUA FRIA (AF) 01 unid. A MOVER OU ISOLAR
	PONTO DE ESGOTO(ESG) 02 unid. NOVO

LISTA DE LOUÇAS E METAIS

LOCAL	LOUÇAS/ METAIS
LAVABO	KIT BACIA PARA CAIXA ACOPLADA CARRARA BRANCO P.606.17 - DECA
LAVABO	TORNEIRA DE MESA BICA ALTA POLO BLACK NOIR 1198.BL33.NO - DECA
COZINHA	CUBA DE EMBUTIR ISIS 2C 34-28 BS EM AÇO INOX AC. 0,69x0,40M - TRAMONTINA
COZINHA	MISTURADOR MONOC. DE MESA COM DUCHA ESPECIAL 2266 C76 - LORENZETTI
COZINHA	CALHA ÚMIDA EM AÇO INOX DE EMBUTIR 0,75x0,18M - TRAMONTINA
A. SERVIÇO	TANQUE DE ENCAIXE HERA 34 L EM AÇO INOX AC. 0,50x0,40x0,23M -TRAMONTINA
A. SERVIÇO	TORNEIRA DE PAREDE LINK BICA CURTA CROMADO 1174.C.LNK - DECA
TERRAÇO	TORNEIRA DOCOL FORNECIDA PELA CONSTRUTORA
TERRAÇO	CUBA EM AÇO INOX FORNECIDA PELA CONSTRUTORA
W.C 01	KIT BACIA PARA CAIXA ACOPLADA CARRARA BRANCO P.606.17 - DECA
W.C 01	MISTURADOR MONOC. DE MESA PRETO 2875 B78 - LORENZETTI
W.C 01	CUBA RETANGULAR BRANCO SLIM L.23050.17 0,50x0,30x0,13M - DECA
W.C 01	DUCHA QUADRADA NA COR PRETA (MARCA A SER DEFINIDA)
W.C 02	KIT BACIA PARA CAIXA ACOPLADA CARRARA BRANCO P.606.17 - DECA
W.C 02	CUBA QUADRADA COM DECK BRANCO SLIM L.21040.M.17 0,40x0,40x0,13M - DECA
W.C 02	MISTURADOR DE MESA BICA ALTA PARA LAVATÓRIO LINK 1877.C.LNK - DECA
W.C 02	DUCHA EDEN DE PAREDE COM DESVIADOR CROMADO- DOCOL
W.C 03	KIT BACIA PARA CAIXA ACOPLADA CARRARA BRANCO P.606.17 - DECA
W.C 03	CUBA QUADRADA COM DECK BRANCO SLIM L.21040.M.17 0,40x0,40x0,13M - DECA
W.C 03	MISTURADOR DE MESA BICA ALTA PARA LAVATÓRIO LINK 1877.C.LNK - DECA
W.C 03	DUCHA EDEN DE PAREDE COM DESVIADOR CROMADO- DOCOL

R02	01/07/2025	EMIÇÃO FINAL	JESSICA ALVES	VENILMA OLIVEIRA	
R01	24/06/2024	EMIÇÃO FINAL	JESSICA ALVES	VENILMA OLIVEIRA	
R00	06/03/2024	EMIÇÃO INICIAL	JESSICA ALVES	VENILMA OLIVEIRA	
Nº de Revisão:	Data:	Descrição:	Responsável:	Desenhista:	
Cliente: ALEXANDRE E CÁTIA			 arquitetura e interiores		
Local: RUA ANTÔNIO BLASQUES, Nº 122, AP 42 - TORRE A - FREGUESIA DO Ó - SÃO PAULO/SP					
Assunto: PONTOS HIDRÁULICOS					
Direitos Reservados - Lei: 5772 DE 21/DEZEMBRO/1971. A ALTERAÇÃO SEM AUTORIZAÇÃO DE SEU AUTOR, FICARÁ SUJEITA AS MEDIDAS LEGAIS CABÍVEIS. A ALTERAÇÃO DESTA PROJETO EXIME SEU AUTOR DE QUAISQUER RESPONSABILIDADES POSTERIORES. TODO ESTE PROJETO FOI ELABORADO COM UNIDADE DE MEDIDAS EM M (METROS). TODAS AS MEDIDAS, ABERTURAS, PRUMOS E PÉ DIREITO, DEVEM SER CONFERIDAS NO LOCAL, ANTES DA REALIZAÇÃO DE QUALQUER ATIVIDADE. DEFINIÇÕES NÃO DESCRITAS OU DIVERGÊNCIAS ENCONTRADAS, DEVERÃO SER SUBMETIDAS A APROVAÇÃO DO COORDENADOR DO PROJETO ANTES DE ORÇAMENTOS E/OU EXECUÇÕES. ESTE PROJETO FOI CONFIGURADO EM FOLHA A3.			Projeto: 91424-PRAC		
Fase: ☐ LT ☐ EP ☐ AP ☒ EX			Escala: 1:75 Revisão: 2		Folha: 05 16


LEGENDA DE AR CONDICIONADO

	CONDENSADORA á confirmar
	EVAPORADORA 05 unid.
	PERCURSO DRENO
	ÁREA DE INTERVENÇÃO

OBS.:
1. Indicamos as marcas: daikin, fujitsu e carrier.

NOTAS

VERIFICAR IN LOCO O MELHOR TRAJETO PARA OS DRENOS.

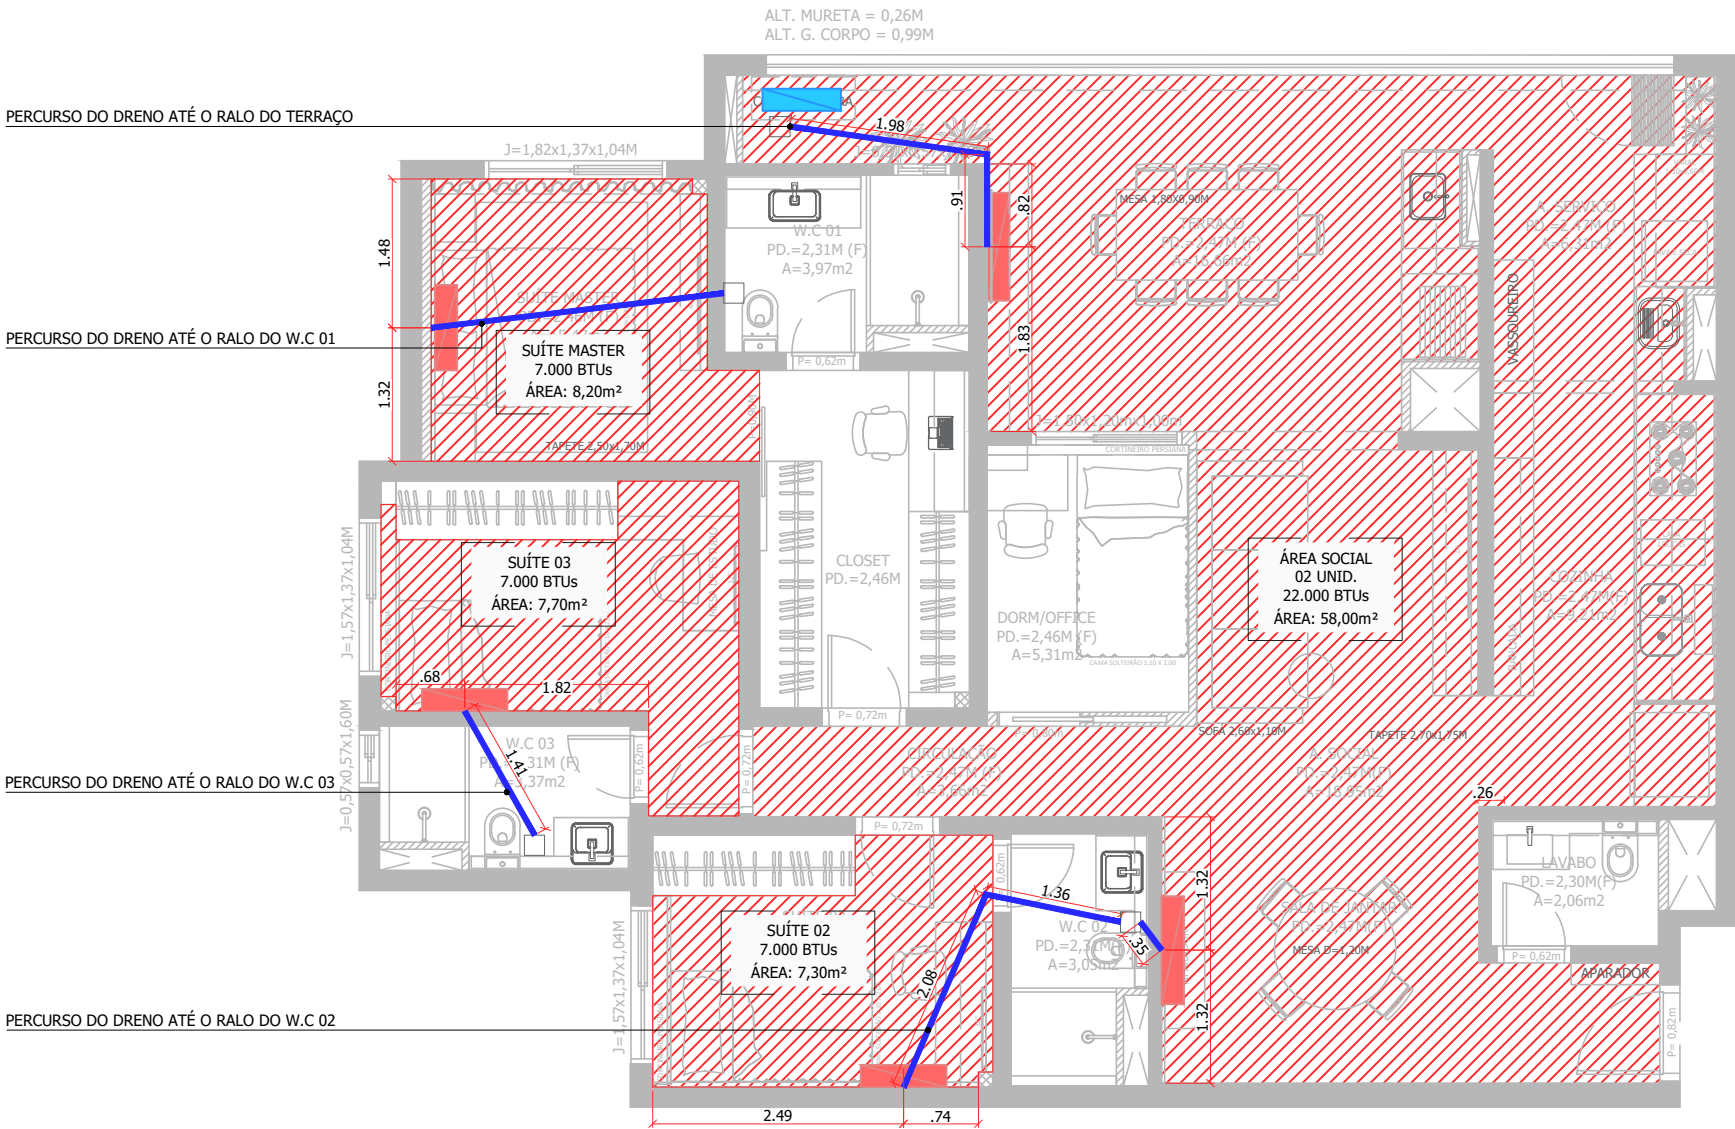


PLANTA BAIXA - AR CONDICIONADO
ESC.: 1:75
ÁREA.:114,00m2

R02	01/07/2025	EMIÇÃO FINAL	JESSICA ALVES	VENILMA OLIVEIRA
R01	24/06/2024	EMIÇÃO FINAL	JESSICA ALVES	VENILMA OLIVEIRA
R00	06/03/2024	EMIÇÃO INICIAL	JESSICA ALVES	VENILMA OLIVEIRA
Nº de Revisão:	Data:	Descrição:	Responsável:	Desenhista:

Ciente:	ALEXANDRE E CÁTIA	Studio Mies arquitetura e interiores
Local:	RUA ANTÔNIO BLASQUES, Nº 122, AP 42 - TORRE A - FREGUESIA DO Ó - SÃO PAULO/SP	
Assunto:	AR CONDICIONADO	
Projeto:		91424-PRAC

DIREITOS RESERVADOS - LEI: 5772 DE 21/DEZEMBRO/1971.
A ALTERAÇÃO SEM AUTORIZAÇÃO DE SEU AUTOR, FICARÁ SUJEITA AS MEDIDAS LEGAIS CABÍVEIS.
A ALTERAÇÃO DESTA PROJETO EXIME SEU AUTOR DE QUAISQUER RESPONSABILIDADES POSTERIORES.
TODO ESTE PROJETO FOI ELABORADO COM UNIDADE DE MEDIDAS EM M (METROS).
TODAS AS MEDIDAS, ABERTURAS, PRUMOS E PÉ DIREITO, DEVEM SER CONFERIDAS NO LOCAL, ANTES DA REALIZAÇÃO DE QUALQUER ATIVIDADE.
DEFINIÇÕES NÃO DESCRITAS OU DIVERGÊNCIAS ENCONTRADAS, DEVERÃO SER SUBMETIDAS A APROVAÇÃO DO COORDENADOR DO PROJETO ANTES DE ORÇAMENTOS E/OU EXECUÇÕES.
ESTE PROJETO FOI CONFIGURADO EM FOLHA A3.

Fase:	Escala:	Folha:
☐ LT ☐ EP ☐ AP ☒ EX	1:75 Revisão: 2	06 16

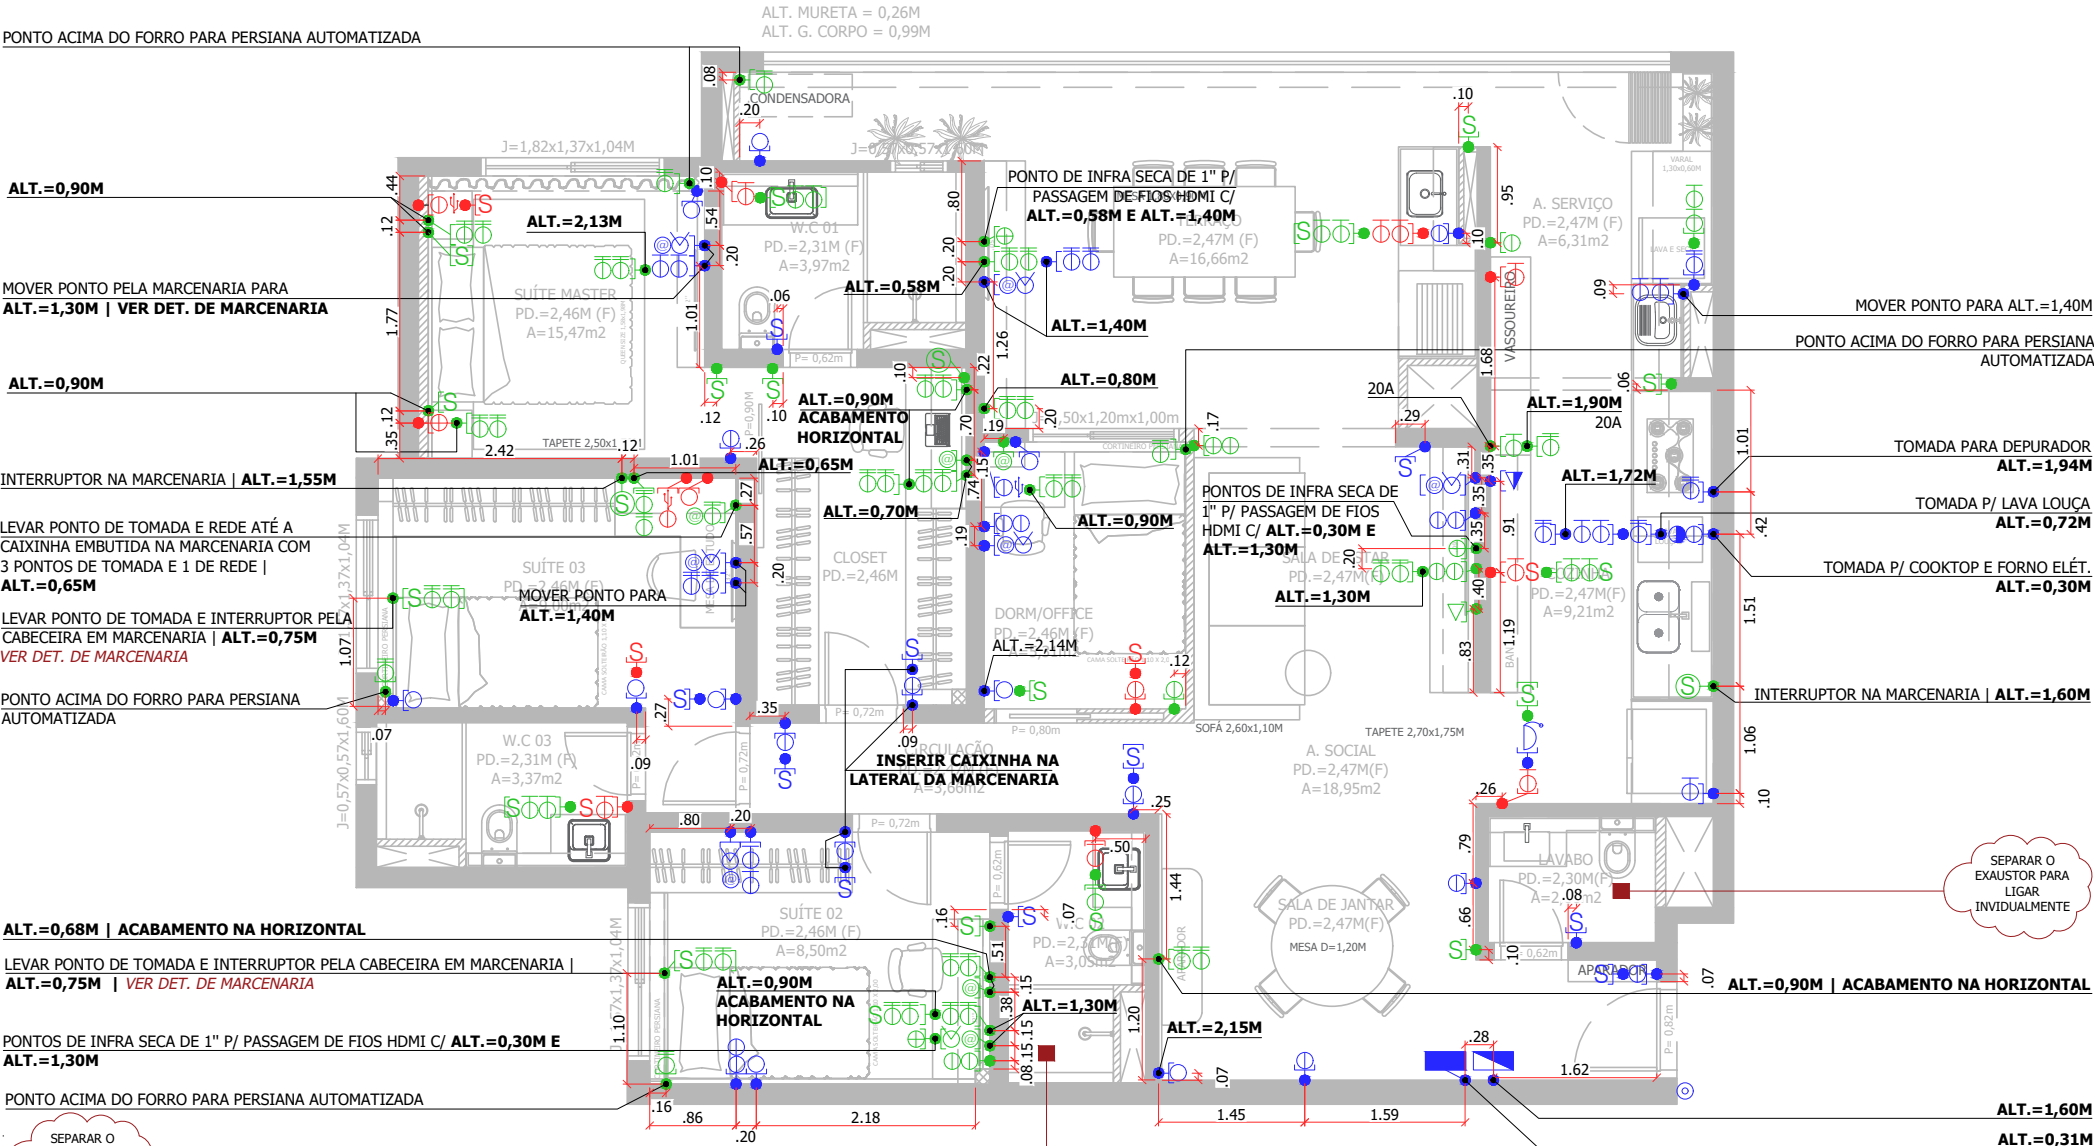

PLANTA BAIXA - PONTOS ELÉTRICOS
ESC.: 1:75
ÁREA.:114,00m2

LISTA DE ELETROS INDICADOS EM PROJETO

LOCAL	ELETROS (LxPxX)	VOLTAGEM	LOCAL	ELETROS (LxPxX)	VOLTAGEM
COZINHA	GELADEIRA FROST FREE 554 LITROS INOX - BRO85AK 0,84x0,79x1,87M - BRASTEMP	110V	A. SERVIÇO	ASPIRADOR DE PÓ ROBÔ (MARCA E MODELO A DEFINIR)	110V
COZINHA	LAVA-LOUÇA 10 SERVIÇOS BLF10BR 0,45x0,64x0,85M - BRASTEMP	110V	S. ESTAR	TV 60" (MARCA E MODELO A DEFINIR)	BIVOLT
COZINHA	COOKTOP 5 BOCAS BDD75AE 0,73x0,46x0,09M - BRASTEMP	BIVOLT	TERRAÇO	TV 50" (MARCA E MODELO A DEFINIR)	BIVOLT
COZINHA	FORNO DE EMBUTIR ELÉT. 84L PRETO BOC84AE 0,61x0,62x0,58M - BRASTEMP	220V	S. MASTER	TV 42" (MARCA E MODELO A DEFINIR)	BIVOLT
COZINHA	MICRO-ONDAS 20L COR INOX ESPELHADO BMS20AR 0,455x0,352x0,262M - BRASTEMP	110V	SUÍTE 02	TV 32" (MARCA E MODELO A DEFINIR)	BIVOLT
COZINHA	AIR FRYER (MARCA E MODELO A DEFINIR)	110V	SUÍTE 03	TV 32" (MARCA E MODELO A DEFINIR)	BIVOLT
COZINHA	DEPURADOR SLIM INOX 60CM - FISHER	110V			
A. SERVIÇO	LAVA E SECA INOX 11 KG WW4000 0,60x0,60x0,85M - SAMSUNG	127V			

NOTA

ATENÇÃO: OS ELETROS SÃO INDICAÇÕES, PORTANTO INDICAMOS QUE SEJAM SEGUIDAS AS VOLTAGENS CONFORME PROJETO.

	TOMADA BAIXA 110V alt=0,30m 25 unid.		PLACA CEGA 09 unid.		USB 01 unid.
	TOMADA BAIXA 220V alt=0,30m 01 unid.		REDE 11 unid.		QUADRO DE ENERGIA
	TOMADA MÉDIA 110V alt=1,10m 21 unid.		TV 07 unid.		QUADRO DE REDE
	TOMADA MÉDIA 220V alt=1,10m 00 unid.		TELEFONE 01 unid.		CAIXINHA 4x2 96 unid.
	TOMADA INDICADA 110V alt=ver planta 49 unid.		INTERFONE 01 unid.		CAIXINHA 4x4 10 unid.
	TOMADA INDICADA 220V alt=ver planta 00 unid.		CAMPAINHA 01 unid.		PONTO A MANTER 54 unid.
	INT.NA MARCENARIA		INFRA SECA 03 unid.		PONTO NOVO 57 unid.
	BOTÃO DA CAMPAINHA 01 unid.		INTERRUPTOR		PONTO A REMOVER 15 unid.

OBS.:

1. Em caso de acréscimos ou adequação de pontos, seguir padrão de altura existente;
2. Verificar se o produto exige alguma infraestrutura, como: cabeamento diferente de 2,5mm?; Disjuntor de quantos amperes mínimo?; Flexível de qual espessura?; Necessário grelha de ar exclusiva para saída de ar quente?;
3. Verificar dimensões e voltagem dos eletrodomésticos e eletrônicos;
4. Usar caixinhas 4x2 deitadas em cima de criados mudo e bancadas de trabalho;
5. Indicamos todos os acabamentos e suportes de elétrica, das marcas: Schneider, Legrand ou Bticino;
6. Indicamos que todas as tomadas sejam de **20A**, para evitar transtornos futuros com novas aquisições.

NOTAS

ATENÇÃO: EM PAREDES ESTRUTURAIS, TRAZER TOMADA PELO PISO ATÉ O FUNDO DA MARCENARIA.

PREVER PONTOS PARA PERSIANAS/CORTINAS AUTOMATIZADAS.

É OBRIGATÓRIA A INSTALAÇÃO DE UM DISJUNTOR EXCLUSIVO PARA FORNO ELÉTRICO, LAVA LOUÇA, MICROONDAS E LAVA E SECA CONFORME ESPECIFICADO NO MANUAL.

R02	01/07/2025	EMIÇÃO FINAL	JESSICA ALVES	VENILMA OLIVEIRA
R01	24/06/2024	EMIÇÃO FINAL	JESSICA ALVES	VENILMA OLIVEIRA
R00	06/03/2024	EMIÇÃO INICIAL	JESSICA ALVES	VENILMA OLIVEIRA
Nº de Revisão:	Data:	Descrição:	Responsável:	Desenhista:
Cliente: ALEXANDRE E CÁTIA				
Local: RUA ANTÔNIO BLASQUES, Nº 122, AP 42 - TORRE A - FREGUESIA DO Ó - SÃO PAULO/SP				
Assunto: PONTOS ELÉTRICOS				
Projeto: 91424-PRAC				
DIREITOS RESERVADOS - LEI: 5772 DE 21/DEZEMBRO/1971. A ALTERAÇÃO SEM AUTORIZAÇÃO DE SEU AUTOR, FICARÁ SUJEITA AS MEDIDAS LEGAIS CABÍVEIS. A ALTERAÇÃO DESTA PROJETO EXIME SEU AUTOR DE QUAISQUER RESPONSABILIDADES POSTERIORES. TODO ESTE PROJETO FOI ELABORADO COM UNIDADE DE MEDIDAS EM M (METROS). TODAS AS MEDIDAS, ABERTURAS, PRUMOS E PÉ DIREITO, DEVEM SER CONFERIDAS NO LOCAL, ANTES DA REALIZAÇÃO DE QUALQUER ATIVIDADE. DEFINIÇÕES NÃO DESCRITAS OU DIVERGÊNCIAS ENCONTRADAS, DEVERÃO SER SUBMETIDAS A APROVAÇÃO DO COORDENADOR DO PROJETO ANTES DE ORÇAMENTOS E/OU EXECUÇÕES. ESTE PROJETO FOI CONFIGURADO EM FOLHA A3.				
Fase: ☐ LT ☐ EP ☐ AP ☒ EX			Escala: 1:75 Revisão: 2	Folha: 07 16

LEGENDA DE INTERRUPTORES


S	INTERRUPTOR SIMPLES 38 unid.	CAIXINHA 4x4 08 unid.
S	INTERRUPTOR PARALELO 26 unid.	PONTO A MANTER 10 unid.
S	INTERRUPTOR INTERMEDIÁRIO 03 unid.	PONTO NOVO 20 unid.
S	INTERRUPTOR NA MARCENARIA 03 unid.	PONTO A REMOVER 05 unid.
T	CAIXINHA 4x2 19 unid.	

OBS.:

- Em caso de acréscimos ou adequação de pontos, seguir padrão de altura existente;
- Verificar dimensões dos mobiliários para que nenhum interruptor fique escondido;
- Indicamos todos os acabamentos e suportes de elétrica das marcas: Schneider, Legrand ou Bticino;
- Os números descritos ao lado dos pontos, é a identificação dos circuitos;

NOTAS

SEPARAR O INTERRUPTOR DO VENTOKIT (EXAUSTOR) DO LAVABO E WC 02 DA ILUMINAÇÃO, PREVER ACIONAMENTO SEPARADO.

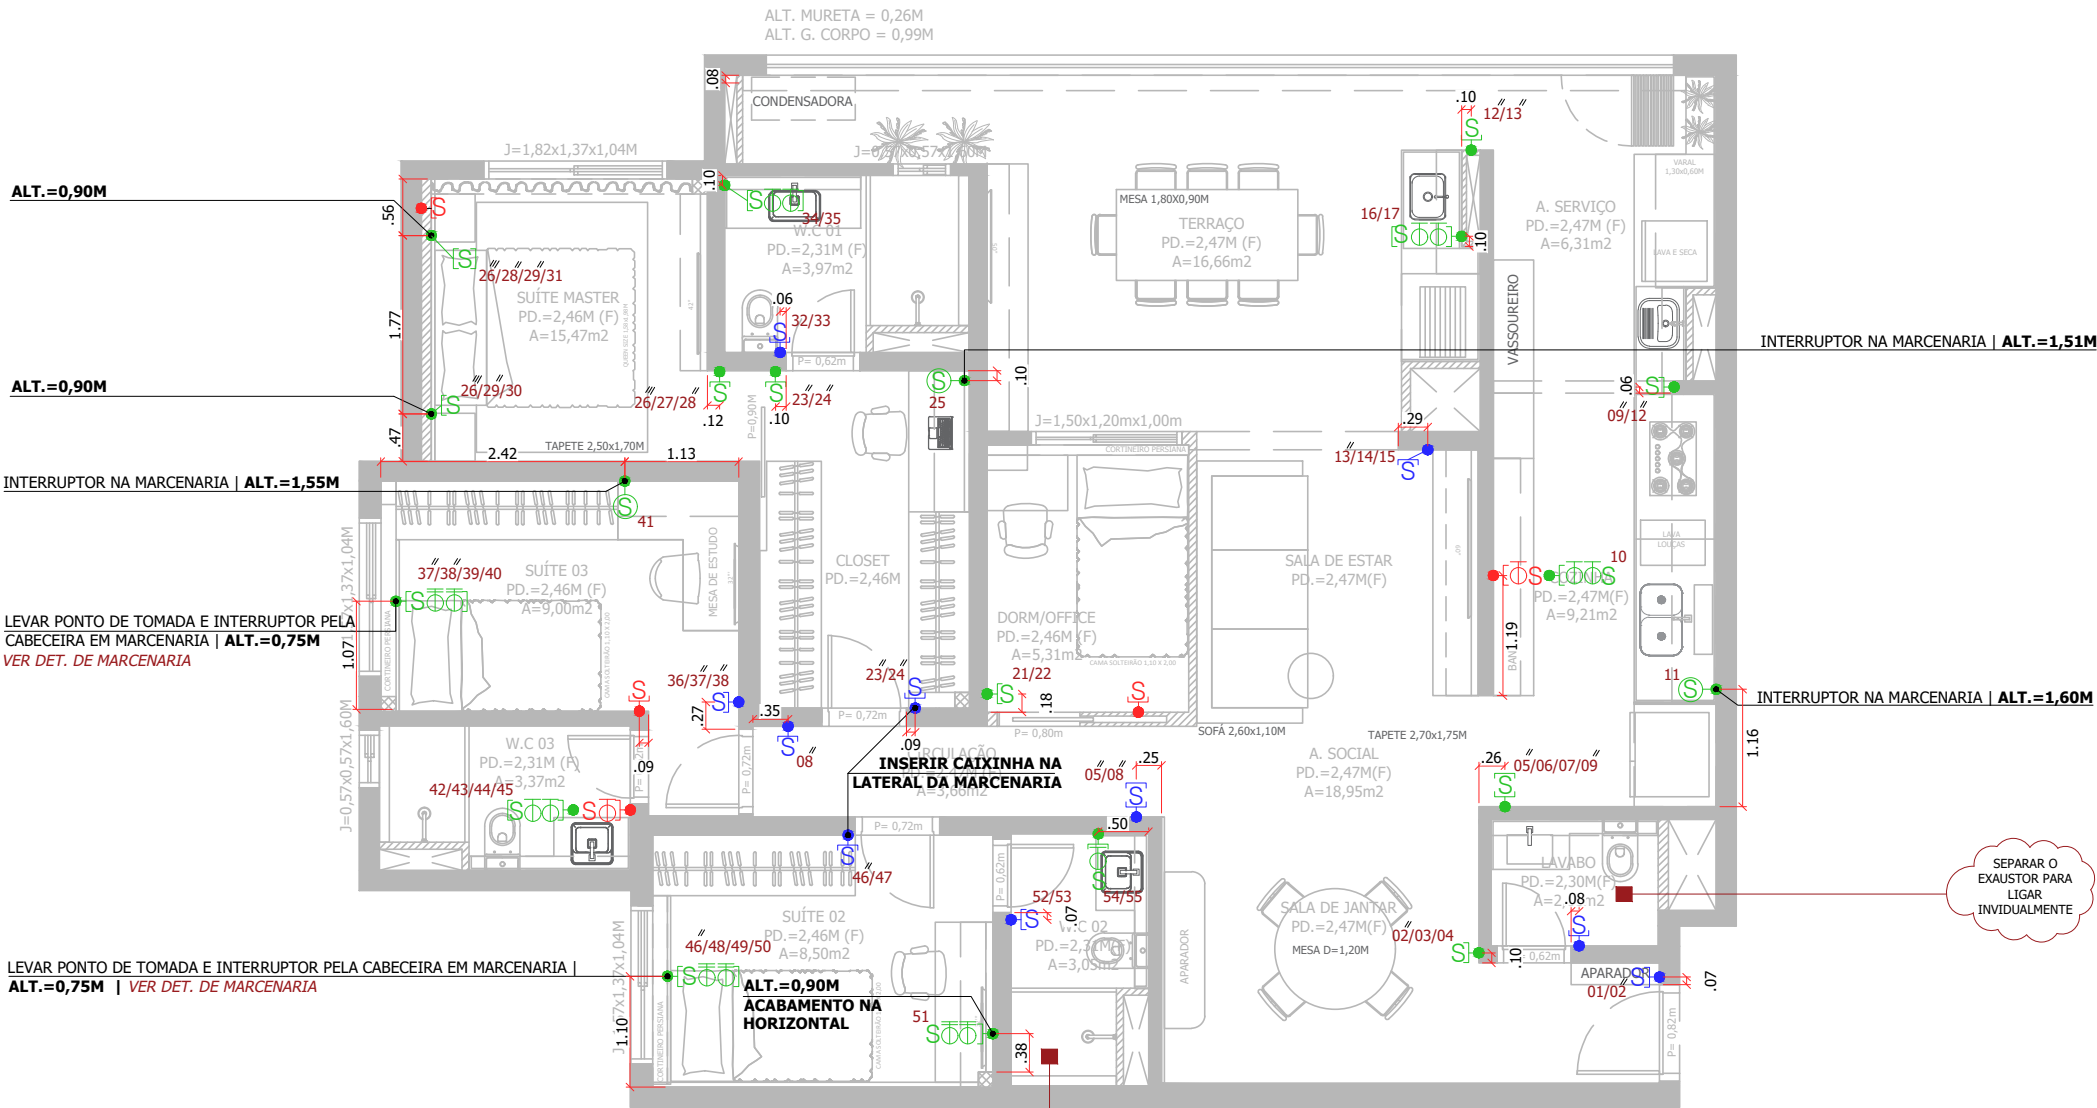

PLANTA BAIXA - INTERRUPTORES
ESC.: 1:75
ÁREA.:114,00m2

R02	01/07/2025	EMIÇÃO FINAL	JESSICA ALVES	VENILMA OLIVEIRA
R01	24/06/2024	EMIÇÃO FINAL	JESSICA ALVES	VENILMA OLIVEIRA
R00	06/03/2024	EMIÇÃO INICIAL	JESSICA ALVES	VENILMA OLIVEIRA
Nº de Revisão:	Data:	Descrição:	Responsável:	Desenhista:

Ciente:	ALEXANDRE E CÁTIA	
Local:	RUA ANTÔNIO BLASQUES, Nº 122, AP 42 - TORRE A - FREGUESIA DO Ó - SÃO PAULO/SP	
Assunto:	INTERRUPTORES	Projeto: 91424-PRAC



DIREITOS RESERVADOS - LEI: 5772 DE 21/DEZEMBRO/1971. A ALTERAÇÃO SEM AUTORIZAÇÃO DE SEU AUTOR, FICARÁ SUJEITA AS MEDIDAS LEGAIS CABÍVEIS. A ALTERAÇÃO DESTA PROJETO EXIME SEU AUTOR DE QUAISQUER RESPONSABILIDADES POSTERIORES. TODO ESTE PROJETO FOI ELABORADO COM UNIDADE DE MEDIDAS EM M (METROS). TODAS AS MEDIDAS, ABERTURAS, PRUMOS E PÉ DIREITO, DEVEM SER CONFERIDAS NO LOCAL, ANTES DA REALIZAÇÃO DE QUALQUER ATIVIDADE. DEFINIÇÕES NÃO DESCRITAS OU DIVERGÊNCIAS ENCONTRADAS, DEVERÃO SER SUBMETIDAS A APROVAÇÃO DO COORDENADOR DO PROJETO ANTES DE ORÇAMENTOS E/OU EXECUÇÕES. ESTE PROJETO FOI CONFIGURADO EM FOLHA A3.	Fase: ☐ LT ☐ EP ☐ AP ☒ EX	Escala: 1:75 Revisão: 2	Folha: 08 16
--	--	----------------------------------	--------------------

PERFIL DE LED NA MARCENARIA (10W)
01 UNID. DE 1,35M | ALT.=1,24M
04 UNID. DE 0,36M | ALT.=1,50M | ALT.=1,74M | ALT.=1,98M | ALT.=2,27M

PERFIL DE LED NO FORRO (24W)
01 UNID. DE 1,27M

FITA DE LED NO FORRO P/ CORTINEIRO ILUMINADO (24W)
01 UNID. DE 2,60M | VER DET.02

PERFIL DE LED NA MARCENARIA (10W)
01 UNID. DE 2,80M | ALT.=1,08M

PERFIL DE LED NA MARCENARIA (10W)
01 UNID. DE 1,76M | ALT.=2,01M

PERFIL DE LED NA MARCENARIA (10W)
01 UNID. DE 1,40M | ALT.=1,51M

PERFIL DE LED NO FORRO (24W)
01 UNID. DE 3,37M
01 UNID. DE 1,85M
01 UNID. DE 1,10M

PERFIL DE LED NA MARCENARIA (10W)
02 UNID. DE 1,20M
ALT.=1,56M | ALT.=1,93M

PERFIL DE LED NA MARCENARIA (10W)
01 UNID. DE 0,45M | ALT.=0,76M
LEVAR PONTO PELA MARCENARIA DA CABECEIRA

FITA DE LED NO FORRO P/ CORTINEIRO ILUMINADO (24W)
01 UNID. DE 1,90M | VER DET.02

PERFIL DE LED NO FORRO (24W)
01 UNID. DE 1,13M

PERFIL DE LED NA MARCENARIA (10W)
01 UNID. DE 1,60M | ALT.=1,23M
03 UNID. DE 0,36M | ALT.=1,58M | ALT.=1,93M | ALT.=2,26M

PERFIL DE LED NA MARCENARIA (10W) | **01 UNID. DE 0,55M | ALT.=0,76M**
LEVAR PONTO PELA MARCENARIA DA CABECEIRA

PONTO NA PAREDE P/ TRIANGULOS ILUMINADOS
ALT.=1,70M | VER IMAGEM 3D

PERFIL DE LED NA MARCENARIA (10W)
01 UNID. DE 3,25M | ALT.=0,99M | FITA DE LED RGBW

PERFIL DE LED NA MARCENARIA (10W)
02 UNID. DE 1,64M | ALT.=1,61M | ALT.=2,21M
01 UNID. DE 0,96M | ALT.=1,92M | FITA DE LED RGBW

DRIVERS P/ FITA DE LED



10W - MÉDIA			24W - FORTE	
01 unid. para fita de = 1,66m	01 unid. para fita de = 1,40m	01 unid. para fita de = 0,45m	01 unid. para fita de = 7,28m	01 unid. para fita de = 2,60m
01 unid. para fita de = 2,04m	01 unid. para fita de = 1,76m	01 unid. para fita de = 2,68m	01 unid. para fita de = 1,24m	01 unid. para fita de = 6,28m
01 unid. para fita de = 2,35m	02 unid. para fita de = 2,80m	01 unid. para fita de = 0,55m	01 unid. para fita de = 2,74m	01 unid. para fita de = 0,71m
02 unid. para fita de = 2,46m	01 unid. para fita de = 4,14m	01 unid. para fita de = 3,23m	01 unid. para fita de = 9,36m	02 unid. para fita de = 1,13m
01 unid. para fita de = 3,56m	01 unid. para fita de = 1,20m	01 unid. para fita de = 5,20m	01 unid. para fita de = 4,35m	01 unid. para fita de = 5,22m
			01 unid. para fita de = 1,90m	01 unid. para fita de = 1,27m

TABELA DE INDICAÇÃO DE ILUMINAÇÃO

LOCAL	TIPO	MODELO
SALA JANTAR	PENDENTE	PENDENTE TUTU BLACK GOLD - BELLA ILUMINAÇÃO
SUÍTE MASTER	PENDENTE	PENDENTE VIVA CROMO NEGRO - BELLA ILUMINAÇÃO

NOTAS

AS INDICAÇÕES DE ILUMINAÇÕES NA TABELA SÃO SUGESTÕES E TAMBÉM REFERÊNCIA DO MODELO INDICADO NO PROJETO 3D.

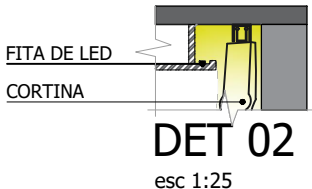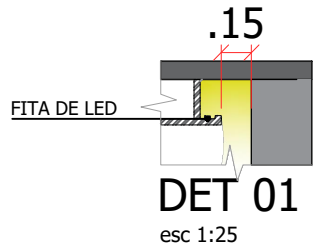

NOTAS

SEPARAR O INTERRUPTOR DO VENTOKIT (EXAUSTOR) DO LAVABO E WC 02 DA ILUMINAÇÃO, PREVER ACIONAMENTO SEPARADO.

R02	01/07/2025	EMIÇÃO FINAL	JESSICA ALVES	VENILMA OLIVEIRA
R01	24/06/2024	EMIÇÃO FINAL	JESSICA ALVES	VENILMA OLIVEIRA
R00	06/03/2024	EMIÇÃO INICIAL	JESSICA ALVES	VENILMA OLIVEIRA
Nº de Revisão:	Data:	Descrição:	Responsável:	Desenhista:
Cliente: ALEXANDRE E CÁTIA				
Local: RUA ANTÔNIO BLASQUES, Nº 122, AP 42 - TORRE A - FREGUESIA DO Ó - SÃO PAULO/SP				
Assunto: ILUMINAÇÃO				
Projeto: 91424-PRAC				

DIREITOS RESERVADOS - LEI: 5772 DE 21/DEZEMBRO/1971.

A ALTERAÇÃO SEM AUTORIZAÇÃO DE SEU AUTOR, FICARÁ SUJEITA AS MEDIDAS LEGAIS CABÍVEIS.

A ALTERAÇÃO DESTA PROJETO EXIME SEU AUTOR DE QUALQUER RESPONSABILIDADES POSTERIORES.

TODO ESTE PROJETO FOI ELABORADO COM UNIDADE DE MEDIDAS EM M (METROS).

TODAS AS MEDIDAS, ABERTURAS, PRUMOS E PÉ DIREITO, DEVEM SER CONFIRMADAS NO LOCAL, ANTES DA REALIZAÇÃO DE QUALQUER ATIVIDADE.

DEFINIÇÕES NÃO DESCRITAS OU DIVERGÊNCIAS ENCONTRADAS, DEVERÃO SER SUBMETIDAS A APROVAÇÃO DO COORDENADOR DO PROJETO ANTES DE ORÇAMENTOS E/OU EXECUÇÕES.

ESTE PROJETO FOI CONFIGURADO EM FOLHA A3.

Fase:	Escala:	Folha:
☐ LT	1:75	09
☐ EP	Revisão:	
☐ AP	2	16
☒ EX		

LEGENDA ILUMINAÇÃO NO TETO

	PLAFON EMB. RETANGULAR LINEAR DIFUSO 03 unid. 0,10x1,20m LED 32w 4000K
	PLAFON EMB. QUADRADO INDIRETO 04 unid. 0,30x0,30m 4 LAMP. E27 3000k
	PENDENTE DECORATIVO 03 unid. MOD. CONFORME TABELA
	SPOT DIRECIONÁVEL COM LÂMPADA DICRÓICA 07 unid. LAMP. LED GU10 4W BIV 3.000K - OSRAM
	SPOT DIRECIONÁVEL COM LÂMPADA MINI DICRÓICA 18 unid. LAMP. LED MR11 3W BIV 2.700K - OSRAM
	SPOT DE EMBUTIR DUPLO COM LÂMPADA DICRÓICA 04 unid. LAMP. LED GU10 4W BIV 3.000K - OSRAM
	SPOT DE EMBUTIR TRIPLO COM LÂMPADA DICRÓICA 02 unid. LAMP. LED GU10 4W BIV 3.000K - OSRAM

LEGENDA ILUMINAÇÃO NA PAREDE

	LUMINARIA TARTARUGA 01 unid. ALUMINIO E-27 60W - FM ALT.=1,90M
	TRIÂNGULOS ILUMINADOS RGB 01 unid. (MARCA E MOD. A DEFINIR)

LEGENDA PERFIL DE LED NA PAREDE

	PERFIL DE LED NA PAREDE 24 W - FORTE 01 unid. de 2,07m 24W - 3000K
--	---

LEGENDA FITA/PERFIL DE LED NO TETO/FORRO

FITA DE LED NO FORRO 24W - FORTE 30,00m		
	01 unid. de 7,28m 24W - 3000K 01 unid. de 1,24m 24W - 3000K 01 unid. de 2,74m 24W - 3000K 01 unid. de 9,36m 24W - 3000K	01 unid. de 4,35m 24W - 3000K 01 unid. de 1,90m 24W - 3000K 01 unid. de 2,60m 24W - 3000K
PERFIL DE LED NO FORRO 24W - FORTE 14,00m		
	01 unid. de 4,21m 24W - 3000K 01 unid. de 0,71m 24W - 3000K 02 unid. de 1,13m 24W - 3000K	01 unid. de 3,37m 24W - 3000K 01 unid. de 1,85m 24W - 3000K 01 unid. de 1,27m 24W - 3000K


LEGENDA PERFIL DE LED NA MARCENARIA

PERFIL DE LED NA MARCENARIA 10W - MÉDIA 32,00m		
	01 unid. de 1,66m 10W - 2700K 01 unid. de 2,04m 10W - 2700K 01 unid. de 2,35m 10W - 2700K 01 unid. de 2,44m 10W - 2700K 02 unid. de 1,23m 10W - 2700K 01 unid. de 2,65m 10W - 2700K 01 unid. de 0,91m 10W - 2700K 01 unid. de 1,40m 10W - 2700K 01 unid. de 1,76m 10W - 2700K	01 unid. de 2,80m 10W - 2700K 01 unid. de 1,35m 10W - 2700K 07 unid. de 0,36m 10W - 2700K 03 unid. de 0,77m 10W - 2700K 01 unid. de 1,53m 10W - 2700K 01 unid. de 1,20m 10W - 2700K 01 unid. de 0,45m 10W - 2700K 01 unid. de 1,60m 10W - 2700K 01 unid. de 0,55m 10W - 2700K
PERFIL DE LED NA MARCENARIA 10W - RGBW 9,00m		
	01 unid. de 3,23m 10W - 2700K 02 unid. de 1,64m 10W - 2700K	02 unid. de 0,96m 10W - 2700K

CORTINEIRO ILUMINADO | VER DET.02

CORTINEIRO ILUMINADO | VER DET.02

CORTINEIRO | VER DET.03

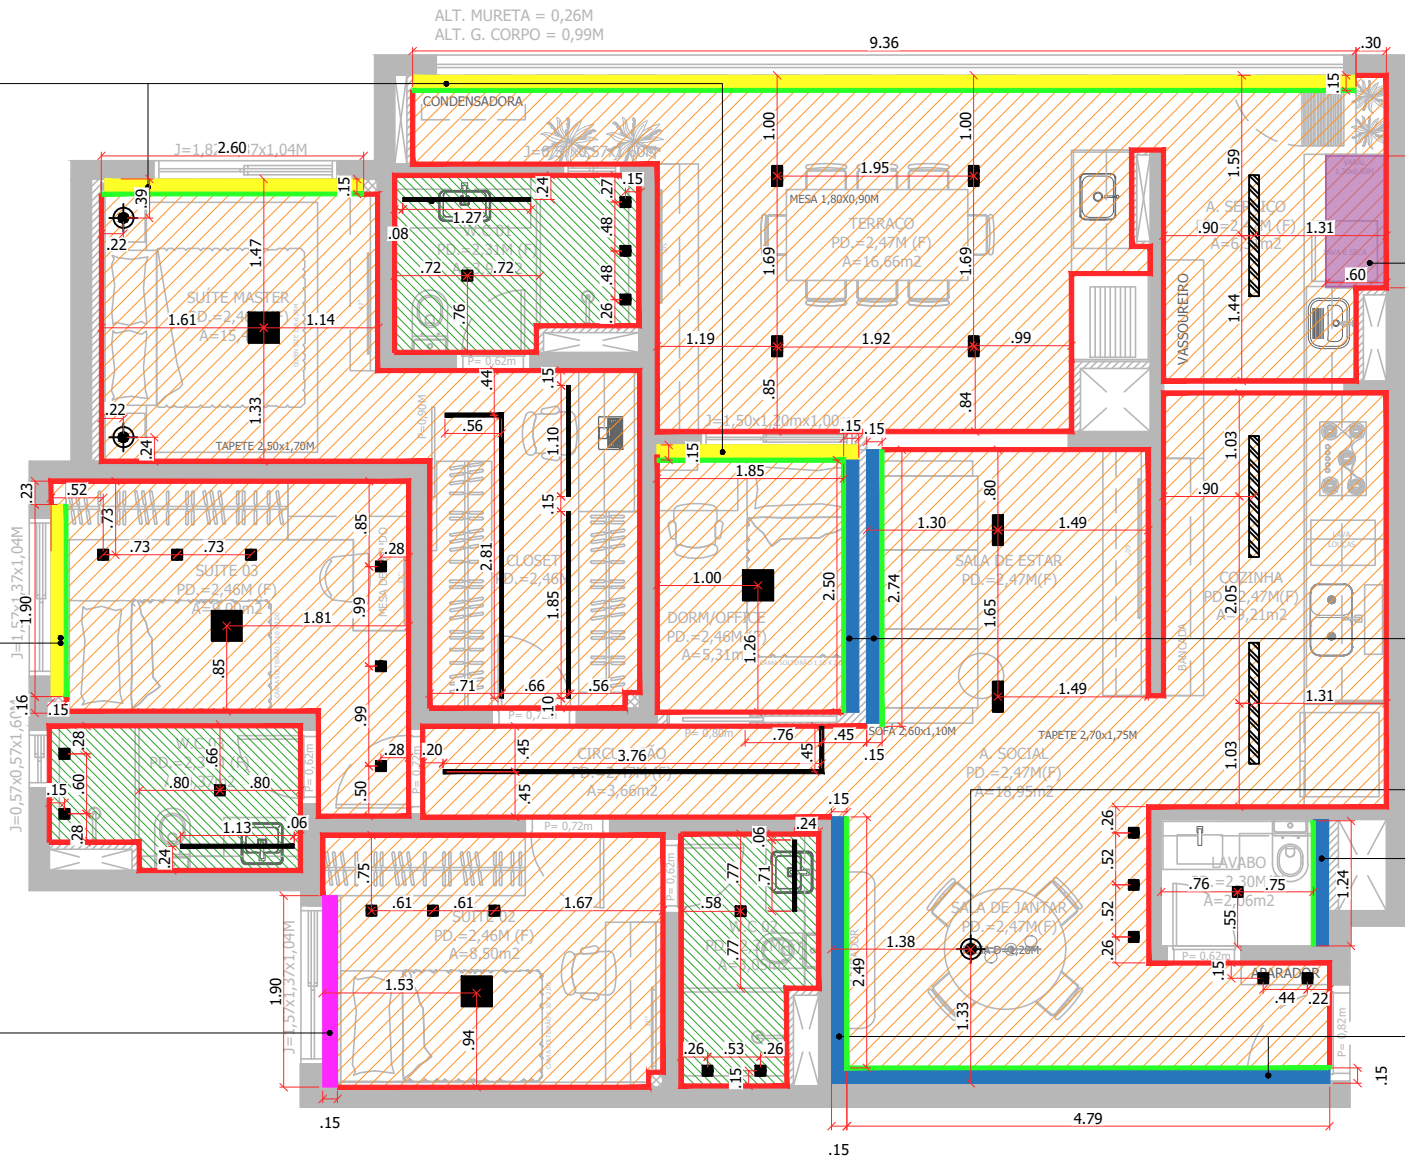

PLANTA BAIXA - FORRO
ESC.: 1:75
ÁREA.:114,00m2

LEGENDA DE FORRO

	FORRO DE GESSO ACARTONADO (DRYWALL) 100,00m2 PLACA ST -BRANCA
	FORRO DE GESSO ACARTONADO (DRYWALL) 12,00m2 PLACA RU -VERDE
	TABICA DE 0,02m 123,00m
	CORTINEIRO ILUMINADO 16,00m
	CORTINEIRO 2,00m
	SANCA ILUMINADA 15,00m

LEGENDA DE ILUMINAÇÃO

	PLAFON EMB. RETANGULAR LINEAR 0,10x1,20M
	PLAFON EMB. QUADRADO 0,30x0,30M
	PENDENTE DECORATIVO
	SPOT DE EMBUTIR
	SPOT DE EMBUTIR DUPLO
	SPOT DE EMBUTIR TRIPLO
	PERFIL DE LED NO FORRO
	FITA DE LED NA SANCA

NOTAS

PREVER REFORÇO NO FORRO PARA PENDENTES E VARAL.




PREVER REFORÇO NO FORRO PARA VARAL

SANCA ILUMINADA | VER DET.01

VERIFICAR MODELO DO PENDENTE

INSERIR NOVOS PONTOS DE ILUMINAÇÃO
NO FORRO EXISTENTE E RECORTE PARA
SANCA ILUMINADA

SANCA ILUMINADA | VER DET.01

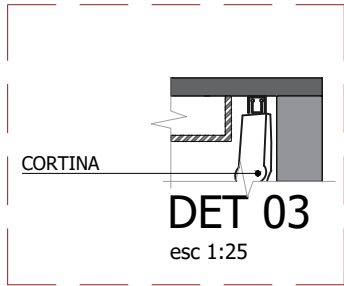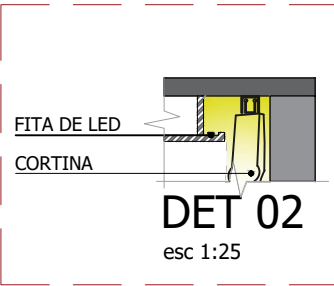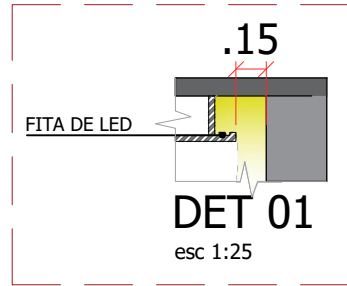

R02	01/07/2025	EMIÇÃO FINAL	JESSICA ALVES	VENILMA OLIVEIRA
R01	24/06/2024	EMIÇÃO FINAL	JESSICA ALVES	VENILMA OLIVEIRA
R00	06/03/2024	EMIÇÃO INICIAL	JESSICA ALVES	VENILMA OLIVEIRA
Nº de Revisão:	Data:	Descrição:	Responsável:	Desenhista:


Cliente:	ALEXANDRE E CÁTIA	Projeto:	91424-PRAC
Local:	RUA ANTÔNIO BLASQUES, Nº 122, AP 42 - TORRE A - FREGUESIA DO Ó - SÃO PAULO/SP		
Assunto:	FORRO		



DIREITOS RESERVADOS - LEI: 5772 DE 21/DEZEMBRO/1971. A ALTERAÇÃO SEM AUTORIZAÇÃO DE SEU AUTOR, FICARÁ SUJEITA AS MEDIDAS LEGAIS CABÍVEIS. A ALTERAÇÃO DESTA PROJETO EXIME SEU AUTOR DE QUAISQUER RESPONSABILIDADES POSTERIORES. TODO ESTE PROJETO FOI ELABORADO COM UNIDADE DE MEDIDAS EM M (METROS). TODAS AS MEDIDAS, ABERTURAS, PRUMOS E PÉ DIREITO, DEVEM SER CONFERIDAS NO LOCAL, ANTES DA REALIZAÇÃO DE QUALQUER ATIVIDADE. DEFINIÇÕES NÃO DESCRITAS OU DIVERGÊNCIAS ENCONTRADAS, DEVERÃO SER SUBMETIDAS A APROVAÇÃO DO COORDENADOR DO PROJETO ANTES DE ORÇAMENTOS E/OU EXECUÇÕES. ESTE PROJETO FOI CONFIGURADO EM FOLHA A3.	Fase: ☐ LT ☐ EP ☐ AP ☒ EX	Escala: 1:75 Revisão: 2	Folha: 10 16
--	--	----------------------------------	--------------------



Fase:	Escala:	Folha:
☐ LT ☐ EP ☐ AP ☒ EX	1:75 Revisão: 2	11 / 16

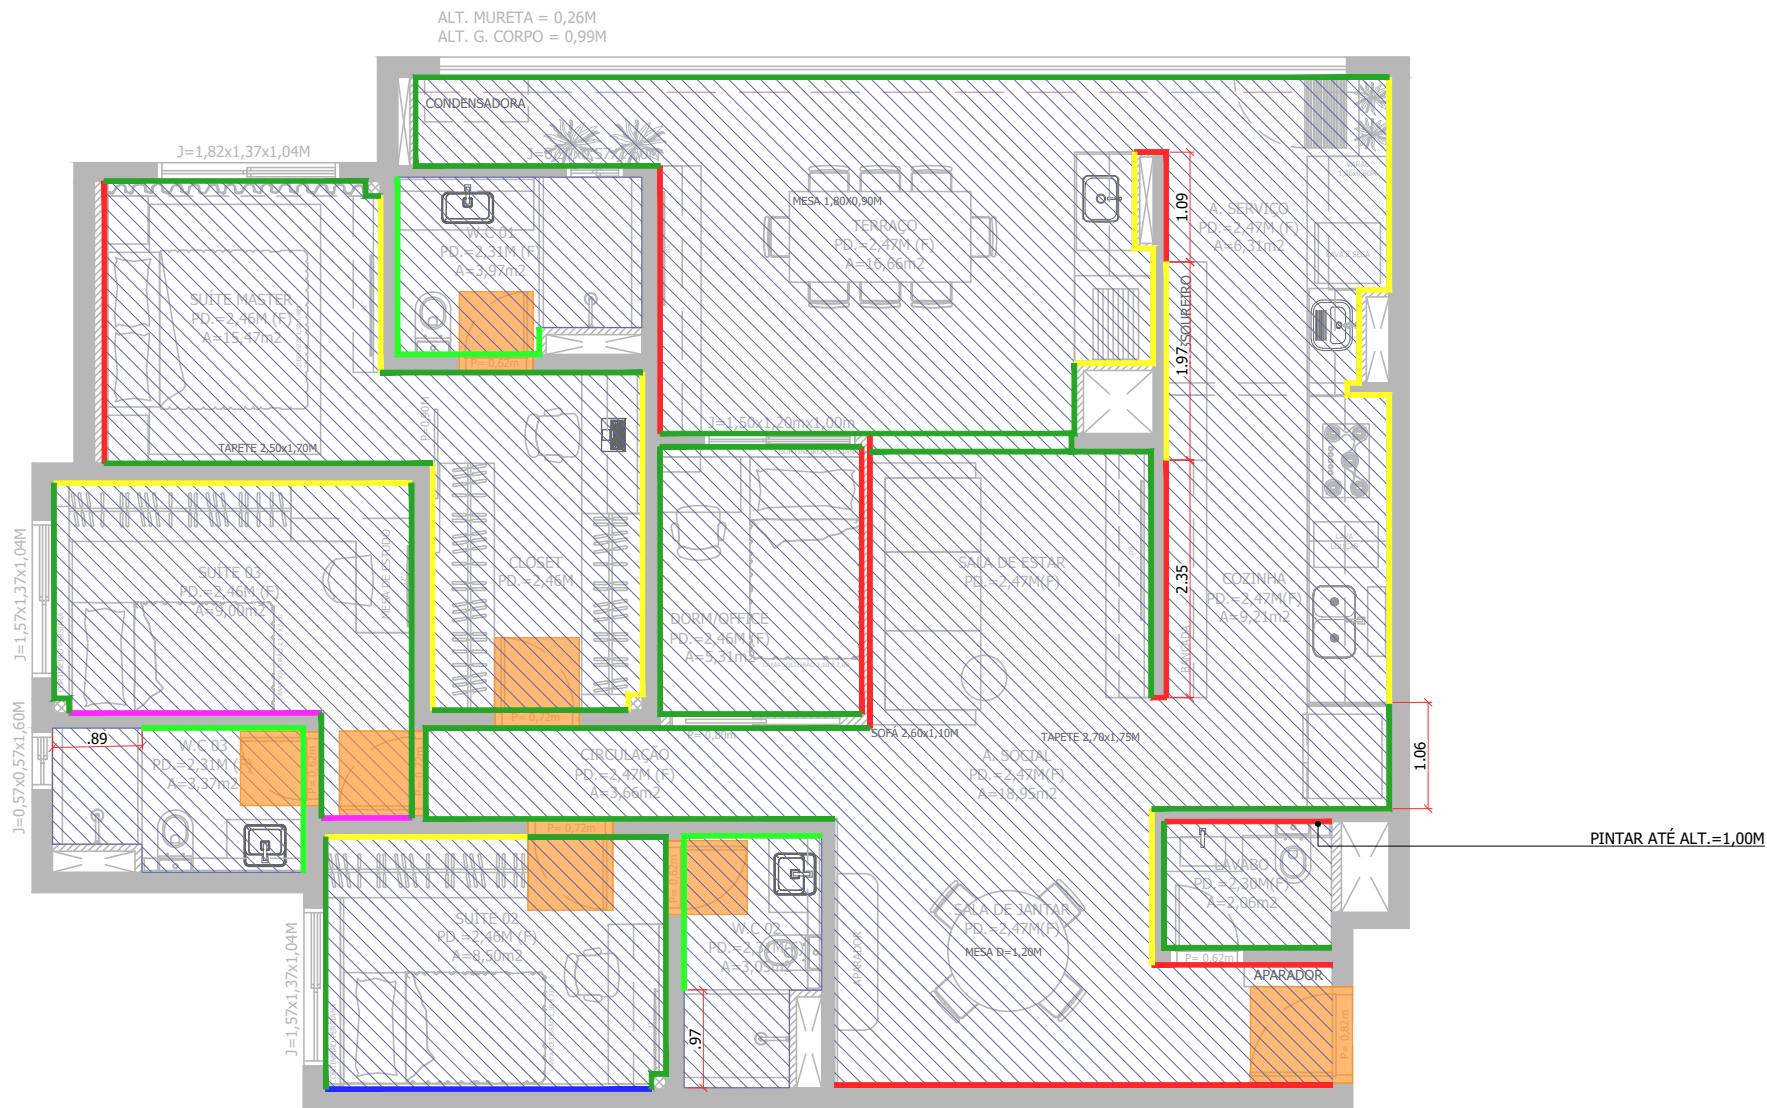

PLANTA BAIXA - PINTURA
ESC.: 1:75
ÁREA.:114,00m2

LEGENDA DE PINTURAS NA PAREDE

	TINTA ACRÍLICA FOSCA COR: PAPEL PICADO SUVINIL 141,00m2
	TINTA ACRÍLICA FOSCA COR: VESTIDO DE SEDA SUVINIL 12,00m2
	TINTA ACRÍLICA FOSCA COR: BRANCO SUVINIL 65,00m2
	TINTA MULTISUPERFÍCIES ACETINADA COR: PAPEL PICADO SUVINIL 23,00m2
	MASSA PARA EFEITO CIMENTO QUEIMADO COR: ELEGANCE CRÔMIO IBRATIN 57,00m2
	MASSA PARA EFEITO CIMENTO QUEIMADO COR: ELEGANCE CRÔMIO IBRATIN TINTA ACRÍLICA FOSCA COR: FRUTO DO CALAFATE SUVINIL 9,00m2

LEGENDA DE PINTURA NO FORRO

	TINTA ACRÍLICA PREMIUM METALATEX COR: BRANCO SHERWIN-WILLIAMS 114,00m2
--	---

LEGENDA DE PINTURA EM PORTAS

	TINTA ESMALTE A BASE DE ÁGUA ACETINADA COR: BRANCO SUVINIL 07 PORTAS
--	---

NOTAS

SUÍTE 02: FAZER A MISTURA DA TINTA FRUTO DO CALAFATE - SUVINIL COM O CIMENTO QUEIMADO PARA CHEGAR NA TEXTURA DESEJADA. (VER IMAGEM 3D)


R02	01/07/2025	EMIÇÃO FINAL	JESSICA ALVES	VENILMA OLIVEIRA
R01	24/06/2024	EMIÇÃO FINAL	JESSICA ALVES	VENILMA OLIVEIRA
R00	06/03/2024	EMIÇÃO INICIAL	JESSICA ALVES	VENILMA OLIVEIRA
Nº de Revisão:	Data:	Descrição:	Responsável:	Desenhista:

Cliente:	ALEXANDRE E CÁTIA	
Local:	RUA ANTÔNIO BLASQUES, Nº 122, AP 42 - TORRE A - FREGUESIA DO Ó - SÃO PAULO/SP	
Assunto:	PINTURA	Projeto: 91424-PRAC
		 arquitetura e interiores

DIREITOS RESERVADOS - LEI: 5772 DE 21/DEZEMBRO/1971. A ALTERAÇÃO SEM AUTORIZAÇÃO DE SEU AUTOR, FICARÁ SUJEITA AS MEDIDAS LEGAIS CABÍVEIS. A ALTERAÇÃO DESTA PROJETO EXIME SEU AUTOR DE QUAISQUER RESPONSABILIDADES POSTERIORES. TODO ESTE PROJETO FOI ELABORADO COM UNIDADE DE MEDIDAS EM M (METROS). TODAS AS MEDIDAS, ABERTURAS, PRUMOS E PÉ DIREITO, DEVEM SER CONFERIDAS NO LOCAL, ANTES DA REALIZAÇÃO DE QUALQUER ATIVIDADE. DEFINIÇÕES NÃO DESCRITAS OU DIVERGÊNCIAS ENCONTRADAS, DEVERÃO SER SUBMETIDAS A APROVAÇÃO DO COORDENADOR DO PROJETO ANTES DE ORÇAMENTOS E/OU EXECUÇÕES. ESTE PROJETO FOI CONFIGURADO EM FOLHA A3.	Fase: ☐ LT ☐ EP ☐ AP ☒ EX	Escala: 1:75 Revisão: 2	Folha: 12 16
--	--	--	----------------------------------

NOTAS

TODAS AS MEDIDAS INDICADAS EM PROJETO SÃO MEDIDAS ACABADAS.

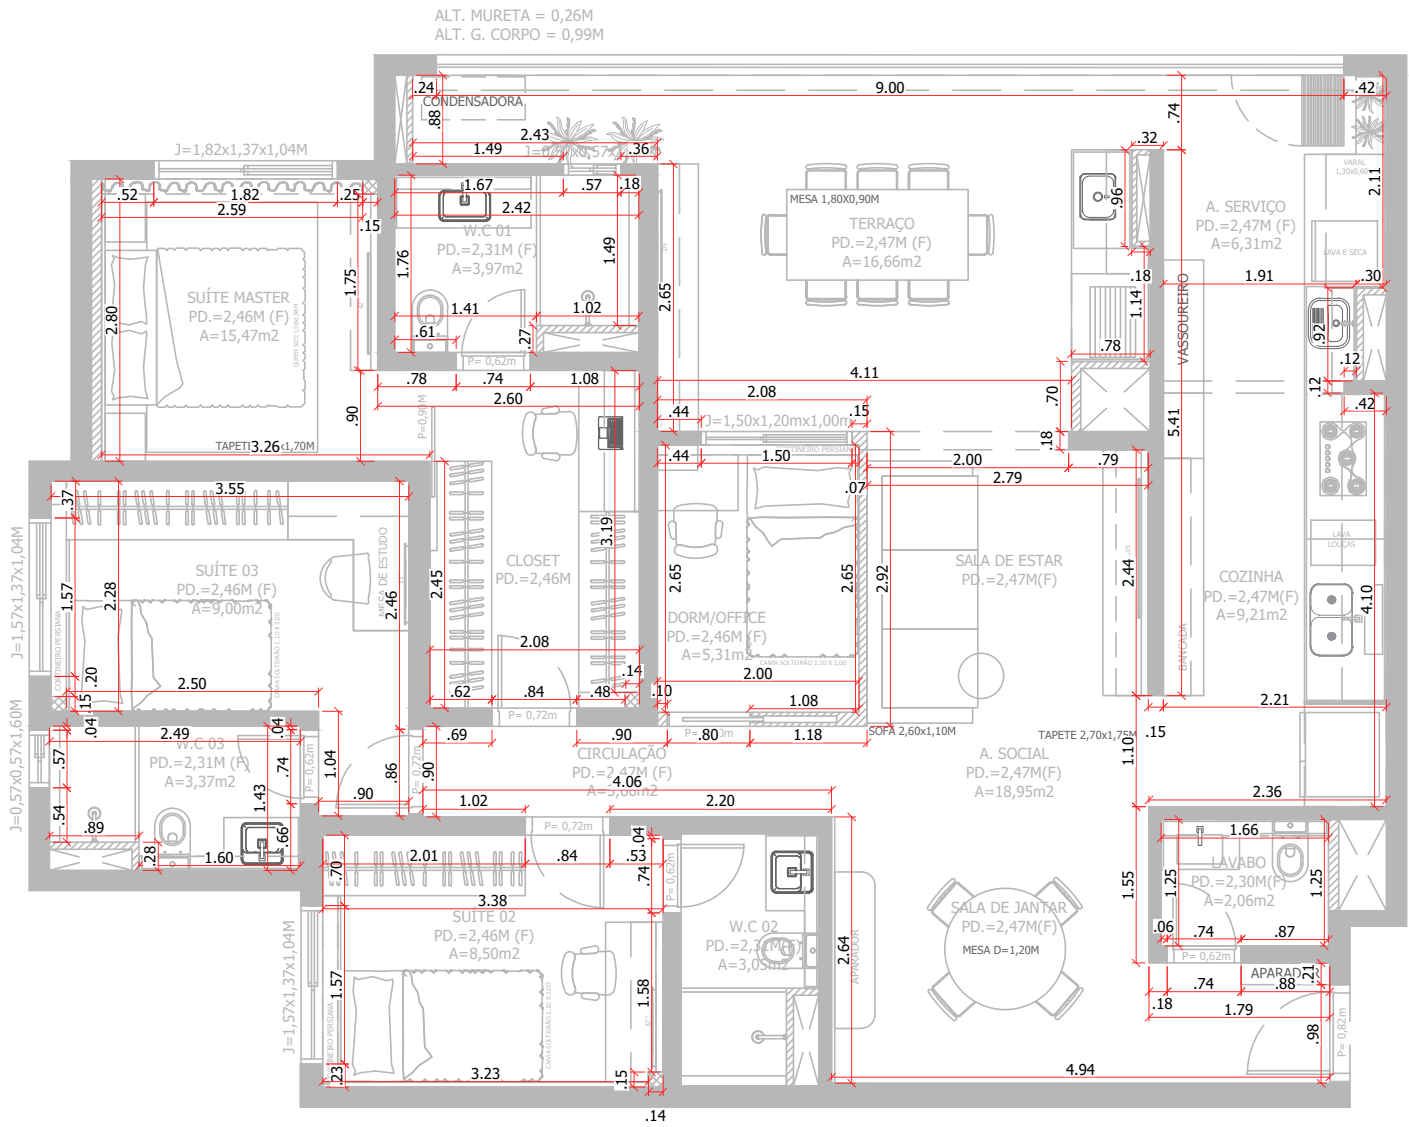

PLANTA BAIXA - ARQUITETURA
ESCALA: 1:75
ÁREA: 114,00m2

R02	01/07/2025	EMIÇÃO FINAL	JESSICA ALVES	VENILMA OLIVEIRA
R01	24/06/2024	EMIÇÃO FINAL	JESSICA ALVES	VENILMA OLIVEIRA
R00	06/03/2024	EMIÇÃO INICIAL	JESSICA ALVES	VENILMA OLIVEIRA
Nº de Revisão:	Data:	Descrição:	Responsável:	Desenhista:

Ciente:	ALEXANDRE E CÁTIA	
Local:	RUA ANTÔNIO BLASQUES, Nº 122, AP 42 - TORRE A - FREGUESIA DO Ó - SÃO PAULO/SP	
Assunto:	ARQUITETURA	Projeto: 91424-PRAC
		Studio Mies arquitetura e interiores

DIREITOS RESERVADOS - LEI: 5772 DE 21/DEZEMBRO/1971. A ALTERAÇÃO SEM AUTORIZAÇÃO DE SEU AUTOR, FICARÁ SUJEITA AS MEDIDAS LEGAIS CABÍVEIS. A ALTERAÇÃO DESTA PROJETO EXIME SEU AUTOR DE QUALQUER RESPONSABILIDADES POSTERIORES. TODO ESTE PROJETO FOI ELABORADO COM UNIDADE DE MEDIDAS EM M (METROS). TODAS AS MEDIDAS, ABERTURAS, PRUMOS E PÉ DIREITO, DEVEM SER CONFERIDAS NO LOCAL, ANTES DA REALIZAÇÃO DE QUALQUER ATIVIDADE. DEFINIÇÕES NÃO DESCRITAS OU DIVERGÊNCIAS ENCONTRADAS, DEVERÃO SER SUBMETIDAS A APROVAÇÃO DO COORDENADOR DO PROJETO ANTES DE ORÇAMENTOS E/OU EXECUÇÕES. ESTE PROJETO FOI CONFIGURADO EM FOLHA A3.	Fase: ☐ LT ☐ EP ☐ AP ☒ EX	Escala: 1:75 Revisão: 2	Folha: 13 16
---	--	----------------------------------	--------------------

MA02 - PRATELEIRA P/ SHAMPOO EM BRANCO PIGUES
ALT. INSTALAÇÃO=1,05M

MA01 - BANCADA EM BRANCO PIGUES COM CUBA DE EMBUTIR/SOBREPOR
ALT. INSTALAÇÃO=0,90M
ALT. SAIA=0,04M
ALT. FRONTÃO=0,10M
ALT. RODABASE=0,10M

MA03 - BANCADA EM BRANCO PIGUES COM CUBA DE EMBUTIR/SOBREPOR
ALT. INSTALAÇÃO=0,90M
ALT. SAIA=0,04M
ALT. FRONTÃO=0,10M
ALT. RODABASE=0,10M

MA04 - PRATELEIRA P/ SHAMPOO EM BRANCO PIGUES ALT. INSTALAÇÃO=0,94M

MA05 - BANCADA EM BRANCO PIGUES COM CUBA DE EMBUTIR/SOBREPOR
ALT. INSTALAÇÃO=0,90M
ALT. SAIA=0,04M
ALT. FRONTÃO=0,10M
ALT. RODABASE=0,10M

MA06 - PRATELEIRA P/ SHAMPOO EM BRANCO PIGUES ALT. INSTALAÇÃO=0,94M

ALT. MURETA = 0,26M
ALT. G. CORPO = 0,99M

INSERIR RODABASE NA BANCADA EXISTENTE
MESA 1,80x0,90M
TERRAÇO
TAMPO EM VERDE UBATUBA PARA CUBA 0,46x0,30M
VER IMAGEM 3D

MA09 - BANCADA EM VERDE UBATUBA COM TANQUE DE EMBUTIR
ALT. INSTALAÇÃO=0,92M
ALT. SAIA=0,04M
ALT. FRONTÃO=0,05M
ALT. RODABASE=0,10M
ÁREA MOLHADA = 1,09x0,44M

MA08 - BANCADA EM VERDE UBATUBA COM CUBA DE EMBUTIR, COOKTOP, CALHA ÚMIDA
ALT. INSTALAÇÃO=0,92M
ALT. SAIA=0,04M
ALT. FRONTÃO=0,05M
ALT. RODABASE=0,10M
ÁREA MOLHADA = 1,29x0,76M

MA07 - BANCADA EM BRANCO PIGUES COM CUBA ESCULPIDA
ALT. INSTALAÇÃO=0,90M
ALT. SAIA=0,04M E 0,25M
ALT. FRONTÃO=0,10M
CUBA ESCULPIDA=0,45x0,29x0,13M

PLANTA BAIXA - MARMORARIA

ESC.: 1:75
ÁREA.:114,00m2

LEGENDA DE MARMORARIA

	INSTALAR BANCADA EM VERDE UBATUBA 02 unid. (VIDE PROJETO DE DET.)
	INSTALAR BANCADA EM BRANCO PIGUES 04 unid. (VIDE PROJETO DE DET.)
	INSTALAR SOLEIRA/ BAGUETE EM BRANCO PRIME 10 unid. (VIDE PROJETO DE DET.)
	INSTALAR PRATELEIRA P/ SHAMPOO EM BRANCO PIGUES 03 unid. (VIDE PROJETO DE DET.)
	TAMPO EM VERDE UBATUBA PARA CUBA 0,46x0,30m 01 unid. (VIDE PROJETO DE DET.)
	INSTALAR RODABASE EM BRANCO PIGUES 06 unid. ALT.: 0,10m (VIDE PROJETO DE DET.)
	INSTALAR RODABASE EM VERDE UBATUBA 15 unid. ALT.: 0,10m (VIDE PROJETO DE DET.)

NOTA

VER PROJETO DE DETALHAMENTO DE MARMORARIA.

LISTA DE LOUÇAS E METAIS

LOCAL	LOUÇAS/ METAIS
LAVABO	TORNEIRA DE MESA BICA ALTA POLO BLACK NOIR 1198.BL33.NO - DECA
COZINHA	CUBA DE EMBUTIR ISIS 2C 34-28 BS EM AÇO INOX AC. 0,69x0,40M - TRAMONTINA
COZINHA	MISTURADOR MONOC. DE MESA COM DUCHA ESPECIAL 2266 C76 - LORENZETTI
COZINHA	CALHA ÚMIDA EM AÇO INOX DE EMBUTIR 0,75x0,18M - TRAMONTINA
A. SERVIÇO	TANQUE DE ENCAIXE HERA 34 L EM AÇO INOX AC. 0,50x0,40x0,23M -TRAMONTINA
A. SERVIÇO	TORNEIRA DE PAREDE LINK BICA CURTA CROMADO 1174.C.LNK - DECA
W.C 01	MISTURADOR MONOC. DE MESA PRETO 2875 B78 - LORENZETTI
W.C 01	CUBA RETANGULAR BRANCO SLIM L.23050.17 0,50x0,30x0,13M - DECA
W.C 02	CUBA QUADRADA COM DECK BRANCO SLIM L.21040.M.17 0,40x0,40x0,13M - DECA
W.C 02	MISTURADOR DE MESA BICA ALTA PARA LAVATÓRIO LINK 1877.C.LNK - DECA
W.C 03	CUBA QUADRADA COM DECK BRANCO SLIM L.21040.M.17 0,40x0,40x0,13M - DECA
W.C 03	MISTURADOR DE MESA BICA ALTA PARA LAVATÓRIO LINK 1877.C.LNK - DECA


R02	01/07/2025	EMIÇÃO FINAL	JESSICA ALVES	VENILMA OLIVEIRA
R01	24/06/2024	EMIÇÃO FINAL	JESSICA ALVES	VENILMA OLIVEIRA
R00	06/03/2024	EMIÇÃO INICIAL	JESSICA ALVES	VENILMA OLIVEIRA
Nº de Revisão:	Data:	Descrição:	Responsável:	Desenhista:

Cliente:
ALEXANDRE E CÁTIA
Local:
RUA ANTÔNIO BLASQUES, Nº 122, AP 42 - TORRE A - FREGUESIA DO Ó - SÃO PAULO/SP
Assunto:
MARMORARIA
Projeto:
91424-PRAC

Studio Mies
arquitetura e interiores

DIREITOS RESERVADOS - LEI: 5772 DE 21/DEZEMBRO/1971.
A ALTERAÇÃO SEM AUTORIZAÇÃO DE SEU AUTOR, FICARÁ SUJEITA AS MEDIDAS LEGAIS CABÍVEIS.
A ALTERAÇÃO DESTA PROJETO EXIME SEU AUTOR DE QUALQUER RESPONSABILIDADES POSTERIORES.
TODO ESTE PROJETO FOI ELABORADO COM UNIDADE DE MEDIDAS EM M (METROS).
TODAS AS MEDIDAS, ABERTURAS, PRUMOS E PÉ DIREITO, DEVEM SER CONFERIDAS NO LOCAL, ANTES DA REALIZAÇÃO DE QUALQUER ATIVIDADE.
DEFINIÇÕES NÃO DESCRITAS OU DIVERGÊNCIAS ENCONTRADAS, DEVERÃO SER SUBMETIDAS A APROVAÇÃO DO COORDENADOR DO PROJETO ANTES DE ORÇAMENTOS E/OU EXECUÇÕES.
ESTE PROJETO FOI CONFIGURADO EM FOLHA A3.

Fase:
☐ LT
☐ EP
☐ AP
☒ EX
Escala:
1:75
Revisão:
2
Folha:
14
16

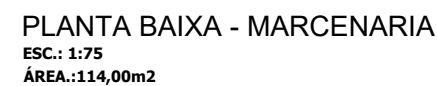

Cliente: ALEXANDRE E CÁTIA	Local: RUA ANTÔNIO BLASQUES, Nº 122, AP 42 - TORRE A - FREGUESIA DO Ó - SÃO PAULO/SP	
Assunto: MARCENARIA	Projeto: 91424-PRAC	arquitetura e interiores


LEGENDA DE VIDRAÇARIA

	ESPELHO ORGÂNICO 01 unid. 0,70x1,00m (VER DET.01)
	ESPELHO LAP. RETO 03 unid. (VIDE PROJETO)
	BOX DE VIDRO TEMP. TRANSLÚCIDO PISO-TETO 01 unid. 1,49x2,31m COR: PRETO
	BOX DE VIDRO TEMP. TRANSLÚCIDO PISO-TETO 01 unid. 1,15x2,31m COR: INOX
	BOX DE VIDRO TEMP. TRANSLÚCIDO CAMARÃO 01 unid. 1,05x2,00m COR: INOX
	TAMPO DE VIDRO TEMPERADO INCOLOR 01 unid. 2,35x0,40M (VIDE PROJETO)
	FECHAMENTO DA SACADA CONF. PROJETO DO CONDOMÍNIO
	FECHAMENTO DE VIDRO TEMP. LEITOSO BRANCO 01 unid. (CONF. MEDIDAS IN LOCO)


NOTA

VERIFICAR MANUAL DO CONDOMÍNIO PARA O PROJETO DO FECHAMENTO DA SACADA/TERRAÇO.

DET. 01

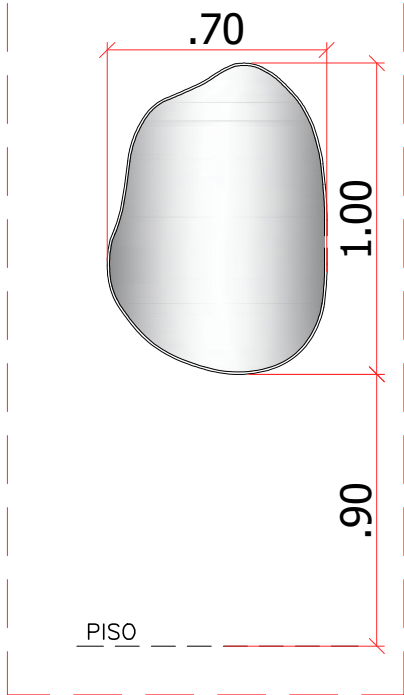

esc 1:25

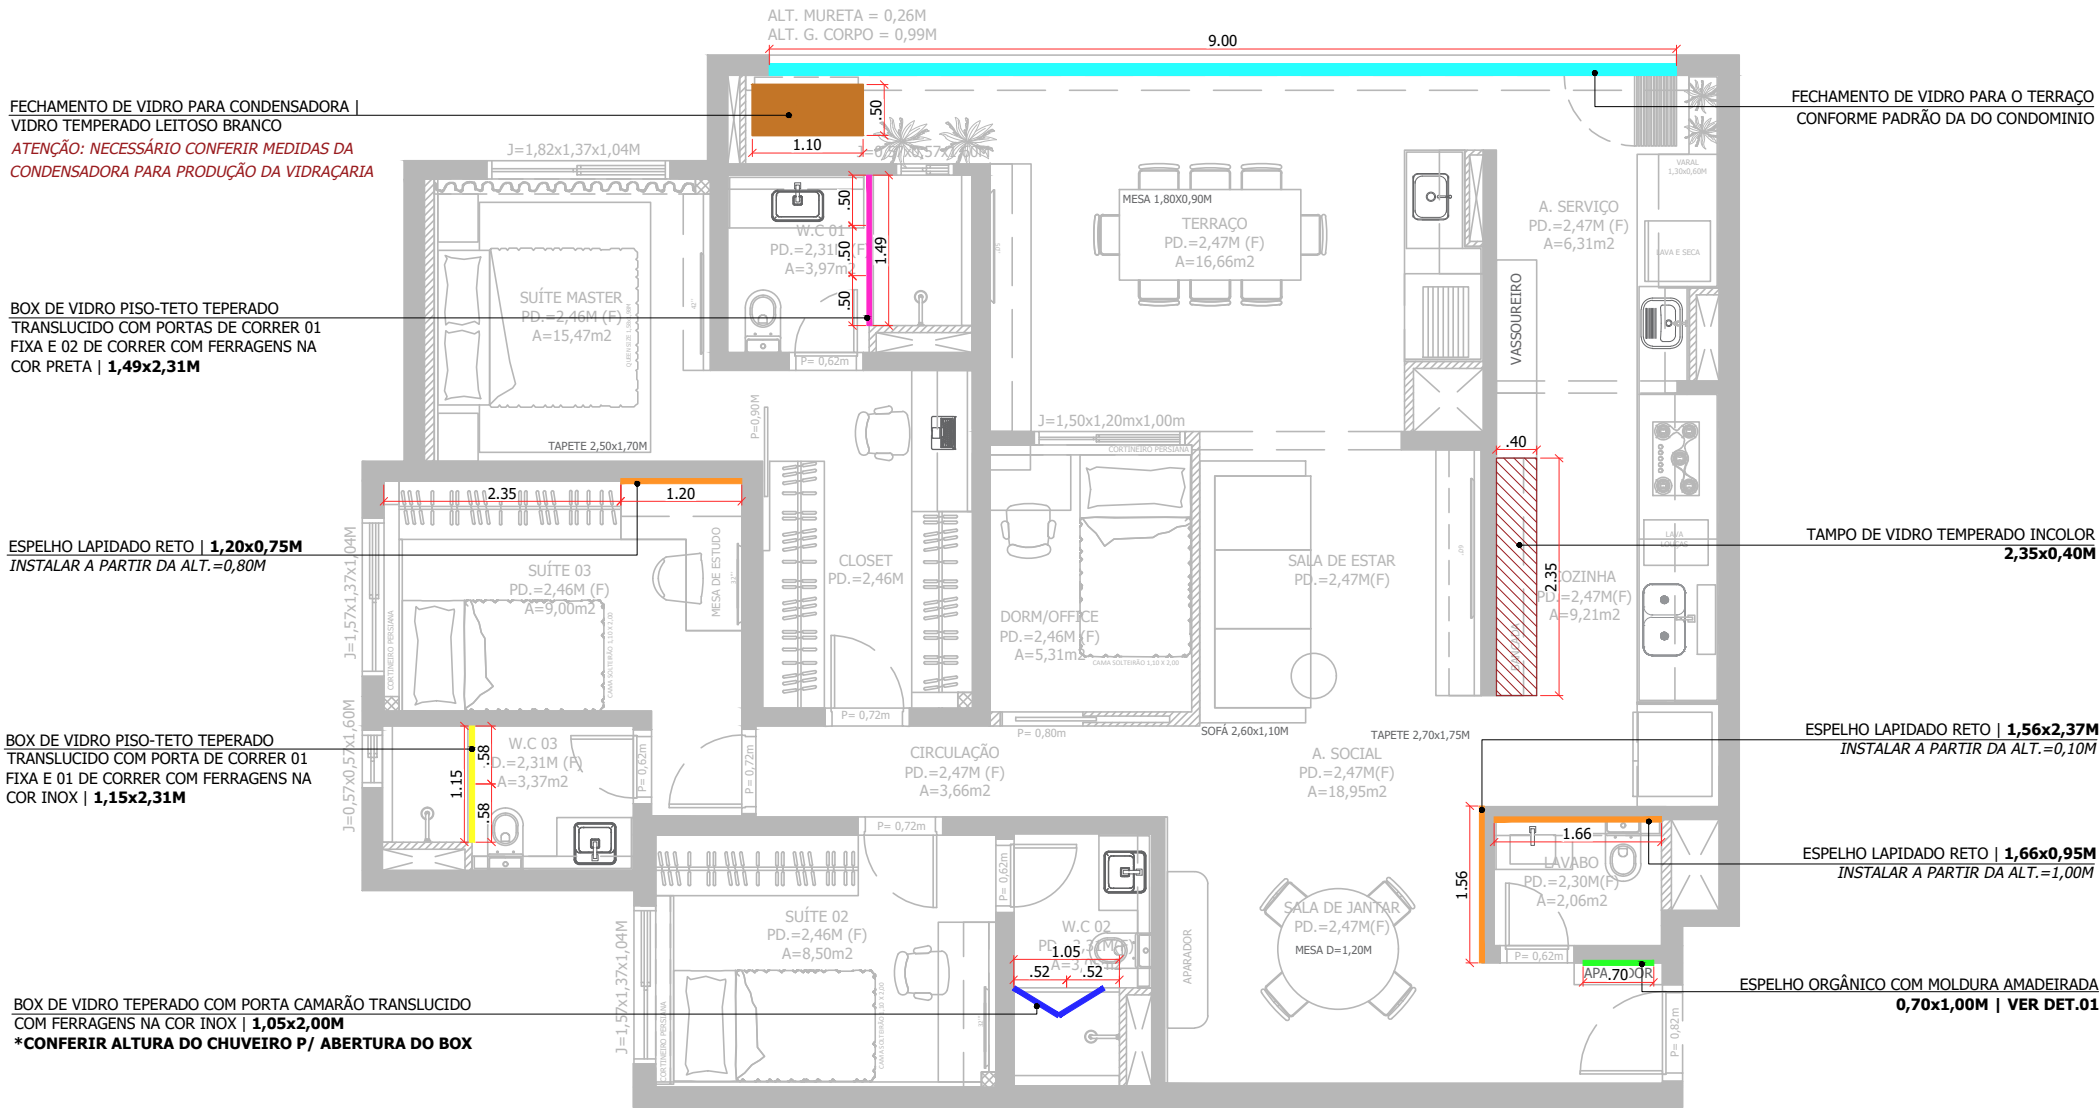

PLANTA BAIXA - VIDRAÇARIA

ESC.: 1:75
ÁREA.:114,00m2

R02	01/07/2025	EMIÇÃO FINAL	JESSICA ALVES	VENILMA OLIVEIRA
R01	24/06/2024	EMIÇÃO FINAL	JESSICA ALVES	VENILMA OLIVEIRA
R00	06/03/2024	EMIÇÃO INICIAL	JESSICA ALVES	VENILMA OLIVEIRA
Nº de Revisão:	Data:	Descrição:	Responsável:	Desenhista:

Cliente:	ALEXANDRE E CÁTIA	Projeto:	91424-PRAC	
Local:	RUA ANTÔNIO BLASQUES, Nº 122, AP 42 - TORRE A - FREGUESIA DO Ó - SÃO PAULO/SP			
Assunto:	VIDRAÇARIA			

DIREITOS RESERVADOS - LEI: 5772 DE 21/DEZEMBRO/1971.
A ALTERAÇÃO SEM AUTORIZAÇÃO DE SEU AUTOR, FICARÁ SUJEITA AS MEDIDAS LEGAIS CABÍVEIS.
A ALTERAÇÃO DESTA PROJETO EXIME SEU AUTOR DE QUAISQUER RESPONSABILIDADES POSTERIORES.
TODO ESTE PROJETO FOI ELABORADO COM UNIDADE DE MEDIDAS EM M (METROS).
TODAS AS MEDIDAS, ABERTURAS, PRUMOS E PÉ DIREITO, DEVEM SER CONFERIDAS NO LOCAL, ANTES DA REALIZAÇÃO DE QUALQUER ATIVIDADE.
DEFINIÇÕES NÃO DESCRITAS OU DIVERGÊNCIAS ENCONTRADAS, DEVERÃO SER SUBMETIDAS A APROVAÇÃO DO COORDENADOR DO PROJETO ANTES DE ORÇAMENTOS E/OU EXECUÇÕES.
ESTE PROJETO FOI CONFIGURADO EM FOLHA A3.

Fase:	Escala:	Folha:
☐ LT ☐ EP ☐ AP ☒ EX	1:75 Revisão: 2	16 / 16