

ESTUDO PRELIMINAR - R02



COBERTURA BRENO

JULHO 2025

guaja.cc + facury.

PLANTA

1º andar

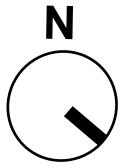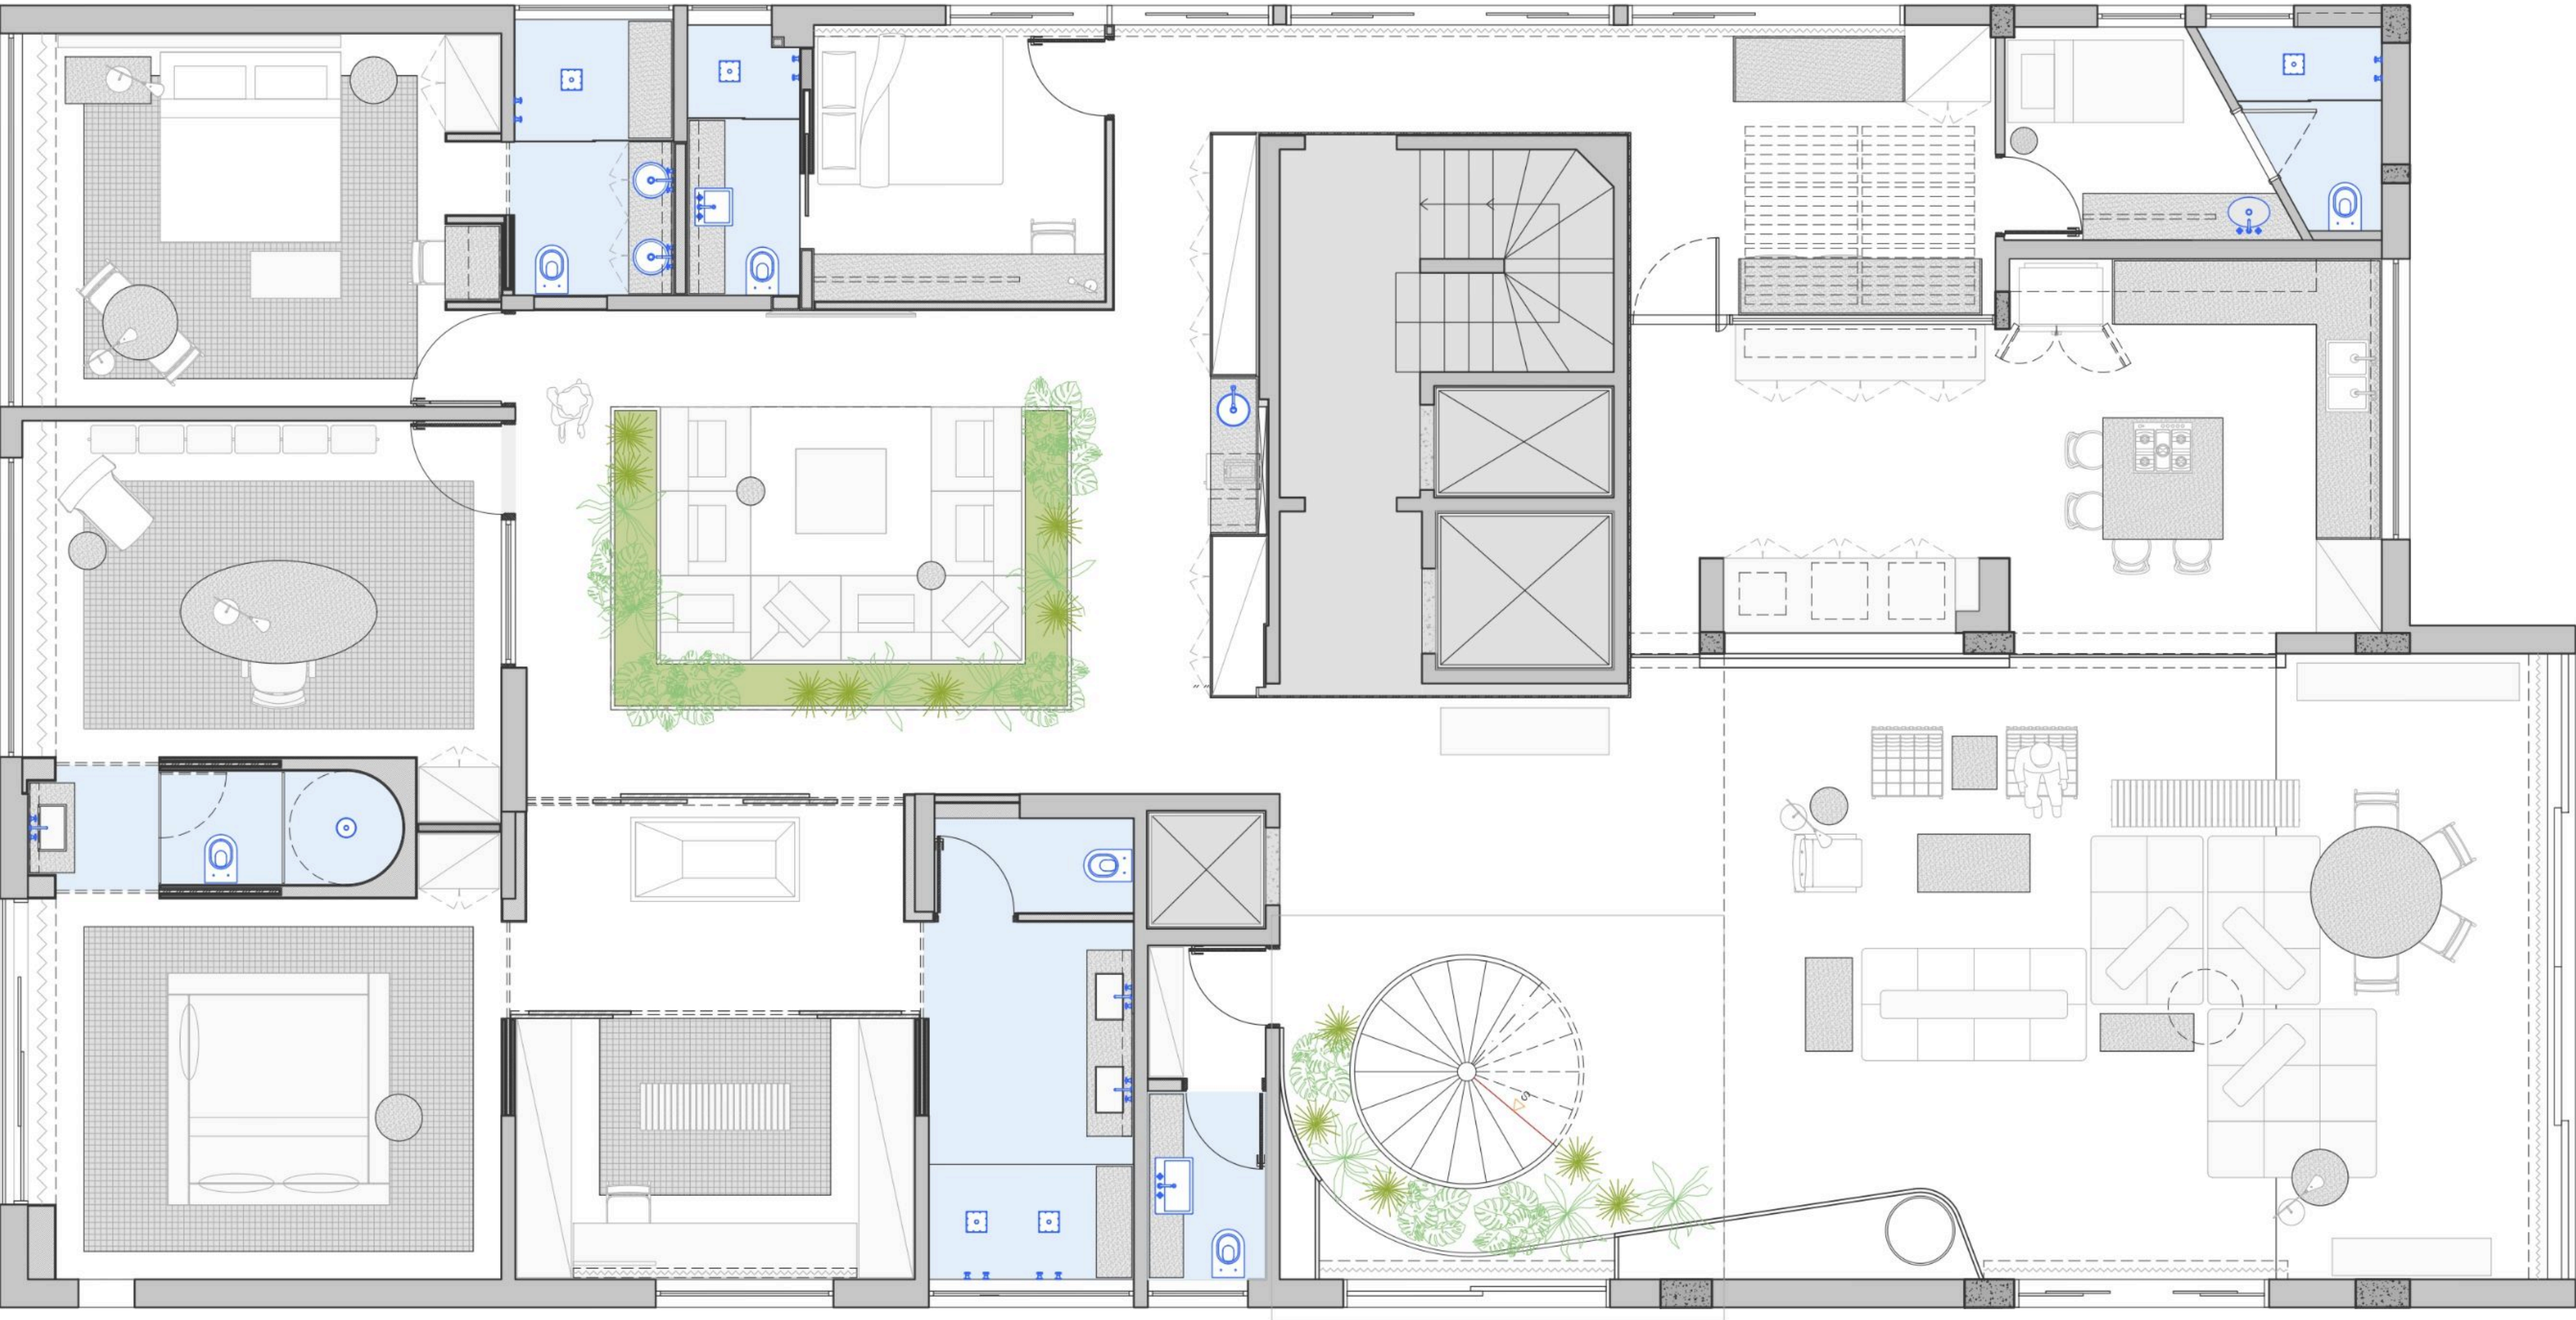

0 1 2m




+



facury.


PLANTA

1º andar

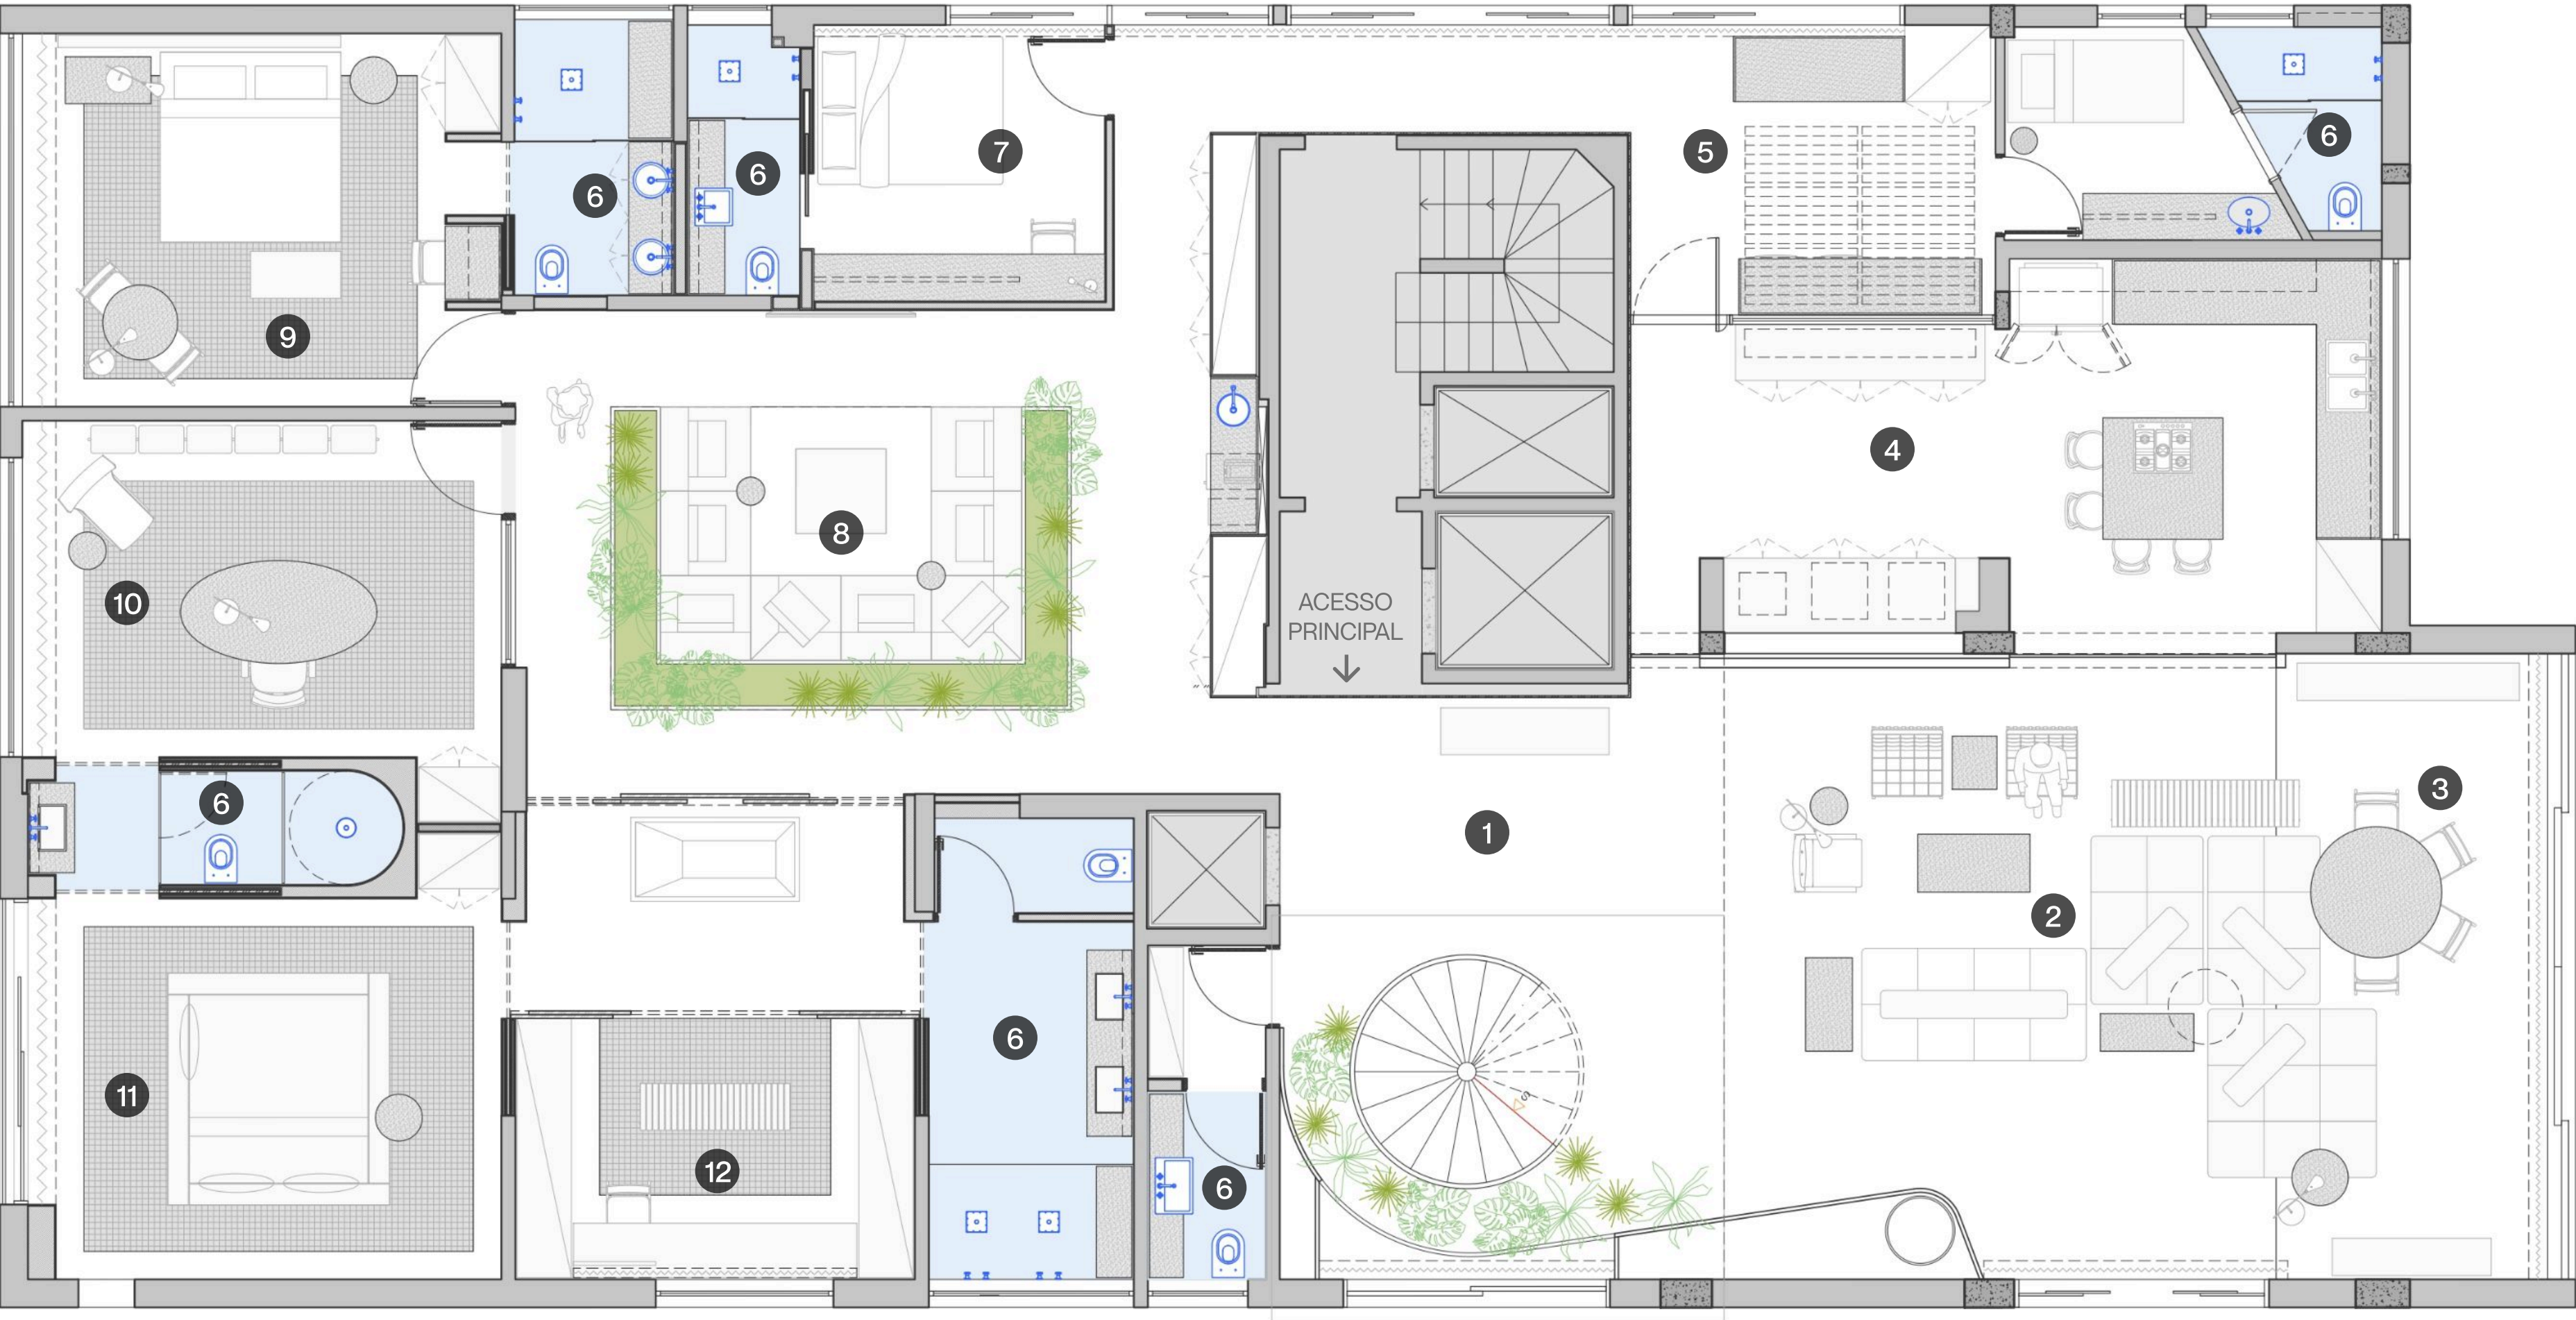

LEGENDA

- 1 Entrada
- 2 Sala de Estar
- 3 Sala de Jantar
- 4 Cozinha
- 5 Área de Serviço
- 6 Banheiro
- 7 Quarto de Apoio
- 8 Jardim de Inverno
- 9 Quarto de Hóspedes
- 10 Escritório
- 11 Quarto Principal
- 12 Closet

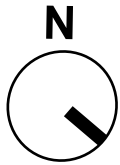


0 1 2m



facury.

PLANTA

1º andar - demolição

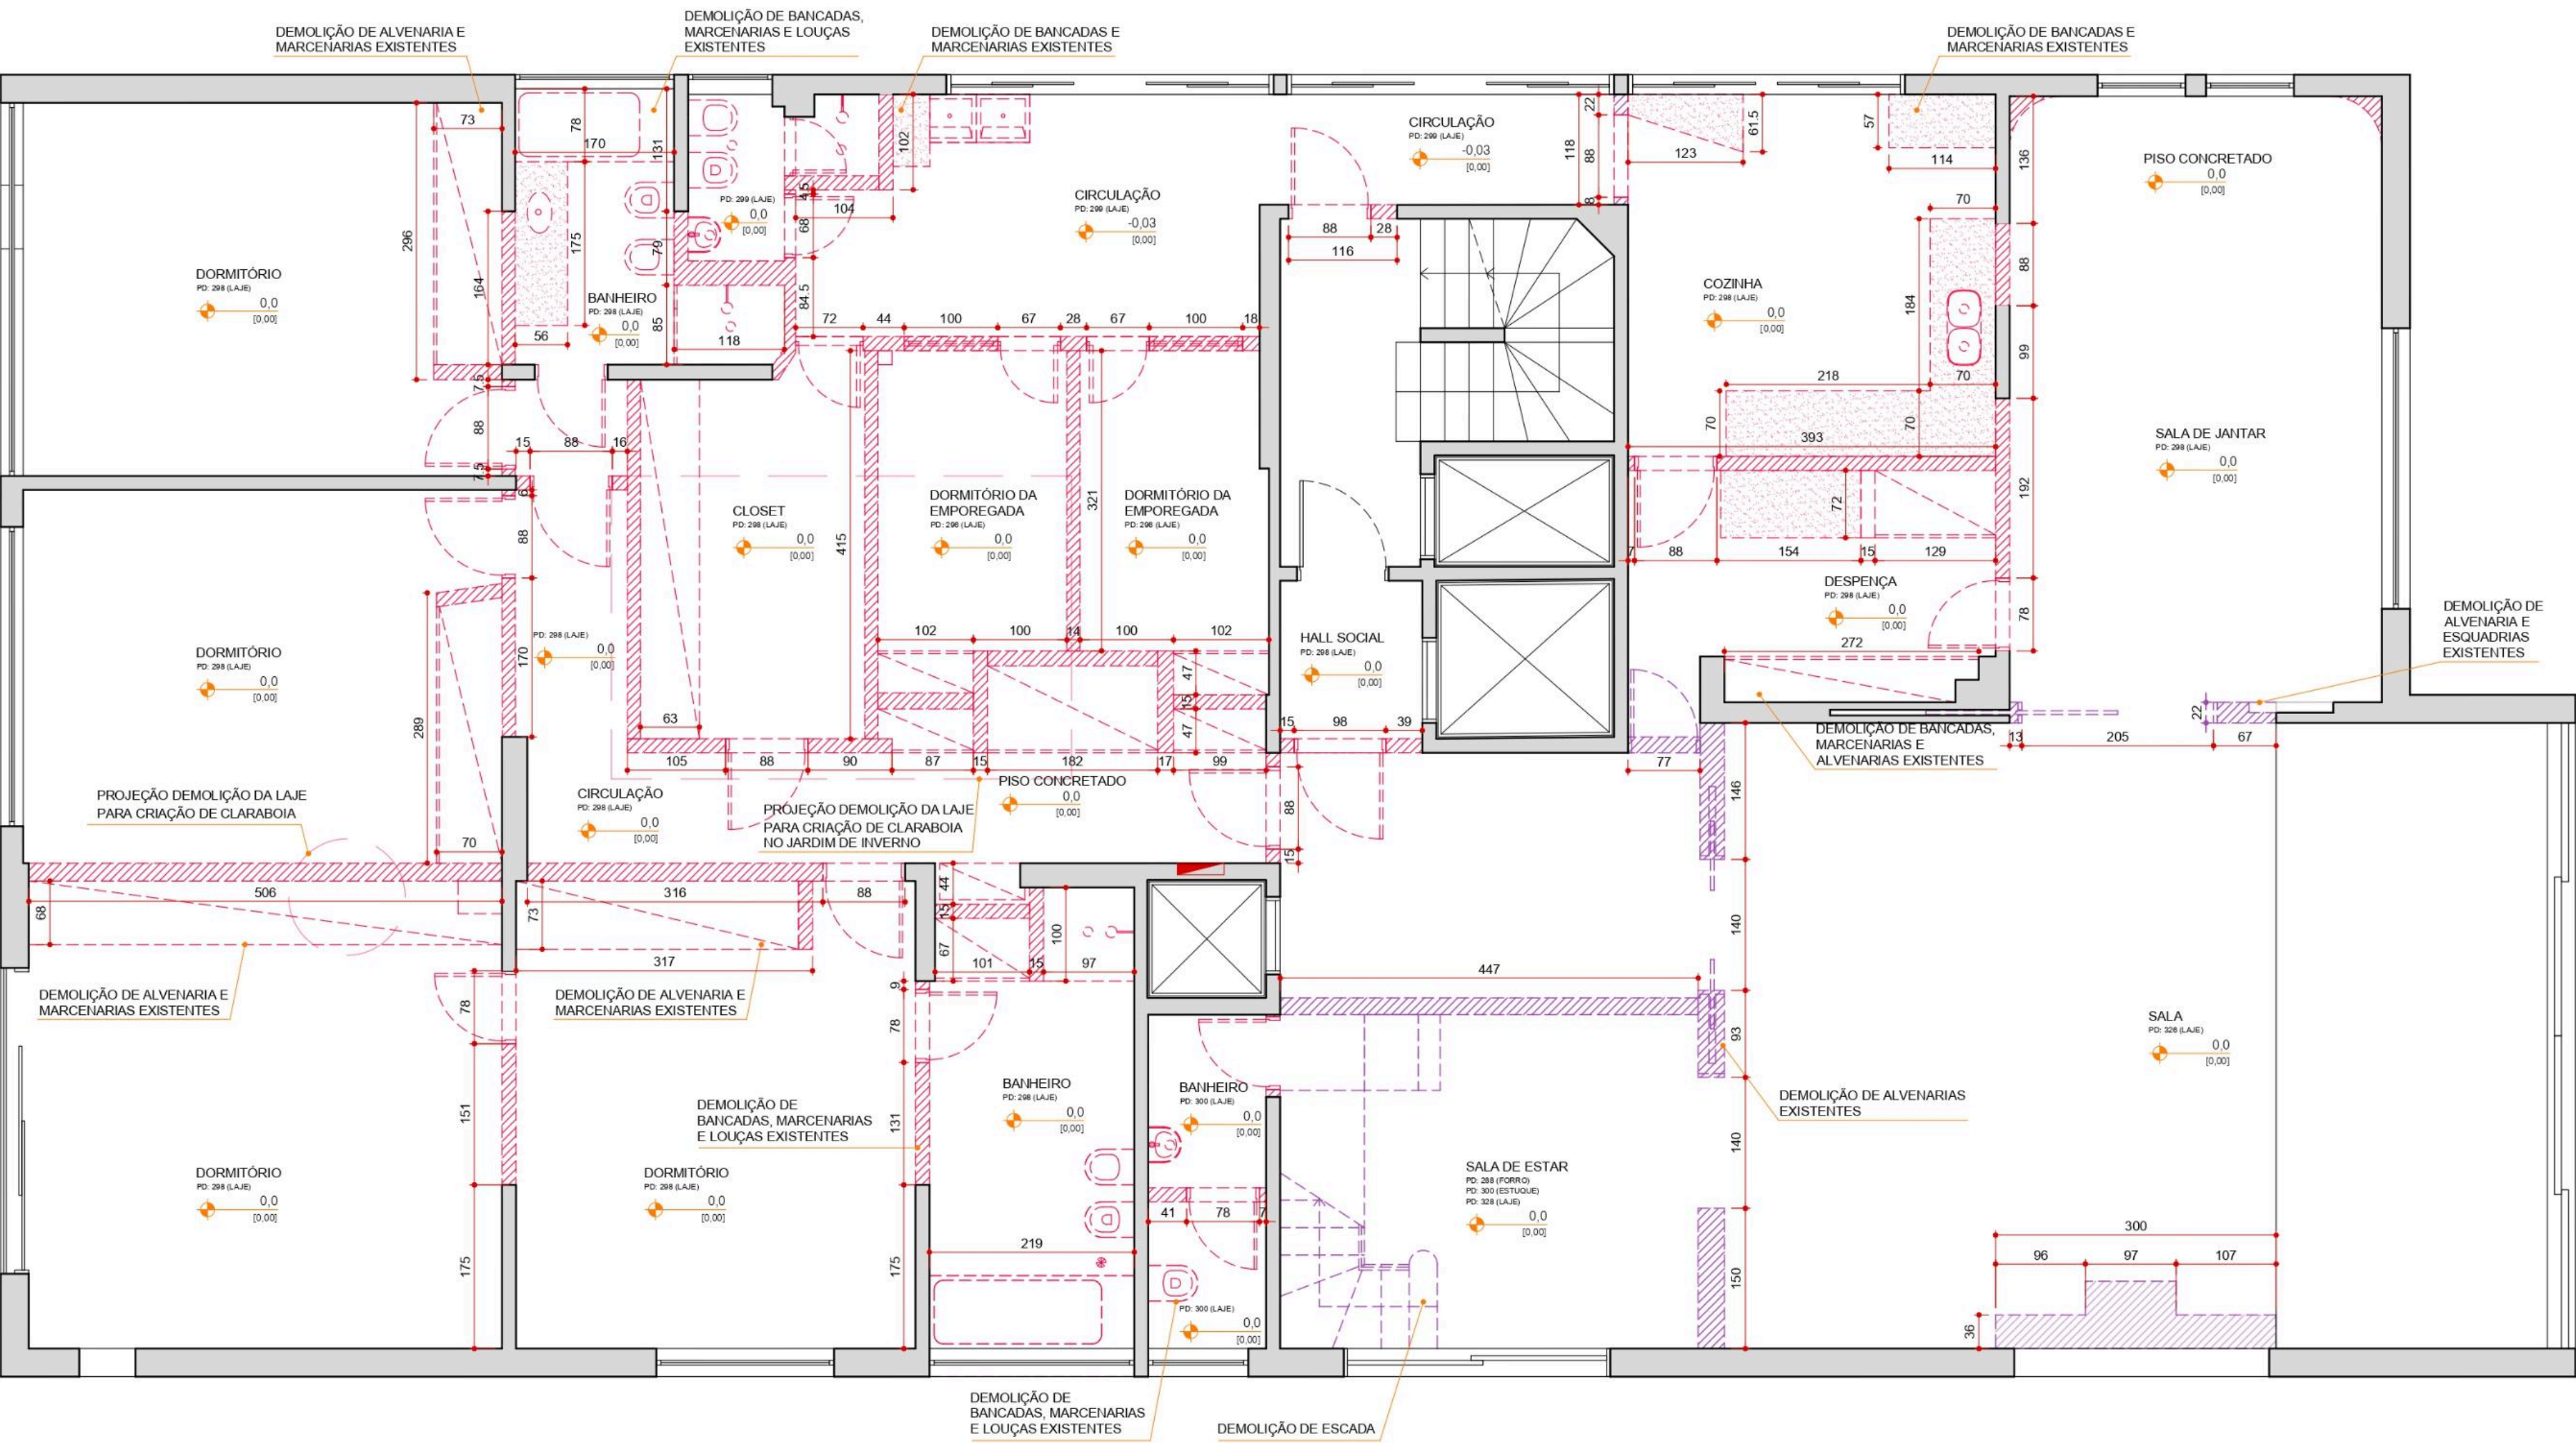


- LEGENDA
- Demolir
 - Demolir em análise



PLANTA

1º andar - construção

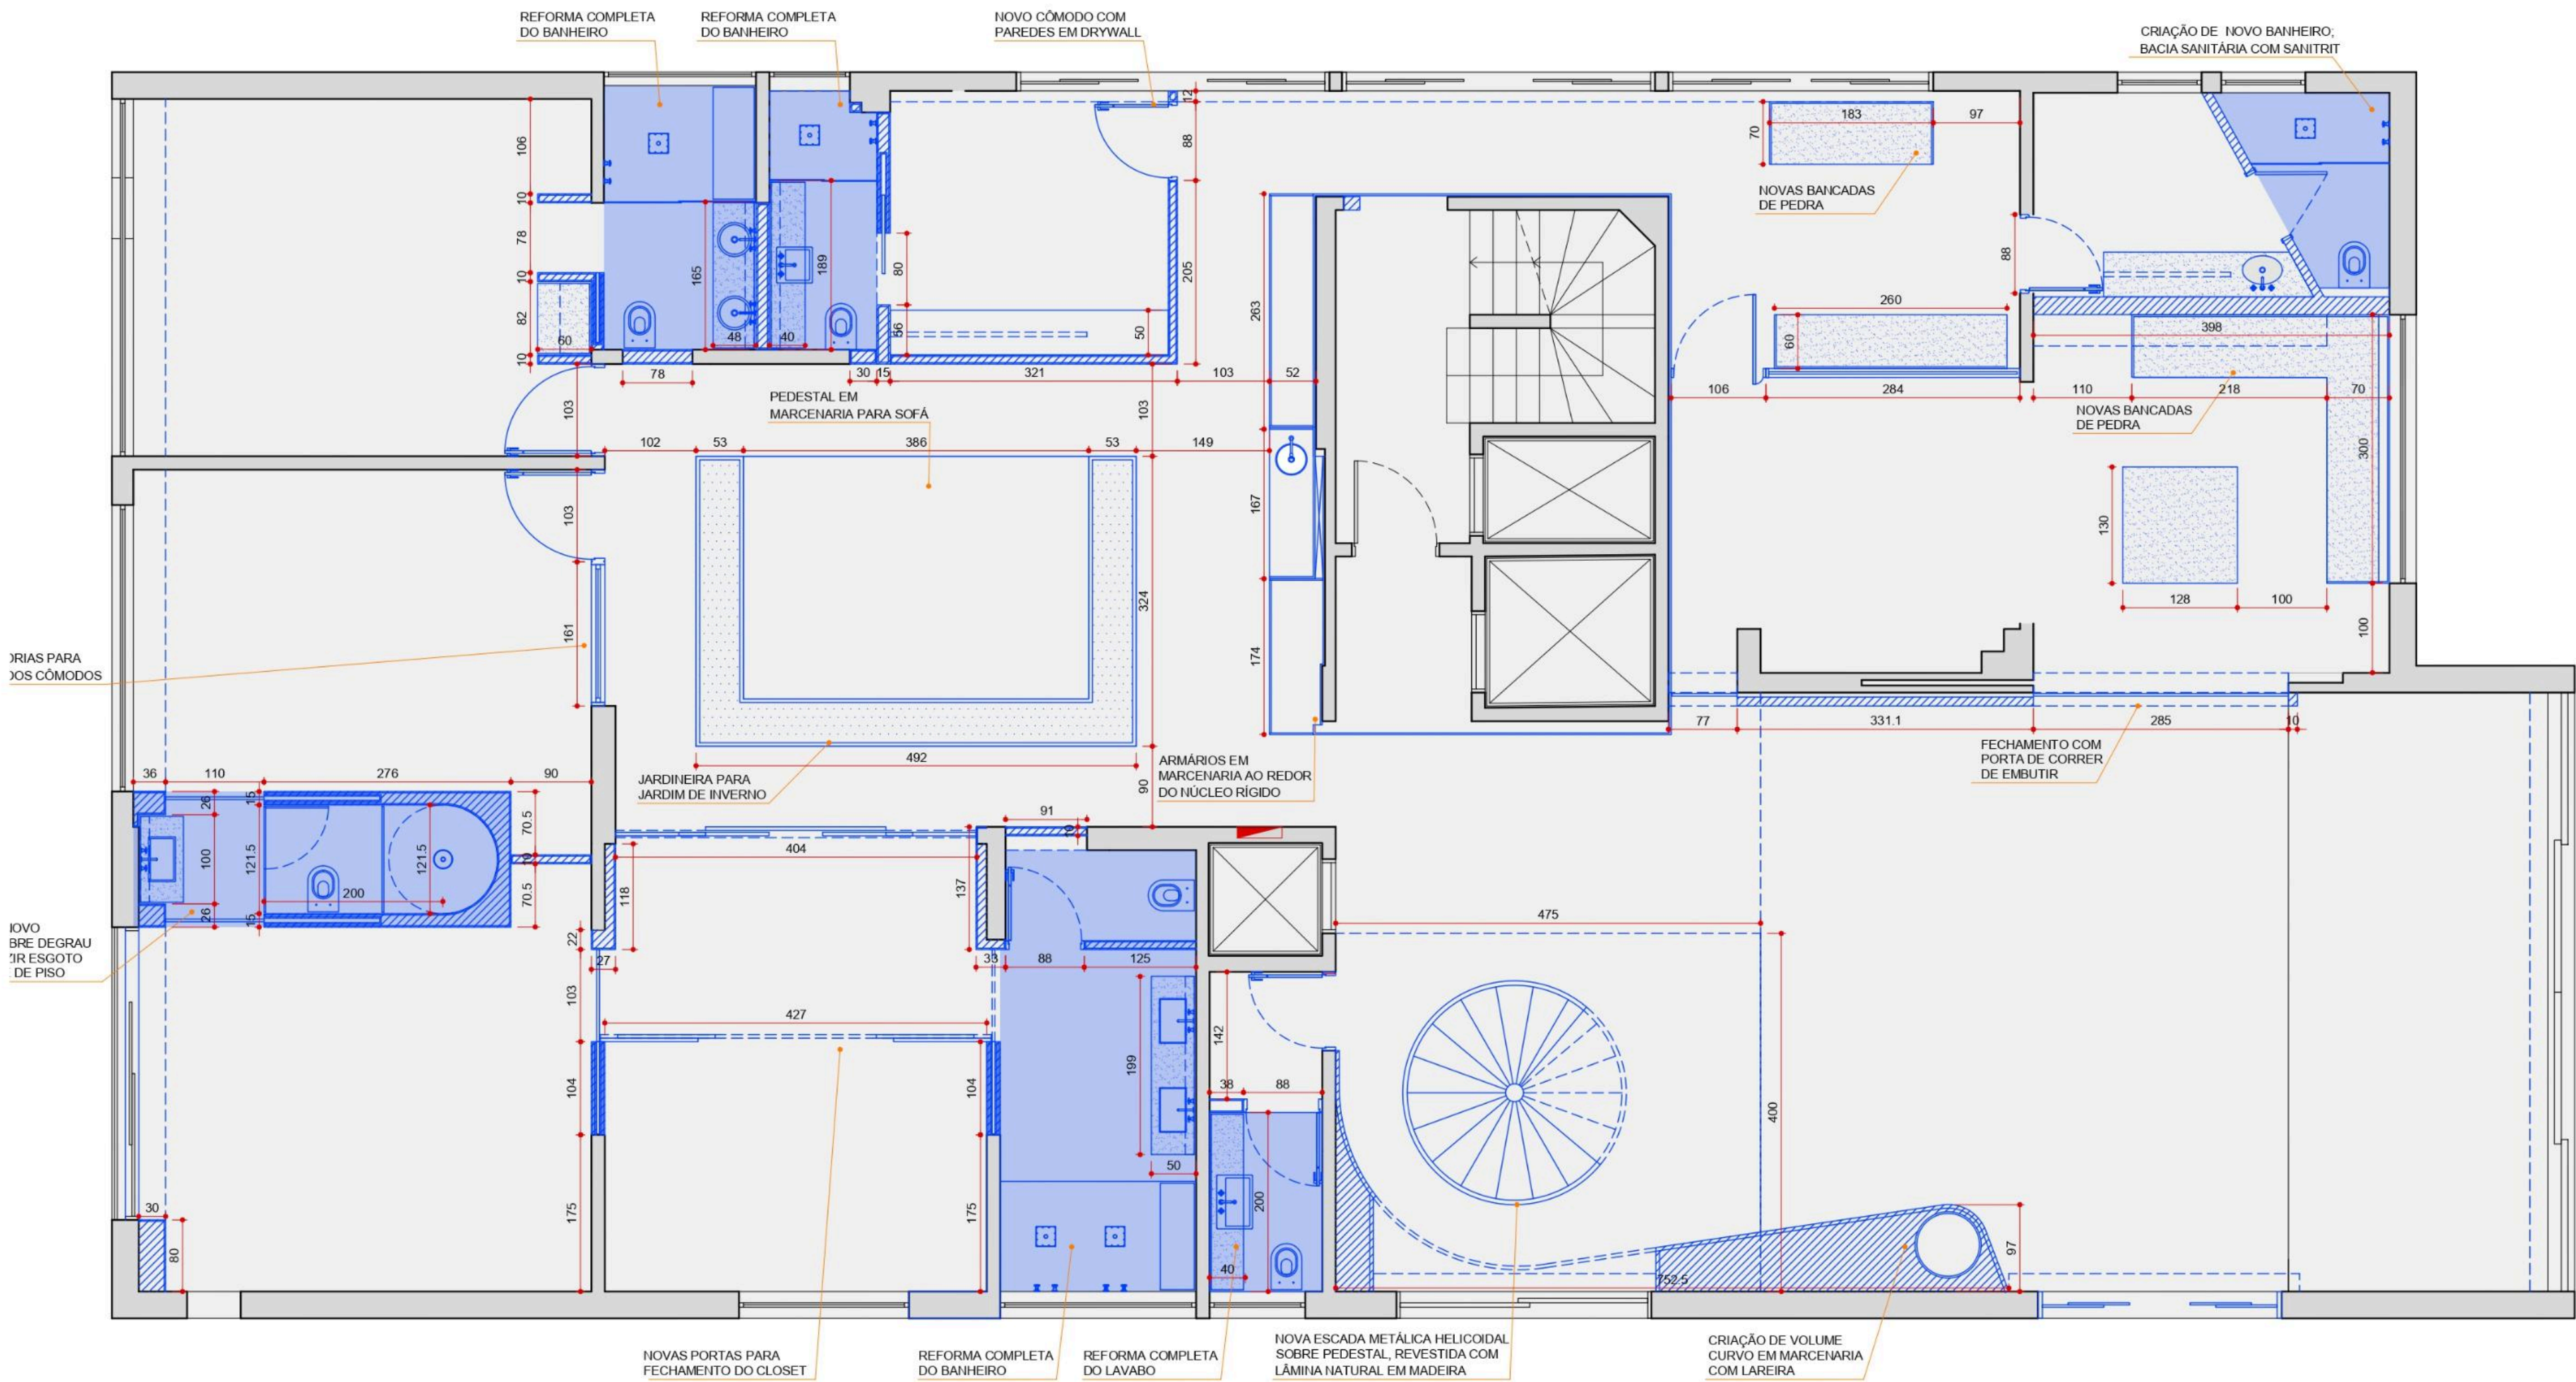


LEGENDA

● Construir

ESCADA HELICOIDAL

Dados iniciais

- Pé-direito: 3780 mm
- Diâmetro da escada: 2500 mm
- Diâmetro do pilar: 200 mm
- Altura do pilar: 6730 mm
- Número de degraus: 21
- Ângulo de rotação da escada: 540°
- Espessura do degrau: 50 mm
- Altura entre degraus (espelho): 180 mm
- Ângulo do degrau: 25,7°
- Comprimento do degrau: 1150 mm
- Largura do degrau efetiva: 556 mm
- Largura do degrau externo: 571 mm
- Material do piso: metálico
- Material do guarda-corpo: lamina de madeira

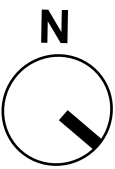


0 1 2m



PLANTA



1º andar - materiais

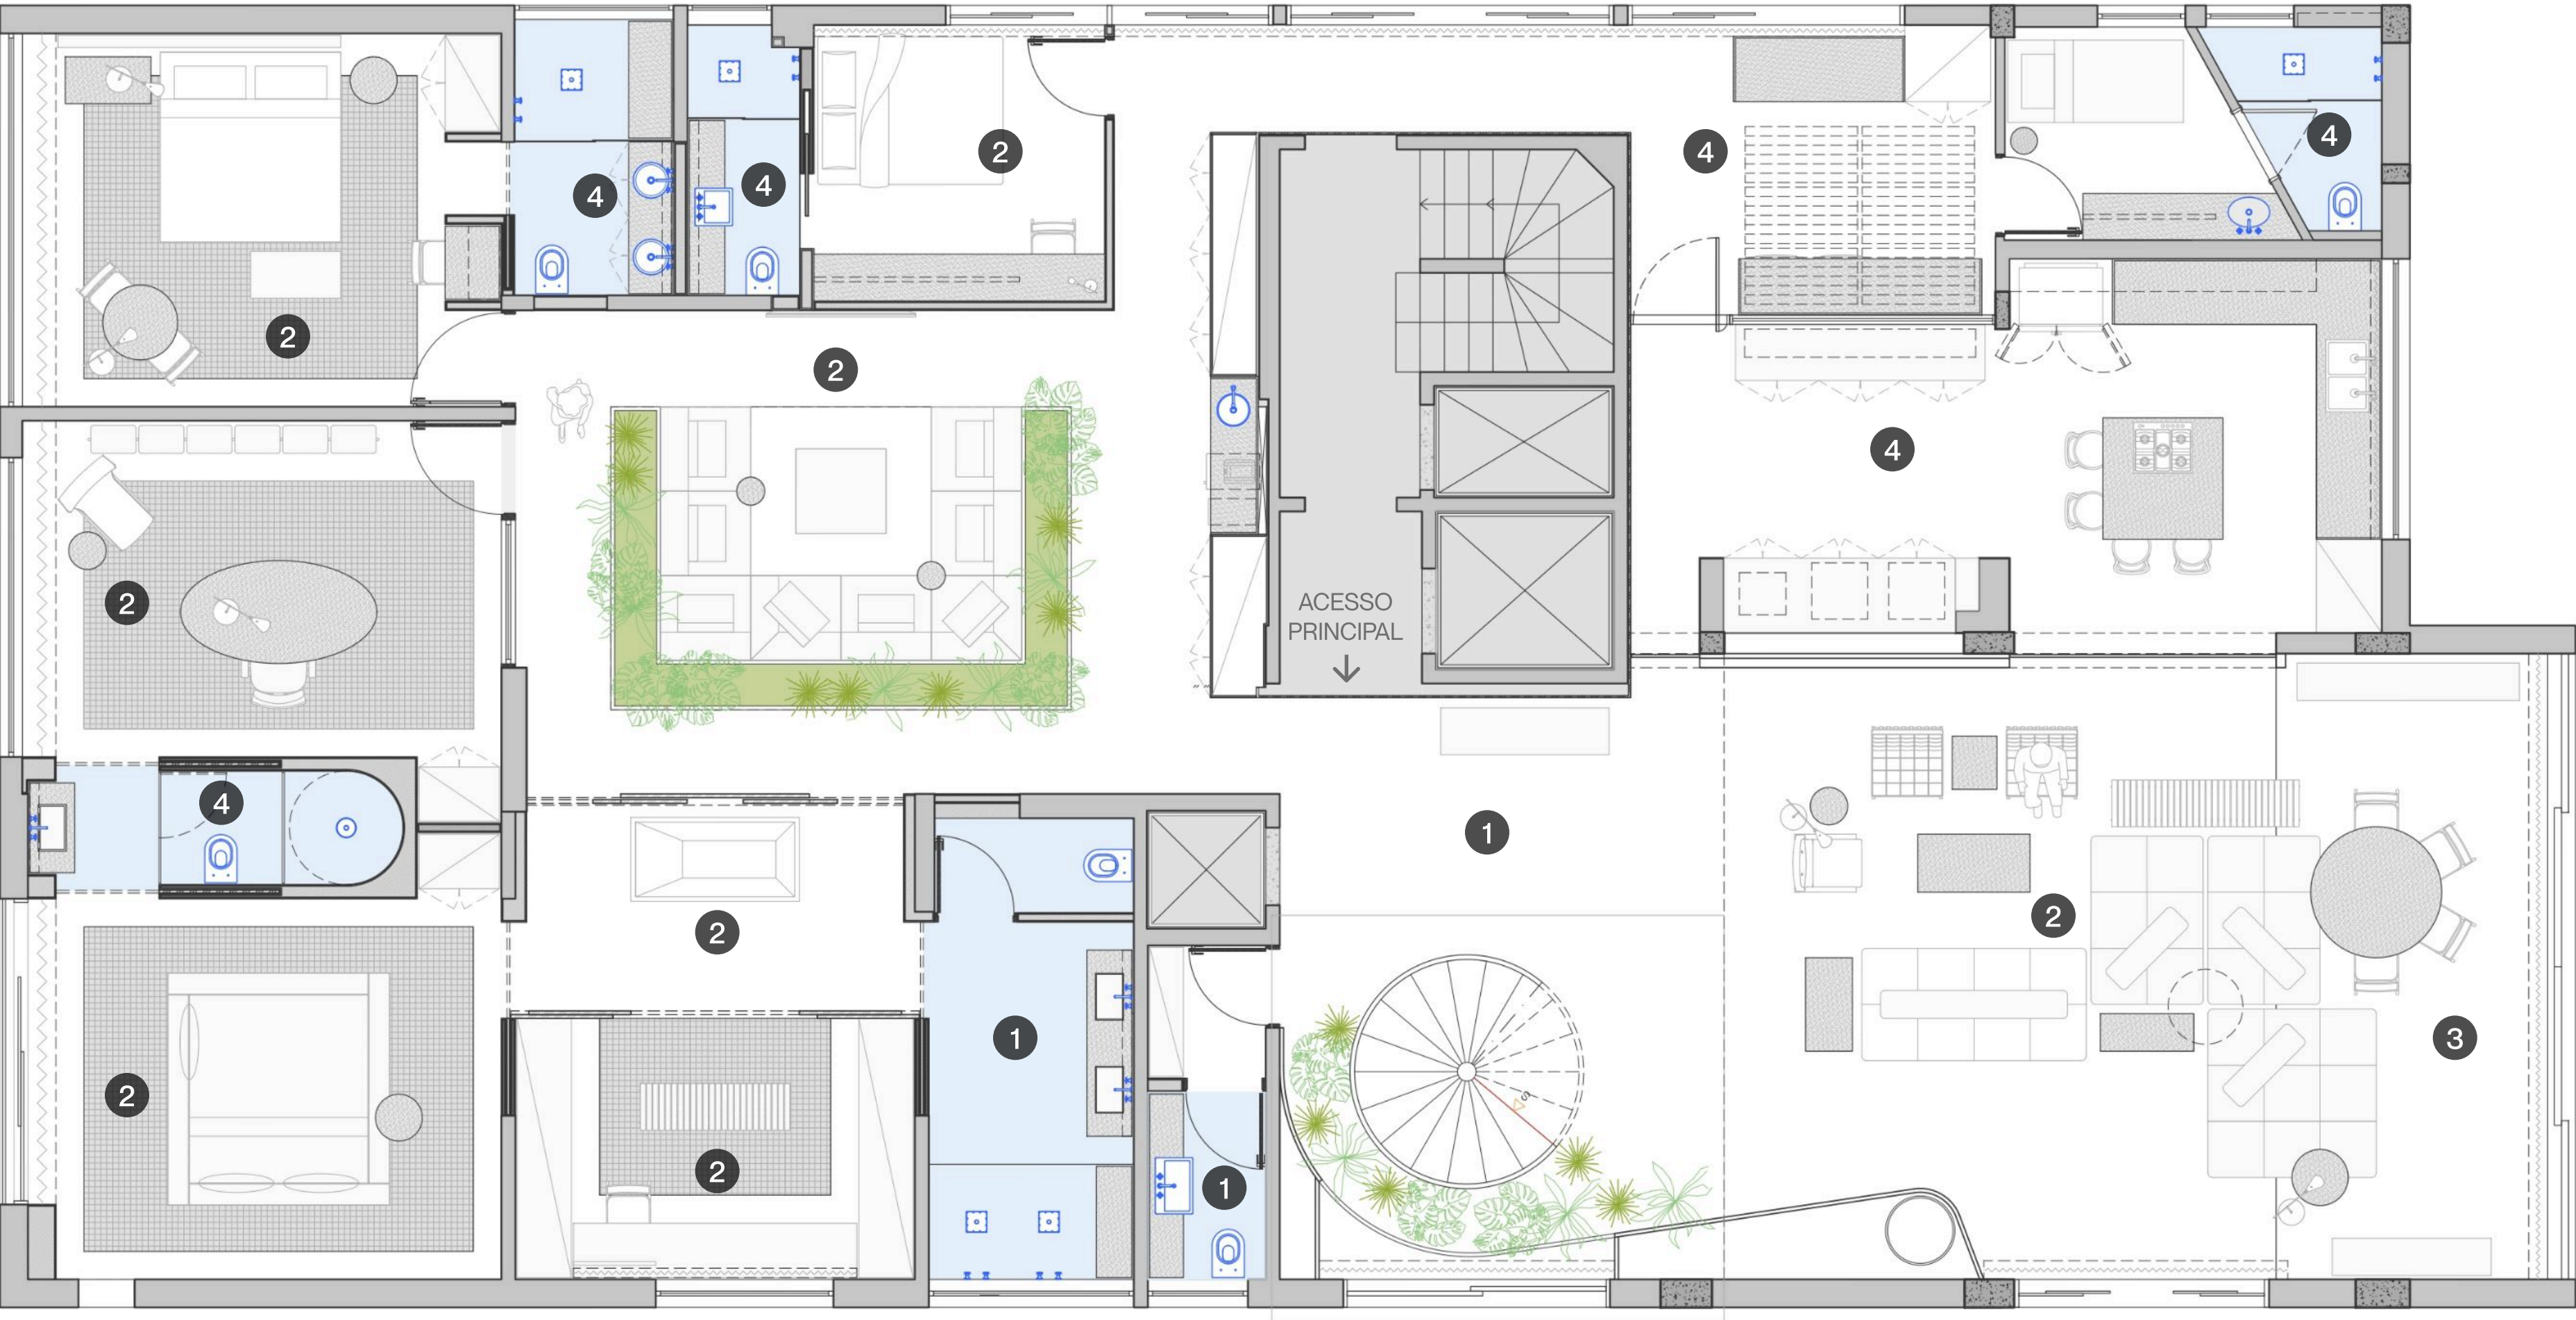

- LEGENDA
- 1 Mármore
 - 2 Madeira
 - 3 Marmorite existente
 - 4 Porcelanato



PLANTA
2º andar

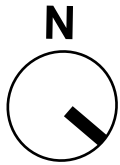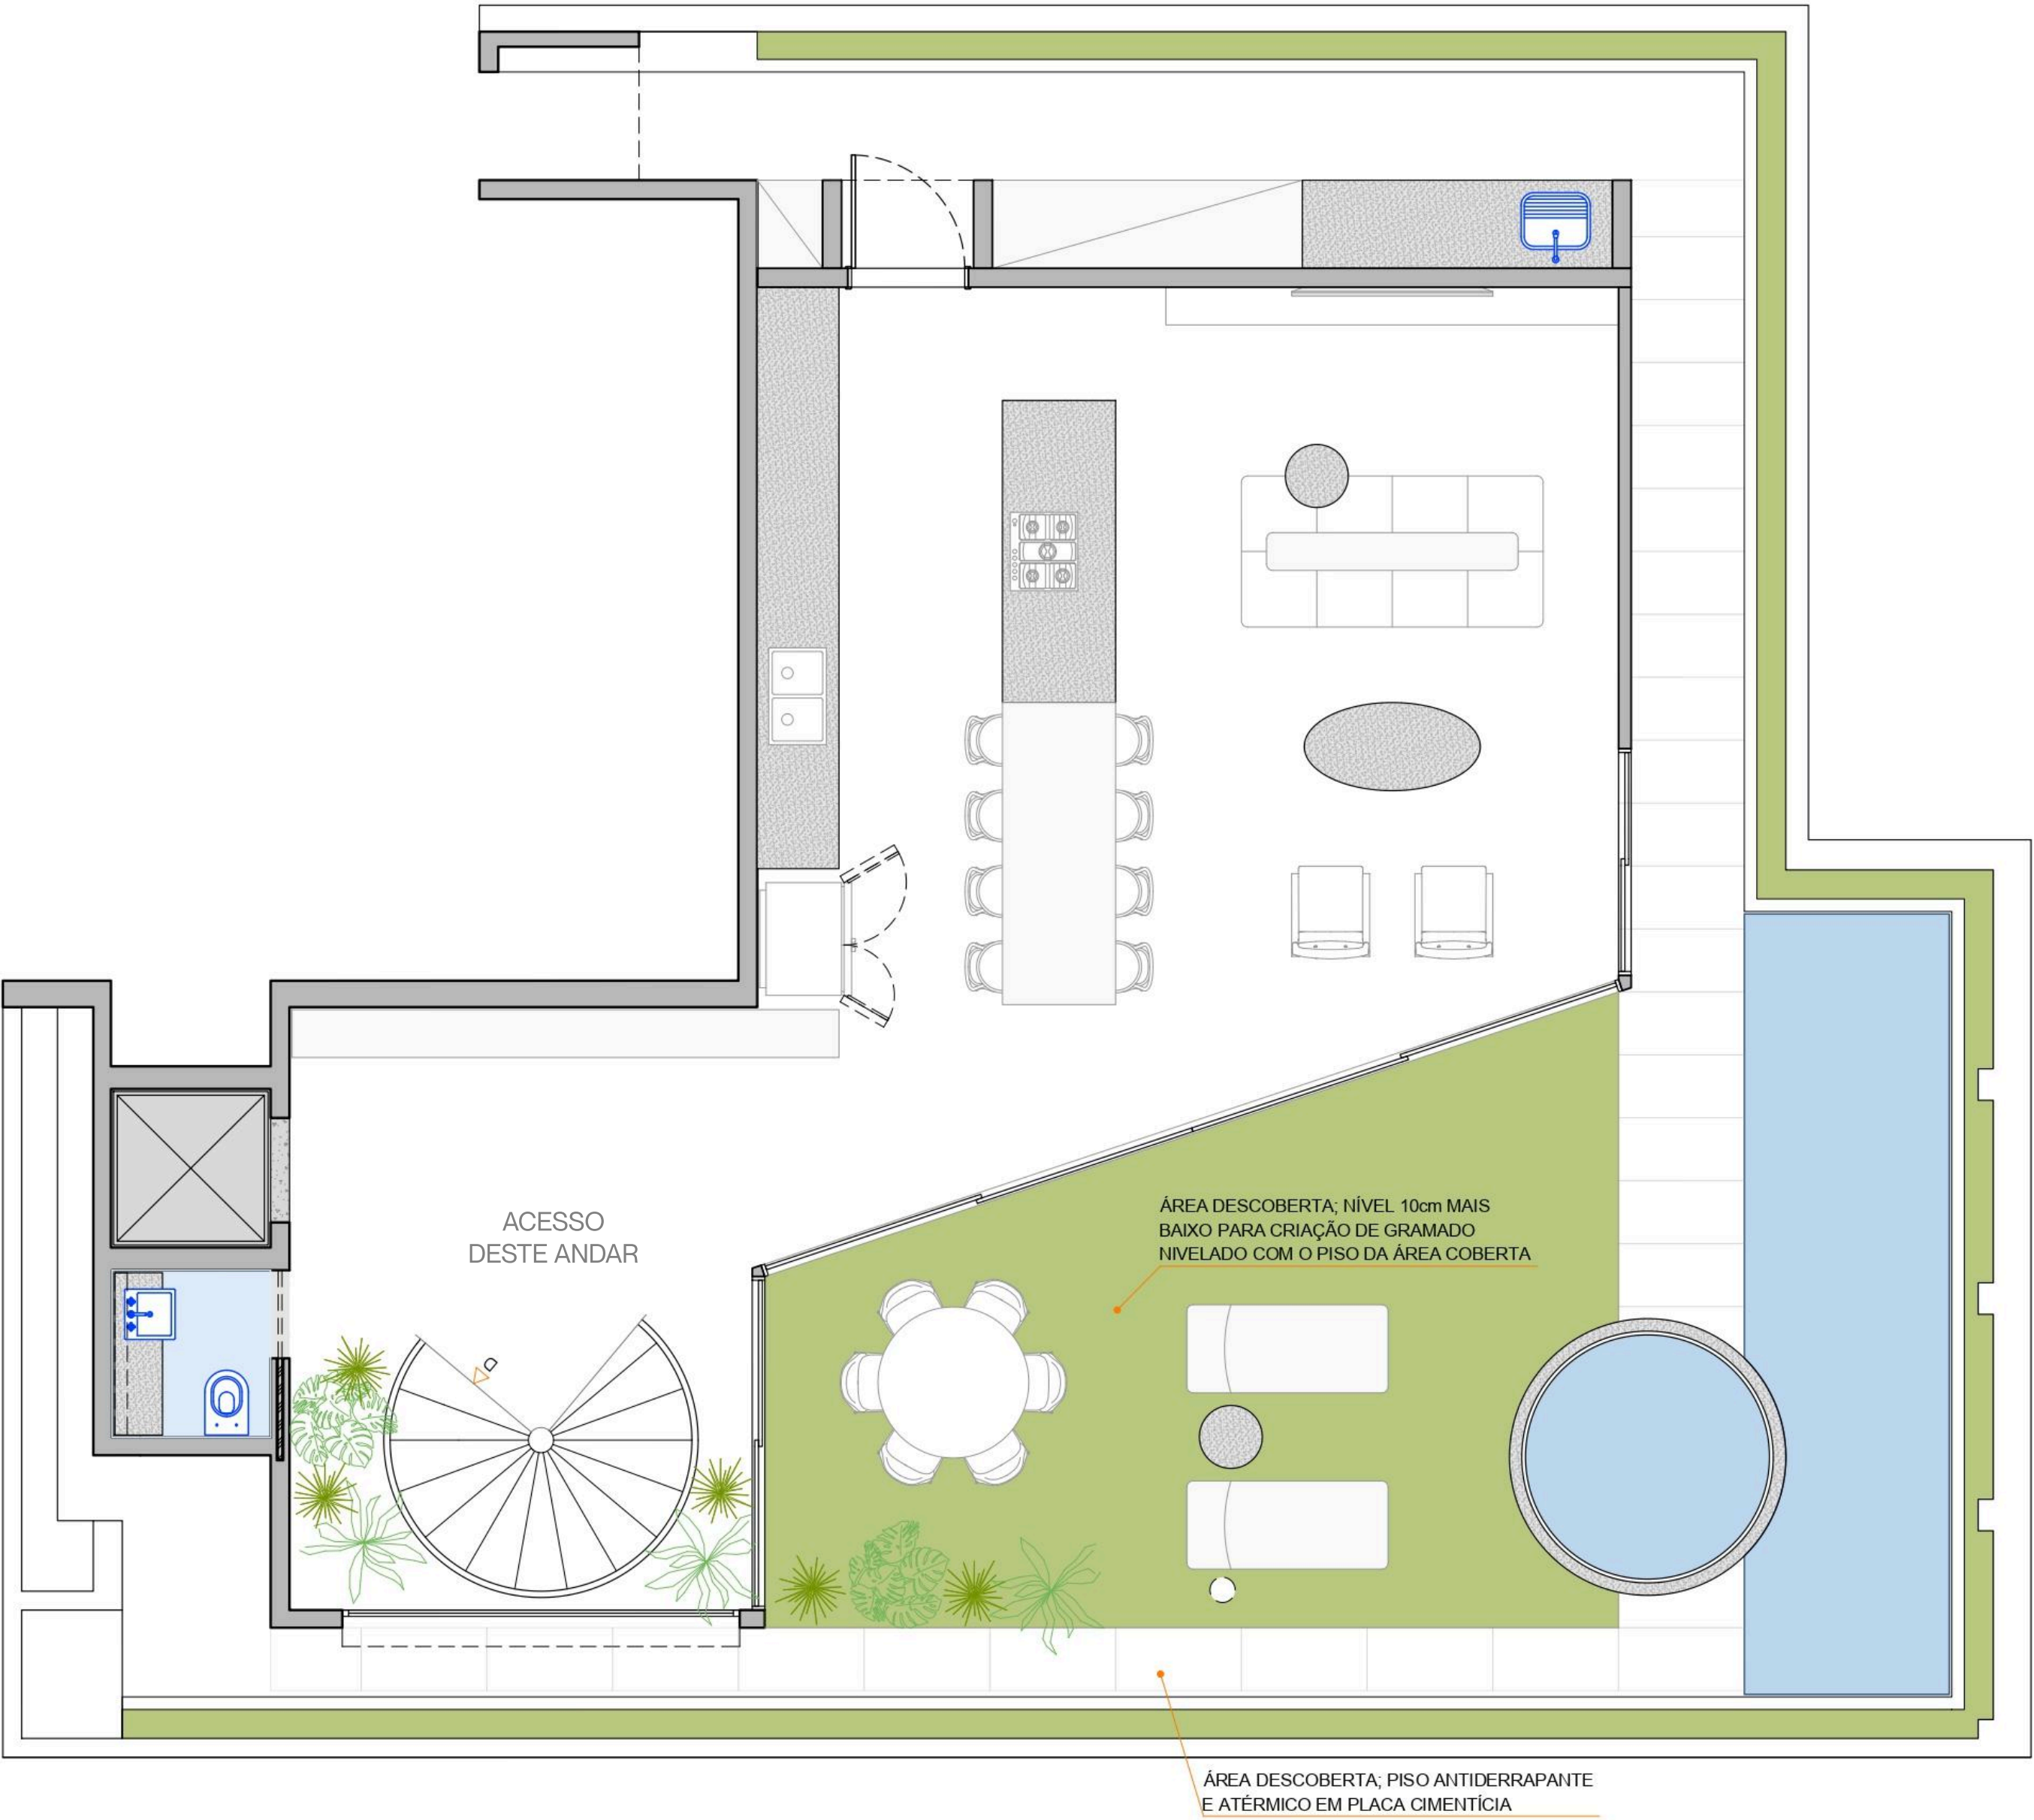

0 1 2m




+




facury.

PLANTA
2º andar

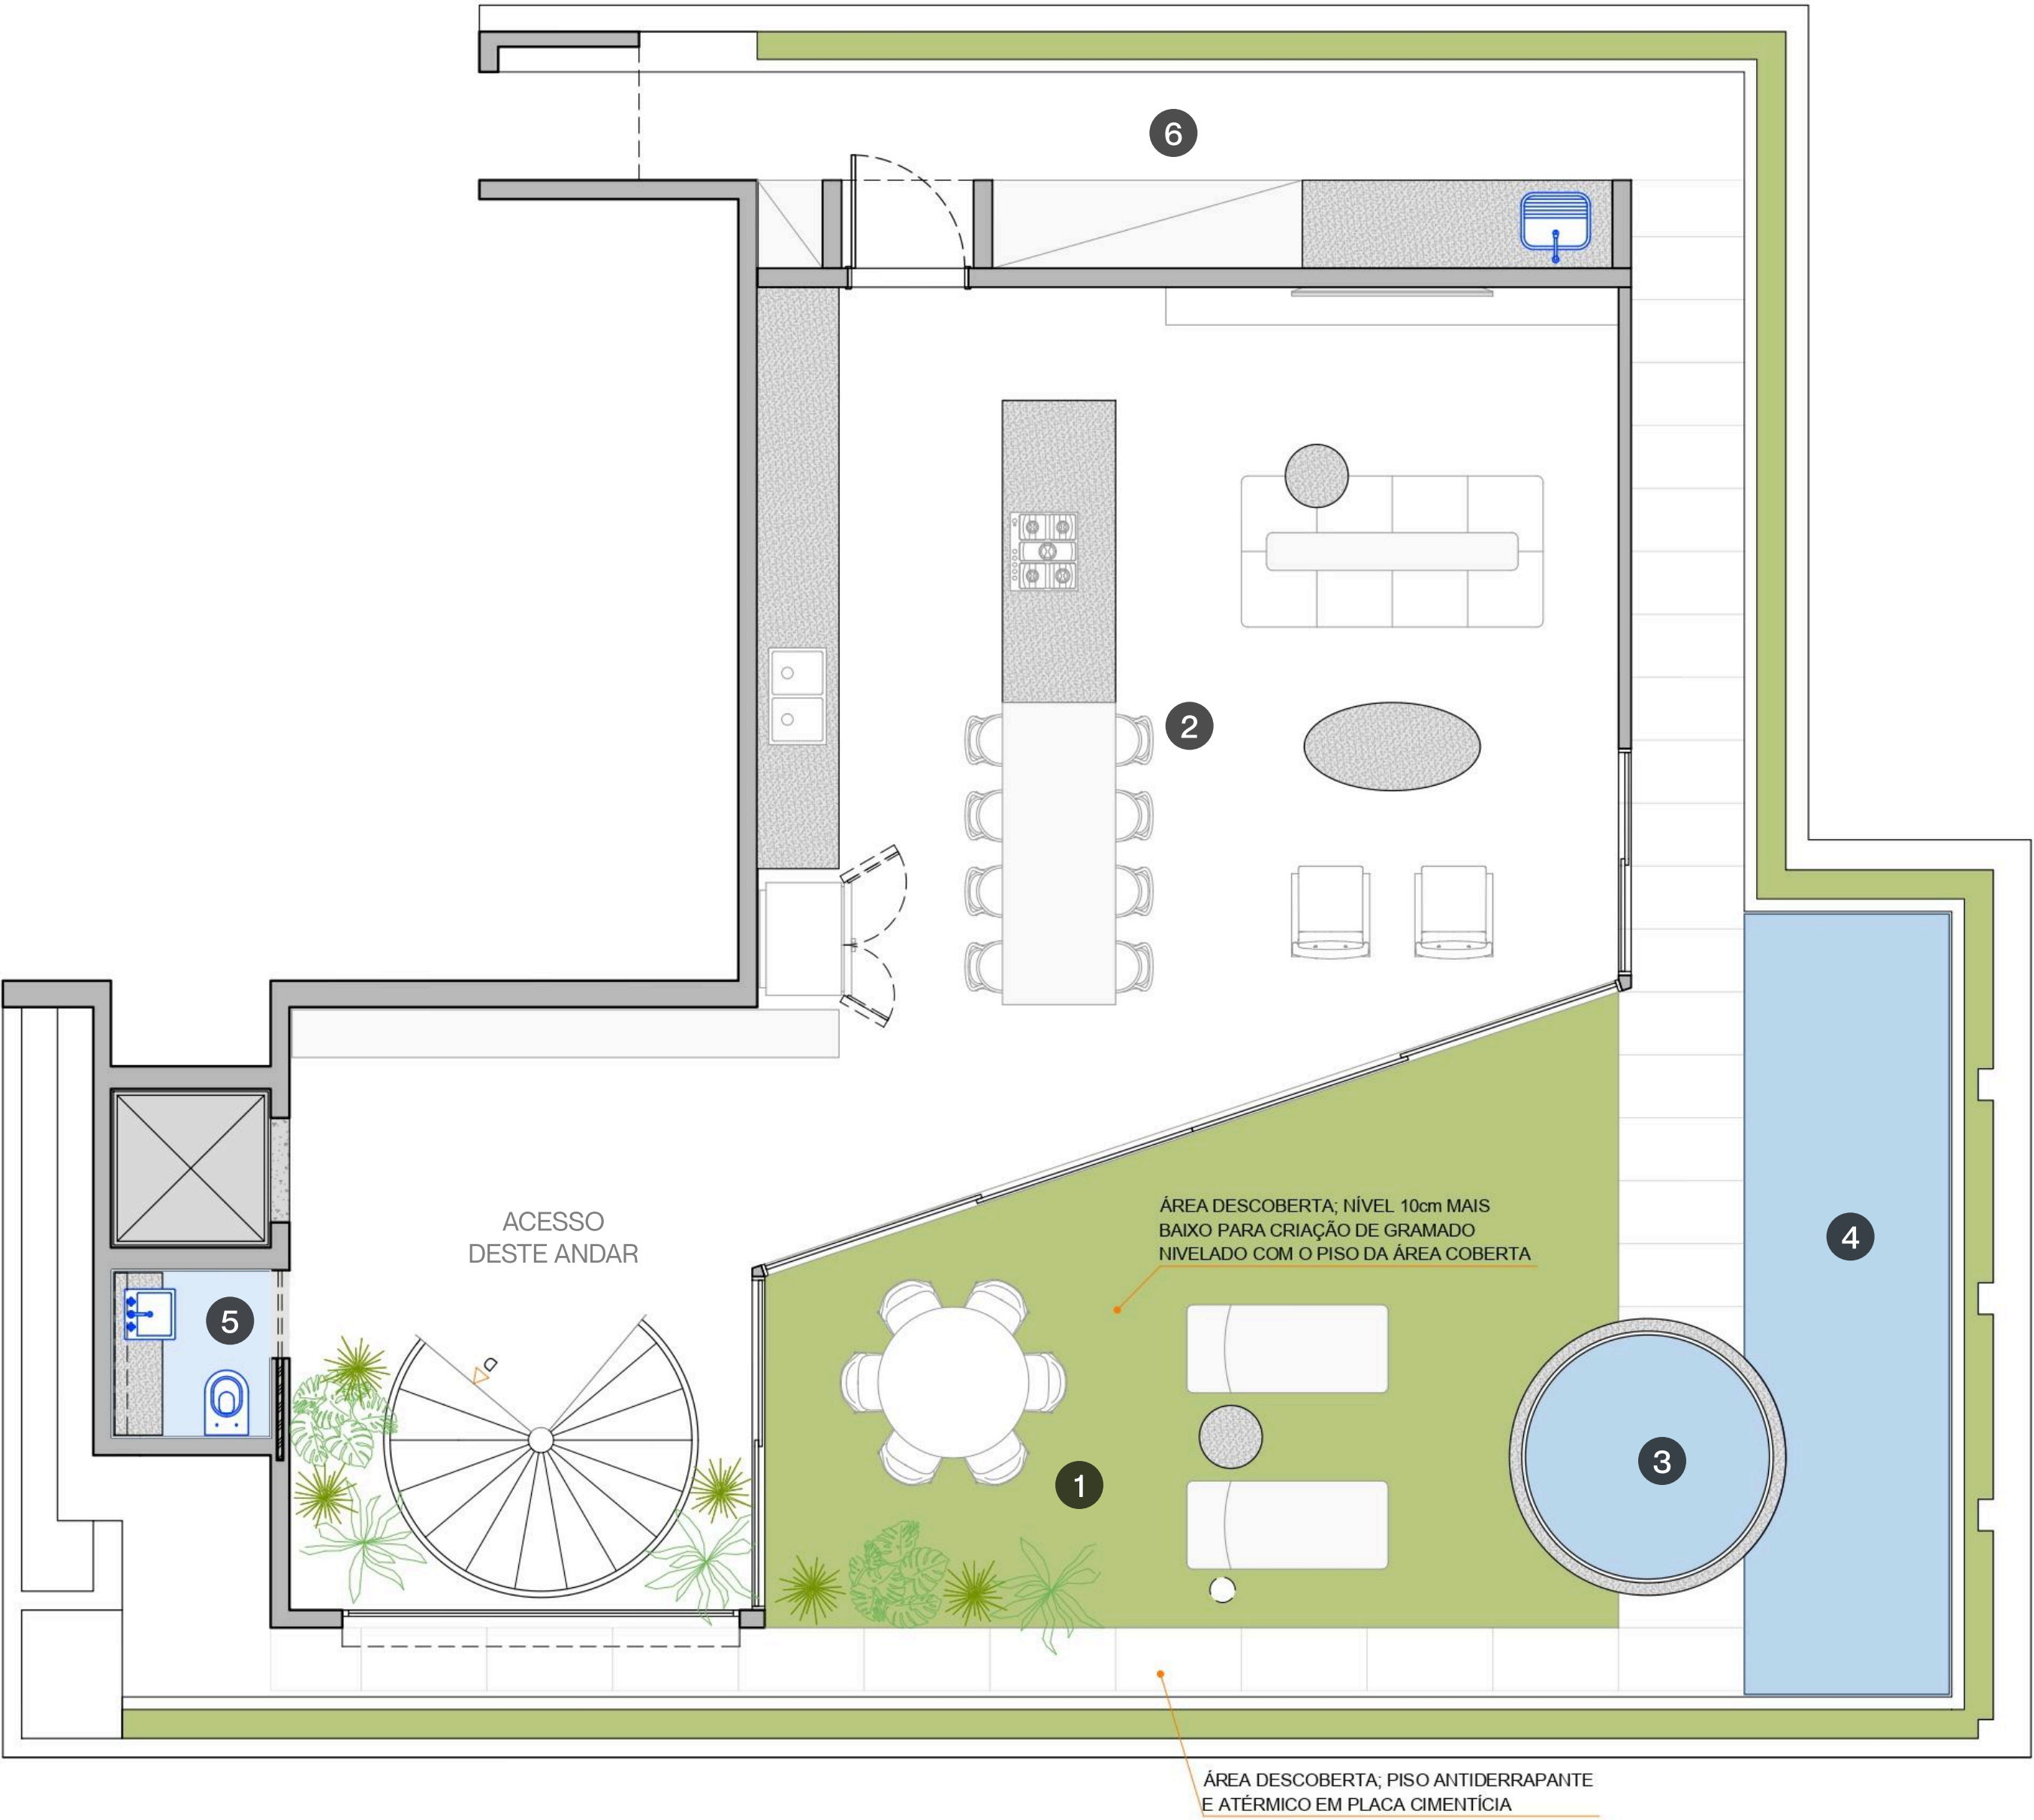


- LEGENDA
- 1 Área descoberta
 - 2 Área Gourmet
 - 3 Ofurô
 - 4 Espelho d'Água
 - 5 Lavabo
 - 6 Serviço

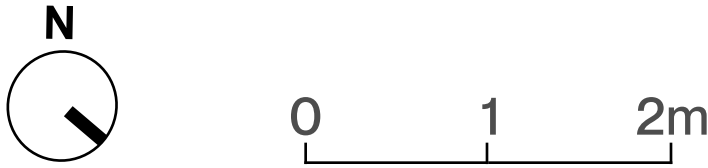

PLANTA

2º andar


- demolição

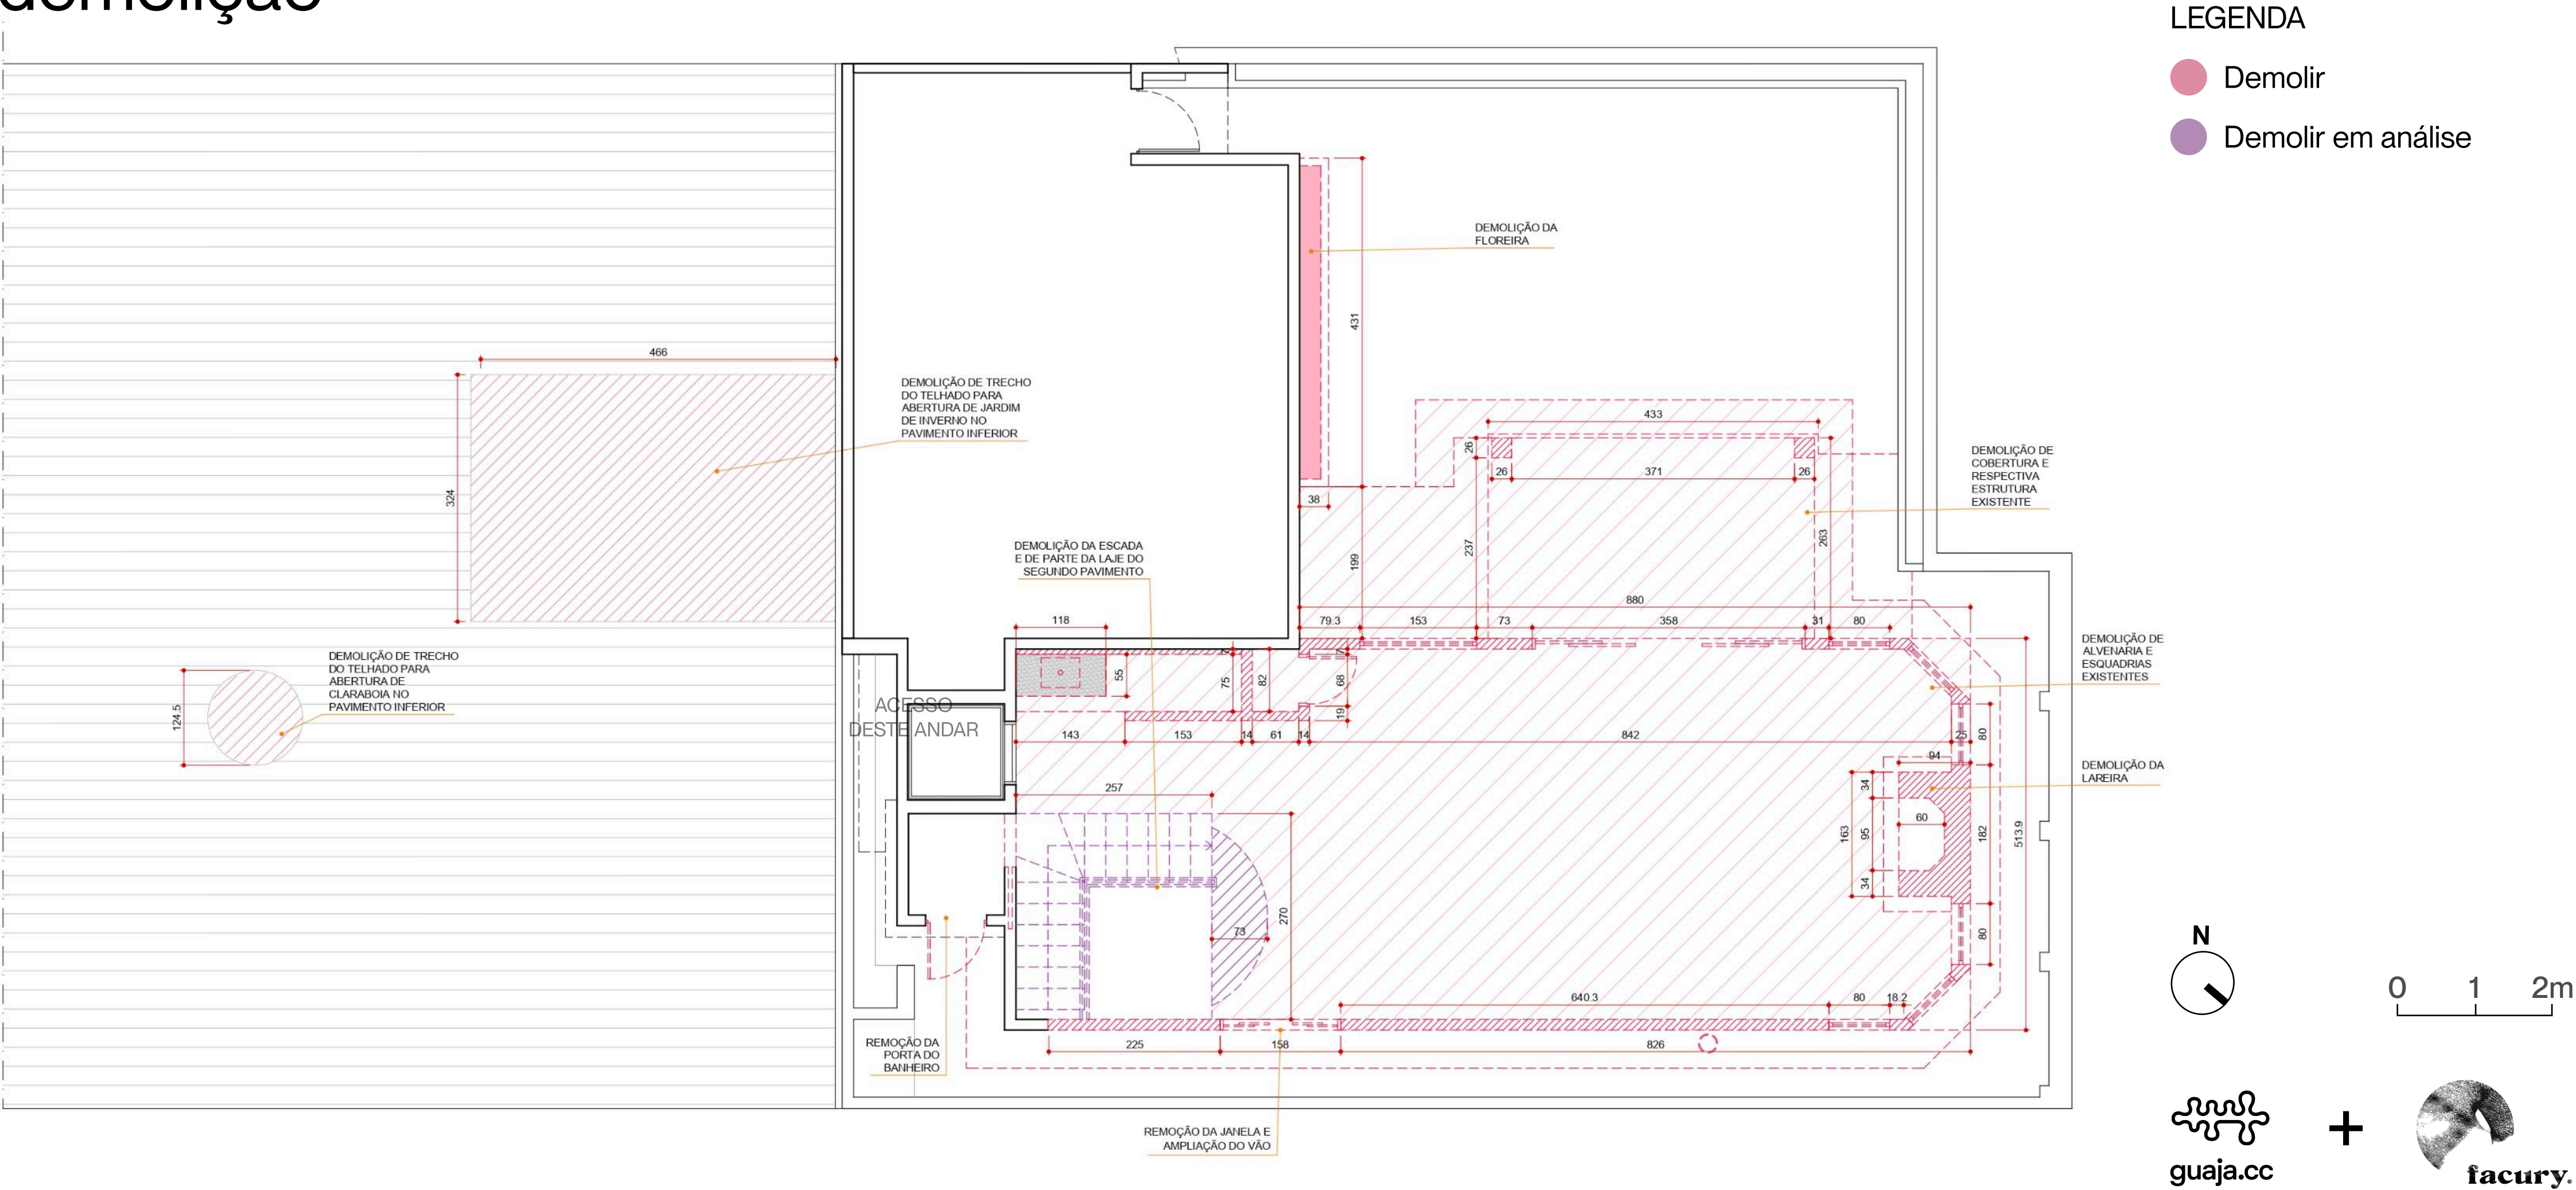

PLANTA

2º andar

- construção

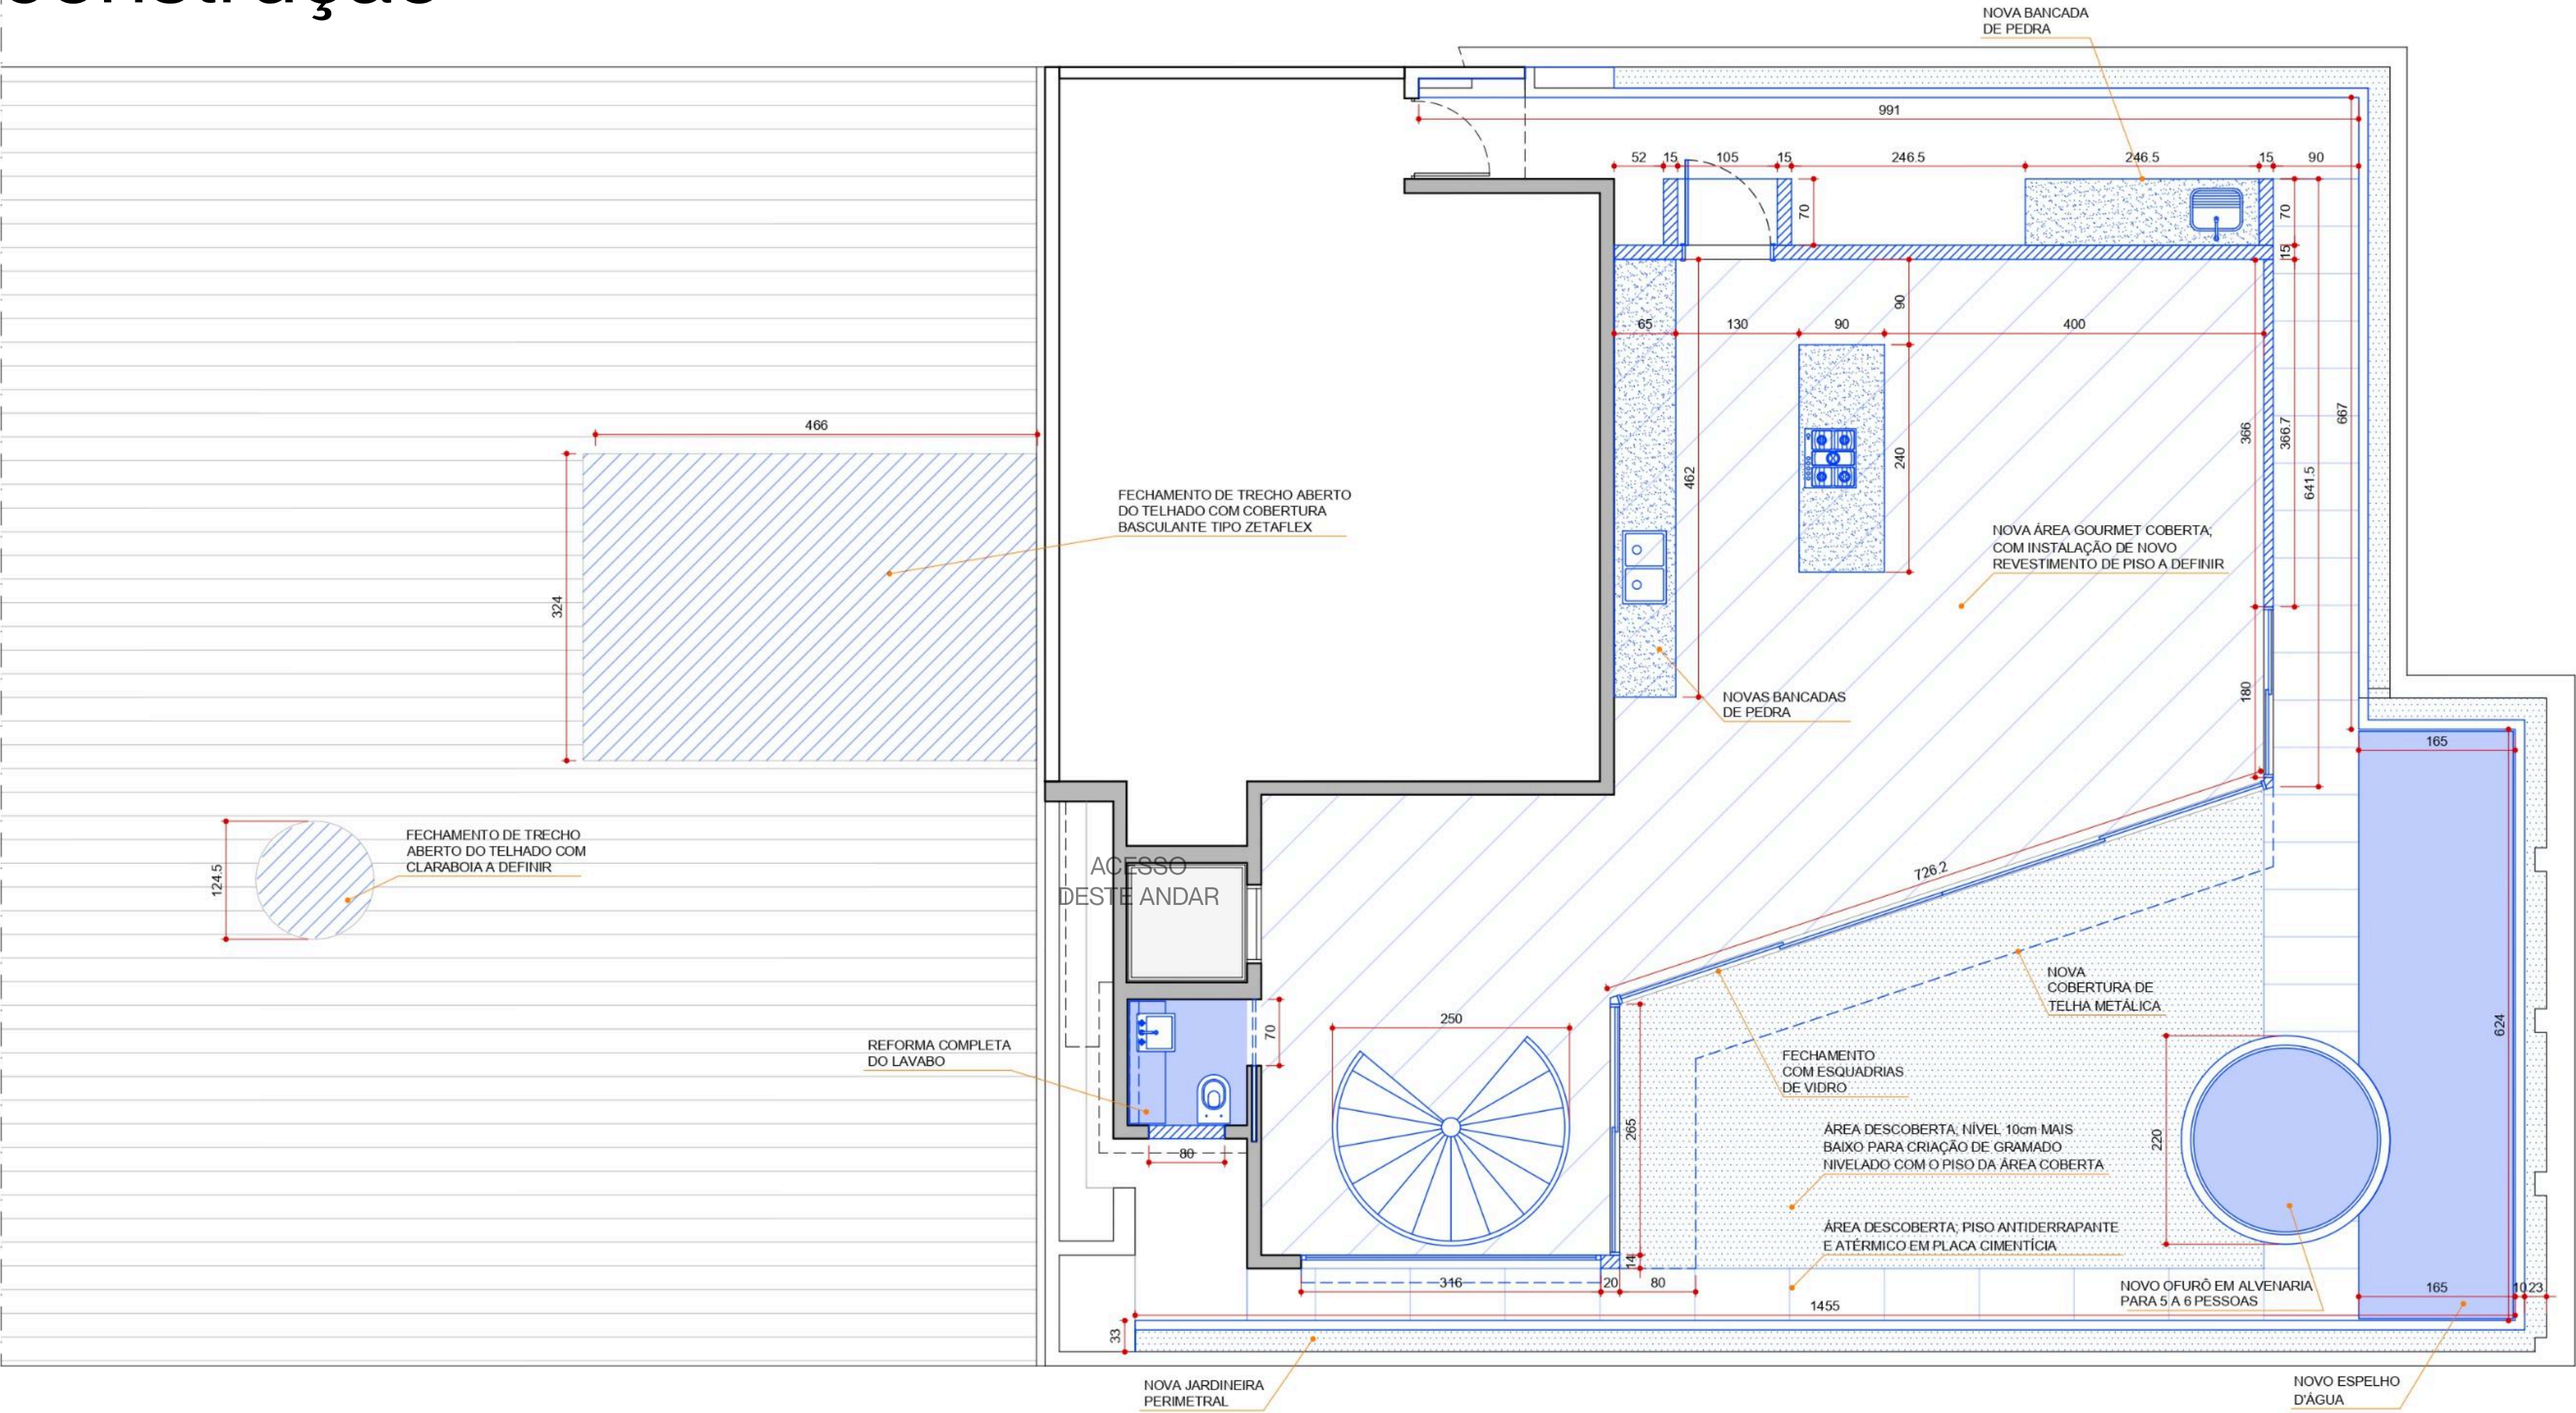

LEGENDA

● Construir

OFURÔ

Dados iniciais

- Altura: 1000 mm
- Diâmetro: 2200 mm
- Material do piso e paredes: porcelanato

ESPELHO D'ÁGUA


Dados iniciais

- Altura: 200 mm
- Material do piso: porcelanato

GRAMA

Dados iniciais

- 100 mm de espessura de terra para a grama

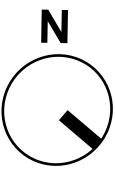


0 1 2m




facury.

PLANTA
2º andar
- materiais

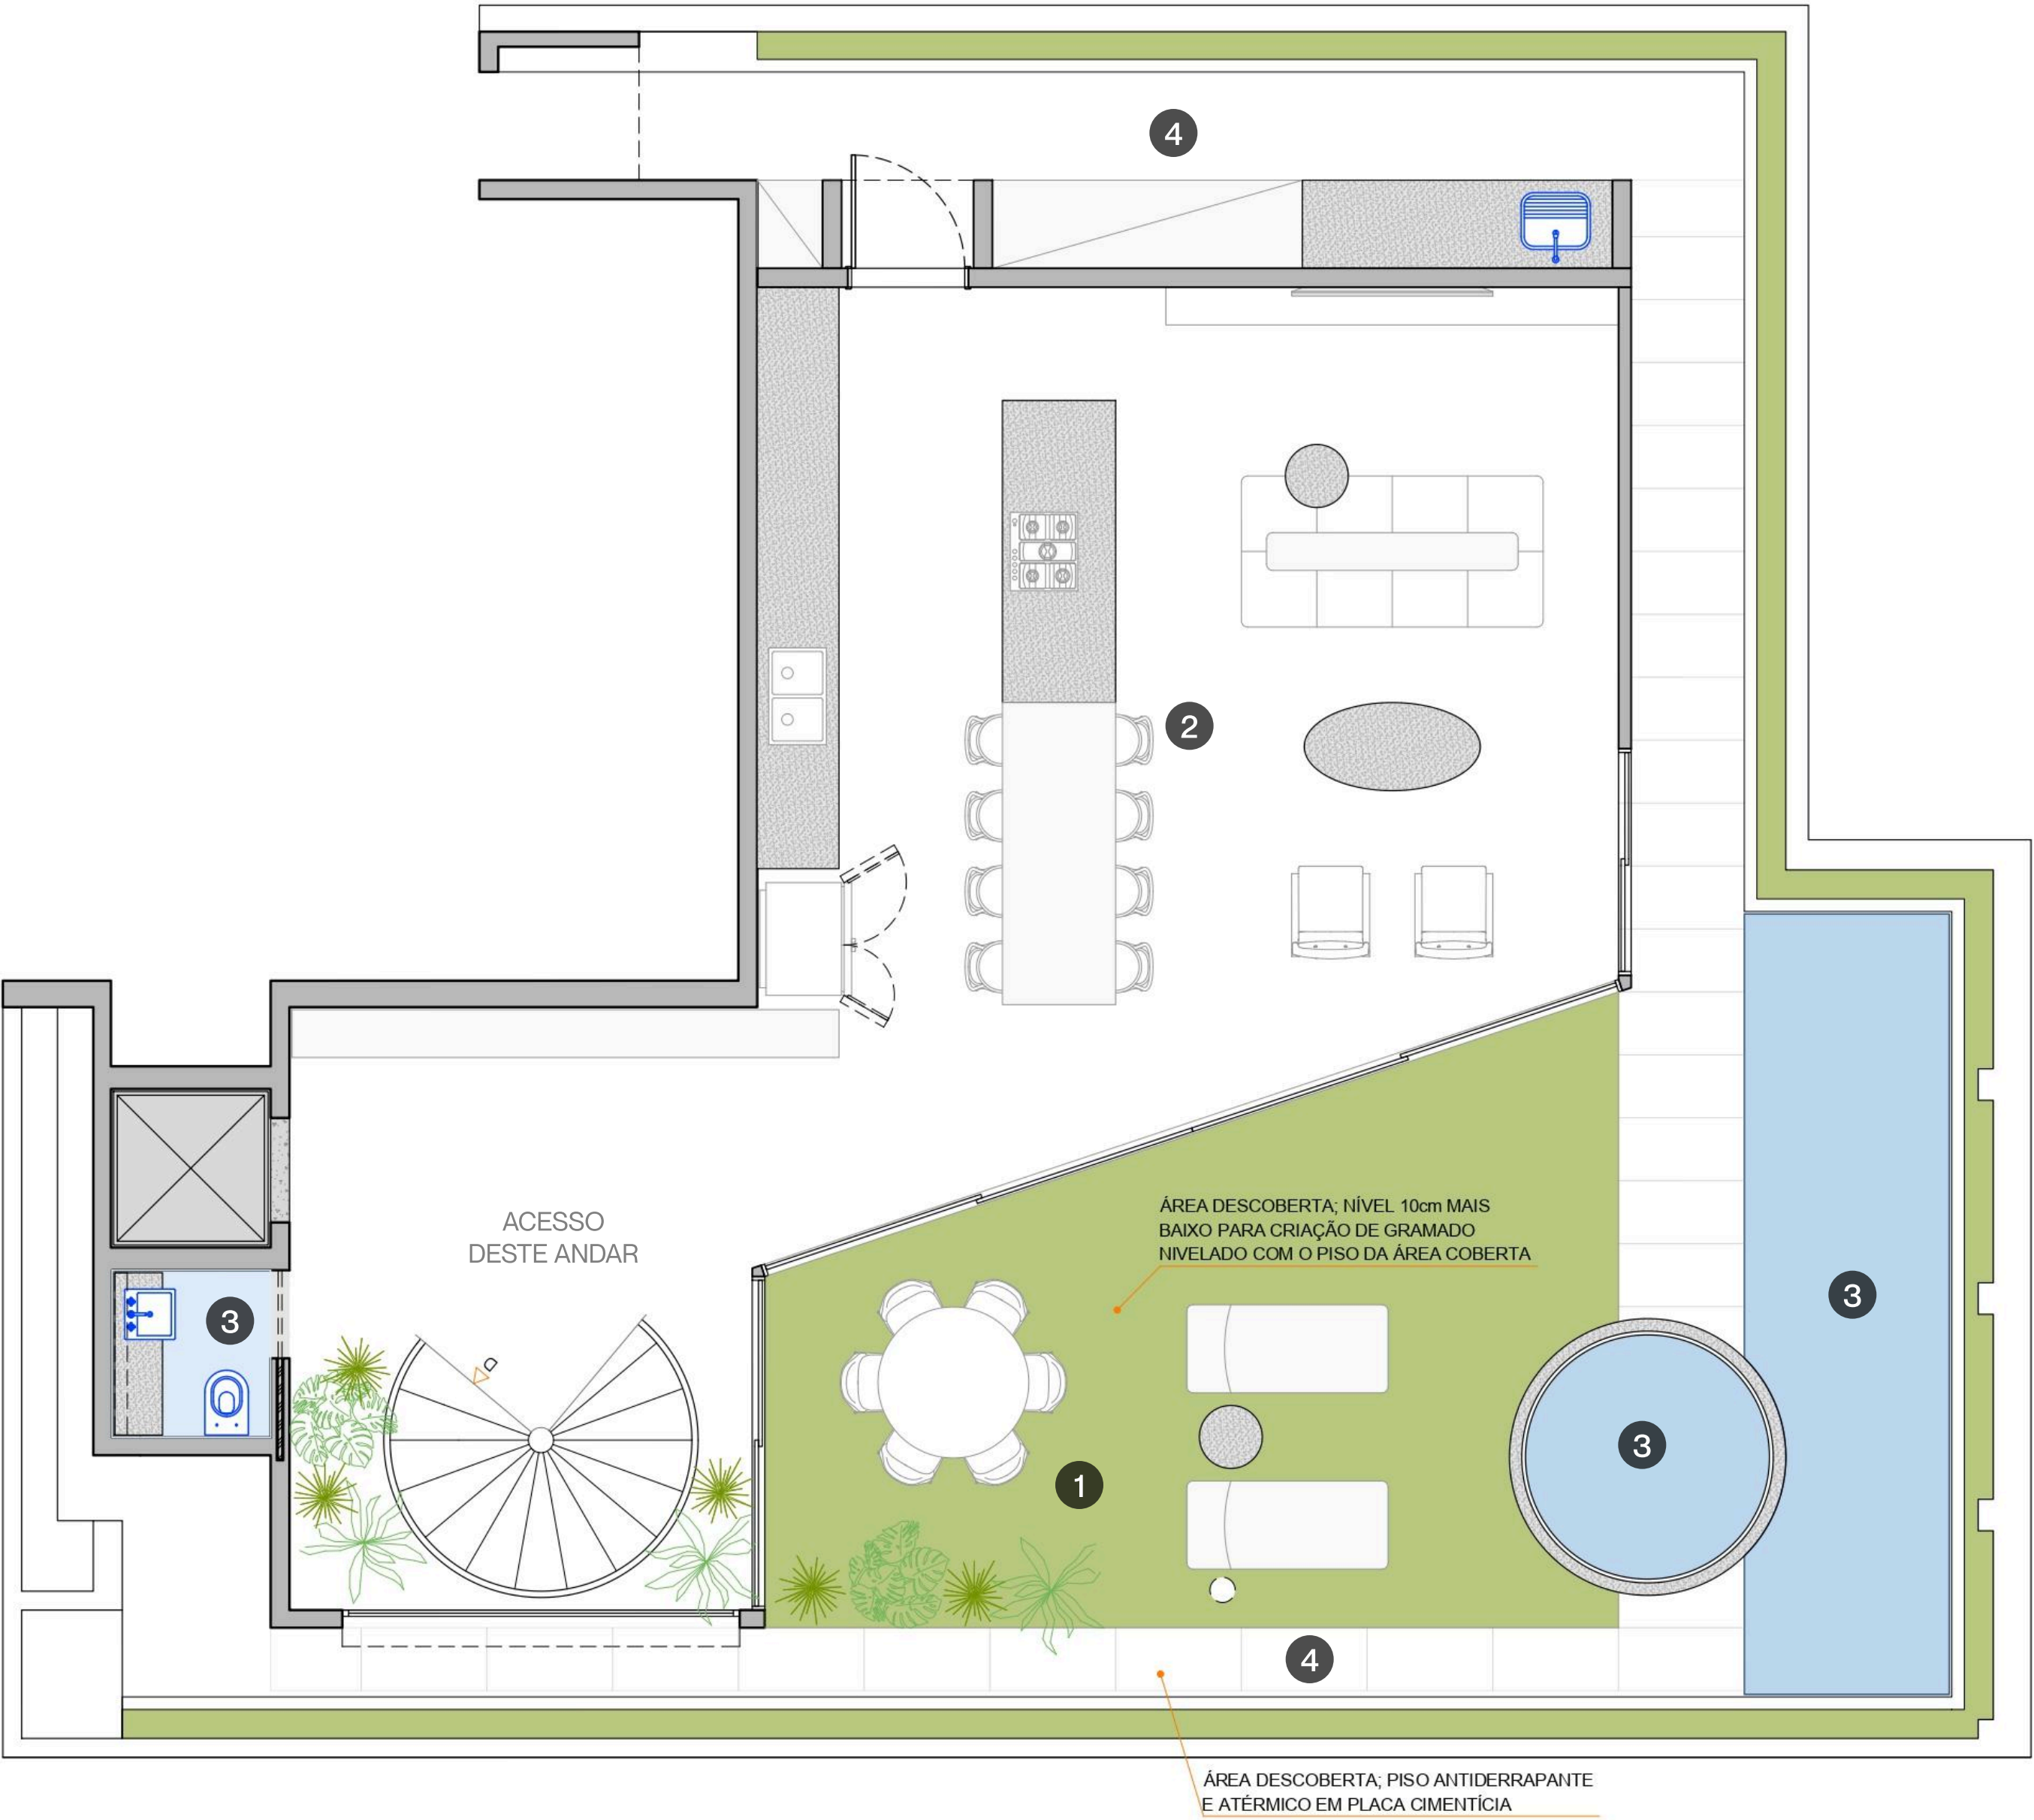

LEGENDA


- 1 Grama
- 2 Microcimento
- 3 Porcelanato
- 4 Placa cimentícia

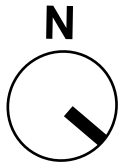


0 1 2m



facury.

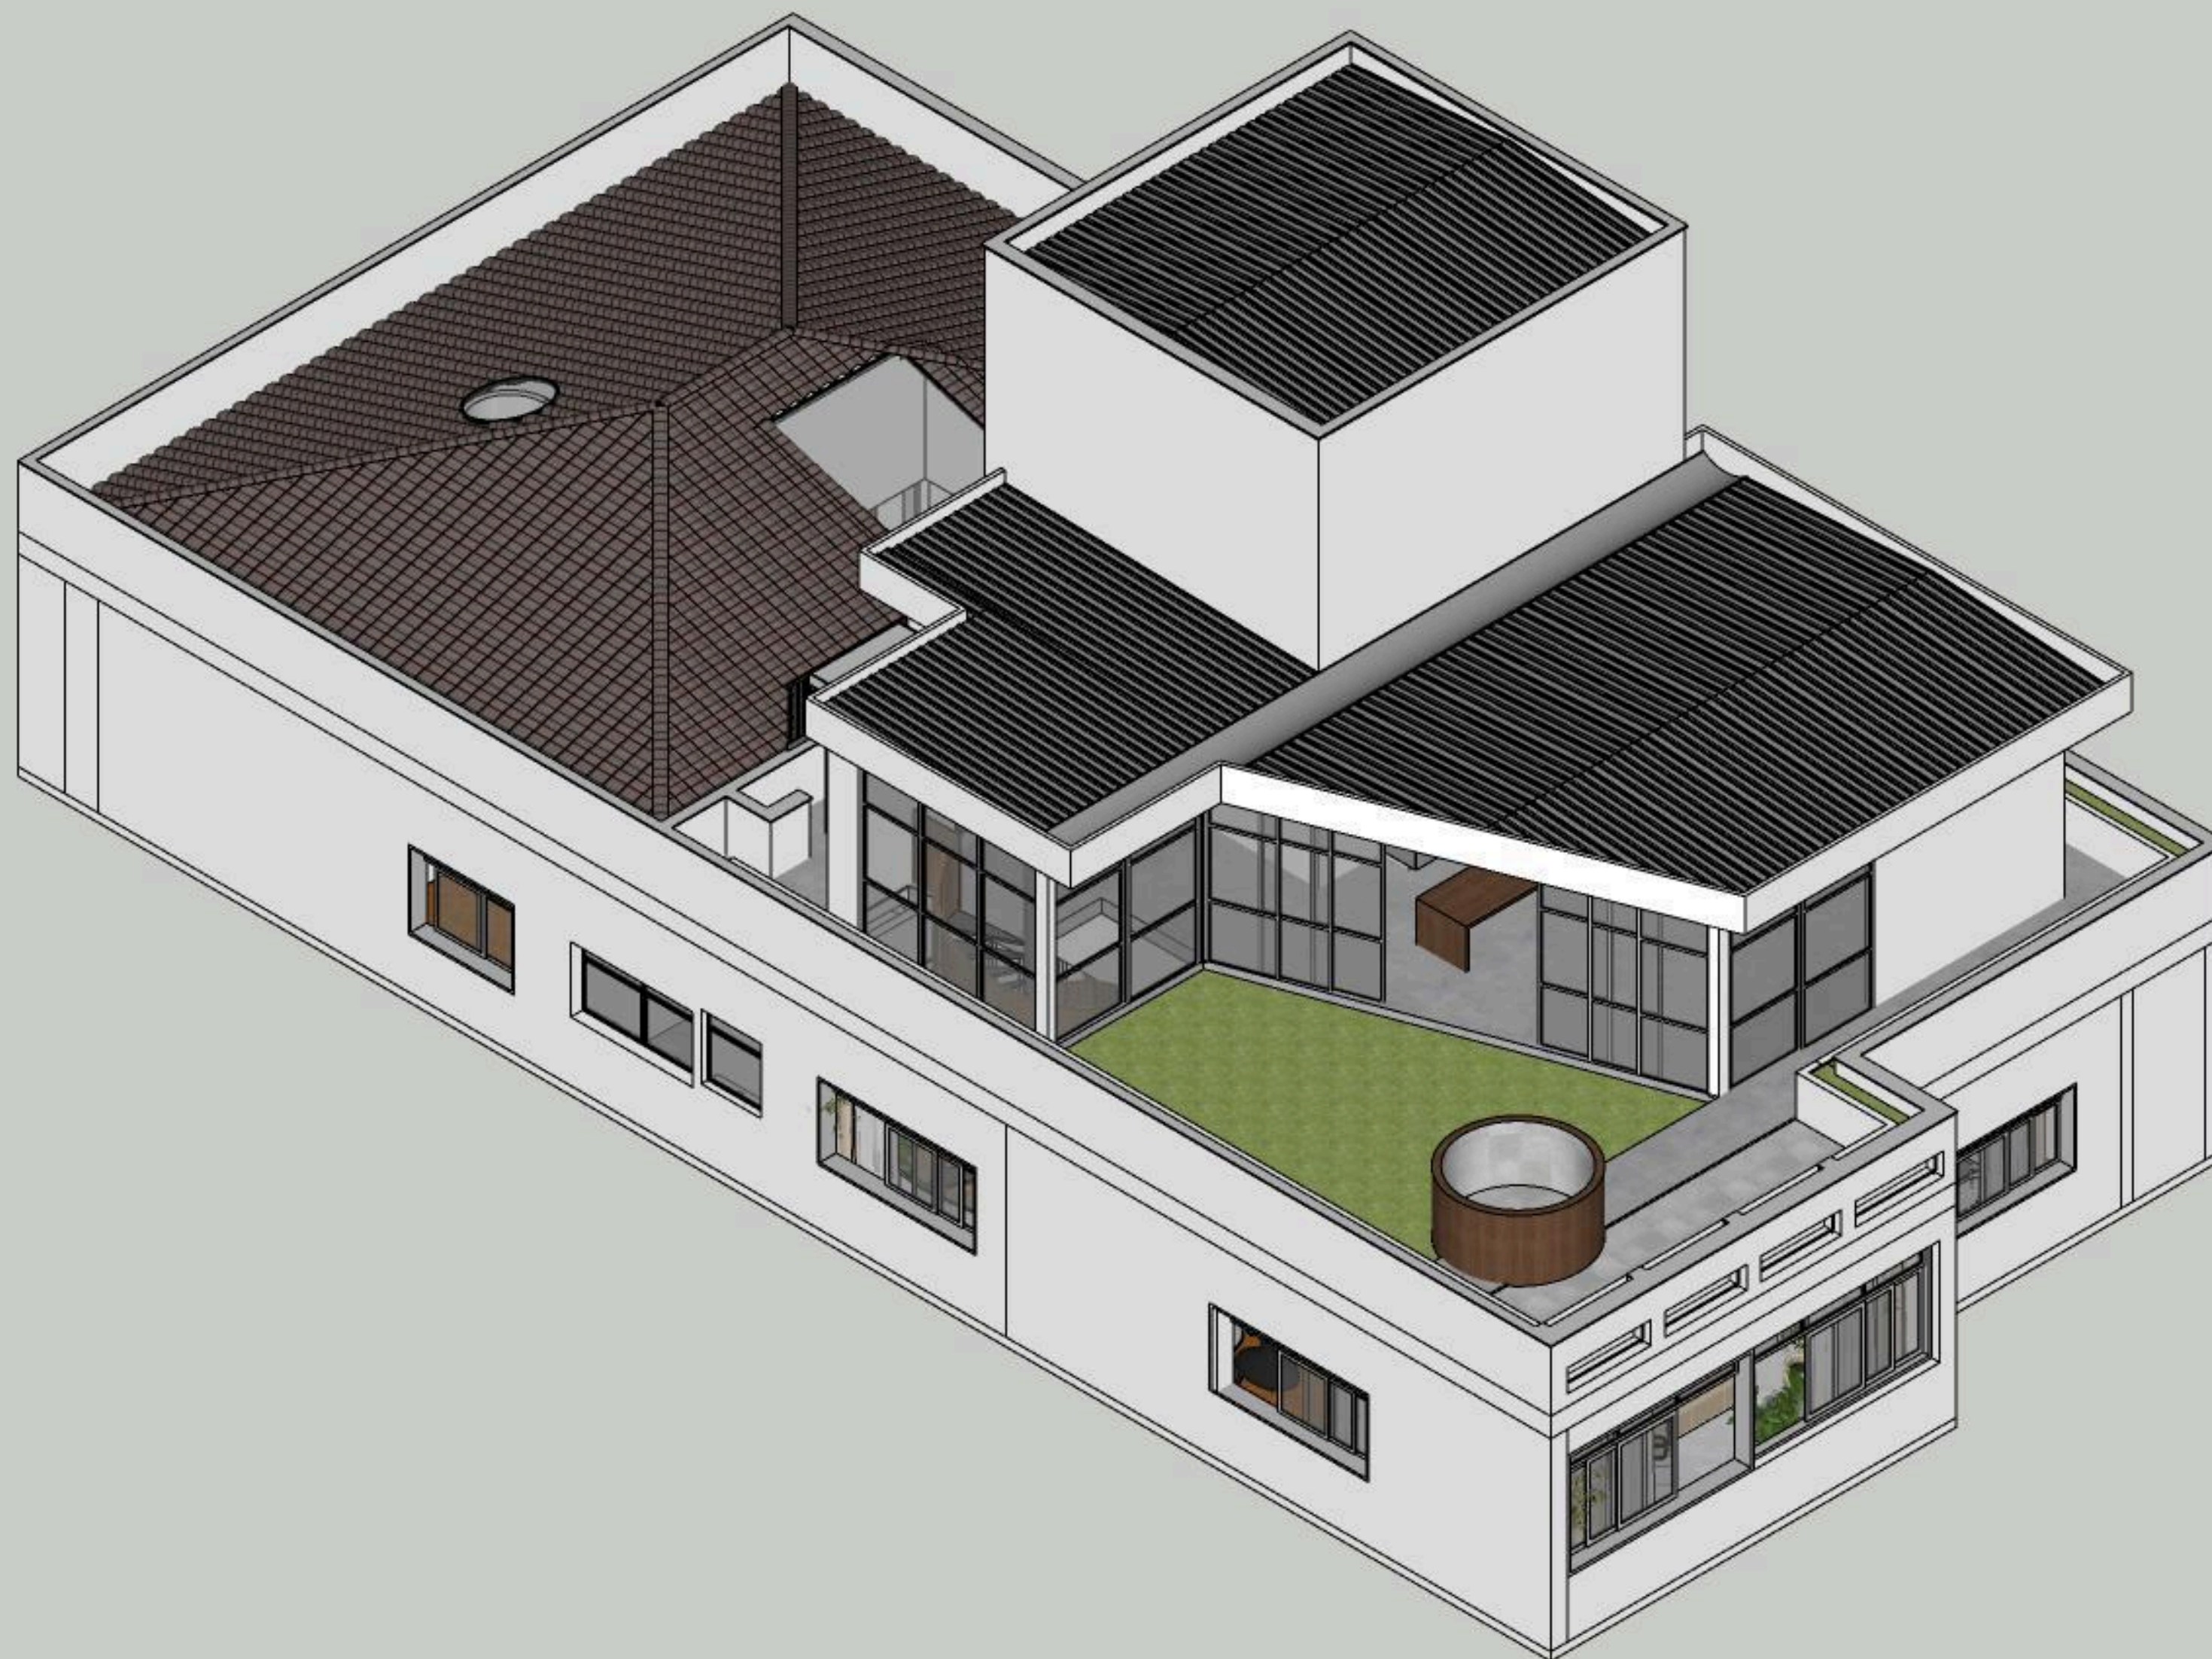

2º PAVIMENTO - VISTA ISOMÉTRICA

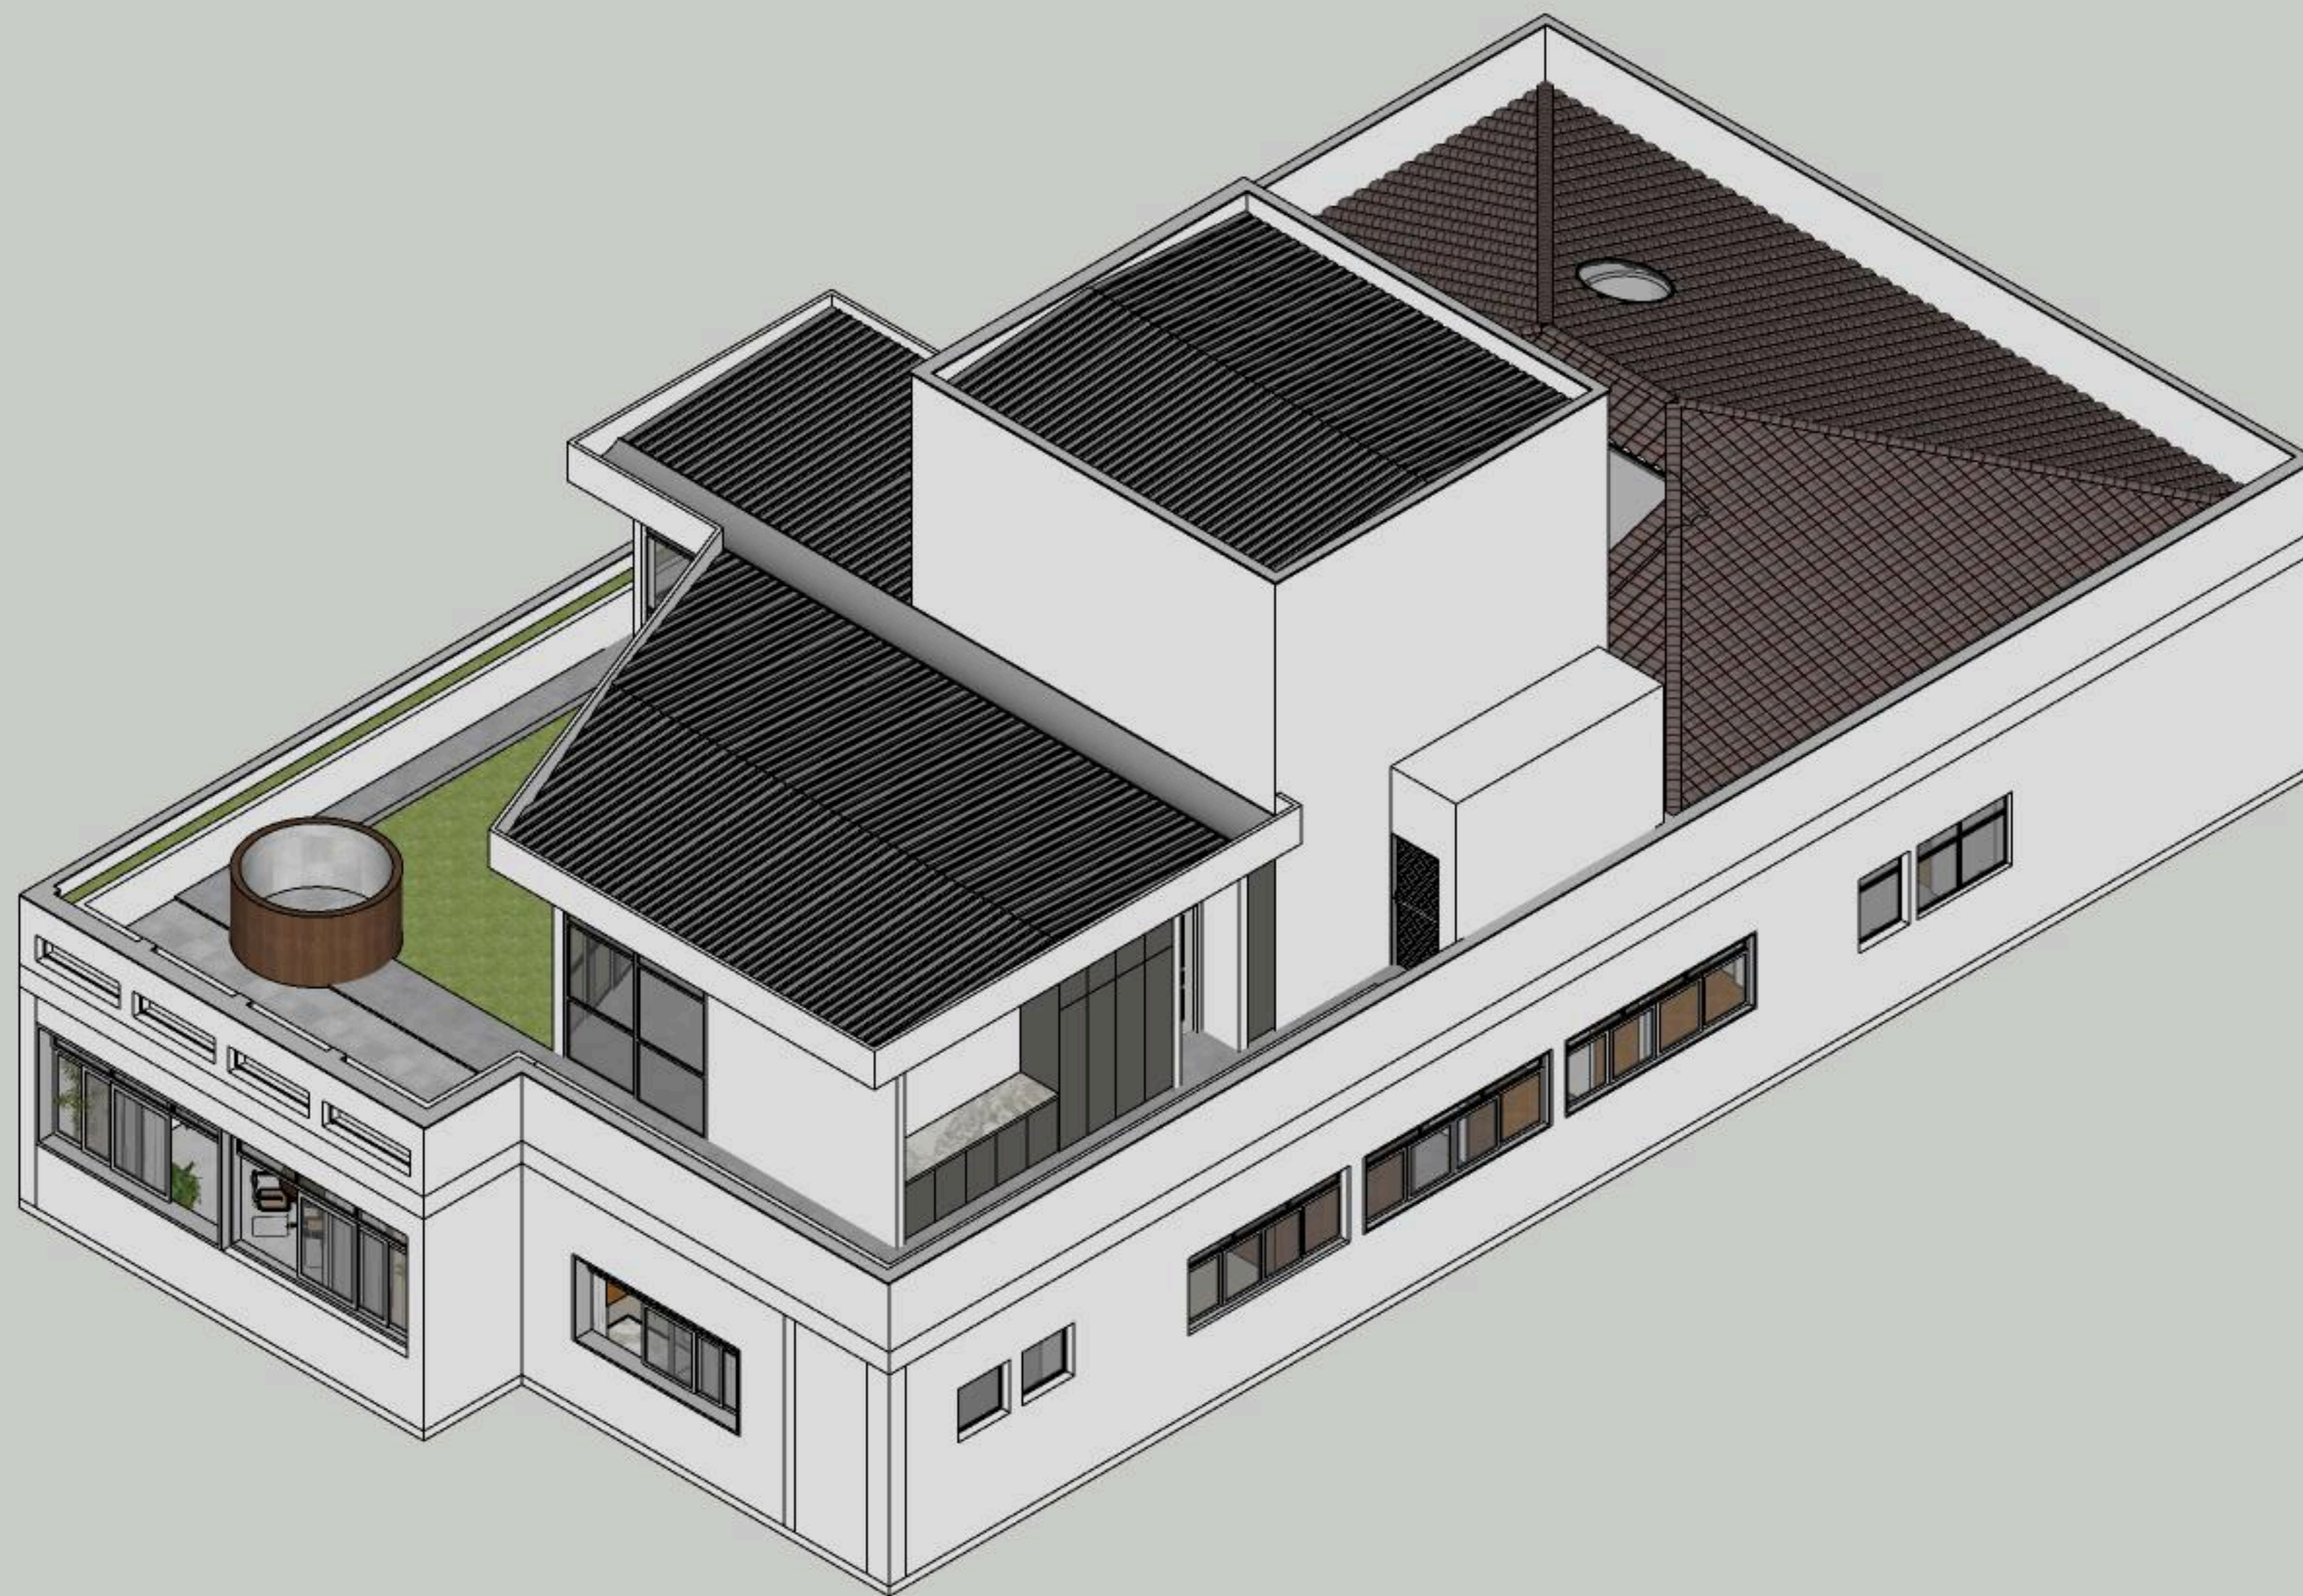

2º PAVIMENTO - VISTA ISOMÉTRICA



1º PAVIMENTO - ESCADA



+





1º PAVIMENTO - ESCADA



+





2º PAVIMENTO - ESCADA



+





2º PAVIMENTO - ÁREA DESCOBERTA




+



OBRIGADO!

Projeto de Arquitetura:

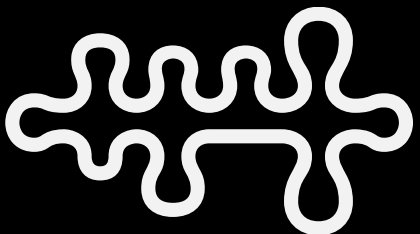

guaja.cc

+



facury.

+



Projeto de Decoração:

Lucas Durães

(31) 9 9784 0246
lucas@guaja.cc
www.guja.com
@guaja.cc

João Pedro Facury

(31) 9 99802 5541
joaopedro@facury.com
www.facury.com
@_facury

Vinicius Fadel

(41) 9 9950-1400
vnimello@gmail.com
@vinicius_fadel

Colaboração:

Diandra Noemi
José Henrique Paiva
Gabrielle Araújo