

PLANTA DE ARQUITETURA

UNLIMITED OCEAN FRONT
FINAL 1



DETALHE VÁLIDO
DO 16° AO 37° PAVIMENTO


LEGENDA

ESCALA: 1 : 75

	ÁREAS COM FORRO / SANCA DE GESSO		PAREDE DRY-WALL
	PILAR DE CONCRETO		PROJEÇÃO DA VIGA
	ALVENARIA		ALÇAPÃO - PREVISÃO PARA MEDIÇÃO INDIVIDUAL DE ÁGUA

PLANTA DE ELÉTRICA

UNLIMITED OCEAN FRONT
FINAL 1

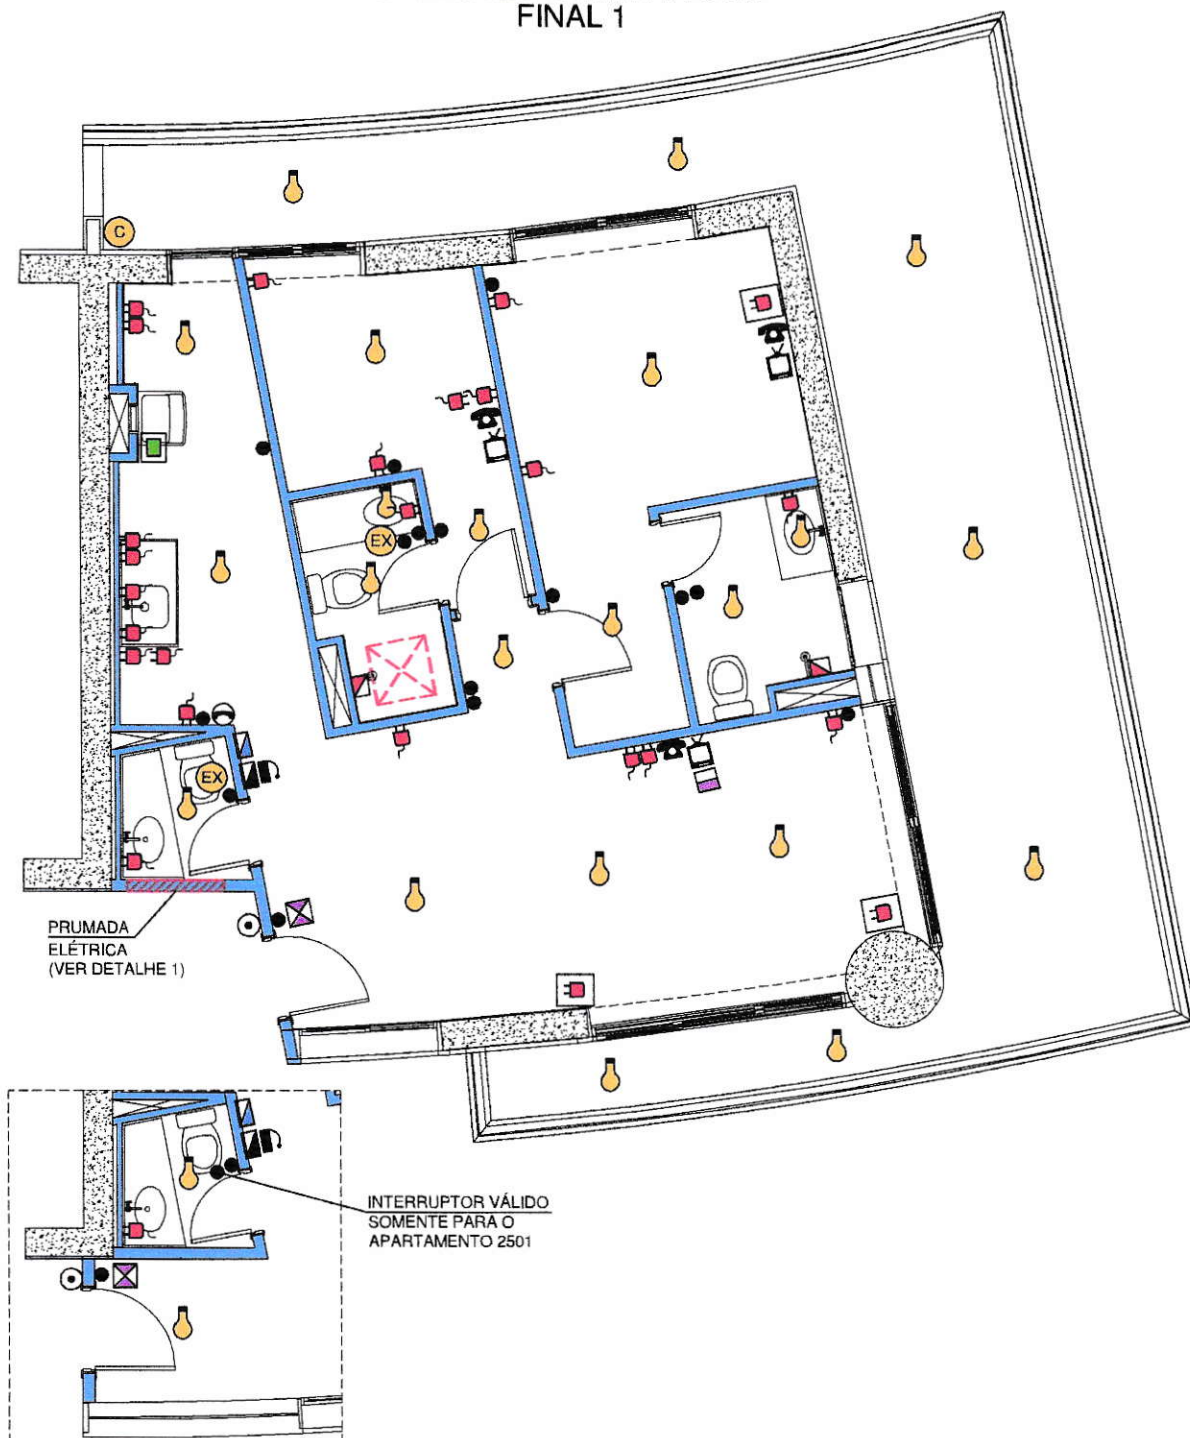

LEGENDA

OBS: NÃO SE DEVE EXECUTAR FUROS NA REGIÃO DO QUADRO DE LUZ E PRUMADA ELÉTRICA

	ILUMINAÇÃO DE TETO		PONTO PARA TV		TOMADA 220V
	INTERRUPTOR DE LUZ		PONTO PARA TELEFONE		TOMADA 220V - NO PISO
	QUADRO DE LUZ		PONTO PARA INTERFONE		PONTO PARA CHUVEIRO ELÉTRICO - 220V
	QUADRO DE SISTEMAS		CAMPAINHA DE PAREDE		PONTO PARA MEDIÇÃO DE GÁS
	PONTO PARA CONDENSADORA (AR CONDICIONADO)		BOTÃO DA CAMPAINHA		PONTO DE EXAUSTOR NO TETO
	PREVISÃO PARA INSTALAÇÃO DE PAINEL DE AUTOMAÇÃO (COMPATÍVEL COM SISTEMA Z-WAVE)		PONTO PARA PREVISÃO DE AUTOMAÇÃO - CAIXA ALTA COM INTERLIGAÇÃO VERTICAL COM O PONTO DA TV		



QUADRO DE LUZ E FORÇA

UNLIMITED OCEAN FRONT
FINAIS 1, 2, 3, 4, 5, 6, 8 e 14

CIRCUITO	DESCRIÇÃO	CORRENTE (A)	POTÊNCIA (KW)	TENSÃO (V)
1	ILUMINAÇÃO E TOMADAS DO DORMITÓRIO 1 E BANHO 1	16	0.50	220
2	ILUMINAÇÃO E TOMADAS SUÍTE 1	16	0.56	220
3	ILUMINAÇÃO SALA, TERRAÇO, COZINHA, ÁREA DE SERVIÇO E VARANDA	16	1.10	220
4	TOMADAS DA COZINHA	20	0.30	220
5	TOMADAS DA ÁREA DE SERVIÇO	20	1.20	220
6	TOMADA DA MÁQUINA DE LAVAR LOUÇA	20	2.00	220
7	PONTO DE FORÇA DO CHUVEIRO	32	4.40	220
8	PONTO DE FORÇA DO CHUVEIRO	32	4.40	220
9	PONTO DE FORÇA DO AR CONDICIONADO	20	2.00	220

DETALHE DA PRUMADA ELÉTRICA

UNLIMITED OCEAN FRONT
DETALHE 1

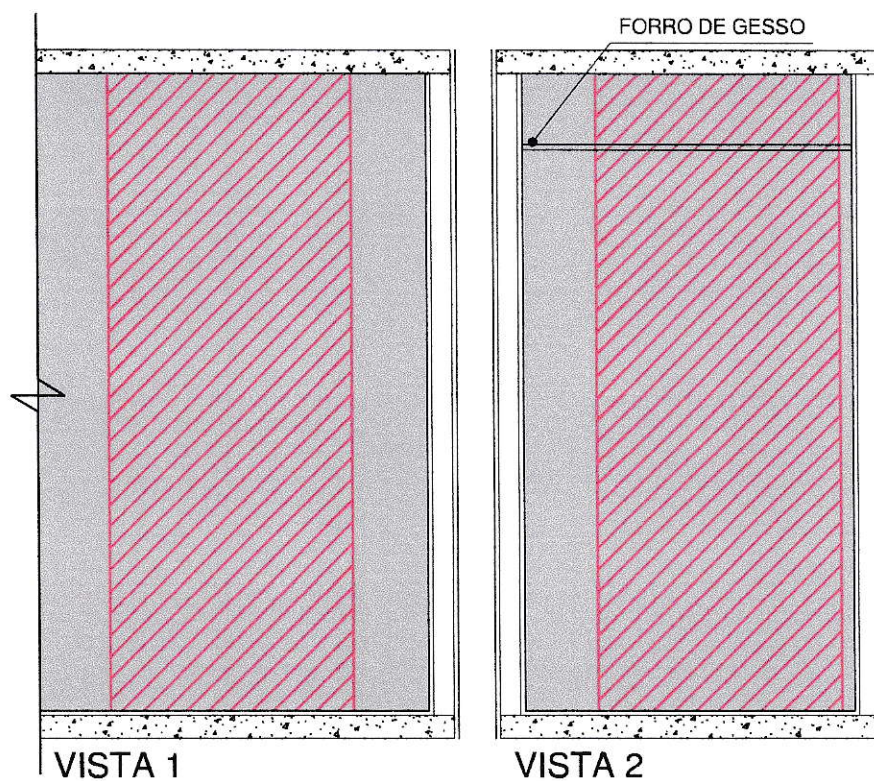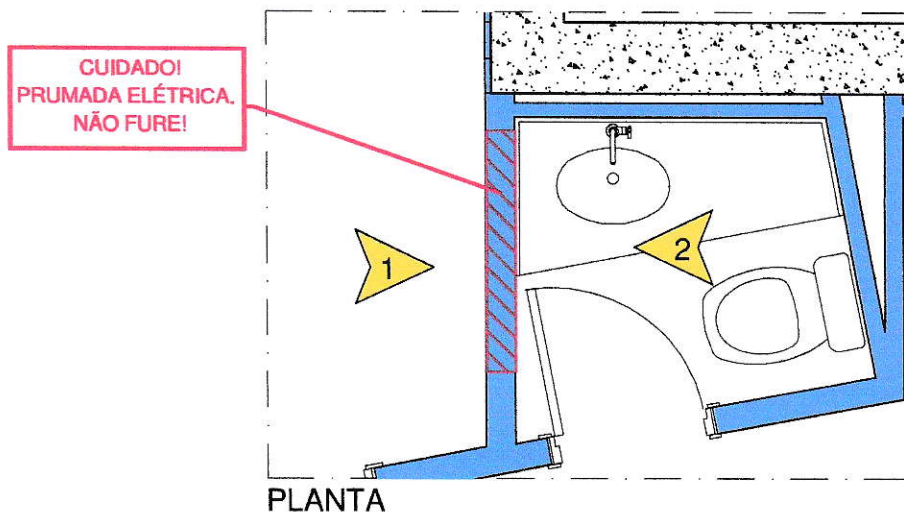


LEGENDA

 PRUMADA ELÉTRICA - NÃO FURAR

PLANTA DE AR CONDICIONADO E PRUMADAS

UNLIMITED OCEAN FRONT
FINAL 1

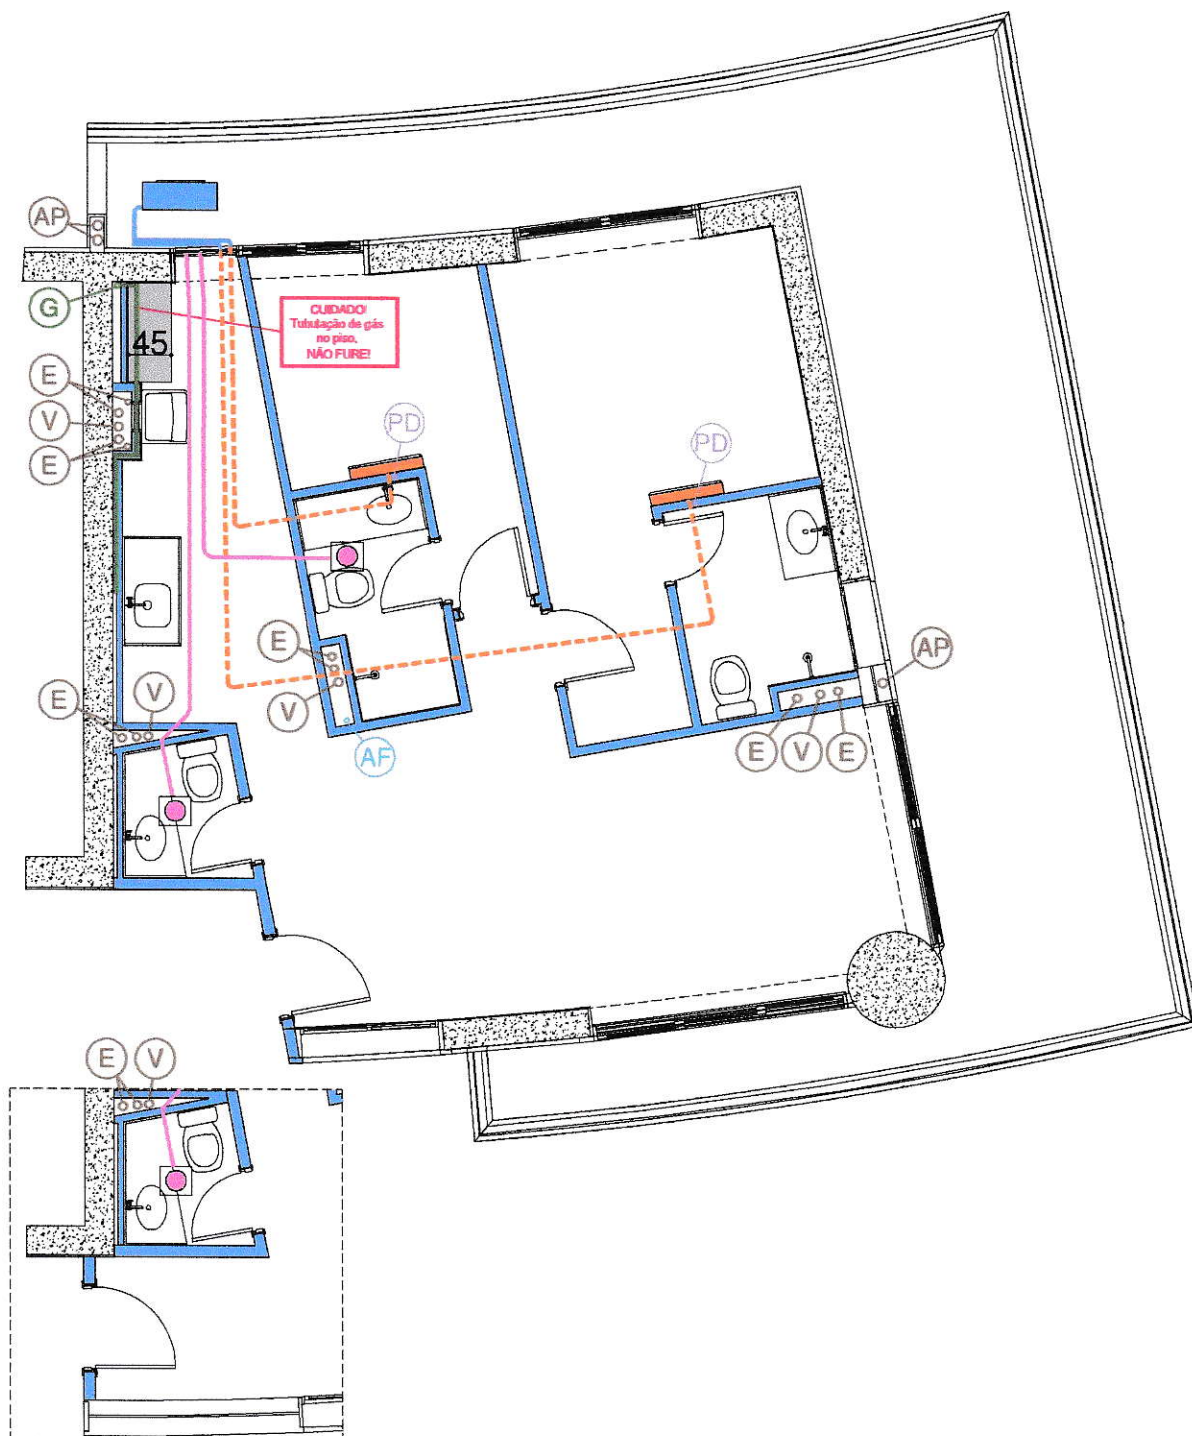

LEGENDA

PRUMADAS

(V)	VENTILAÇÃO
(E)	ESGOTO
(AP)	ÁGUA PLUVIAL
(AF)	ÁGUA FRIA
(G)	GÁS

PONTOS

(PD)	DRENO
------	-------

	TUBULAÇÃO DE GÁS
	TUBULAÇÃO FRIGORÍGENA
	PREVISÃO PARA TUBULAÇÃO FRIGORÍGENA
	LOCAL PREVISTO P/ INSTALAÇÃO DA CONDENSADORA
	LOCAL PREVISTO P/ INSTALAÇÃO DA EVAPORADORA DE AR CONDICIONADO DE PAREDE
	TUBULAÇÃO DO EXAUSTOR NO TETO
	PONTO DO EXAUSTOR

OBS.: NÃO EXECUTAR FUROS NA REGIÃO DAS PRUMADAS!


LEMBRE-SE DE QUE OS ENCANAMENTOS QUE PASSAM POR UMA PAREDE HIDRÁULICA, MOSTRADA NOS BANHEIROS, COZINHA ETC., TAMBÉM ESTÃO PASSANDO POR ESTA MESMA PAREDE NA ÁREA SECA VIZINHA. NAS COLOCAÇÕES DOS ARMÁRIOS, TOMAR TODOS OS CUIDADOS POSSÍVEIS.

ATENÇÃO: USAR LIMITADOR DE BROCA E NÃO ULTRAPASSAR 2 CM DE PROFUNDIDADE!

NÃO FURAR NAS ÁREAS INDICADAS NA COR CINZA

PLANTA DE AR CONDICIONADO E PRUMADAS

UNLIMITED OCEAN FRONT
FINAL 1

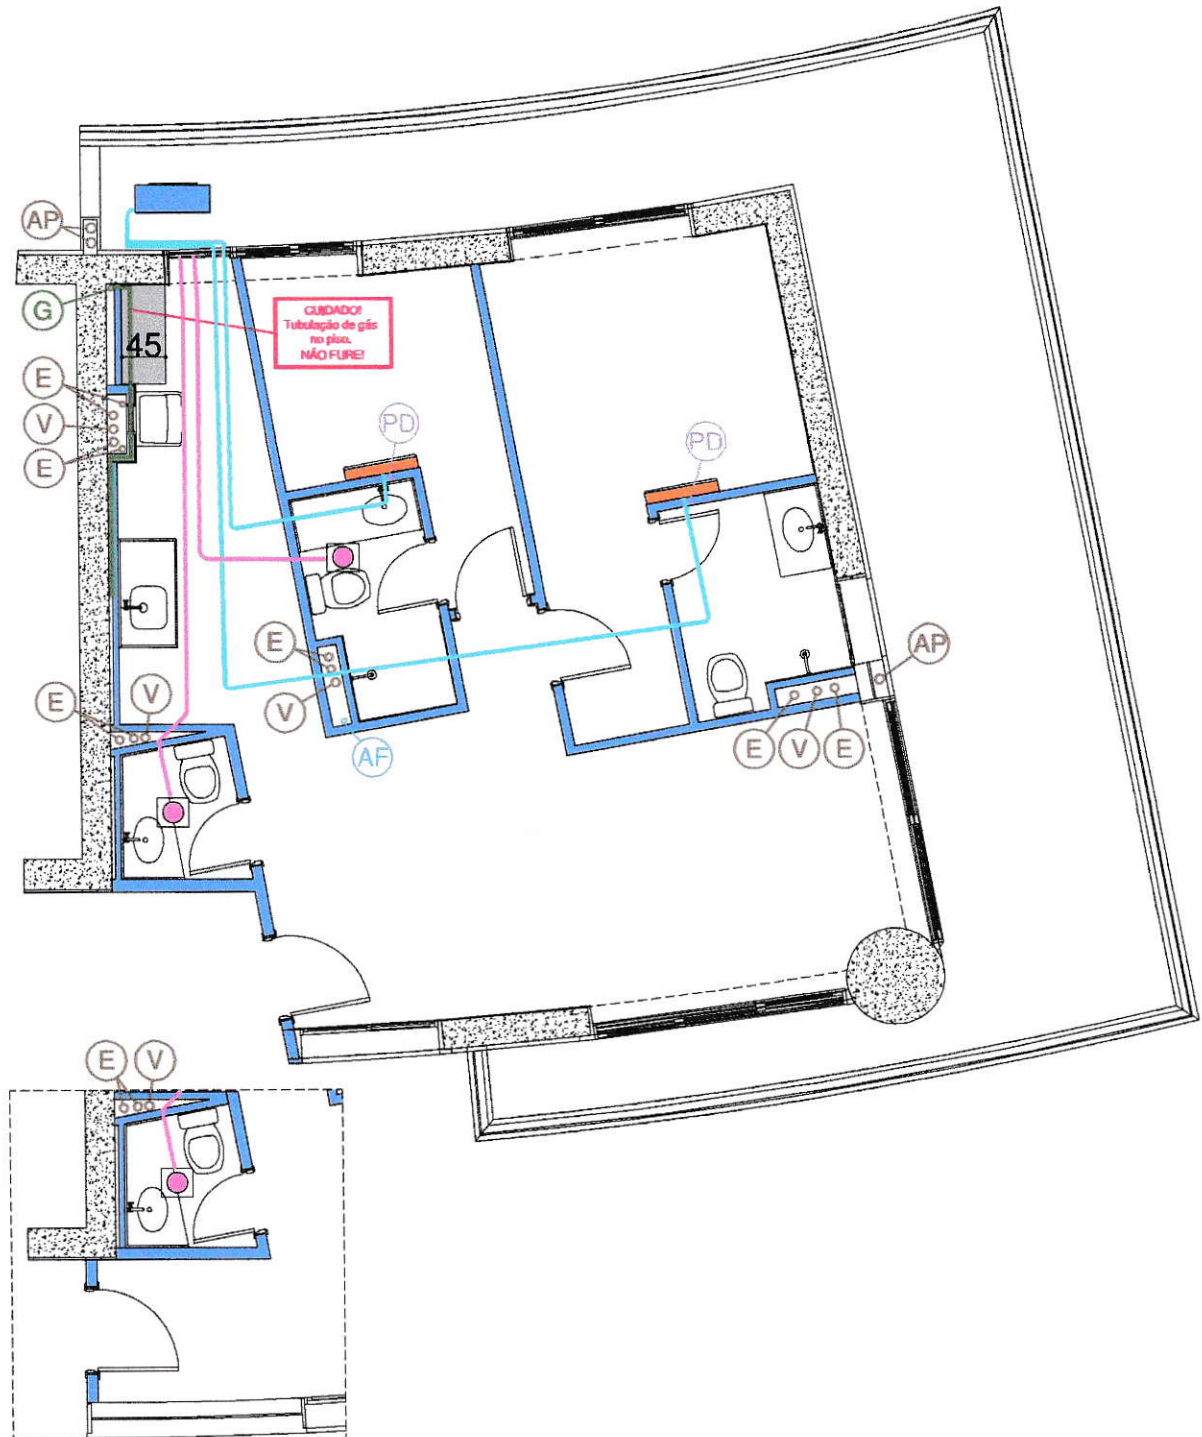

LEGENDA

PRUMADAS

(V)	VENTILAÇÃO
(E)	ESGOTO
(AP)	ÁGUA PLUVIAL
(AF)	ÁGUA FRIA
(G)	GÁS

PONTOS

(PD)	DRENO
------	-------

	TUBULAÇÃO DE GÁS
	TUBULAÇÃO FRIGORÍGENA (PARA OS PROPRIETÁRIOS QUE ADQUIRIRAM O KIT)
	LOCAL PREVISTO P/ INSTALAÇÃO DA CONDENSADORA
	LOCAL PREVISTO P/ INSTALAÇÃO DA EVAPORADORA DE AR CONDICIONADO DE PAREDE
	TUBULAÇÃO DO EXAUSTOR NO TETO
	PONTO DO EXAUSTOR

OBS.: NÃO EXECUTAR FUROS NA REGIÃO DAS PRUMADAS!





LEMBRE-SE DE QUE OS ENCANAMENTOS QUE PASSAM POR UMA PAREDE HIDRÁULICA, MOSTRADA NOS BANHEIROS, COZINHA ETC., TAMBÉM ESTÃO PASSANDO POR ESTA MESMA PAREDE NA ÁREA SECA VIZINHA. NAS COLOCAÇÕES DOS ARMÁRIOS, TOMAR TODOS OS CUIDADOS POSSÍVEIS.

ATENÇÃO: USAR LIMITADOR DE BROCA E NÃO ULTRAPASSAR 2 CM DE PROFUNDIDADE!

NÃO FURAR NAS ÁREAS INDICADAS NA COR CINZA

ESQUEMA HIDRÁULICO

UNLIMITED OCEAN FRONT
FINAL 1
BANHO 1

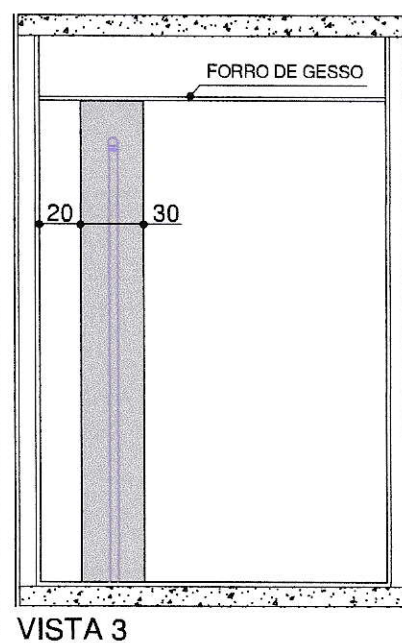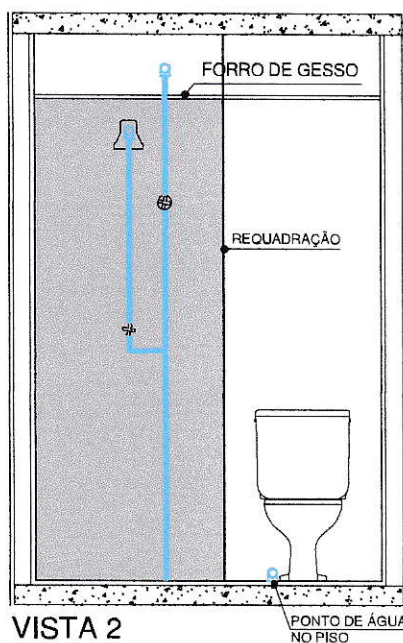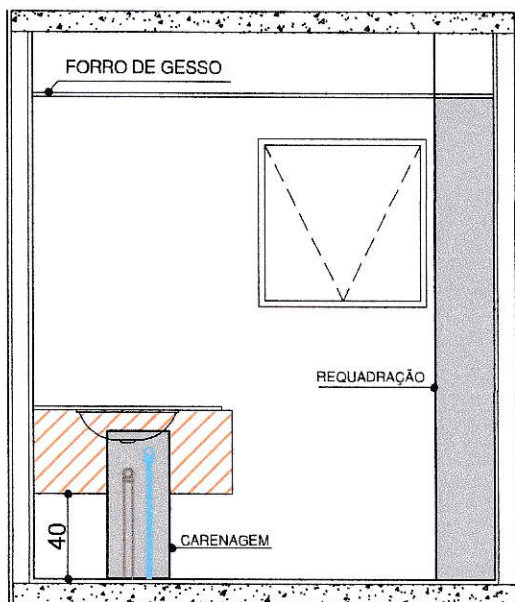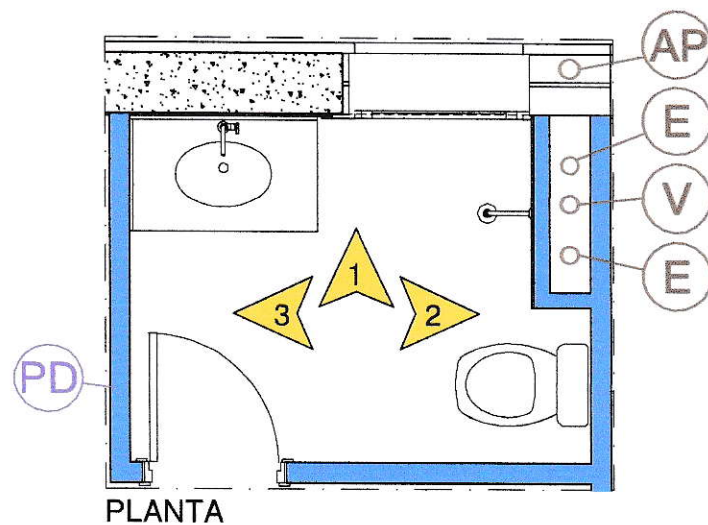

LEGENDA

PRUMADAS

V	VENTILAÇÃO
E	ESGOTO
AP	ÁGUA PLUVIAL
AF	ÁGUA FRIA
G	GÁS

PONTOS

PD	DRENO
----	-------

TUBULAÇÕES

ÁGUA FRIA PEX
ESGOTO
GÁS
DRENO

OBSERVAÇÕES:

NAS MEDIDAS ACIMA, USE COMO REFERÊNCIA OS PONTOS APARENTES DE ÁGUA, GÁS, ESGOTO E REGISTROS.
AS MEDIDAS INDICADAS NAS VISTAS ESTÃO EM CENTÍMETROS.

ANTES DE FURAR:

USAR LIMITADOR DE BROCA E NÃO ULTRAPASSAR 2 CM DE PROFUNDIDADE. LEMBRE-SE QUE OS ENCAMENTOS QUE PASSAM NA(S) PAREDE(S) ACIMA TAMBÉM ESTÃO PASSANDO POR ESTA MESMA PAREDE NO LADO OPOSTO. CONSULTE A PLANTA DE PRUMADAS. NÃO FURE AS SANCAS E FORROS DE GESSO POIS ELES TAMBÉM ABRIGAM TUBULAÇÕES HIDRÁULICAS.

NÃO FURAR NAS ÁREAS INDICADAS NA COR CINZA


CONCRETO

REFORÇO DE MADEIRA


VISTA

ESQUEMA HIDRÁULICO

UNLIMITED OCEAN FRONT
FINAL 1
BANHO 2

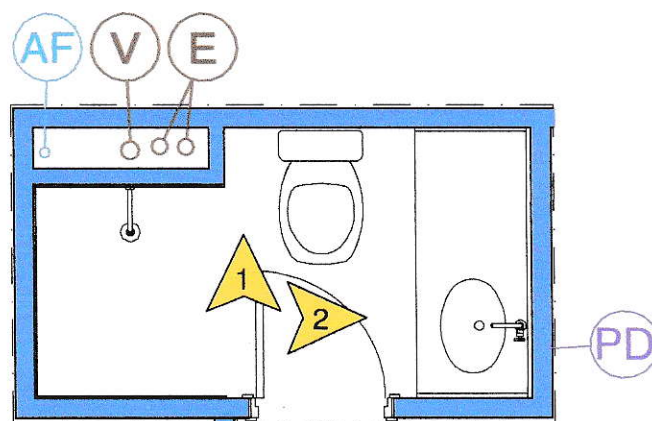

PLANTA

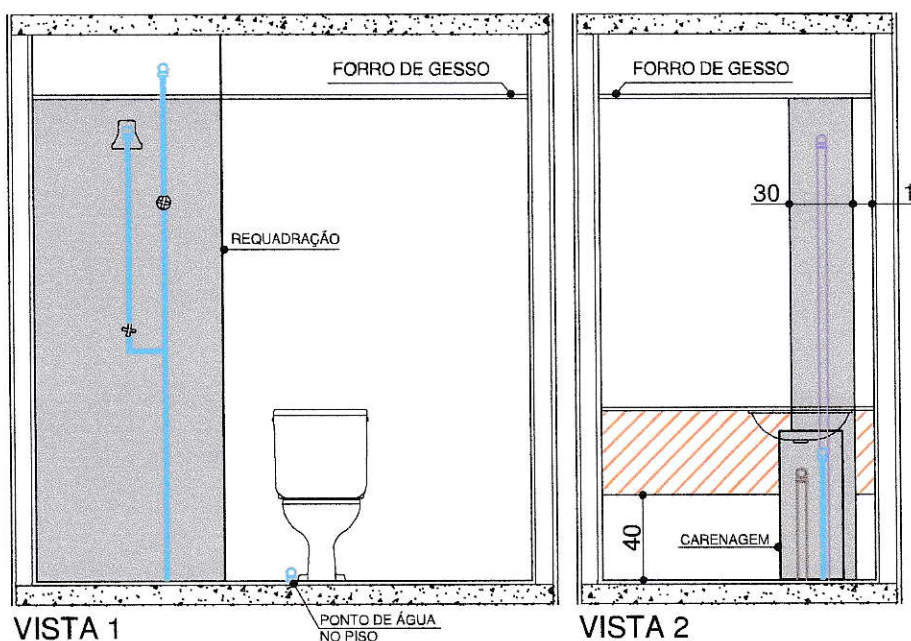

VISTA 1

VISTA 2

LEGENDA

PRUMADAS

V	VENTILAÇÃO
E	ESGOTO
AF	ÁGUA PLUVIAL
AF	ÁGUA FRIA
G	GÁS

PONTOS

PD	DRENO
----	-------

TUBULAÇÕES

ÁGUA FRIA PEX
ESGOTO
GÁS
DRENO

OBSERVAÇÕES:

NAS MEDIDAS ACIMA, USE COMO REFERÊNCIA OS PONTOS APARENTES DE ÁGUA, GÁS, ESGOTO E REGISTROS.
AS MEDIDAS INDICADAS NAS VISTAS ESTÃO EM CENTÍMETROS.


ANTES DE FURAR:

USAR LIMITADOR DE BROCA E NÃO ULTRAPASSAR 2 CM DE PROFUNDIDADE.
LEMBRE-SE QUE OS ENCANAMENTOS QUE PASSAM NA(S) PAREDE(S) ACIMA
TAMBÉM ESTÃO PASSANDO POR ESTA MESMA PAREDE NO LADO OPOSTO.
CONSULTE A PLANTA DE PRUMADAS.
NÃO FURE AS SANCAS E FORROS DE GESSO POIS ELES TAMBÉM ABRIGAM
TUBULAÇÕES HIDRÁULICAS.


NÃO FURAR NAS ÁREAS INDICADAS NA GOR CINZA
CONCRETO
REFORÇO DE MADEIRA
VISTA

ESQUEMA HIDRÁULICO

UNLIMITED OCEAN FRONT
FINAL 1
LAVABO

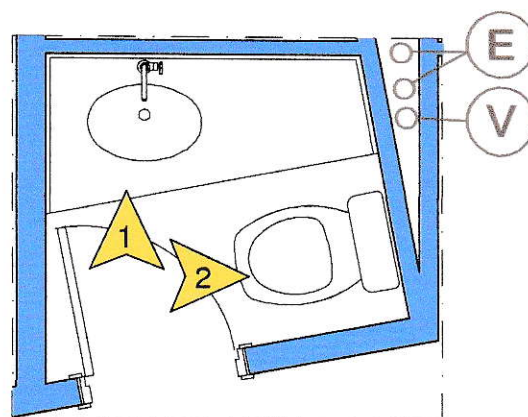

PLANTA

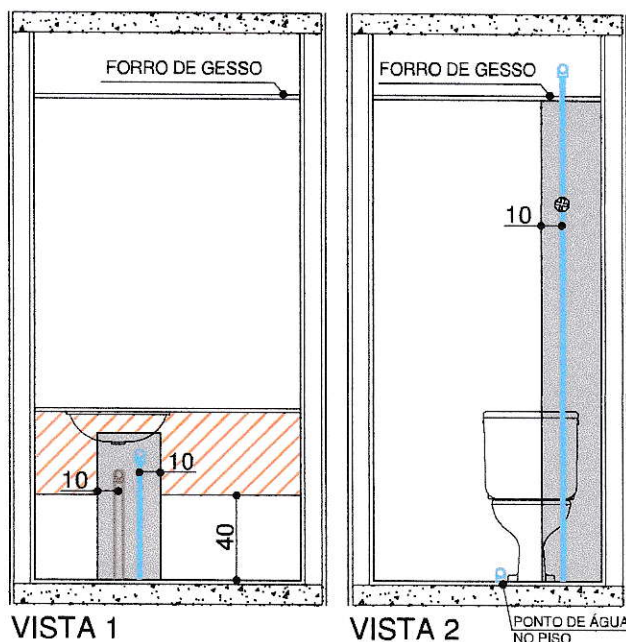

VISTA 1

VISTA 2

PONTO DE ÁGUA NO PISO

LEGENDA

PRUMADAS

V	VENTILAÇÃO
E	ESGOTO
AP	ÁGUA PLUVIAL
AF	ÁGUA FRIA
G	GÁS

PONTOS

PD	DRENO
----	-------

TUBULAÇÕES

ÁGUA FRIA PEX
ESGOTO
GÁS
DRENO

OBSERVAÇÕES:

NAS MEDIDAS ACIMA, USE COMO REFERÊNCIA OS PONTOS APARENTES DE ÁGUA, GÁS, ESGOTO E REGISTROS.
AS MEDIDAS INDICADAS NAS VISTAS ESTÃO EM CENTÍMETROS.

ANTES DE FURAR:

USAR LIMITADOR DE BROCA E NÃO ULTRAPASSAR 2 CM DE PROFUNDIDADE. LEMBRE-SE QUE OS ENCANAMENTOS QUE PASSAM NA(S) PAREDE(S) ACIMA TAMBÉM ESTÃO PASSANDO POR ESTA MESMA PAREDE NO LADO OPOSTO. CONSULTE A PLANTA DE PRUMADAS. NÃO FURE AS SANCAS E FORROS DE GESSO POIS ELES TAMBÉM ABRIGAM TUBULAÇÕES HIDRÁULICAS.

NÃO FURAR NAS ÁREAS INDICADAS NA COR CINZA



CONCRETO

REFORÇO DE MADEIRA

VISTA

ESQUEMA HIDRÁULICO

UNLIMITED OCEAN FRONT
FINAL 1
COZINHA E ÁREA DE SERVIÇO

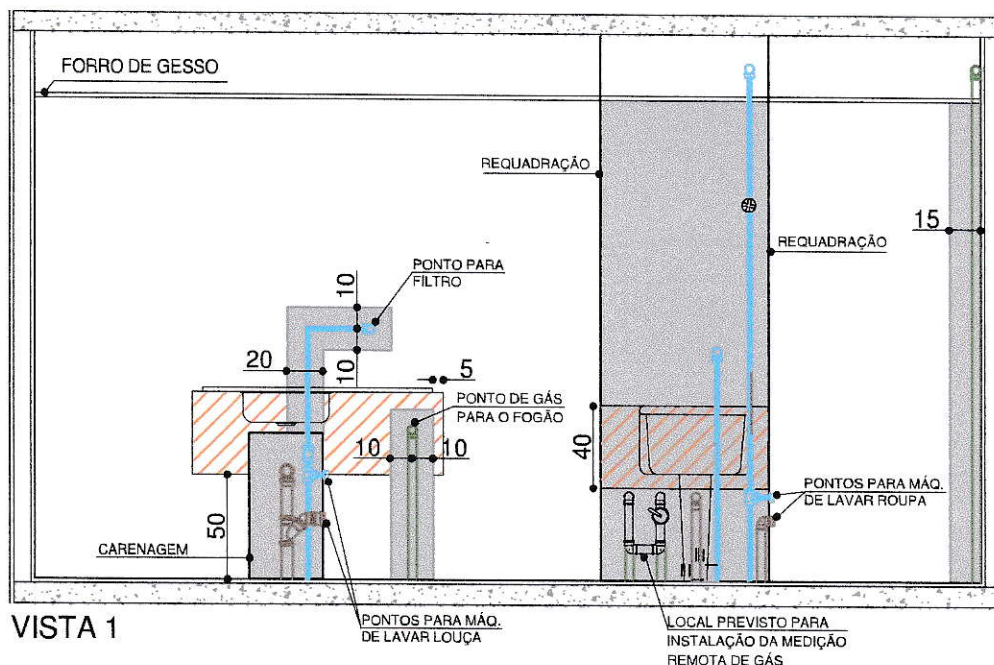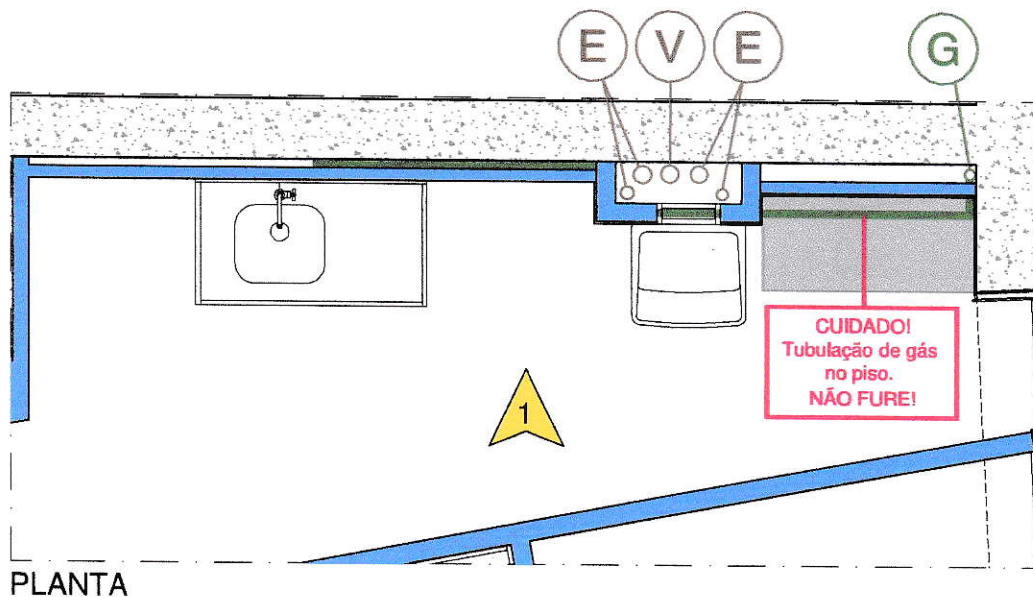

LEGENDA

PRUMADAS

V	VENTILAÇÃO
E	ESGOTO
AP	ÁGUA PLUVIAL
AF	ÁGUA FRIA
G	GÁS

PONTOS

PD	DRENO
----	-------

TUBULAÇÕES

ÁGUA FRIA PEX
ESGOTO
GÁS
DRENO

OBSERVAÇÕES:

NAS MEDIDAS ACIMA, USE COMO REFERÊNCIA OS PONTOS APARENTES DE ÁGUA, GÁS, ESGOTO E REGISTROS.
AS MEDIDAS INDICADAS NAS VISTAS ESTÃO EM CENTÍMETROS.

ANTES DE FURAR:

USAR LIMITADOR DE BROCA E NÃO ULTRAPASSAR 2 CM DE PROFUNDIDADE. LEMBRE-SE QUE OS ENCANAMENTOS QUE PASSAM NA(S) PAREDE(S) ACIMA TAMBÉM ESTÃO PASSANDO POR ESTA MESMA PAREDE NO LADO OPOSTO. CONSULTE A PLANTA DE PRUMADAS. NÃO FURE AS SANCAS E FORROS DE GESSO POIS ELES TAMBÉM ABRIGAM TUBULAÇÕES HIDRÁULICAS.

■	NÃO FURAR NAS ÁREAS INDICADAS NA COR CINZA
■	CONCRETO
■	REFORÇO DE MADEIRA
▲	VISTA