


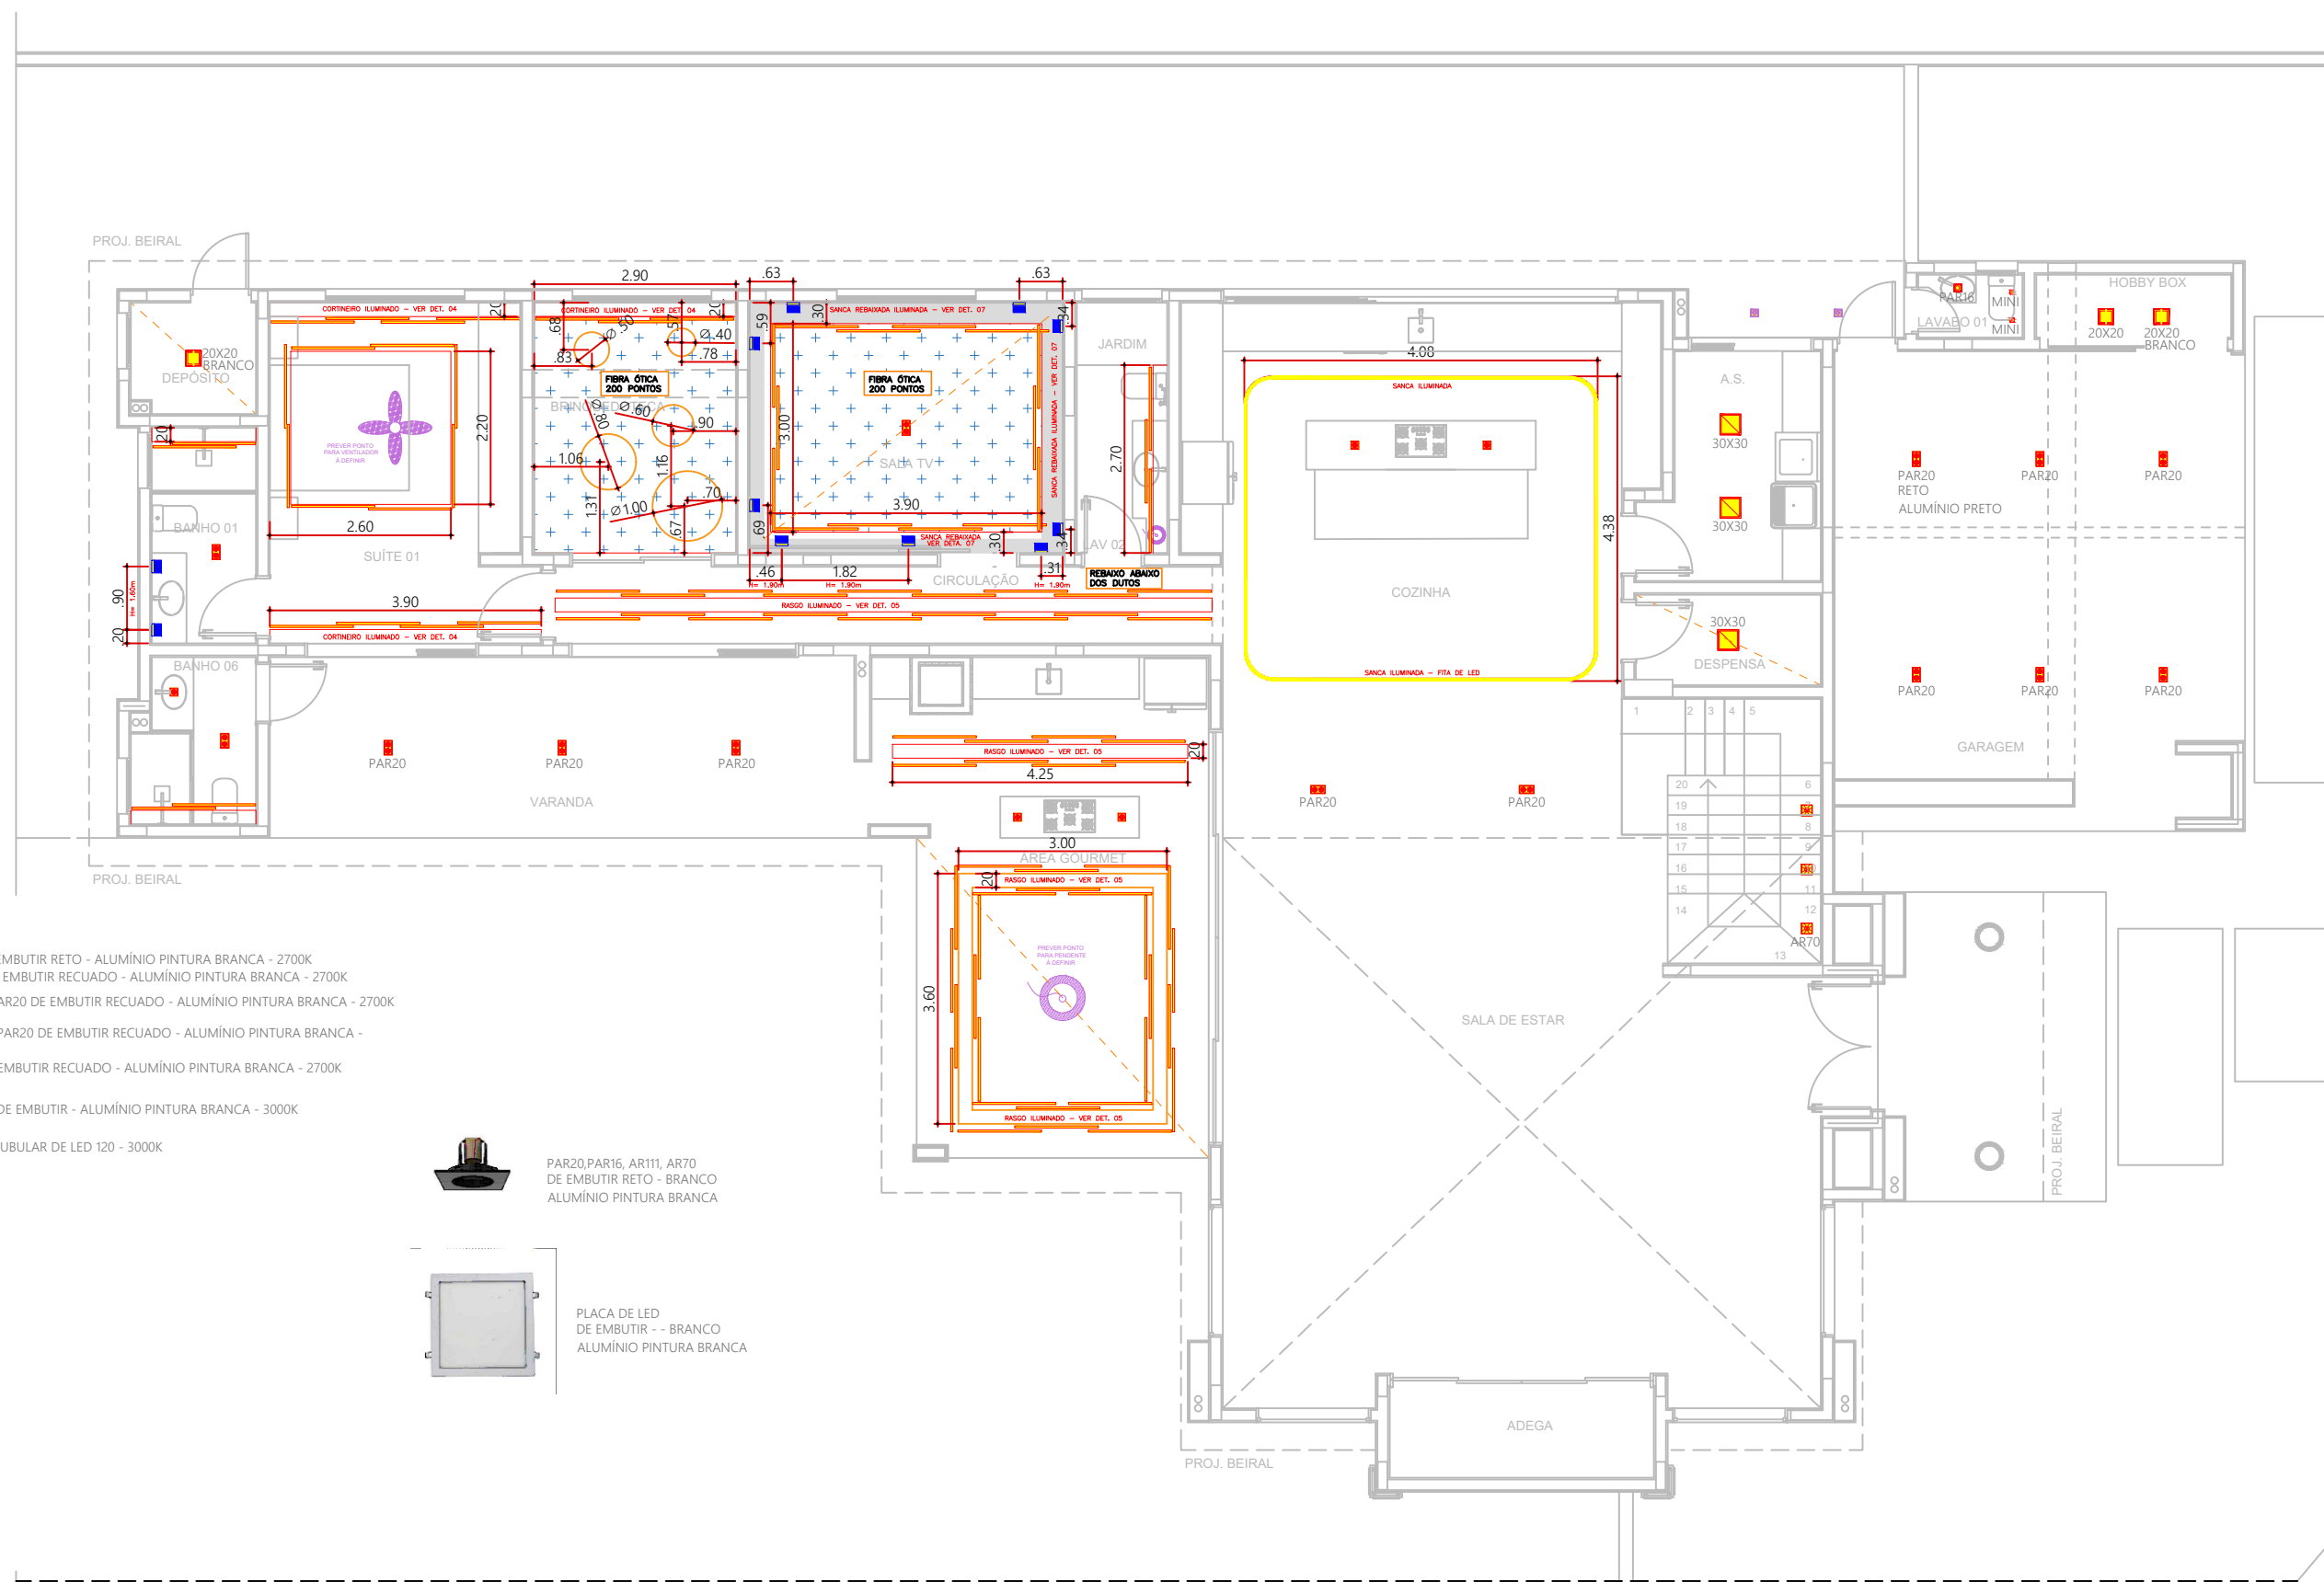

- SPOT MINI DE EMBUTIR RETO - ALUMÍNIO PINTURA BRANCA - 2700K
- SPOT PAR16 DE EMBUTIR RECUADO - ALUMÍNIO PINTURA BRANCA - 2700K
- SPOT DUPLO PAR20 DE EMBUTIR RECUADO - ALUMÍNIO PINTURA BRANCA - 2700K
- SPOT SIMPLES PAR20 DE EMBUTIR RECUADO - ALUMÍNIO PINTURA BRANCA - 2700K
- SPOT AR70 DE EMBUTIR RECUADO - ALUMÍNIO PINTURA BRANCA - 2700K
- PLACA DE LED DE EMBUTIR - ALUMÍNIO PINTURA BRANCA - 3000K

— LÂMPADA TUBULAR DE LED 120 - 3000K



PAR20, PAR16, AR111, AR70
DE EMBUTIR RETO - BRANCO
ALUMÍNIO PINTURA BRANCA



PLACA DE LED
DE EMBUTIR - - BRANCO
ALUMÍNIO PINTURA BRANCA

RESIDÊNCIA
CC

CLIENTES: CARLOS E CAMILA
CONDOMÍNIO MIRANTE DO VALE
ESCALA: 1/100

PROJETO DE INTERIORES
PLANTA DE FORRO DE GESSO - PAV. INFERIOR
DATA: 10/05/2025

www.bierthenfreire@arq.com

Cel: 9 9135 2403 / 9 7412 9779 |

e-mail: bierthen.freire@outlook.com

