



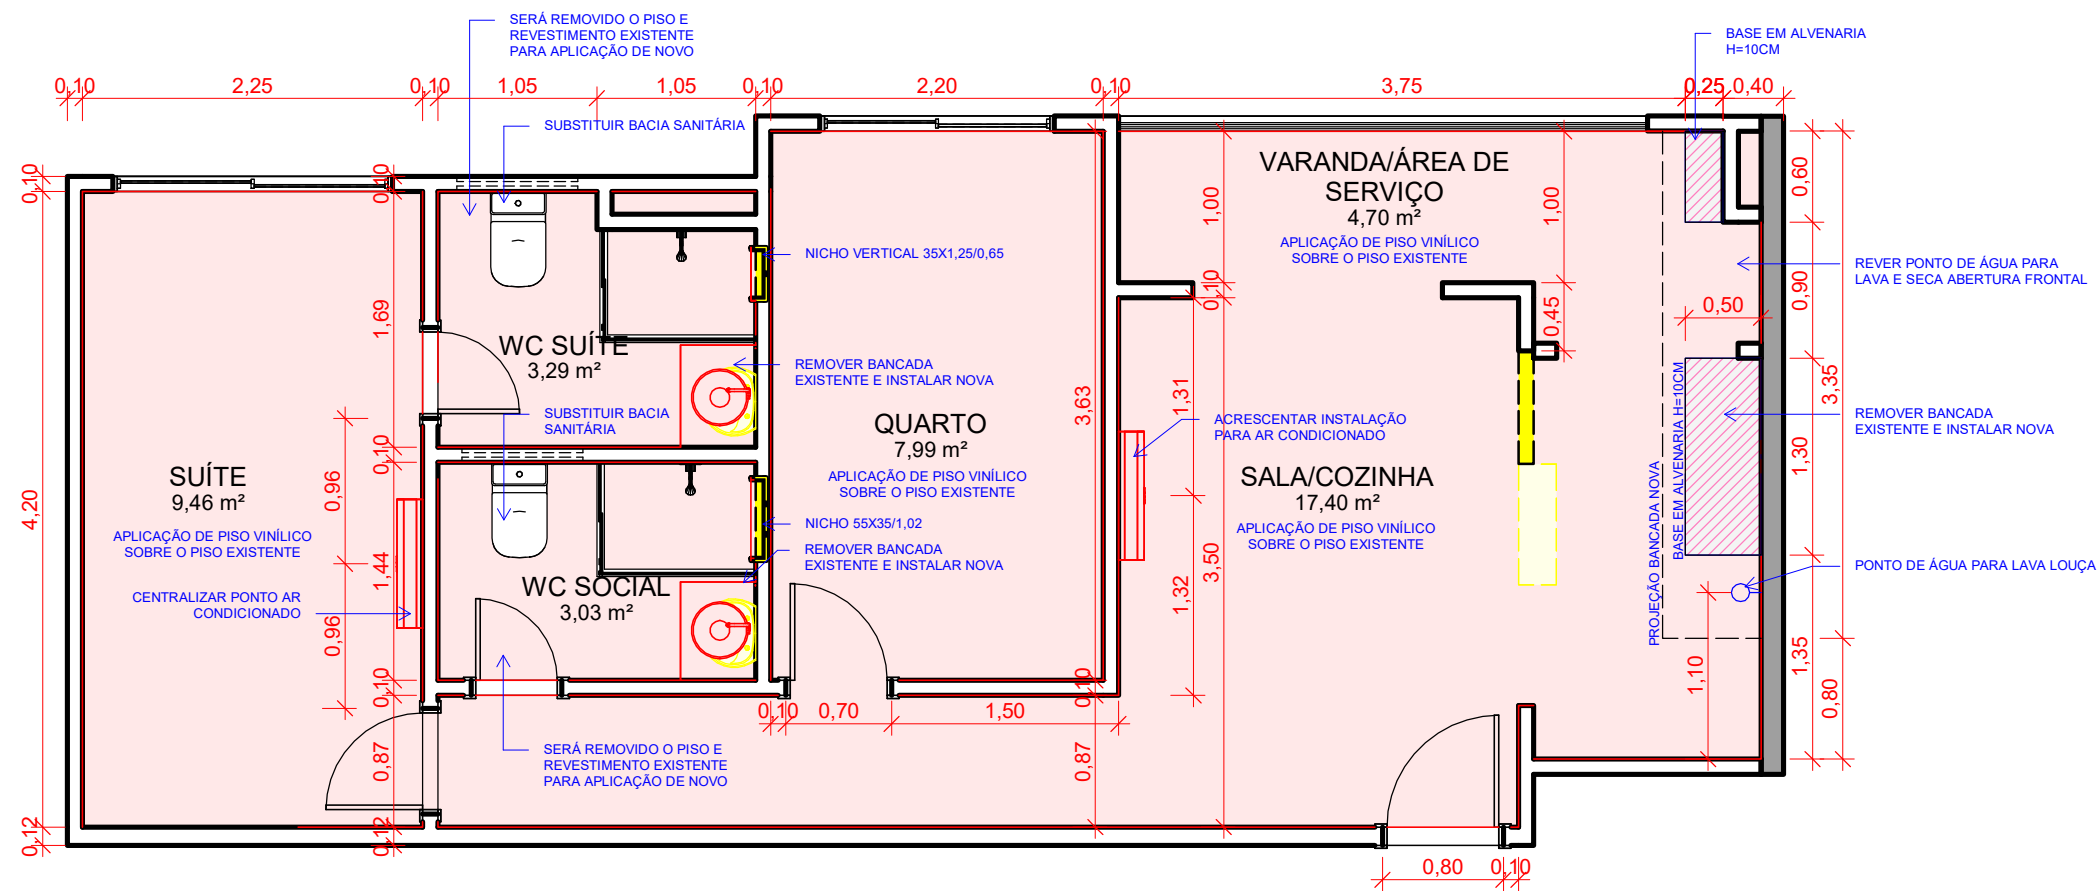


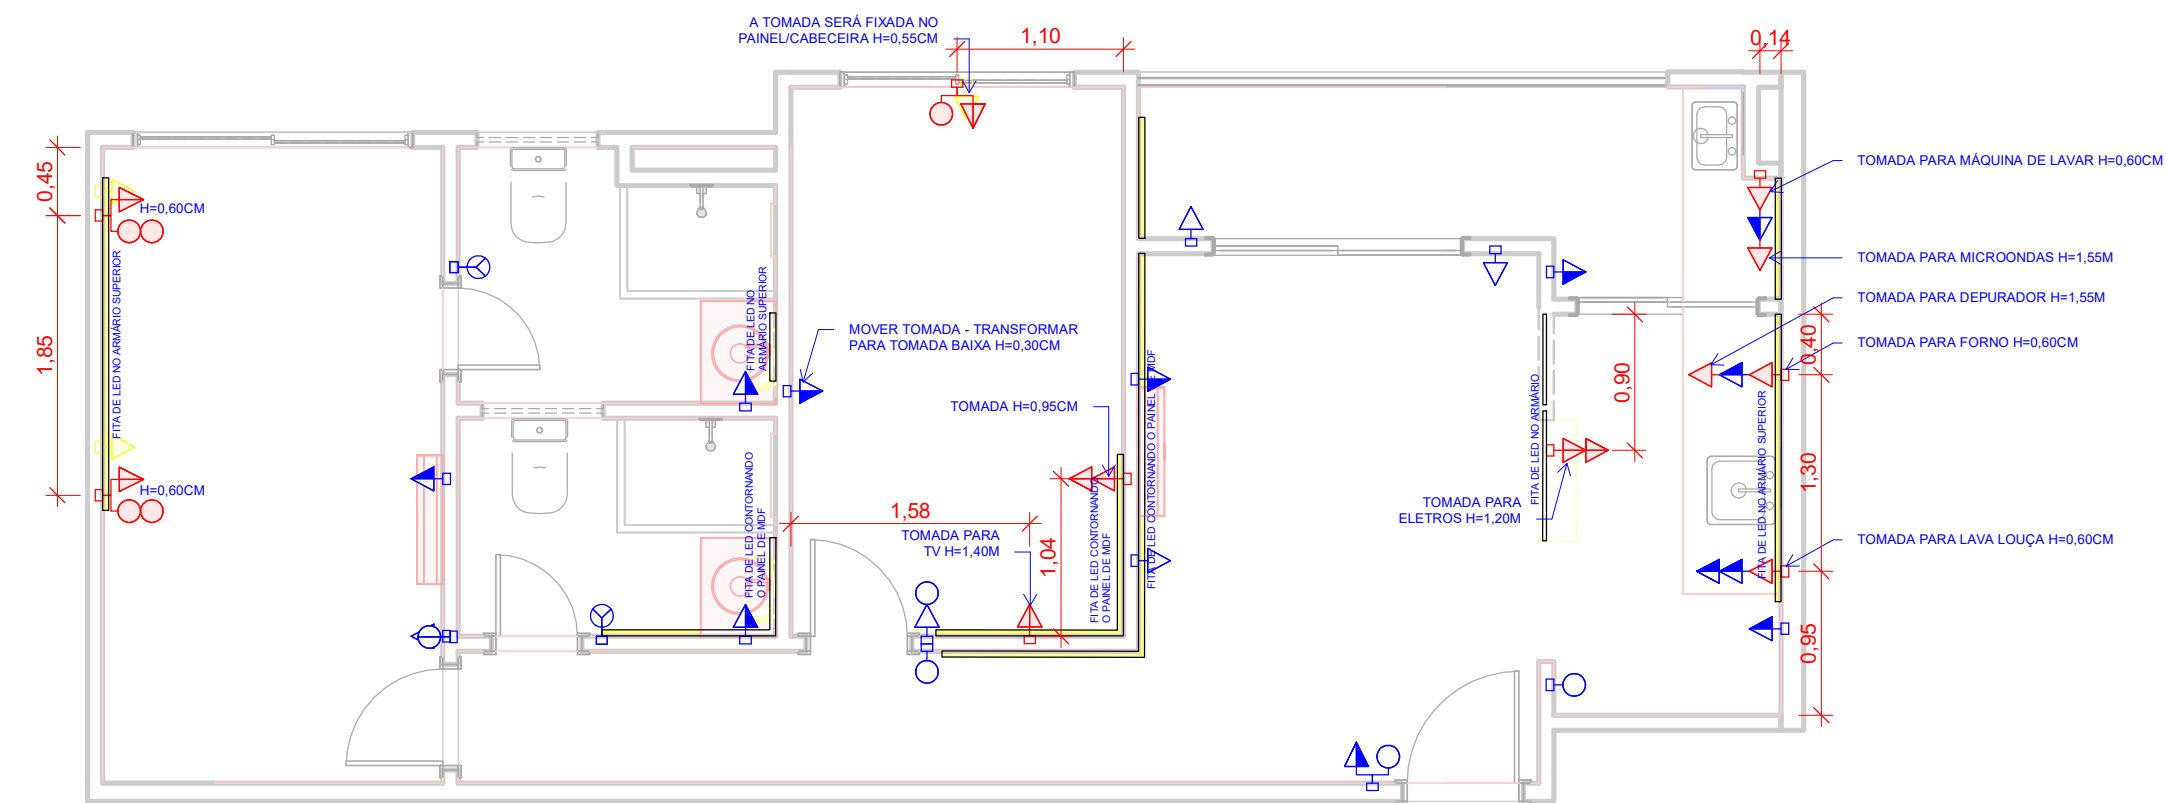

LEGENDA ELÉTRICA	
	TOMADA SIMPLES BAIXA
	TOMADA DUPLA BAIXA
	TOMADA SIMPLES MÉDIA
	TOMADA DUPLA MÉDIA
	TOMADA SIMPLES ALTA
	TOMADA DUPLA ALTA
	PONTO TELEFONE
	PONTO TV
	TOMADA DE PISO/TETO *VER ESPECIFICAÇÃO NA PLANTA
	INTERRUPTOR SIMPLES
	INTERRUPTOR DUPLO
	INTERRUPTOR TRIPLO
	CAIXA DE PASSAGEM
	INTERRUPTOR DUPLO +TOMADA
	INTERRUPTOR SIMPLES +TOMADA

*AS TOMADAS QUE NÃO ESTIVEREM COM INFORMAÇÃO DE ALTURA DEVERÃO SEGUIR A ALTURA PADRÃO:

TOMADA BAIXA $H=0,30\text{M}$
TOMADA MÉDIA $H=1,30\text{M}$
TOMADA ALTA $H=2,00\text{M}$

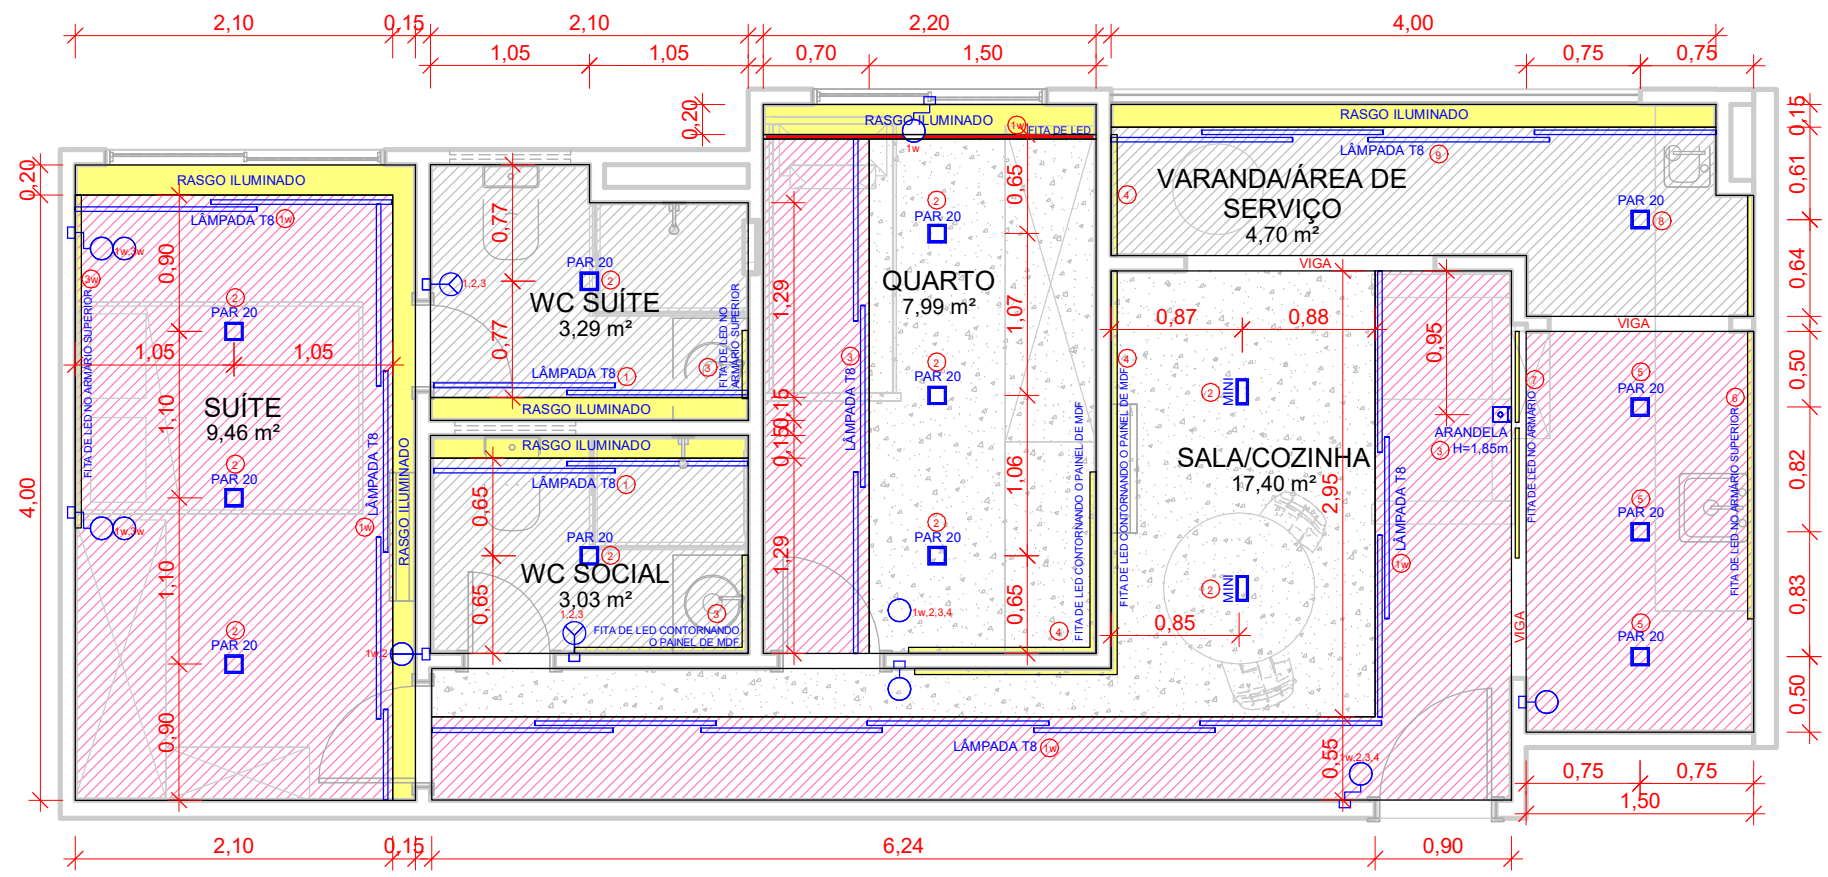

1 PLANTA BAIXA
ESCALA 1 : 50


TABELA LUMINÁRIAS	
QUANTIDADE	TIPO
1	ARANDELA
5	LUMINÁRIA DE EMBUTIR COM 01 LÂMPADA PAR 20
2	LUMINÁRIA DE SOBREPOR RETANGULAR TRILHO MINI DICRÓICA
4	LUMINÁRIA SPOT REDONDO DE EMBUTIR HOLE COM 01 LÂMPADA PAR 20
3	LUMINÁRIA SPOT REDONDO DE SOBREPOR HOLE COM 01 LÂMPADA PAR 20
1	LÂMPADA T8 60CM
25	LÂMPADA T8 120CM

OBS:
- SUGESTÃO DA TEMPERATURA DA COR DAS LÂMPADAS: 3000K OU 4000K.


LEGENDA GESSO

- REBAIXAMENTO DE GESSO EXISTENTE
- REBAIXAMENTO DE GESSO 15CM
- LAJE
- RASGO/CORTINEIRO ILUMINADO

2 GESSO
ESCALA 1 : 25

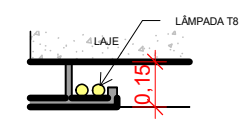

3 DETALHE
ESCALA 1 : 25

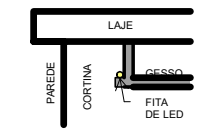

3 DET. CORTINEIRO QUARTO
ESCALA 1 : 25