


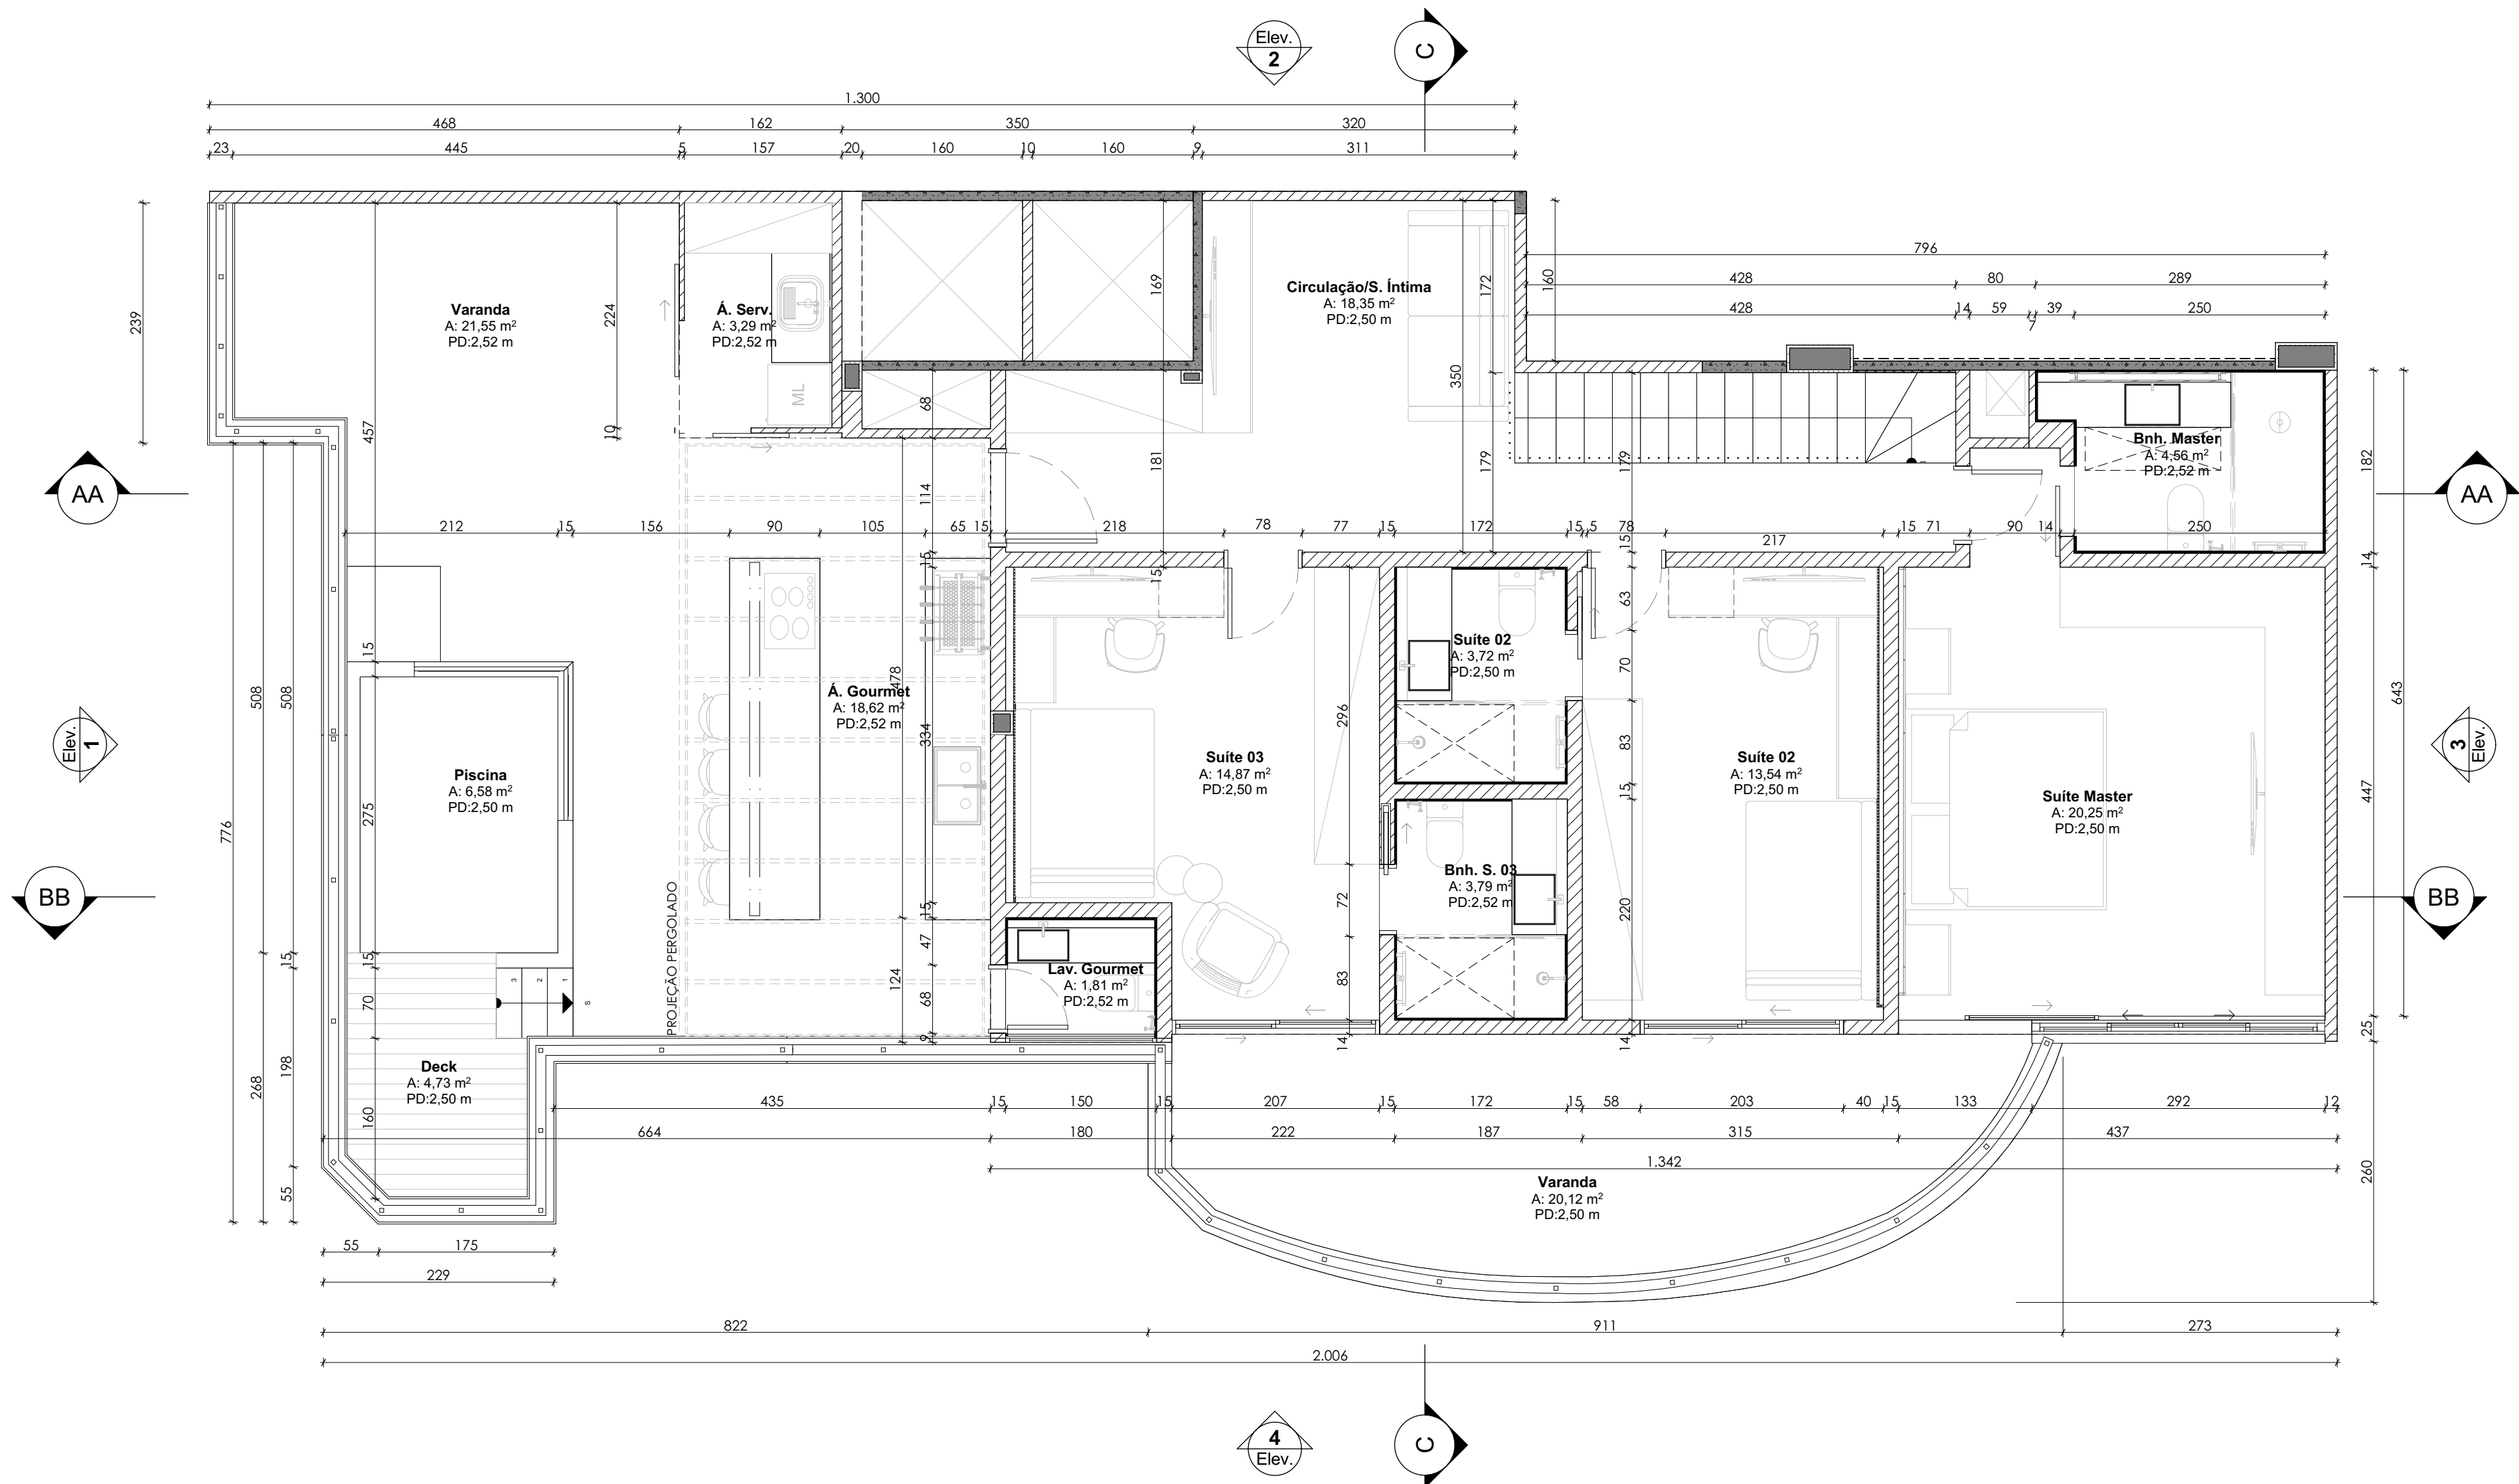

OBSERVAÇÕES:
01. MEDIDAS EM CENTÍMETROS.
02. TODAS AS MEDIDAS DEVEM SER VERIFICADAS NO LOCAL DA OBRA ANTES DA EXECUÇÃO.
03. A ESPECIFICAÇÃO E ESPESSURA DOS VIDROS E ESPELHOS SÃO MERAMENTE SUGESTIVAS E DEVERÃO SER DEFINIDAS PELO RESPONSÁVEL PELA EXECUÇÃO.
04. CONSULTAR CADERNO DE ESPECIFICAÇÃO DE MATERIAIS PARA VERIFICAR ACABAMENTOS E REVESTIMENTOS.
05. EQUIPAMENTOS E ELETRODOMÉSTICOS USADOS COMO REFERENCIA NECESSITAM DE APROVAÇÃO DO CLIENTE.
06. CONFERIR MEDIDAS NOS DMS/PROJETOS HIDRÁULICOS

LD

LEILA
DIONIZIOS
ARQUITETURA | LUMINOTÉCNICA

CONDOMÍNIO 02, BL.6 S.121 - BARRA DA TIJUCA - RJ
TEL.: 2487 - 6405 / 2025 - 2103
leiladionizio@leiladionizio.com.br

ENDEREÇO:
Condomínio Waterways - Avenida Lúcio Costa, 4600 Barra da Tijuca RIO DE JANEIRO RJ 22630-011

CIDADE: RIO DE JANEIRO ESTADO: RJ **LD2421.PE-LILIAN E BRUNO**

PROPRIETÁRIO
LILIAN E BRUNO

RESPONSÁVEL EXECUÇÃO

FASE PROJETO
PE | ARQUITETURA

ESCALA
1:50

DIMENSÃO DA FOLHA
420,0x804,0

CONTEÚDO
PLANTA DE ARQUITETURA - 2º pavimento

RESPONSÁVEL
LEILA DIONIZIO CAU: A188903-6

DATA
14/01/2025

FOLHA

REVISÃO

REVISÃO
R02